


101
1
SYSTÉM ROV
SOUŘADNICOVÝ SYST

Obsah změny:	
-	
-	
-	

Ředitelství sil a drah ČR Na Pankráci 546/58	Stavbu zajišťuje Ing. J. Štěrba
--	------------------------------------

SG_Velké projekty_BIM 2020
zastoupené

SUDOP PRAHA a.s. Obšanská 1a, 130 80 Praha 3
hlavní inženýr projektu: Ing. Roman Peřík telefon: +420 267 094 111

				
---	---	---	---	---

SUDOP PRAHA a.s.	Veřejný firma:	Asistent veřejného
Ošlešná 1a, 130 80 Praha 3		ING. PAVEL MI

tel.: +420 267 094 111 e-mail: Praha@sudop.cz	ING. ROMAN PETŘÍK	Specialista pro -
--	-------------------	----------------------

PUDIS projektová, průzkumná a konzultační společnost
PUDIS a.s., Podbabská 1014/20, 160 00 Praha 6
tel.: +420 267 004 111, www.pudis.cz, info@pudis.cz

OLEHOVSKÁ	ING. MICHAL TUREK	PETR KOTLABA	ING. MICHAL
			<i>Číslo směrnice:</i>

8 Jaroměř - Trutnov VD-ZDS + TP + AD	Projektový stupeň
	Dokum.

EKTY POZEMNÍCH KOMUNIKACÍ VČETNĚ PROPUSTKŮ
 AVNÍ TRASA D11 1108

E - 13.část	Měřítko:
	1:1000
	Číslo přílohy:

JEDE VE SMYSLU PRÍSLUŠNÉ SMLOUVY O DILO, ŽADÁVA JEDNO ČASŤ NEHODÍ EHT DLE ZÁKONA č 121/2000 Sb. KOPÍROVÁNIA NEBO JINÝMI ZPŮSOBEM ROZŠÍŘOVÁNIA BEZ SOUHLASU