


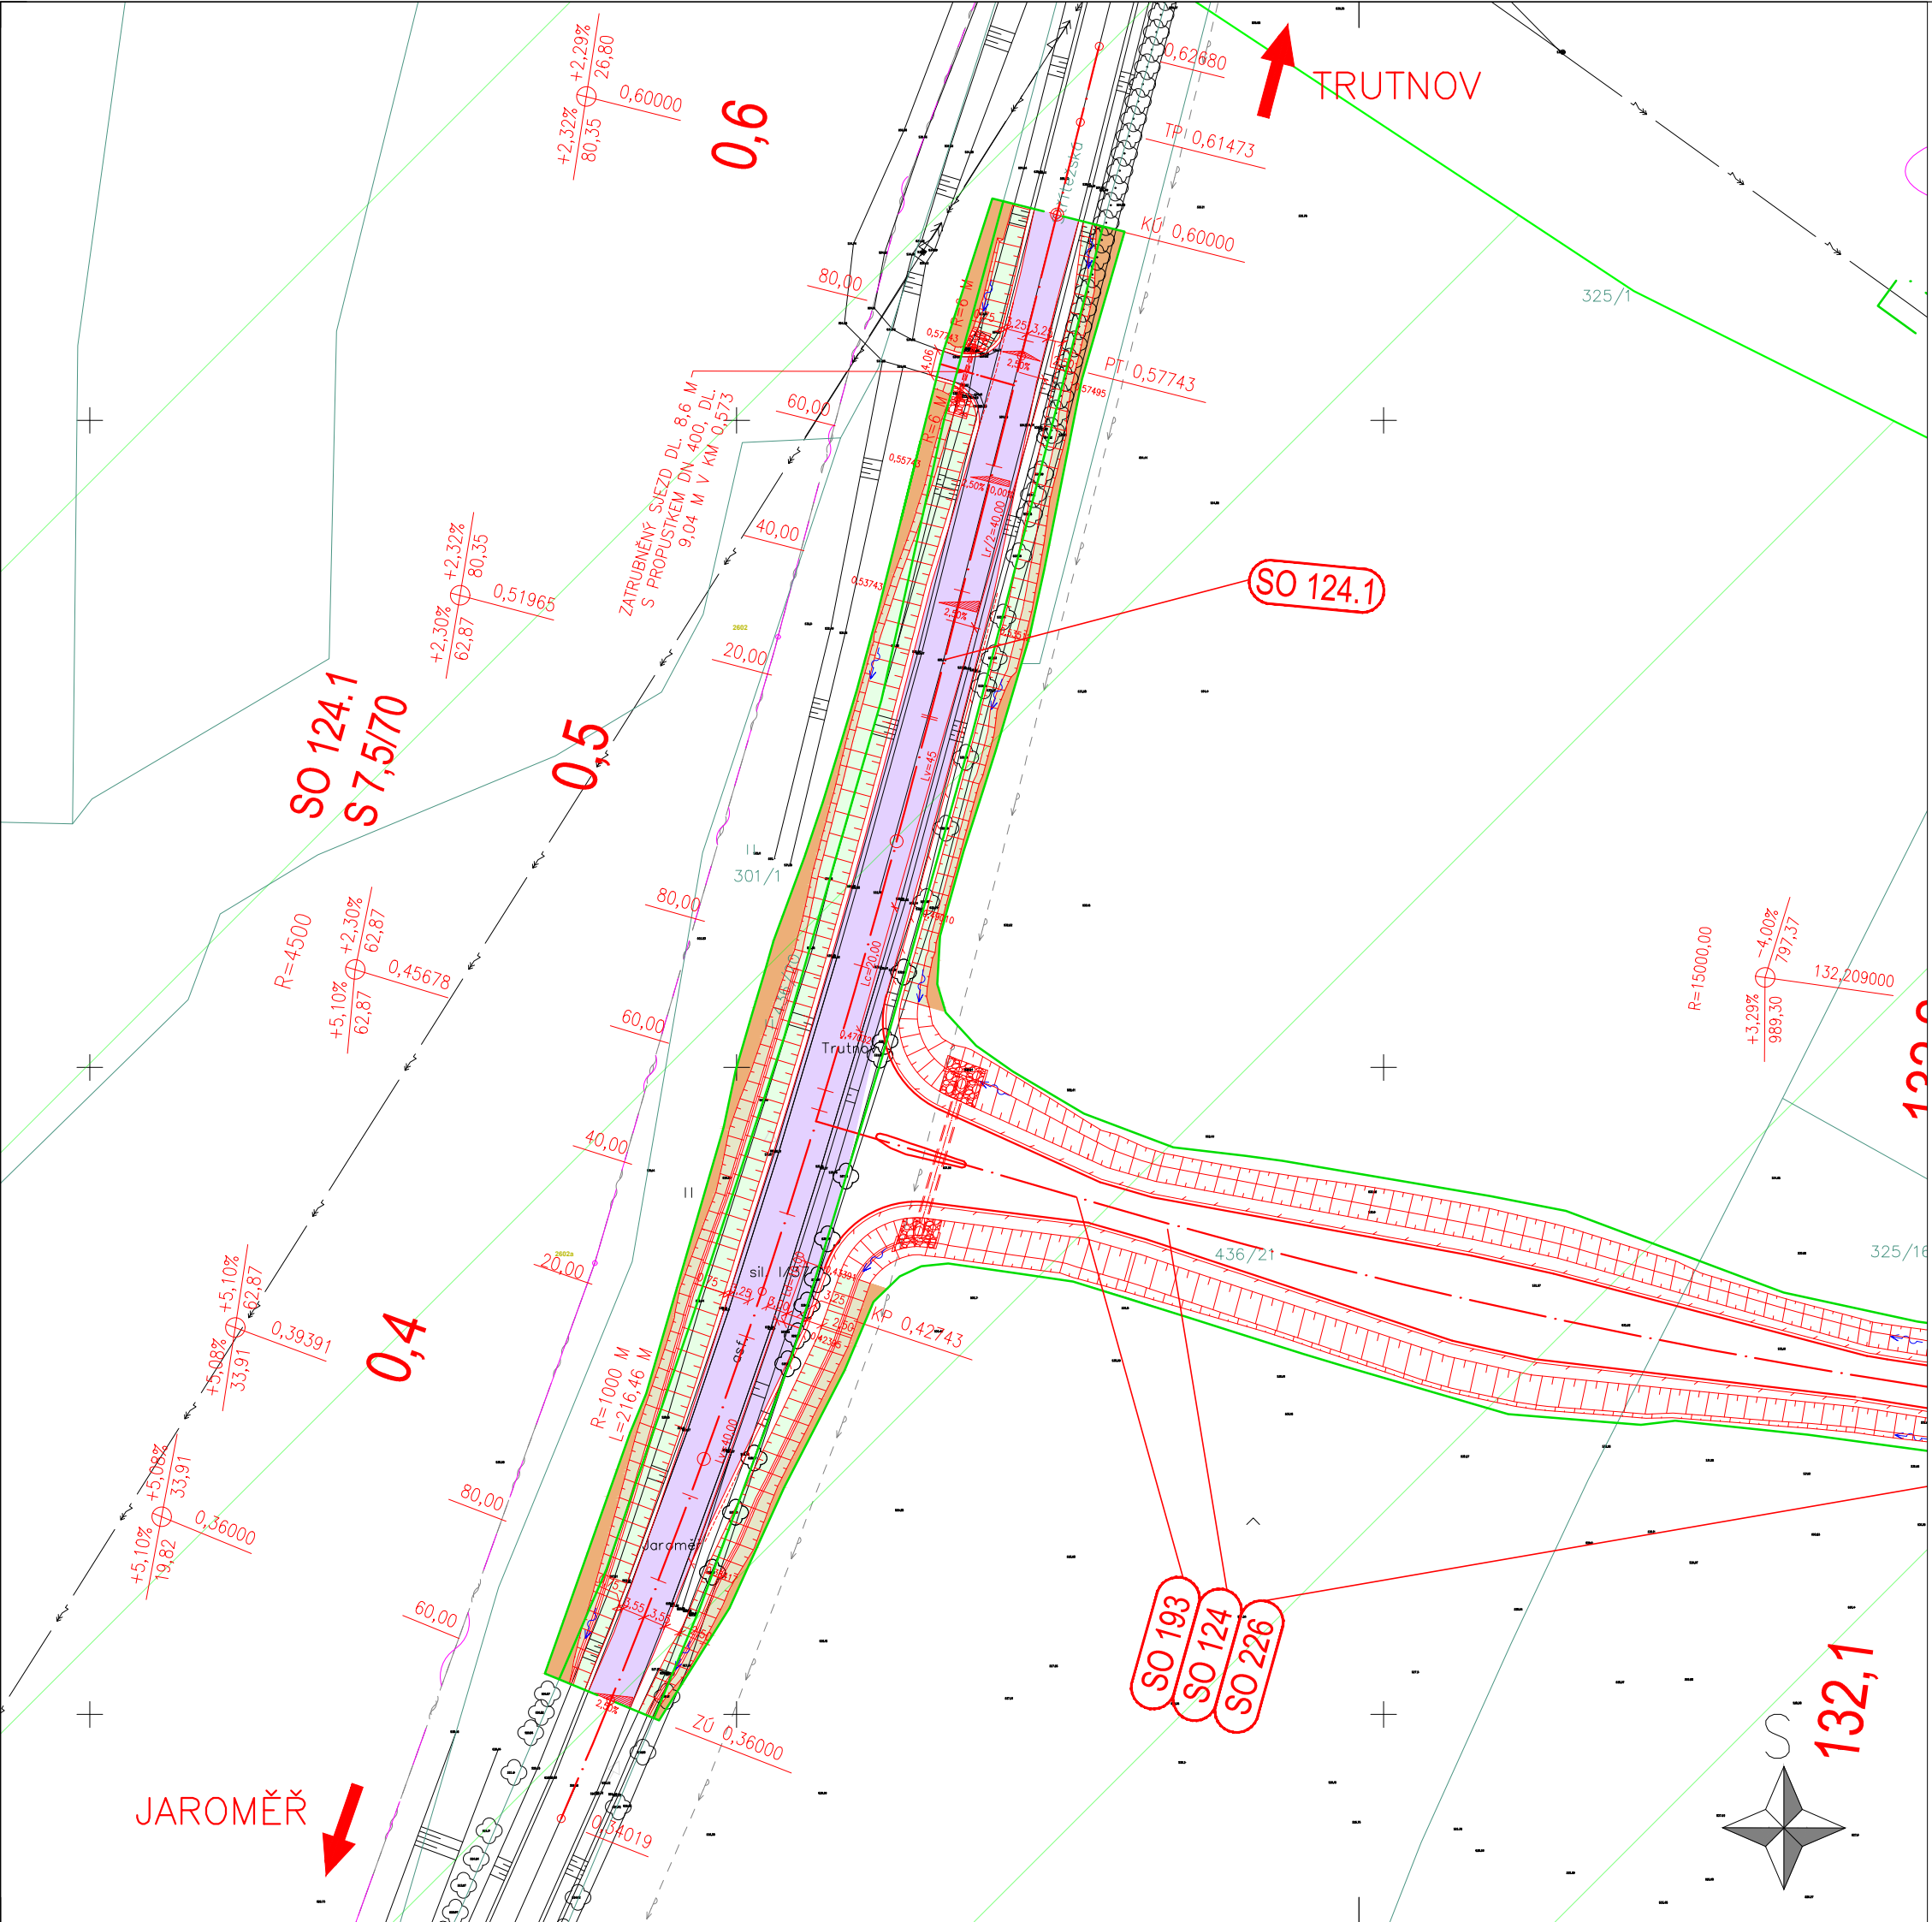

LEGENDA

- HRANY:**
- Nově navržené hrany trvalých SO
 - Nově navržené hrany provizorních komunikací
 - Související investice
 - Oplocení
- BAREVNÉ PLOCHY:**
- Vozovka D11 – asfaltový kryt
 - Vozovka silnic a MK
 - Zpevněná polní cesta/účelová komunikace – asfaltový kryt
 - Nezpevněná polní cesta/účelová komunikace – nestmelený kryt
 - Násyp
 - Zářez
 - Technologické napojení na stav.vrstvy
 - Úprava terénu v rovině
 - Ostrůvky pojížděné
 - Ostrůvky nepojížděné
 - Prstenec okružní křižovatky
 - Chodník

- ZÁBORY STAVBY:**
- Zábor trvalý
 - Zábor dočasný – do 1 roku
 - Zábor dočasný – nad 1 rok

- STÁVAJÍCÍ POLOHOPIS :**
- Stávající polohopis
 - Stávající stav – strom, neplod.půda, park, std.
 - Stávající hranice parcel KN
 - Stávající polohopis katastrálního území

- STÁVAJÍCÍ INŽ. SÍTĚ :**
- Sdělovací – nadzemní
 - Sdělovací – podzemní
 - Silnoproudé vedení – NN podzemní
 - Silnoproudé vedení – NN nadzemní
 - Silnoproudé vedení – VN nadzemní
 - Silnoproudé vedení – VN podzemní
 - Silnoproudé vedení – VN nadzemní
 - Plynovod – NTL
 - Plynovod – STL
 - Plynovod – VTL
 - veřejné osvětlení
 - Vodovod
 - Vodovod – pitná
 - Kanalizace – bez rozlišení

PŘESNOST ZÁKRESŮ STÁVAJÍCÍCH INŽENÝRSKÝCH SÍTÍ ODPOVÍDÁ KVALITĚ PODKLADŮ JEJICH SPRÁVCŮ. ZAKRESLENÁ VEDENÍ JSOU POUZE ORIENTAČNÍ A PŘED ZAHÁJENÍM STAVEBNÍCH PRACÍ JE NUTNO JE ZA ÚČASTI JEJICH SPRÁVCŮ VYTÝČIT.

SO 124.1 D.1.1

VÝŠKOVÝ SYSTÉM Bpv

SOUŘADNICOVÝ SYSTÉM S-JTSK

Číslo změny:	Obsah změny:	Datum změny:
01	-	-
02	-	-
03	-	-

Objednatel:	Ředitelství silnic a dálnic s. p. Na Pankráci 546/56, 140 00 Praha 4
	Stavbu zajišťuje Závod Praha Na Pankráci 546/56, 140 00 Praha 4

Zhotovitel: Společníci ve sdružení	SG_Velké projekty_BIM 2020 zastoupené
SUDOP PRAHA a.s. Hlavní inženýr projektu: Ing. Roman Petřík	Olšanská 1a, 130 80 Praha 3 telefon: +420 267 094 111

--	--	--	--	--

Správce:	SUDOP PRAHA a.s. Olšanská 1a, 130 80 Praha 3 tel.: +420 267 094 111 e-mail: praha@sudop.cz	Vedoucí týmu:	Asistent vedoucího týmu:
		ING. ROMAN PETŘÍK	ING. PAVEL MICHL
			Specialista profese:
			-

Zpracovatel částí:	projektová, průzkumná a konzultační společnost PUDIS a.s., Podbabská 1014/20, 160 00 Praha 6 tel.: +420 267 004 111, www.pudis.cz, info@pudis.cz
--------------------	--

Vedoucí střediska:	Odpovědný projektant SO, IO, PS:	Vypracoval:	Kontroloval:
ING. ZDEŇKA BOLEHOVSKÁ	ING. MICHAL TUREK	ING. TOMÁŠ VÁŇA	ING. MICHAL TUREK

Název akce:	Číslo smlouvy:
D11 1108 Jaroměř - Trutnov VD-ZDS + TP + AD	22-014.250
Část:	Projektový stupeň:
D.1.1 OBJEKTY POZEMNÍCH KOMUNIKACÍ VČETNĚ PROPUSTKŮ SO 124.1 PŘELOŽKA SILNICE III/30015 (KM 132,22), PŘIDATNÉ PRUHY NA SIL. I/37	VD-ZDS
Název přílohy:	Datum:
SITUACE	11/2024
	Číslo části:
	D.1.1
	Měřítko:
	1:1000
	Počet formátů:
	3xA4
	Číslo přílohy:
	2