
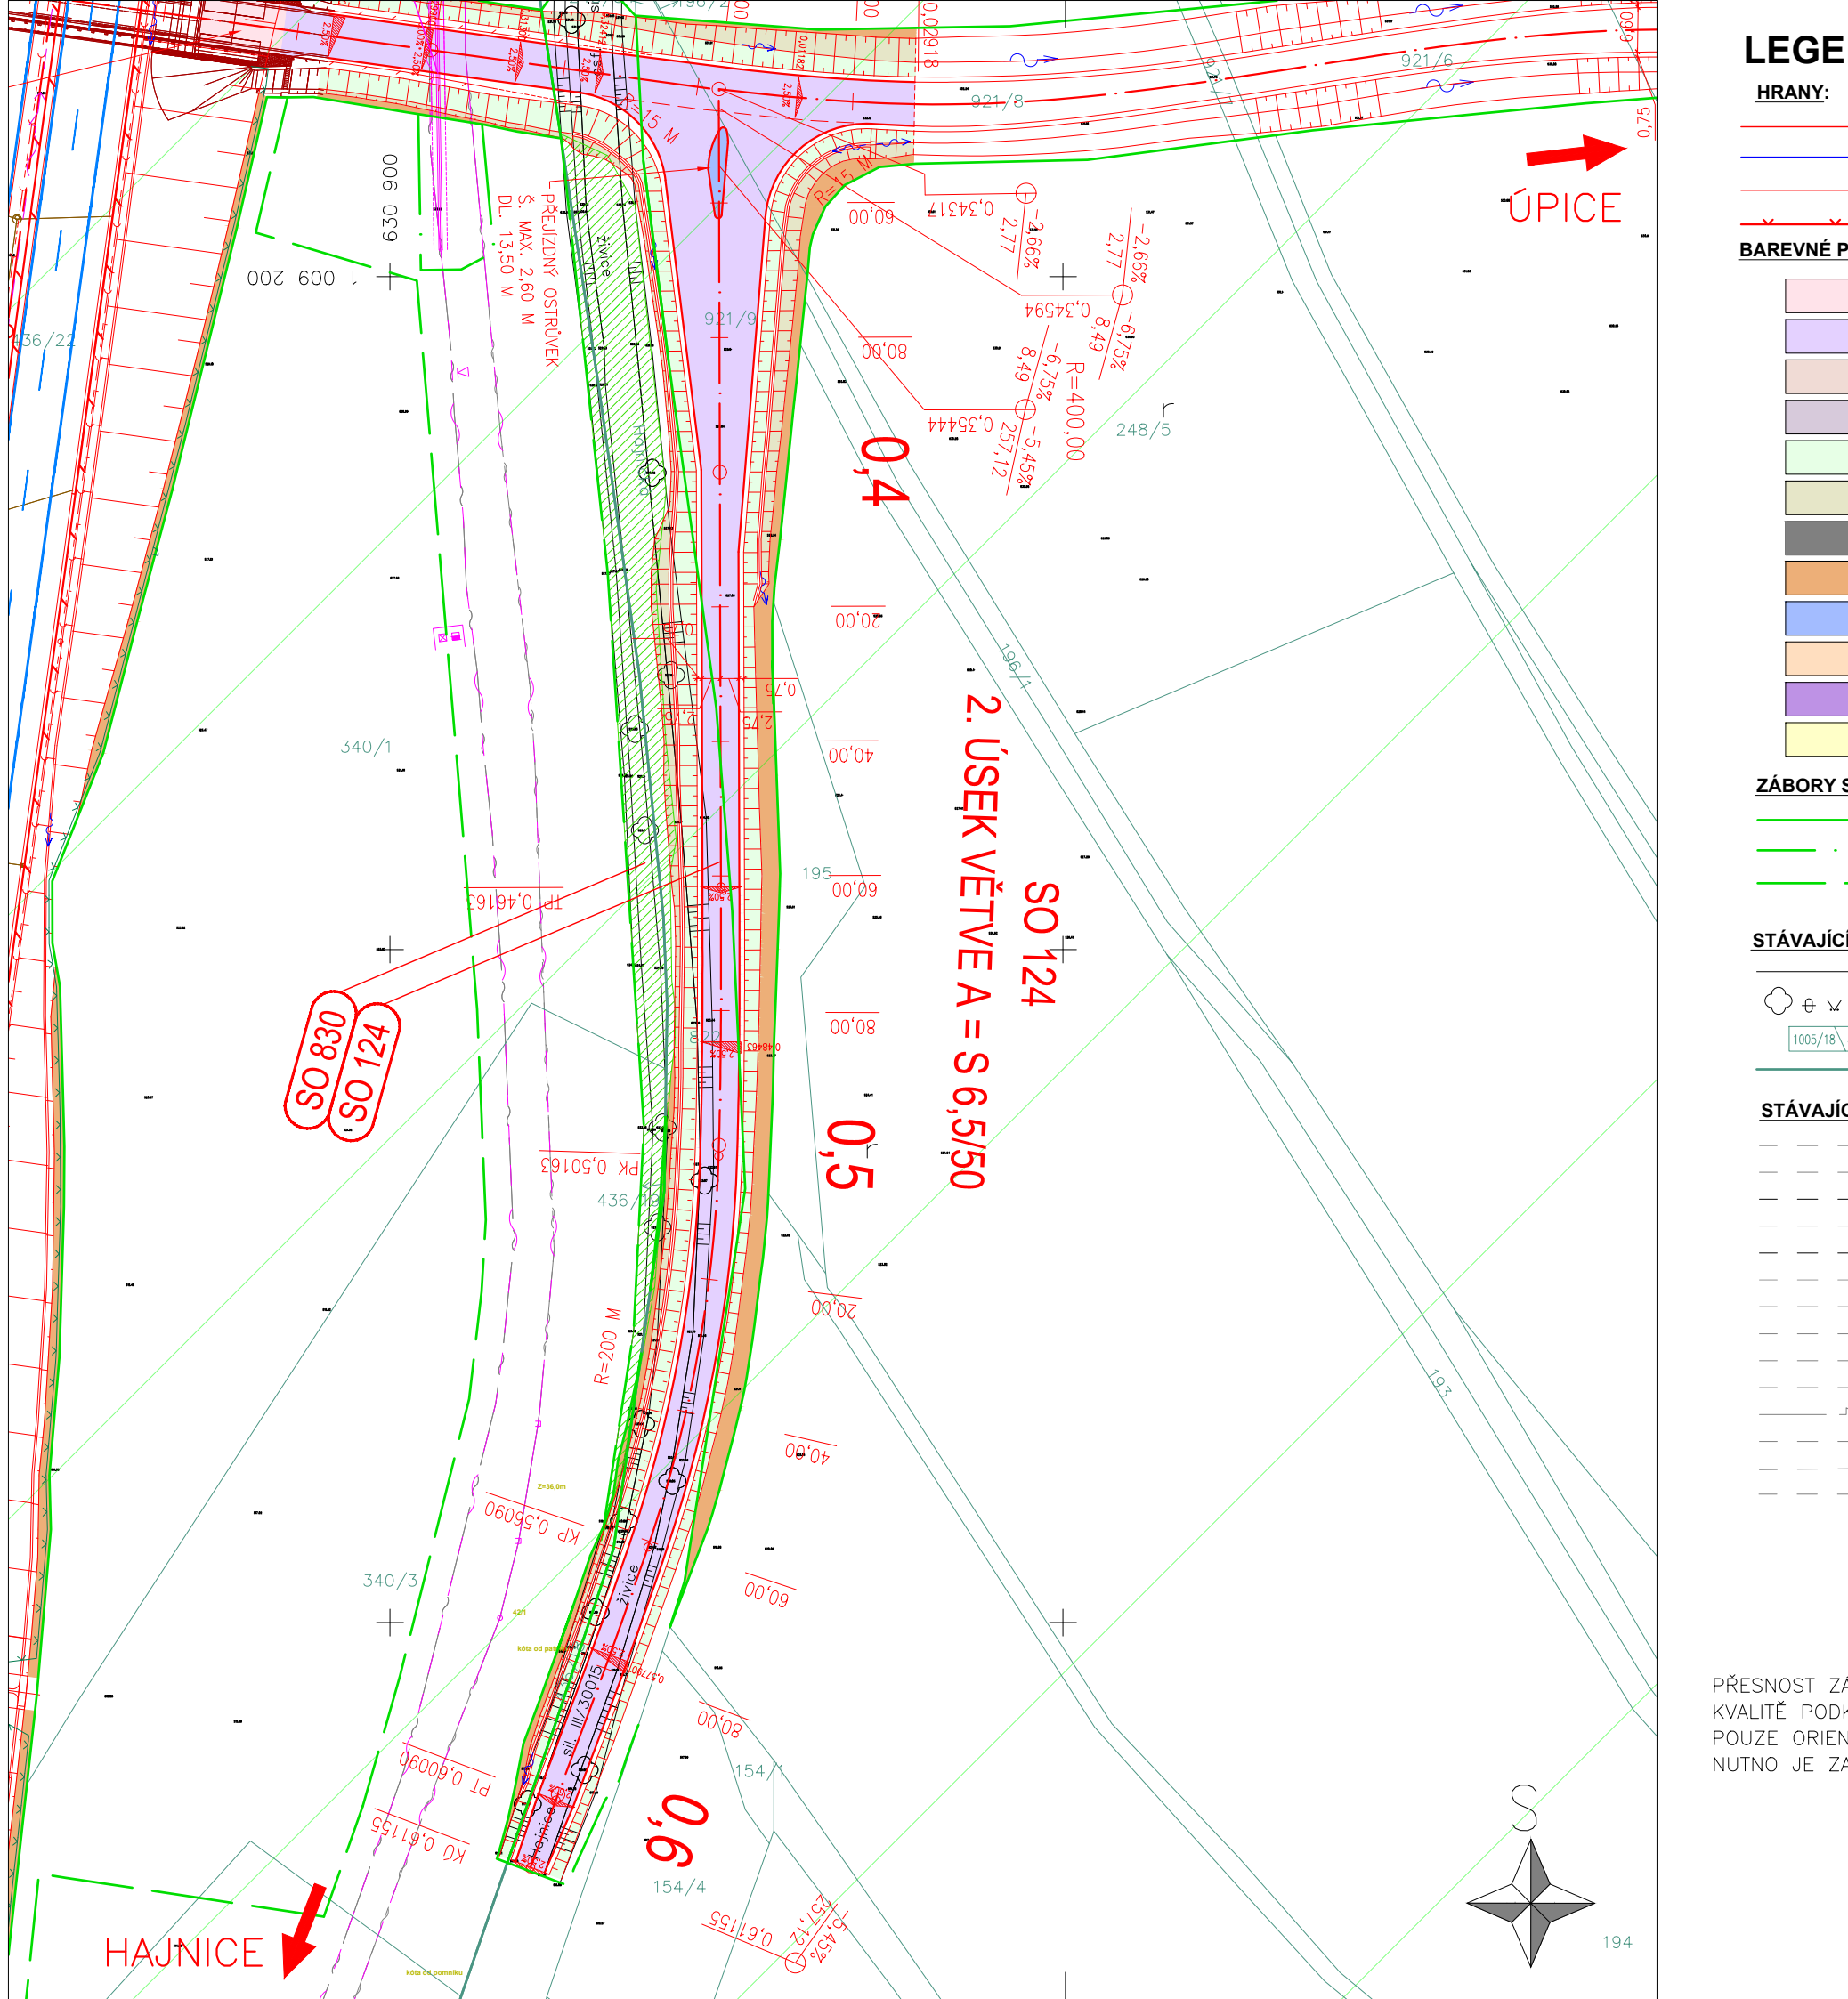


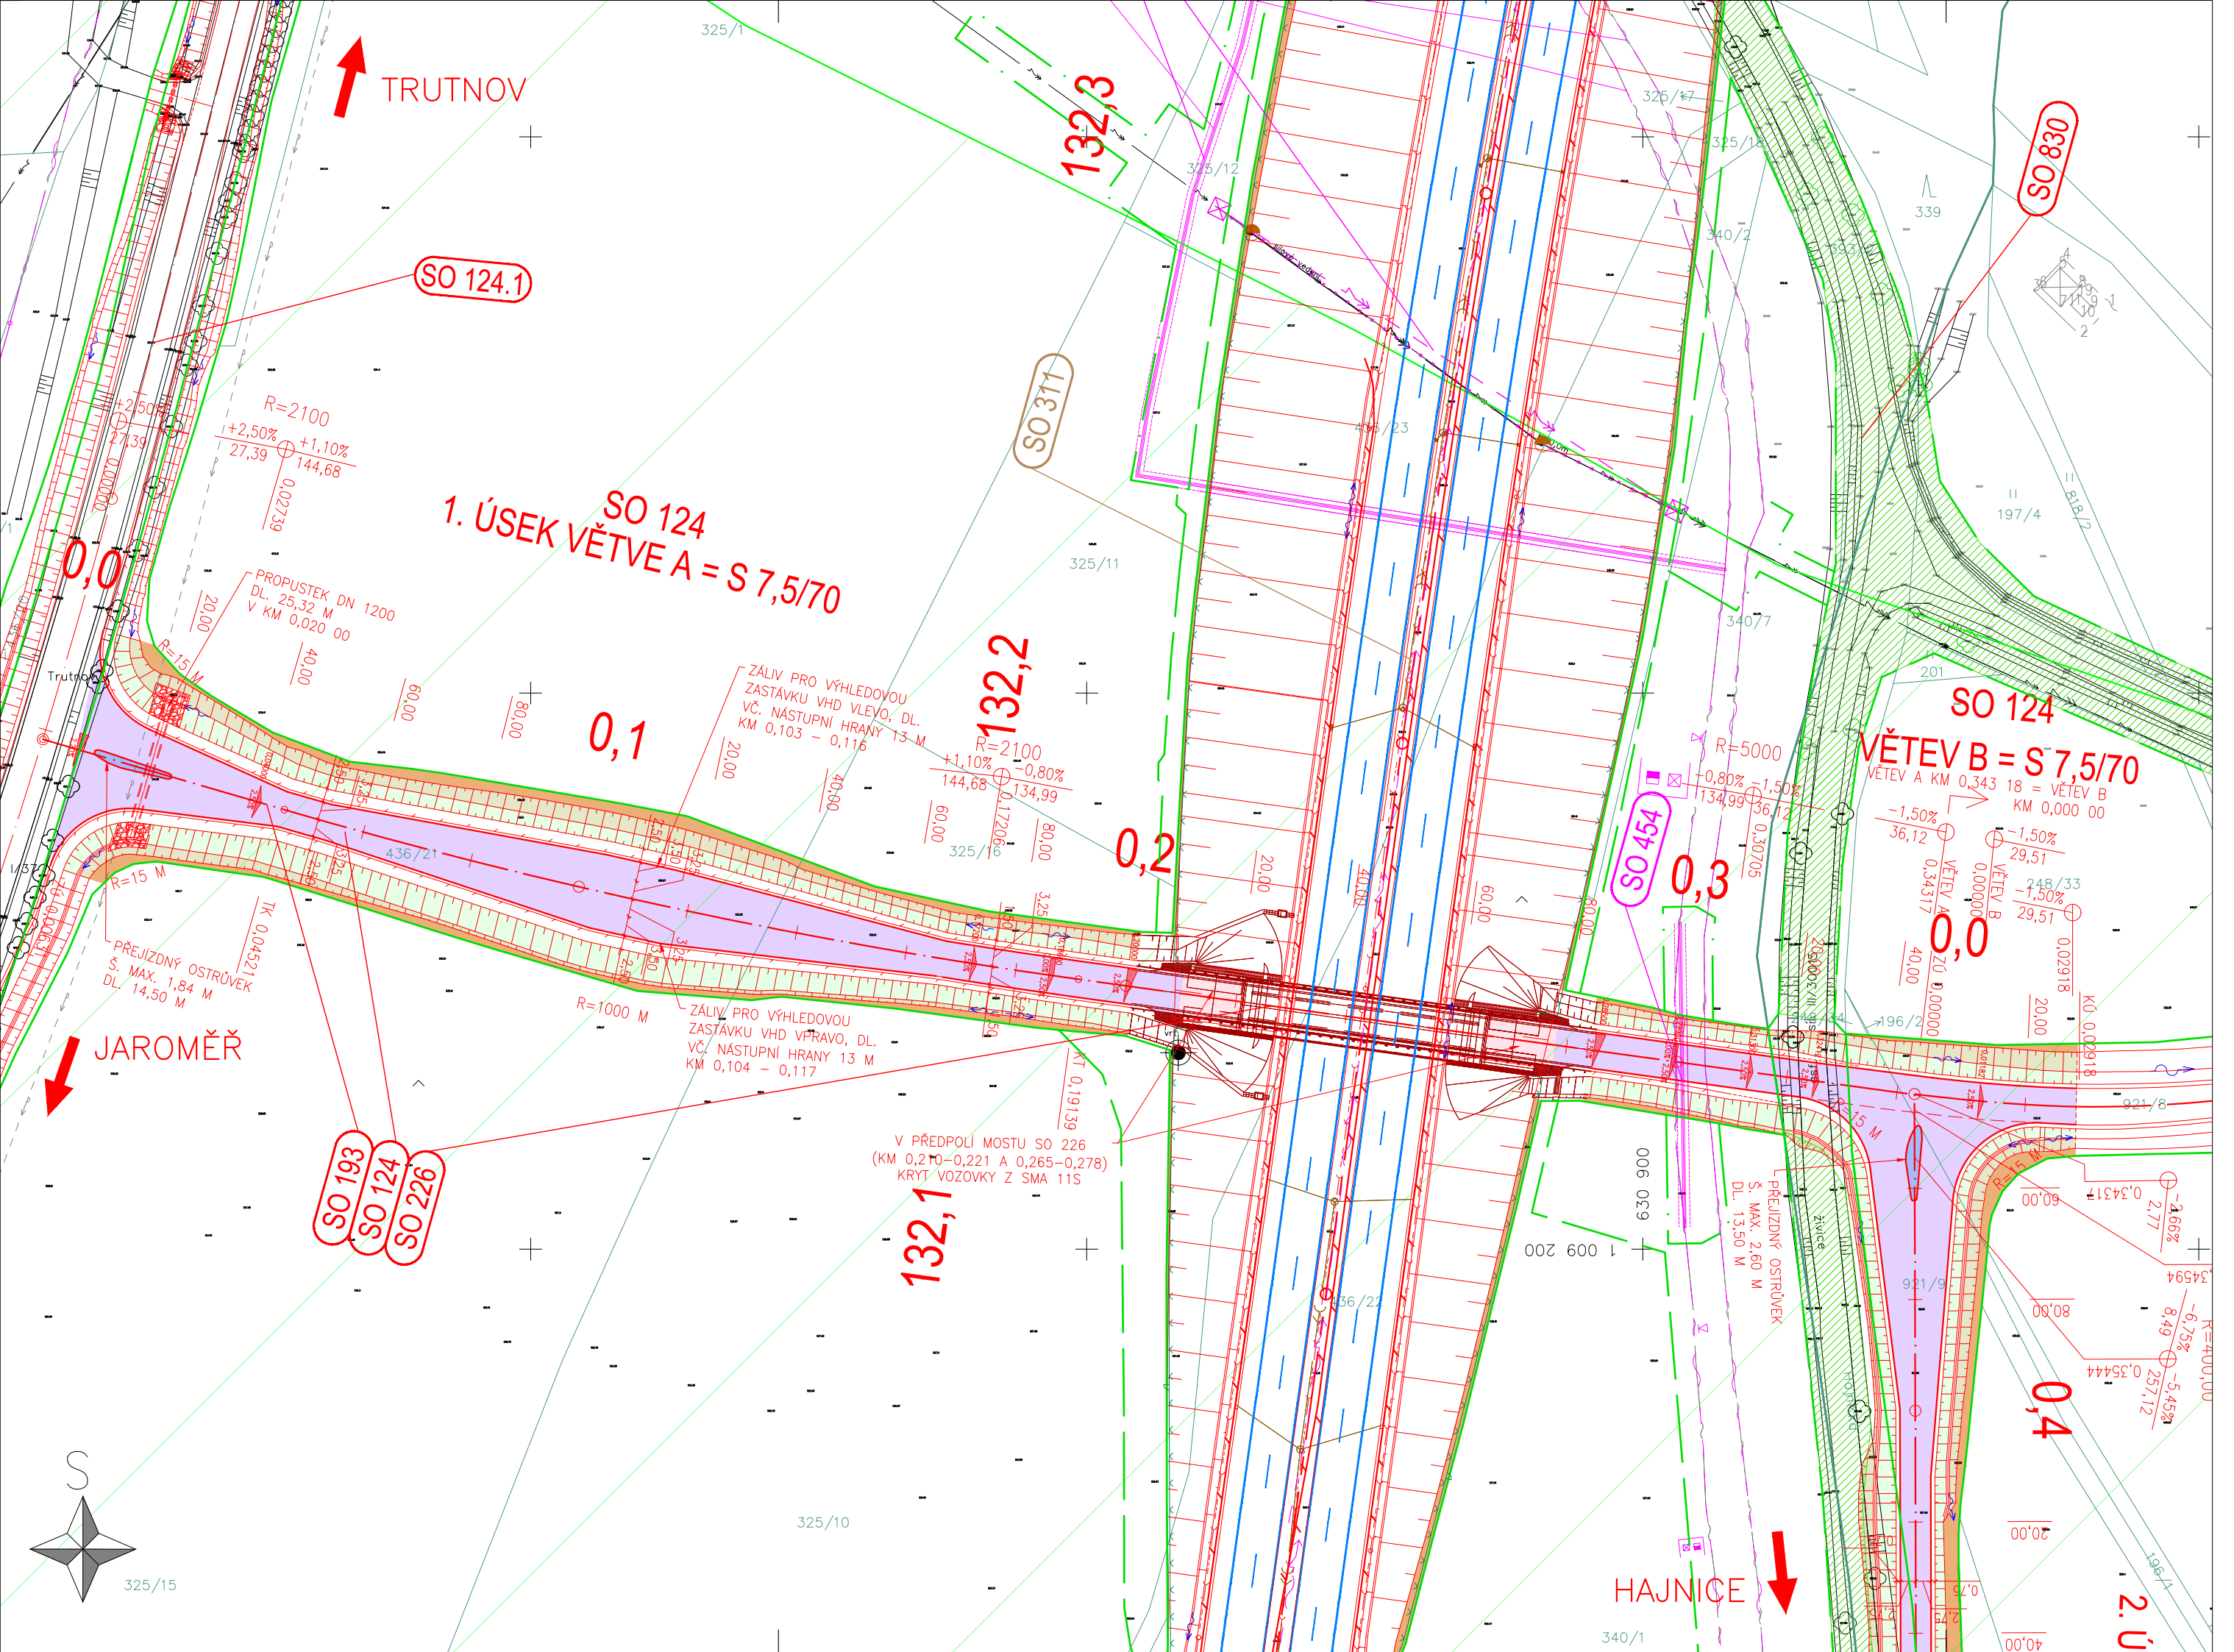

**LEGENDA**  
**HRANY:**

- Nově navržené hrany trvalých SO
- Nově navržené hrany provizorních komunikací
- Související investice
- Oplocení

**BAREVNÉ PLOCHY:**

- Vozovka D11 – asfaltový kryt
- Vozovka silnic a MK
- Zpevněná polní cesta/úcelová komunikace – asfaltový kryt
- Nezpevněná polní cesta/úcelová komunikace – nestmelený kryt
- Násyp
- Zářez
- Technologické napojení na stav.vrstvy
- Úprava terénu v rovině
- Ostrůvky pojízdné
- Ostrůvky nepojízdné
- Prstenec okružní křižovatky
- Chodník

**ZÁBORY STAVBY:**

- Záběr trvalý
- Záběr dočasný – do 1 roku
- Záběr dočasný – nad 1 rok

**STÁVAJÍCÍ POLOHOPIS:**

- Stávající polohopis
- Stávající stav – strom, neplod.přda, park, std.
- Stávající hranice parcel KN
- Stávající polohopis katastrálního území

**STÁVAJÍCÍ INŽ. SÍTĚ:**

- Sdělovací – nadzemní
- Sdělovací – podzemní
- Silnoproudé vedení – NN podzemní
- Silnoproudé vedení – NN nadzemní
- Silnoproudé vedení – VN nadzemní
- Silnoproudé vedení – VN podzemní
- Silnoproudé vedení – VVN nadzemní
- Plynovod – NTL
- Plynovod – STL
- Plynovod – VTL
- veřejné osvětlení
- Vodovod
- Vodovod – pitná
- Kanalizace – bez rozlišení

PŘESNOST ZAKRESŮ STÁVAJÍCÍCH INŽENÝRSKÝCH SÍTÍ ODPOVÍDÁ KVALITĚ PODKLADŮ JEJICH SPRÁVCŮ. ZAKRESLENÁ VEDENÍ JSOU POUZE ORIENTAČNÍ A PŘED ZAHÁJENÍM STAVEBNÍCH PRACÍ JE NUTNO JE ZA ÚČASTI JEJICH SPRÁVCŮ VYTÝČIT.

# SO 124

## D.1.1

VÝŠKOVÝ SYSTÉM BpV

SOUŘADNICOVÝ SYSTÉM S-JTSK

| Číslo změny: | Obsah změny: | Datum změny: |
|--------------|--------------|--------------|
| 01           | -            | -            |
| 02           | -            | -            |
| 03           | -            | -            |

Objednatel:

Ředitelství silnic a dálnic s. p.  
Na Pankráci 546/56, 140 00 Praha 4

Stavbu zajišťuje Závod Praha  
Na Pankráci 546/56, 140 00 Praha 4

Zhotovitel: Společnosti ve sdružení

SG\_Velké projekty BIM 2020  
zastoupené

SUDOP PRAHA a.s.  
Hlavní inženýr projektu: Ing. Roman Petřík

Olšanská 1a, 130 80 Praha 3  
telefon: +420 267 094 111

Správce:

SUDOP PRAHA a.s.  
Olšanská 1a, 130 80 Praha 3  
tel.: +420 267 094 111  
e-mail: praha@sudop.cz

Vedoucí týmu:

ING. ROMAN PETŘÍK

Asistent vedoucího týmu:

ING. PAVEL MICHL

Specialista profese:

-

Zpracovatel částí:

PUDIS projektová, průzkumná a konzultační společnost  
PUDIS a.s., Podbabská 1014/20, 160 00 Praha 6  
tel.: +420 267 004 111, www.pudis.cz, info@pudis.cz

| Vedoucí střediska:     | Odpovědný projektant SO, IO, PS: | Vypracoval:     | Kontroloval:      |
|------------------------|----------------------------------|-----------------|-------------------|
| ING. ZDENKA BOLEHOVSKÁ | ING. MICHAL TUREK                | ING. TOMÁŠ VÁŇA | ING. MICHAL TUREK |

Název akce:

D11 1108 Jaroměř - Trutnov VD-ZDS + TP + AD

Část:

D.1.1 OBJEKTY POZEMNÍCH KOMUNIKACÍ VČETNĚ PROPUSTKŮ  
SO 124 PŘELOŽKA SILNICE III/30015 (KM 132,22)

Název přílohy:

SITUACE

| Číslo smlouvy: | Projektový stupeň: | Datum:  | Číslo části: | Měřítko: | Počet formátů: | Číslo přílohy: |
|----------------|--------------------|---------|--------------|----------|----------------|----------------|
| 22-014.250     | VD-ZDS             | 11/2024 | D.1.1        | 1:1000   | 5xA4           | 2              |

DOKUMENT LZE UŽÍVAT POUZE VE SMYSLU PŘÍSLUŠNÉ SMLOUVY O DÍLO. ŽÁDNÁ JEHO ČÁST NEMŮŽE BYTÍ DLE ZÁKONA Č.121/2000 Sb. KOPÍROVÁNA NEBO JINÝM ZPŮSOBEM ROZŠÍŘOVÁNA. BEZ SOUHLASU SUDOP PRAHA a.s.