


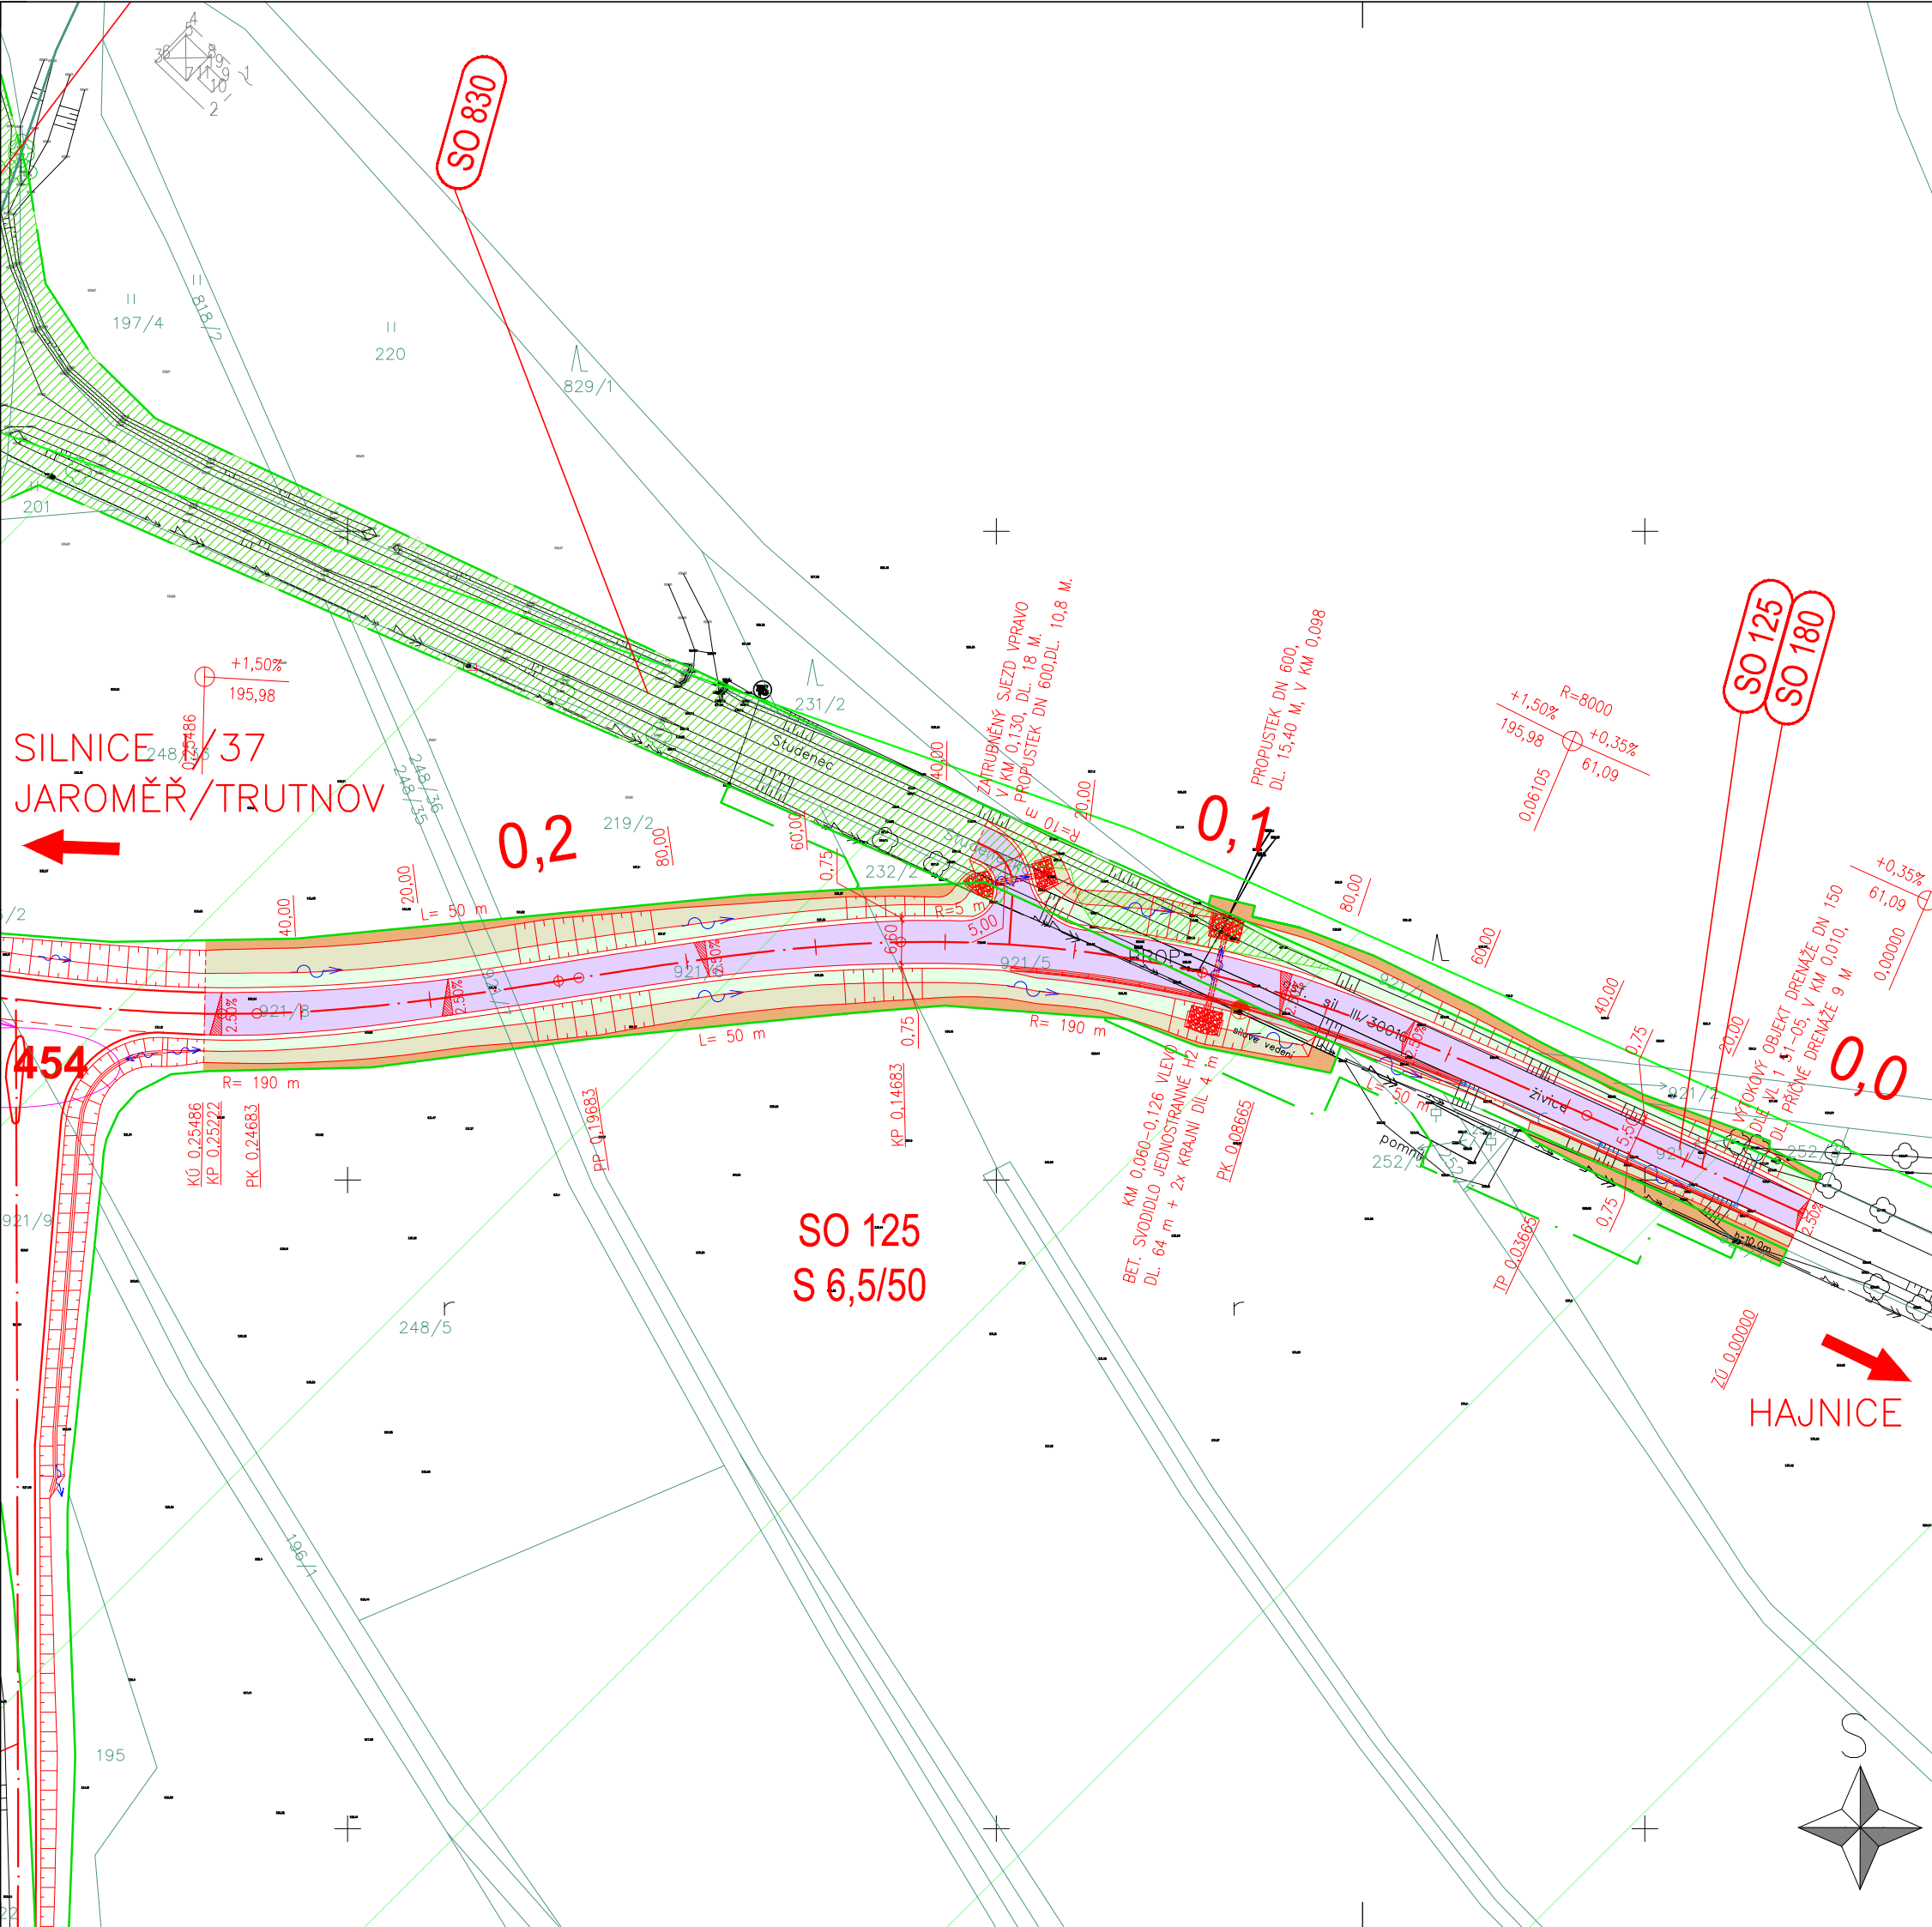

LEGENDA

- HRANY:**
- Nově navržené hrany trvalých SO
 - Nově navržené hrany provizorních komunikací
 - Související investice
 - Oplocení
- BAREVNÉ PLOCHY:**
- Vozovka D11 – asfaltový kryt
 - Vozovka silnic a MK
 - Zpevněná polní cesta/účelová komunikace – asfaltový kryt
 - Nezpevněná polní cesta/účelová komunikace – nestmelený kryt
 - Násyp
 - Zářez
 - Technologické napojení na stav.vrstvy
 - Úprava terénu v rovině
 - Ostrůvky pojížděné
 - Ostrůvky nepojížděné
 - Prstenec okružní křižovatky
 - Chodník

- ZÁBORY STAVBY:**
- Zábor trvalý
 - Zábor dočasný – do 1 roku
 - Zábor dočasný – nad 1 rok
- STÁVAJÍCÍ POLOHOPIS :**
- Stávající polohopis
 - Stávající stav – strom, neplod.půda, park, std.
 - Stávající hranice parcel KN
 - Stávající polohopis katastrálního území
- STÁVAJÍCÍ INŽ. SÍTĚ :**
- Sdělovací – nadzemní
 - Sdělovací – podzemní
 - Silnoproudé vedení – NN podzemní
 - Silnoproudé vedení – NN nadzemní
 - Silnoproudé vedení – VN nadzemní
 - Silnoproudé vedení – VN podzemní
 - Silnoproudé vedení – VVN nadzemní
 - Plynovod – NTL
 - Plynovod – STL
 - Plynovod – VTL
 - VO – veřejné osvětlení
 - Vodovod
 - Vodovod – pitná
 - Kanalizace – bez rozlišení

PŘESNOST ZÁKRESŮ STÁVAJÍCÍCH INŽENÝRSKÝCH SÍTÍ ODPOVÍDÁ KVALITĚ PODKLADŮ JEJICH SPRÁVCŮ. ZAKRESLENÁ VEDENÍ JSOU POUZE ORIENTAČNÍ A PŘED ZAHÁJENÍM STAVEBNÍCH PRACÍ JE NUTNO JE ZA ÚČASTI JEJICH SPRÁVCŮ VYTÝČIT.

SO 125
D.1.1

VÝŠKOVÝ SYSTÉM Bpv SOUŘADNICOVÝ SYSTÉM S-JTSK

Číslo změny:	Obsah změny:	Datum změny:
01	-	-
02	-	-
03	-	-

Objednatel:
**ŘEDITELSTVÍ SILNIC A DÁLNIC**

Ředitelství silnic a dálnic s. p.
Na Pankráci 546/56, 140 00 Praha 4

Stavbu zajišťuje Závod Praha
Na Pankráci 546/56, 140 00 Praha 4

Zhotovitel: Společníci ve sdružení

SG_Velké projekty_BIM 2020
zastoupené

SUDOP PRAHA a.s.
Hlavní inženýr projektu: Ing. Roman Petřík

Olšanská 1a, 130 80 Praha 3
telefon: +420 267 094 111



Správce:
**SUDOP PRAHA**

SUDOP PRAHA a.s.
Olšanská 1a, 130 80 Praha 3
tel.: +420 267 094 111
e-mail: praha@sudop.cz

Vedoucí týmu:
ING. ROMAN PETŘÍK

Asistent vedoucího týmu:
ING. PAVEL MICHL
Specialista profese:
-

Zpracovatel částí:
**PUDIS**

projektová, průzkumná a konzultační společnost
PUDIS a.s., Podbabská 1014/20, 160 00 Praha 6
tel.: +420 267 004 111, www.pudis.cz, info@pudis.cz

Vedoucí střediska:	Odpovědný projektant SO, IO, PS:	Vypracoval:	Kontroloval:
ING. ZDEŇKA BOLEHOVSKÁ	ING. MICHAL TUREK	BC. ZARRINA UTEULINA	ING. MICHAL TUREK

Název akce:	Číslo smlouvy: 22-014.250
D11 1108 Jaroměř - Trutnov VD-ZDS + TP + AD	Projektový stupeň: VD-ZDS
Část: D.1.1 OBJEKTY POZEMNÍCH KOMUNIKACÍ VČETNĚ PROPUSTKŮ SO 125 PŘELOŽKA III/30016 (KM 132,15)	Datum: 11/2024
Název přílohy:	Číslo částí: D.1.1
SITUACE	Měřítko: 1:1000
	Počet formátů: 3xA4
	Číslo přílohy: 2