POZNÁMKA:

I. ZÁKRESY INŽENÝRSKÝCH SÍTÍ:
JSOU JEJICH OVĚŘENÍ A VYTYČENÍ V CELÉM ZÁJMOVÉM ÚZEMÍ STAVBY.

II. OCHRANNÁ A BEZPEČNOSTNÍ PÁSMA:

Ochranná pásma silnic:

DÁLNICE, RYCHLOSTNÍ SILNICE, RYCHLOSTNÍ MK
100 m(od osy přilehlého jízdního pásu nebo osy větve)

OSTATNÍ SILNICE I. TŘ., MK I. TŘÍDY
50 m (od osy vozovky nebo osy přilehlého jízdního pásu)

SILNICE II. a III. TŘ. a MK II. TŘ.
15 m (od osy vozovky nebo osy přilehlého jízdního pásu)

Ochranná pásma dráhy jsou dle CELOSTÁTNÍ DRÁHA, REGIONÁLNÍ DRÁHA
60 m od osy krajní koleje (nejméně však 30 m od hranic obvodu dráhy)

Ochranná pásma

Elektro nadzemní vedení:

NAPĚTÍ DO 1 kV	1 m(od krajního vodiče)
NAPĚTÍ NAD 1 kV DO 35 kv VČETNĚ	7 m(od krajního vodiče)
NAPĚTÍ NAD 35 kV DO 110 kV VČETNĚ	12 m(od krajního vodiče)
NAPĚTÍ NAD 110 kV DO 220 kV VČETNĚ	15 m(od krajního vodiče)
NAPĚTÍ NAD 220 kV DO 400 kV VČETNĚ	20 m(od krajního vodiče)
NAPĚTÍ NAD 400 kV	30 m(od krajního vodiče)

Elektro podzemní vedení:

SDĚLOVACÍ KABELOVÁ VEDENÍ MÍSTNÍ I DÁLKOVÁ	1,5 m(od krajního kabelu)
SILNOPROUDÁ VEDENÍ DO 110 kV VČETNĚ	1 m(po obou stranách krajního kabelu)
SILNOPROUDÁ VEDENÍ NAD 110 kV VČETNĚ	3 m(po obou stranách krajního kabelu)

U vedení, která byla realizována do roku 1994, se ochranná pásma stanovují podle původních předpisů.

Vodovody a kanalizace:

VODOVODNÍ POTRUBÍ DO DN 500 VČETNĚ	1,5 m(od okraje potrubí)
VODOVODNÍ POTRUBÍ NAD DN 500	2,5 m(od okraje potrubí)
KANALIZACE DO DN 500 VČETNĚ	1,5 m (od okraje stoky)
KANALIZACE NAD DN 500	2,5 m(od okraje stoky)

Plynovody:

Ochranná NTL a STL PLYNOVODY	1 m (od půdorysu)
OSTATNÍ PLYNOVODY A TECHNOLOGICKÉ OBJEKTY	4 m (od půdorysu)

Bezpečnostní pásma:

REGULAČNÍ STANICE VYSOKOTLAKÉ		10 m(od půdorysu)
REGULAČNÍ STANICE VELMI VYSOKOTLAKÉ		20 m(od půdorysu)
VYSOKOTLAKÝ PLYNOVOD	DO DN 100	15 m(od půdorysu)
	DO DN 250	20 m(od půdorysu)
	NAD DN 250	40 m(od půdorysu)
VELMI VYSOKOTLAKÉ PLYNOVODY	DO DN 300	100 m(od půdorysu)
	DO DN 500	150 m(od půdorysu)
	NAD DN 500	200 m(od půdorysu)

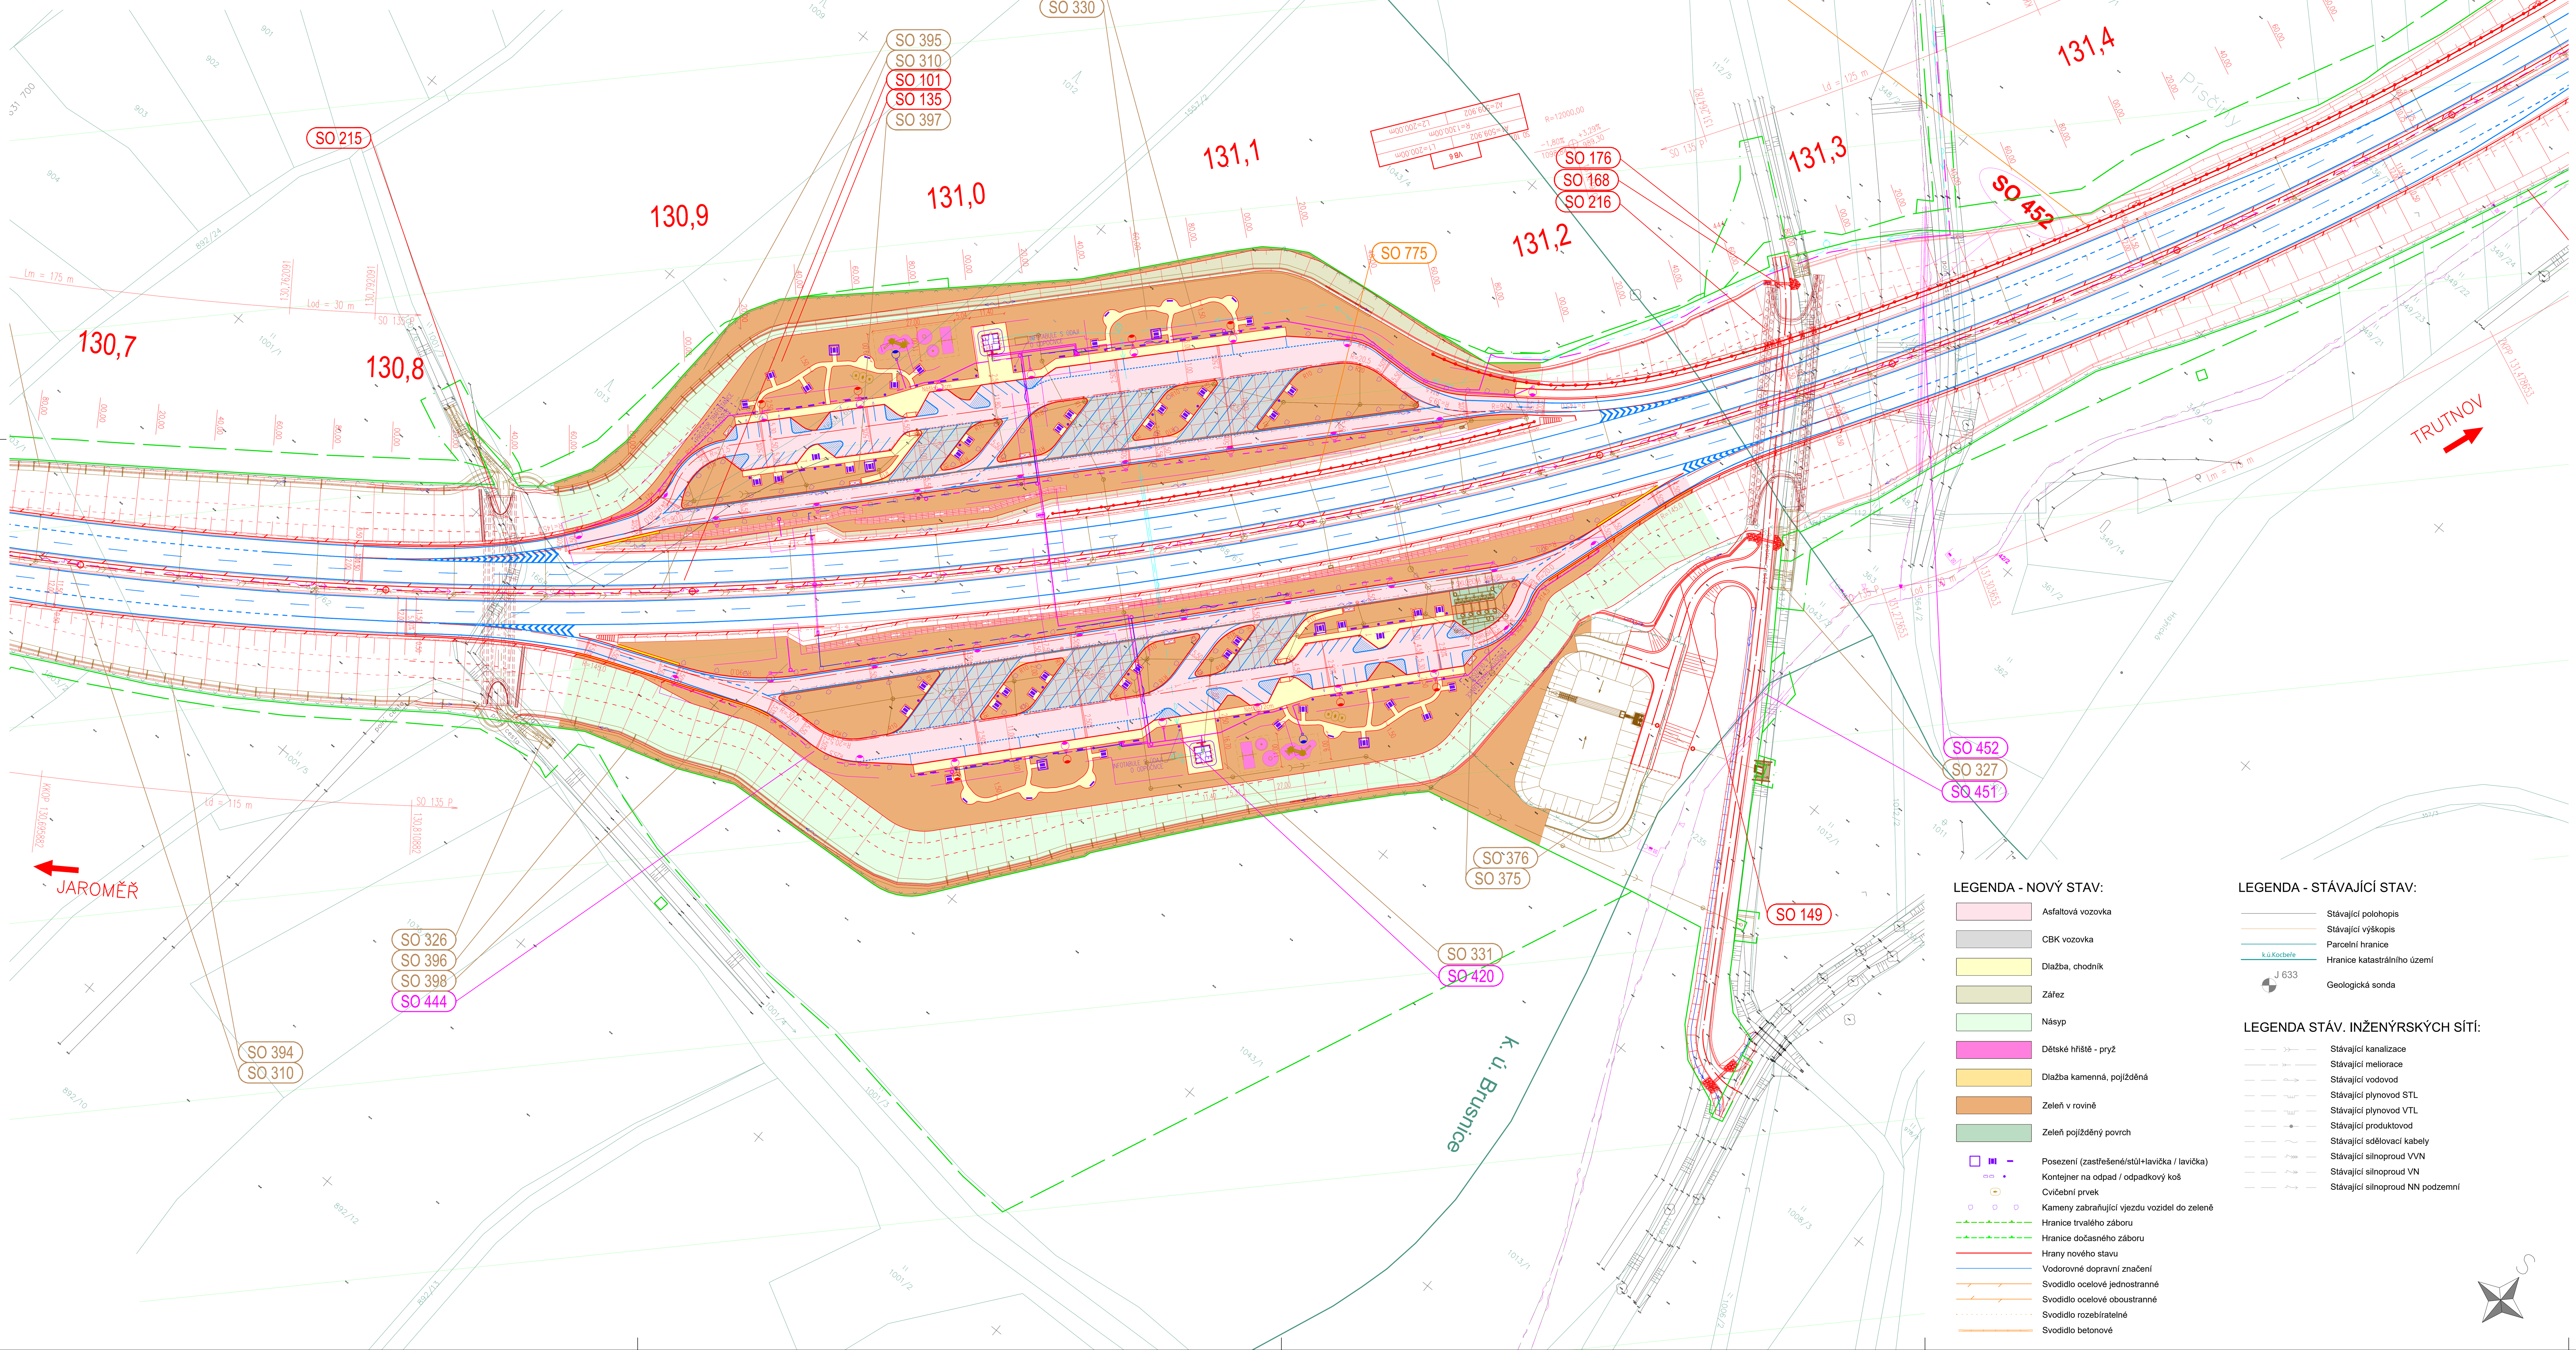

ŘADA 000 - OBJEKTY PŘÍPRAVY STAVENIŠTĚ

SO 020 Příprava území

ŘADA 100 - OBJEKTY POZEMNÍCH KOMUNIKACÍ (VČ. PROPUSTKŮ)

SO 101 Hlavní trasa D11 1108
SO 102 Přeložka silnice I/37 u MÚK Choustníkovo Hradiště
SO 103 Úprava I/37 v km 125,70
SO 110 MÚK Choustníkovo Hradiště
SO 111 MÚK Kocbeře
SO 116 Služební sjezd k Trutnovské podpěře SO 201
SO 117 Služební sjezd k Jaroměřské podpěře SO 201
SO 120 Přeložka místní komunikace v Choustníkově Hradišti (km 118,628)
SO 121 Přeložka silnice III/29926 (km 121,97)
SO 122 Přeložka silnice II/300 (MÚK Kocbeře)
SO 123 Přeložka silnice III/30015 (km127,57)
SO 124 Přeložka silnice III/30015 (km 132,22)
SO 125 Přeložka III/30016 (km 132,15)
SO 126 Přeložka místní komunikace v k.ú. Kocbeře
SO 127 Komunikace pro pěší MÚK Kocbeře
SO 135 Odpočívka Brusnice v km 131,0
SO 140 Příjezd k sedimentační nádrži km 114,68
SO 141 Příjezd k retenční nádrži km 116,82
SO 142 Příjezd k retenční nádrži km 117,25
SO 143 Příjezd k retenční nádrži km 119,55
SO 144 Příjezd k Jaroměřskému portálu tunelu
SO 145 Příjezd k Trutnovskému portálu tunelu
SO 146.1 Příjezd k DUN v km 116,84 vlevo
SO 146.2 Příjezd k DUN v km 119,02 vpravo
SO 147.1 Příjezd k DUN v km 124,35
SO 147.2 Příjezd k retenční nádrži km 124,35
SO 148 Příjezd k retenční nádrži a DUN km 127,55
SO 149 Příjezd k retenční nádrži km 131,2
SO 150 Přístupy na pozemky v k.ú Hořenice
SO 151 Přístupy na pozemky v k.ú Brod n. Lab.
SO 152 Přeložka polní cesty v km 114,75
SO 153 Přeložka polní cesty v km 115,51
SO 154 Přístupy na pozemky v k.ú Slotov
SO 155 Přístupy na pozemky v k.ú Dolní Vlčkovice
SO 156 Přeložka polní cesty v km 116,80
SO 157 Přístupy na pozemky v k.ú Choustníkovo Hradiště
SO 158 Přístupy na pozemky v k.ú Zboží u Dvora Králové
SO 159 Přístupy na pozemky v k.ú Kocbeře
SO 160 Přístupy na pozemky v k.ú Horní Ždár
SO 161 Přístupy na pozemky v k.ú Brusnice ČÁST 1
SO 162 Přeložka lesní cesty v km 124,460 - 124,560
SO 163 Přeložka lesní cesty v km 124,55-124,90 vlevo
SO 164 Přeložka lesní cesty v km 125,37 - 125,80 vlevo
SO 165 Přeložka lesní cesty v km 126,860
SO 166 Přeložka polní cesty v km 128,30 - 128,77
SO 167 Přeložka polní cesty v km 130,30 - 130,50 vlevo
SO 168 Přeložka polní cesty v km 131,25
SO 169 Přeložka polní cesty v km 131,69
SO 170 Provizorní přeložka I/37
SO 171 Provizorní přeložka místní komunikace v Ch. Hradišti km 118,628
SO 172 Provizorní přeložka účelové komunikace km 119,3
SO 173 Provizorní přeložka silnice II/299 km 119,8
SO 174 Provizorní přeložky silnice II/300 MUK Kocbeře
SO 175 Provizorní přeložka silnice III/30015 km 127,5
SO 176 Provizorní přeložka polní cesty km 131,2
SO 177 Provizorní přeložka polní cesty km 131,6
SO 180 Dopravní opatření
SO 186 Stavební úpravy komunikace před, při a po stavbě (úsek ZÚ - MÚK Kocbeře)
SO 187 Stavební úpravy komunikace před, při a po stavbě (úsek MÚK Kocbeře-KÚ)
SO 188 Propustek na II/299
SO 190.1 Svislé a vodorovné dopravní značení ve správě ŘSD
SO 190.2 Portály pro dopravní značení ve správě ŘSD
SO 190.3 Proměnné dopravní značení ve správě ŘSD
SO 191 Dopravní značení - Přeložky silnic I.tř.
SO 193 Dopravní značení - Přeložky silnic II. a III.tř.
SO 194 Dopravní značení - Přeložky místních komunikací

ŘADA 200 - MOSTNÍ OBJEKTY A KONSTRUKCE

SO 201 Most přes údolí Labe v km 114,267
SO 202 Most přes účelovou komunikaci v km 115,510
SO 203 Most přes potok Drahyně v km 116,939
SO 204 Most přes Kocbeřský potok v km 118,903
SO 205 Most přes účelovou komunikaci v km 119,294
SO 206 Most přes meliorační kanál v km 119,420
SO 207 Most přes silnici II/299 v km 119,888
SO 208 Most přes přeložku lesních cest a údolí lesního potoka v km 124.358
SO 209 Most přes lesní cestu a údolí lesního potoka v km 124.878
SO 210 Most přes silnici I/37 v km 125.723
SO 211 Most přes Kocbeřský potok v km 125.780
SO 212 Most přes údolí Hajnického potoka a silnici III/30015 v km 127.366
SO 213 Most přes polní cestu u Tadeášových Domků v km 128.755
SO 214 Most přes údolí a polní cestu v km 130.171
SO 215 Most přes pravý přítok Běluňky v km 130.837
SO 216 Most přes polní cestu a potok Běluňka v km 131.263
SO 217 Most přes polní cestu u obce Střítež v km 131.688
SO 218 Most přes lesní rokli u obce Nová Střítež v km 132.713
SO 221 Nadjezd na I/37 v km 117,871
SO 222 Nadjezd na místní komunikaci v km 118,628
SO 223 Nadjezd na III/299 26 v km 121,973
SO 224 Lávka pro pěší v km 122,483
SO 225 Nadjezd na přeložce silnice II/300 (MÚK Kocbeře) v km 122.923
SO 226 Nadjezd na přeložce silnice III/30015 v km 132.150
SO 227 Ekodukt v km 121,060
SO 241 Podchod pro pěší a cyklisty pod jihozápadní rampou MÚK Kocbeře v km 0.042

ŘADA 300 - VODOHOSPODÁŘSKÉ OBJEKTY

SO 301 Dešťová kanalizace dálnice km 113,370 - 114,100
SO 302 Dešťová kanalizace dálnice km 114,100 - 115,530
SO 303 Dešťová kanalizace dálnice km 115,530 - 116,770
SO 304 Dešťová kanalizace dálnice km 116,770 - 118,970
SO 305 Dešťová kanalizace dálnice km 118,970 - 119,650
SO 306 Dešťová kanalizace dálnice km 119,650 - 124,420
SO 307 Dešťová kanalizace dálnice km 124.310 – 125,700
SO 308 Dešťová kanalizace dálnice km 119,789 – 126.140
SO 309 Dešťová kanalizace dálnice km 126,930 – 128,506
SO 310 Dešťová kanalizace dálnice km 128,550 – 132,130
SO 311 Dešťová kanalizace dálnice km 132,200 – 133,000
SO 320 Úprava potoka Drahyně v km 116,915
SO 321 Přeložka Kocbeřského potoka v km 118,900
SO 322 Úprava pravostr. přít. Kocbeřského potoka v km 124,420
SO 323 Úprava pravostr. přít. Kocbeřského potoka v km 124,980
SO 324 Přeložka Kocbeřského potoka v km 125,780
SO 325 Úprava Hajnického potoka v km 127,423
SO 326 Přeložka pravost. přít. Běluňky v km 130,840
SO 327 Úprava koryta Běluňky v km 131,260
SO 330 Splašková kanalizace a ČOV odpočívky Brusnice – levá strana
SO 331 Splašková kanalizace a ČOV odpočívky Brusnice – pravá strana
SO 340 Přeložka vodvodu PE D63 v km 122,416
SO 341 Přeložka vodvodu L DN150 v km 122,900
SO 342 Přeložka vodvodu L DN150 v km 124,407
SO 343 Přeložka vodvodu PVC D110 v km 127,167
SO 601.48 Přípojka vodovodu pro požární vodovod
SO 344 Přeložka vodvodu L D110 v km 132,964
SO 345 Vodovod a zásobní nádrž odpočívky Brusnice
SO 360 Sedimentační nádrž v km 114,680 včetně odtoku
SO 361 Sedimentační nádrž v km 116,750 včetně odtoku
SO 362 Retenční nádrž v km 116,820 včetně odtoku
SO 363 Sedimentační nádrž v km 117,300 včetně odtoku
SO 364 Retenční nádrž v km 117,250 včetně odtoku
SO 365 Sedimentační nádrž v km 119,020 včetně odtoku
SO 366 Retenční nádrž v km 119,000 včetně odtoku
SO 367 Sedimentační nádrž v km 119,640 včetně odtoku
SO 368 Retenční nádrž v km 119,550 včetně odtoku
SO 369 Sedimentační nádrž v km 124,320 včetně odtoku
SO 370 Retenční nádrž v km 124,400 včetně odtoku
SO 371 Sedimentační nádrž v km 125,750 včetně odtoku
SO 372 Retenční nádrž v km 125,700 včetně odtoku
SO 373 Sedimentační nádrž v km 127,560 včetně odtoku
SO 374 Retenční nádrž v km 127,550 včetně odtoku
SO 375 Sedimentační nádrž v km 131.140 včetně odtoku
SO 376 Retenční nádrž v km 131,200 včetně odtoku
SO 377 Retenční nádrž v km 114,680 včetně odtoku
SO 380 Úprava meliorací km 117,200-119,600
SO 390 Protierozní ochrana km 123.3
SO 391 Levostranný retenční příkop km 124.58 - 124.86
SO 392 Pravostranný retenční příkop km 125.76 - 125.9157
SO 393 Levostranný retenční příkop km 130.6355 – 130.828
SO 394 Pravostranný retenční příkop km 130.6194 - 130.828
SO 395 Levostranný retenční příkop km 130.8592 – 131.0173
SO 396 Pravostranný retenční příkop km 130.848 – 131.062
SO 397 Odvodnění levé strany odpočívky Brusnice km 130.9 – 131.15
SO 398 Odvodnění pravé strany odpočívky Brusnice km 130.9 – 131.15

ŘADA 400 - ELEKTRO A SDĚLOVACÍ OBJEKTY

SO 401 Úprava nadzemního vedení VVN (2x110kV) km 113,6
SO 410 Úprava nadzemního vedení VN (1x35kV) v km 114,65
SO 411 Úprava nadzemního vedení VN (2x35kV) v km 115,2
SO 412 Úprava nadzemního vedení VN (1x35kV) v km 116,7
SO 413 Úprava podzemního vedení VN (1x35kV) v km 117,4
SO 414 Úprava nadzemního vedení VN (1x35kV) v km 119,6
SO 415 Úprava nadzemního vedení VN (1x35kV) v km 120,6
SO 416 Úprava nadzemního vedení VN (1x35kV) v km 122,4
SO 417 Úprava nadzemního vedení VN (1x35kV) v km 122,75-123,1
SO 418 Úprava nadzemního vedení VN (1x35kV) v km 128,6
SO 419 Úprava nadzemního vedení VN (2x35kV) v km 129,4-130,0
SO 420 Úprava nadzemního vedení VN (1x35kV) v km 132,3
SO 421 Přemístění jednosloupové trafostanice 35/0,4kV v km 114,65
SO 430 Úprava vedení NN kabelizace (1x1kV) v km 127,1
SO 431 Úprava vedení NN kabelizace (1x1kV) v km 128,3
SO 432 Úprava veřejného osvětlení v km 118,6
SO 433 Úprava hlavního domovního vedení k vysílači v km 114,65
SO 434 Přípojka VN pro Tunel Kamenný vrch
SO 439 Rozvod 1kV - odpočívky Brusnice
SO 444 Veřejné osvětlení - odpočívky Brusnice

ŘADA 400 - ELEKTRO A SDĚLOVACÍ OBJEKTY

SO 490 Přípojky vedení NN pro systém DIS
SO 490.1 Přípojné místo ČEZ v km 114,2
SO 490.2 Přípojné místo ČEZ v km 118,65
SO 490.3 Přípojné místo ČEZ 124
SO 490.5 Přípojné místo ČEZ 131,4
SO 491.1 Elektroměr ŘSD+ vedení 1kV do RM3 v km 118,6
SO 491.2 Elektroměr ŘSD+ vedení 1kV do RM3 v km 124
SO 491.4 Elektroměr ŘSD+ vedení 1kV do RM3 v km 114,1
SO 491.5 Elektroměr ŘSD + vedení 1kV do R1

ŘADA 400 - ELEKTRO A SDĚLOVACÍ OBJEKTY

SO 450 Přeložka podzemního vedení CETIN a.s. v km 119,809-119,905
SO 451 Přeložka podzemního vedení CETIN a.s. v km 131,180-131,227
SO 452 Přeložka podzemního vedení CETIN a.s. v km 131,395-131,328
SO 453 Přeložka podzemního vedení CETIN a.s. v km 131,540-131,686
SO 454 Přeložka podzemního vedení CETIN a.s. v km 132,122-132,175
SO 455 Přeložka podzemního vedení CETIN a.s. v km 132,251-132,398
SO 460 Přeložka nadzemního vedení CETIN a.s. v km 117,611-118,192
SO 461 Přeložka podzemního vedení CETIN a.s. v km 118,588-118,630
SO 462 Úprava podzemního vedení CETIN a.s. v km 118,609-118,639
SO 463 Přeložka podzemního vedení CETIN a.s. v km 121,849-121,867
SO 464 Přeložka podzemního vedení CETIN a.s. v km 121,789-121,850
SO 465 Přeložka podzemního vedení CETIN a.s. v km 121,973-121,998
SO 466 Úprava podzemního vedení CETIN a.s. v km 122,438-122,480
SO 467 Úprava podzemního vedení CETIN a.s. v km 122,856-122,924
SO 468 Úprava podzemního vedení CETIN a.s. v km 125,649-125,814
SO 469 Přeložka podzemního vedení CETIN a.s. v km 127,464-127,526
SO 491 Systém DIS-SOS-kabelové vedení
SO 492 Systém DIS-SOS-hlásky
SO 493 Systém DIS-SOS - šachty a prostupy
SO 494 Systém DIS-SOS - trubky pro optické kabely
SO 495 Systém DIS-SOS - meteostanice
SO 496 Systém DIS-SOS - automatické sčítače dopravy
SO 497 Systém DIS-SOS - kamerový dohled
SO 498 Systém DIS-SOS - optické kabely ŘSD
SO 499 Systém DIS-SOS - doplňkové objekty
SO 499.1 Dálniční informační systém DIS
SO 499.2 Elektrické závory
SO 499.3 Rozvod v komorách mostů
SO 499.4 EZS
SO 499.5 Úpravy na dispečinku SSÚD a PČR
SO 499.6 WIM
SO 499.7 Vykrývací radiostanice pro údržbu

ŘADA 500 - OBJEKTY TRUBNÍCH VEDENÍ

SO 520 Úprava STL plynovodu v km 118,667

ŘADA 600 - OBJEKTY PODZEMNÍCH STAVEB

SO 601 Tunel Kamenný vrch

ŘADA 650 - OBJEKTY DRAH

neobsazeno

ŘADA 700 - OBJEKTY POZEMNÍCH STAVEB

SO 760 PHS v km 114,010 – 114,970 vlevo
SO 761 PHS v km 114,010 – 114,970 vpravo
SO 762 PHS v km 116,720 – 117,440 vlevo
SO 763 PHS v km 116,770 – 117,270 vpravo
SO 764 PHS v km 117,940 – 119,120 vlevo
SO 765 PHS v km 118,470 – 119,980 vpravo
SO 766 PHS v km 120,160 – 120,850 vpravo
SO 767 PHS v km 121,970 – 122,340 vlevo
SO 768 PHS v km 122,000 – 122,470 vpravo
SO 769 PHS v km 123,680 – 124,300 vpravo
SO 770 PHS v km 124,530 – 124,810 vpravo
SO 771 PHS v km 125,910 – 126,150 vlevo
SO 772 PHS v km 126,920 – 127,500 vpravo
SO 773 PHS v km 126,920 – 127,550 vlevo
SO 774 PHS v km 128,010 – 129,170 vlevo
SO 775 PHS v km 131,020 – 131,920 vlevo
SO 776 PHS v km 132,670 – KÚ vlevo

ŘADA 800 - OBJEKTY ÚPRAVY ÚZEMÍ

SO 801 Vegetační úpravy správce ŘSD
SO 806 Vegetační úprava sil. II a III.tř.
SO 830 Technické rekultivace
SO 860 Oplocení dálnice

ŘADA 900 - VOLNÁ ŘADA

SO 900 Ochrana D11 1108 před vandalismem a zcizováním majetku státu

LEGENDA - NOVÝ STAV:

- Asfaltová vozovka
- CBK vozovka
- Dlažba, chodník
- Zářez
- Násyp
- Dětské hřiště - pryž
- Dlažba kamenná, pojížděná
- Zeleň v rovině
- Zeleň pojížděný povrch
- Posezení (zastřešené/stůl+lavička / lavička)
- Kontejner na odpad / odpadkový koš
- Cvičební prvek
- Kameny zabraňující vjezdu vozidel do zeleně
- Hranice trvalého záboru
- Hranice dočasného záboru
- Hrany nového stavu
- Vodorovné dopravní značení
- Svodidlo ocelové jednostranné
- Svodidlo ocelové oboustranné
- Svodidlo rozebíratelné
- Svodidlo betonové

LEGENDA - STÁVAJÍCÍ STAV:

- Stávající polohopis
- Stávající výškopis
- Parcelní hranice
- k.ú.Kocbeře — Hranice katastrálního území
- J 633 — Geologická sonda

LEGENDA STÁV. INŽENÝRSKÝCH SÍTÍ:

- Stávající kanalizace
- Stávající meliorace
- Stávající vodovod
- Stávající plynovod STL
- Stávající plynovod VTL
- Stávající produktovod
- Stávající sdělovací kabely
- Stávající silnoproud VVN
- Stávající silnoproud VN
- Stávající silnoproud NN podzemní

SO 135
D.1.1

VÝŠKOVÝ SYSTÉM Bpv — SOUŘADNICOVÝ SYSTÉM S-JTSK

Číslo změny:	Obsah změny:	Datum změny:
01	-	-
02	-	-
03	-	-

Objednatel: ŘEDITELSTVÍ SILNIC A DÁLNIC
Ředitelství silnic a dálnic s. p.
Na Pankráci 546/56, 140 00 Praha 4
Stavbu zajišťuje Závod Praha
Na Pankráci 546/56, 140 00 Praha 4

Zhotovitel: Společníci ve sdružení SG_Velké projekty_BIM 2020 zastoupené
SUDOP PRAHA a.s.
Hlavní inženýr projektu: Ing. Roman Petřík
Olšanská 1a, 130 80 Praha 3
telefon: +420 267 094 111

Správce: SUDOP PRAHA a.s., Olšanská 1a, 130 80 Praha 3, tel.: +420 267 094 111, e-mail: praha@sudop.cz

Vedoucí týmu:	Asistent vedoucího týmu:	Specialista profese:
ING. ROMAN PETŘÍK	ING. PAVEL MICHL	-

Zpracovatel části: PUDIS — projektová, průzkumná a konzultační společnost
PUDIS a.s., Podbabská 1014/20, 160 00 Praha 6
tel.: +420 267 004 111, www.pudis.cz, info@pudis.cz

Vedoucí střediska:	Odpovědný projektant SO, IO, PS:	Vypracoval:	Kontroloval:
ING. ZDEŇKA BOLEHOVSKÁ	ING. MICHAL TUREK	PETR KOTLABA	ING. MICHAL TUREK

Název akce: **D11 1108 Jaroměř - Trutnov VD-ZDS + TP + AD**	Číslo smlouvy: 22-014.250
	Projektový stupeň: VD-ZDS
Část: D.1.1 OBJEKTY POZEMNÍCH KOMUNIKACÍ VČETNĚ PROPUSTKŮ **SO 135 ODPOČÍVKA BRUSNICE V KM 131,0**	Datum: 11/2024
	Číslo části: D.1.1
Název přílohy: **SITUACE**	Měřítko: 1:1000 / Počet formátů: 10xA4
	Číslo přílohy: **2**

DOKUMENT LZE UŽÍVAT POUZE VE SMYSLU PŘÍSLUŠNÉ SMLOUVY O DÍLO. ŽÁDNÁ JEHO ČÁST NEMŮŽE BÝT DLE ZÁKONA č.121/2000 Sb. KOPÍROVÁNA NEBO JINÝM ZPŮSOBEM ROZŠIŘOVÁNA BEZ SOUHLASU SUDOP PRAHA a.s.