
# SO 226 - NADJEZD NA PŘELOŽCE SILNICE III/30015 V KM 132,150

## POHLED 1-1 : SITUACE

M 1:500

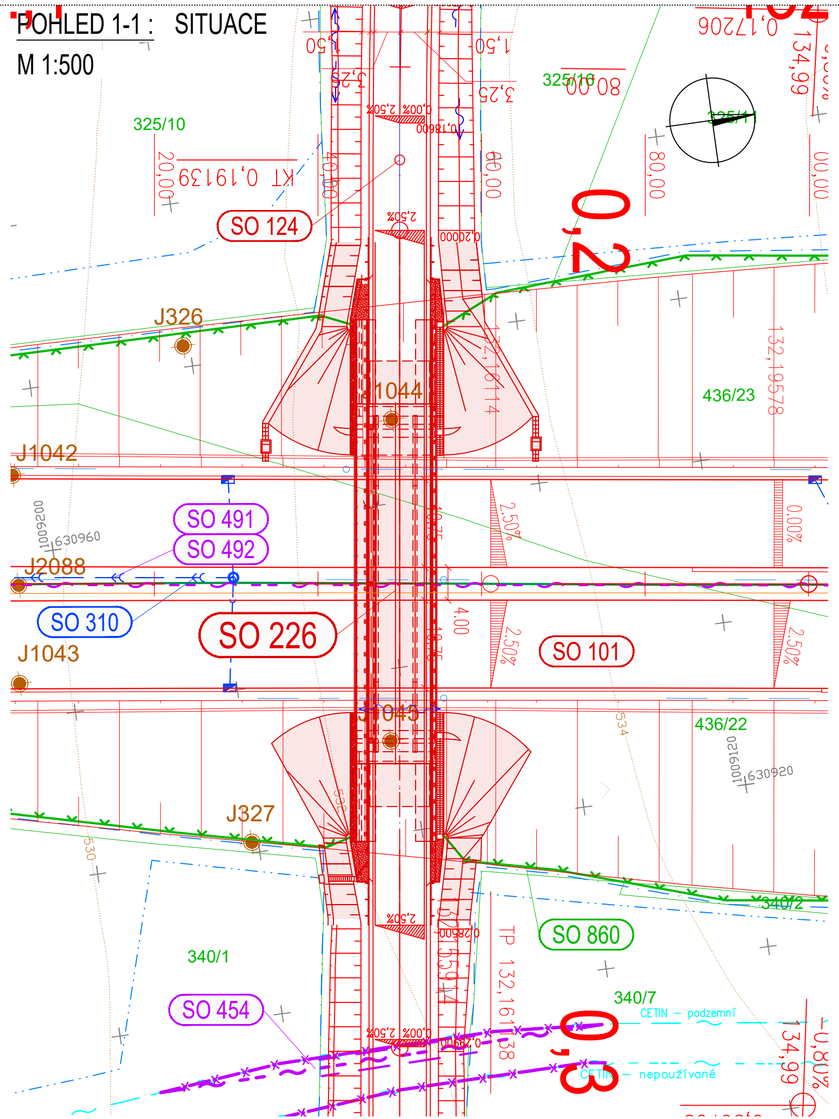


## SEZNAM SOUVISEJÍCÍCH STAVEBNÍCH OBJEKTŮ

| | |
|---|---|
| **ŘADA 000** | **OBJEKTY PŘÍPRAVY STAVENIŠTĚ** |
| SO 020 | Příprava území |
| **ŘADA 100** | **OBJEKTY POZEMNÍCH KOMUNIKACÍ** |
| SO 101 | Hlavní trasa D11 1108 |
| SO 124 | Přeložka III/30015 (km 132,22) |
| SO 180 | Dopravní opatření |
| SO 190.1 | Svislé a vodorovné dopravní značení ve správě ŘSD |
| SO 193 | Dopravní značení - Přeložky silnic II. a III. tř. |
| **ŘADA 300** | **VODOHOSPODÁŘSKÉ OBJEKTY** |
| SO 310 | Dešťová kanalizace dálnice km 128,550 - 132,130 |
| **ŘADA 400** | **ELEKTRO A SDĚLOVACÍ OBJEKTY** |
| SO 454 | Přeložka podzemního vedení CETIN a.s. v km 131,664 - 131,682 |
| SO 491 | Systém DIS-SOS - kabelové vedení |
| SO 494 | Systém DIS-SOS - trubky pro optické kabely |
| **ŘADA 800** | **OBJEKTY ÚPRAVY ÚZEMÍ** |
| SO 801 | Vegetační úpravy správce ŘSD |
| SO 806 | Vegetační úpravy sil. II. a III. tř. |
| SO 830 | Rekultivace |
| SO 860 | Oplocení dálnice |
| **ŘADA 900** | **DALŠÍ OBJEKTY** |
| SO 900 | Ochrana D11 1108 před vandalismem a zcizováním majetku státu |

LEGENDA ČAR:

- HRANICE PARCEL KN
- HRANICE KÚ
- VRSTEVNICE
- HRANICE TRVALÉHO ZÁBORU
- HRANICE DOČASNÉHO ZÁBORU

# SO 226
# D.1.2

VÝŠKOVÝ SYSTÉM Bpv — SOUŘADNICOVÝ SYSTÉM S-JTSK

| Číslo změny: | Obsah změny: | Datum změny: |
|---|---|---|
| 01 | - | - |
| 02 | - | - |
| 03 | - | - |

*Objednatel:*
ŘEDITELSTVÍ SILNIC A DÁLNIC
Ředitelství silnic a dálnic s. p.
Na Pankráci 546/56, 140 00 Praha 4

Stavbu zajišťuje Závod Praha
Na Pankráci 546/56, 140 00 Praha 4

*Zhotovitel: Společníci ve sdružení*
SG_Velké projekty_BIM 2020
zastoupené
SUDOP PRAHA a.s.
Hlavní inženýr projektu: Ing. Roman Petřík
Olšanská 1a, 130 80 Praha 3
telefon: +420 267 094 111

SUDOP PRAHA | PUDIS | SUDOP BRNO | DOPRAVOPROJEKT BRNO | DOPRAVOPROJEKT

*Správce:*
SUDOP PRAHA
SUDOP PRAHA a.s.
Olšanská 1a, 130 80 Praha 3
tel.: +420 267 094 111
e-mail: praha@sudop.cz

*Vedoucí týmu:* ING. ROMAN PETŘÍK

*Asistent vedoucího týmu:* ING. PAVEL MICHL

*Specialista profese:* ING. PAVEL JIŘÍČEK, PH.D.

*Zpracovatel části:*
PUDIS
projektová, průzkumná a konzultační společnost
PUDIS a.s., Podbabská 1014/20, 160 00 Praha 6
tel.: +420 267 004 111, www.pudis.cz, info@pudis.cz

| Vedoucí střediska: | Odpovědný projektant SO, IO, PS: | Vypracoval: | Kontroloval: |
|---|---|---|---|
| ING. MIROSLAV KROUPAR | ING. LUDVÍK KOLPASKÝ | TOMÁŠ POKORNÝ | ING. LUDVÍK KOLPASKÝ |

*Název akce:*
**D11 1108 Jaroměř - Trutnov VD-ZDS + TP + AD**

*Číslo smlouvy:* 22-014.250

*Projektový stupeň:* VD-ZDS

*Část:*
D.1.2 MOSTNÍ OBJEKTY A ZDI
**SO 226 NADJEZD NA PŘELOŽCE SILNICE III/30015 V KM 132,150**

*Datum:* 11/2024

*Číslo části:* D.1.2

*Název přílohy:*
**SITUACE**

*Měřítko:* 1:500

*Počet formátů:* 3xA4

*Číslo přílohy:* 02

DOKUMENT LZE UŽÍVAT POUZE VE SMYSLU PŘÍSLUŠNÉ SMLOUVY O DÍLO. ŽÁDNÁ JEHO ČÁST NEMŮŽE BÝT DLE ZÁKONA č.121/2000 Sb. KOPÍROVÁNA NEBO JINÝM ZPŮSOBEM ROZŠIŘOVÁNA BEZ SOUHLASU SUDOP PRAHA a.s.