


SO 226 NADJEZD NA PŘELOŽCE SILNICE III/30015 V KM 132,150

POHLED 1-1 : PŮDORYS
M 1:100

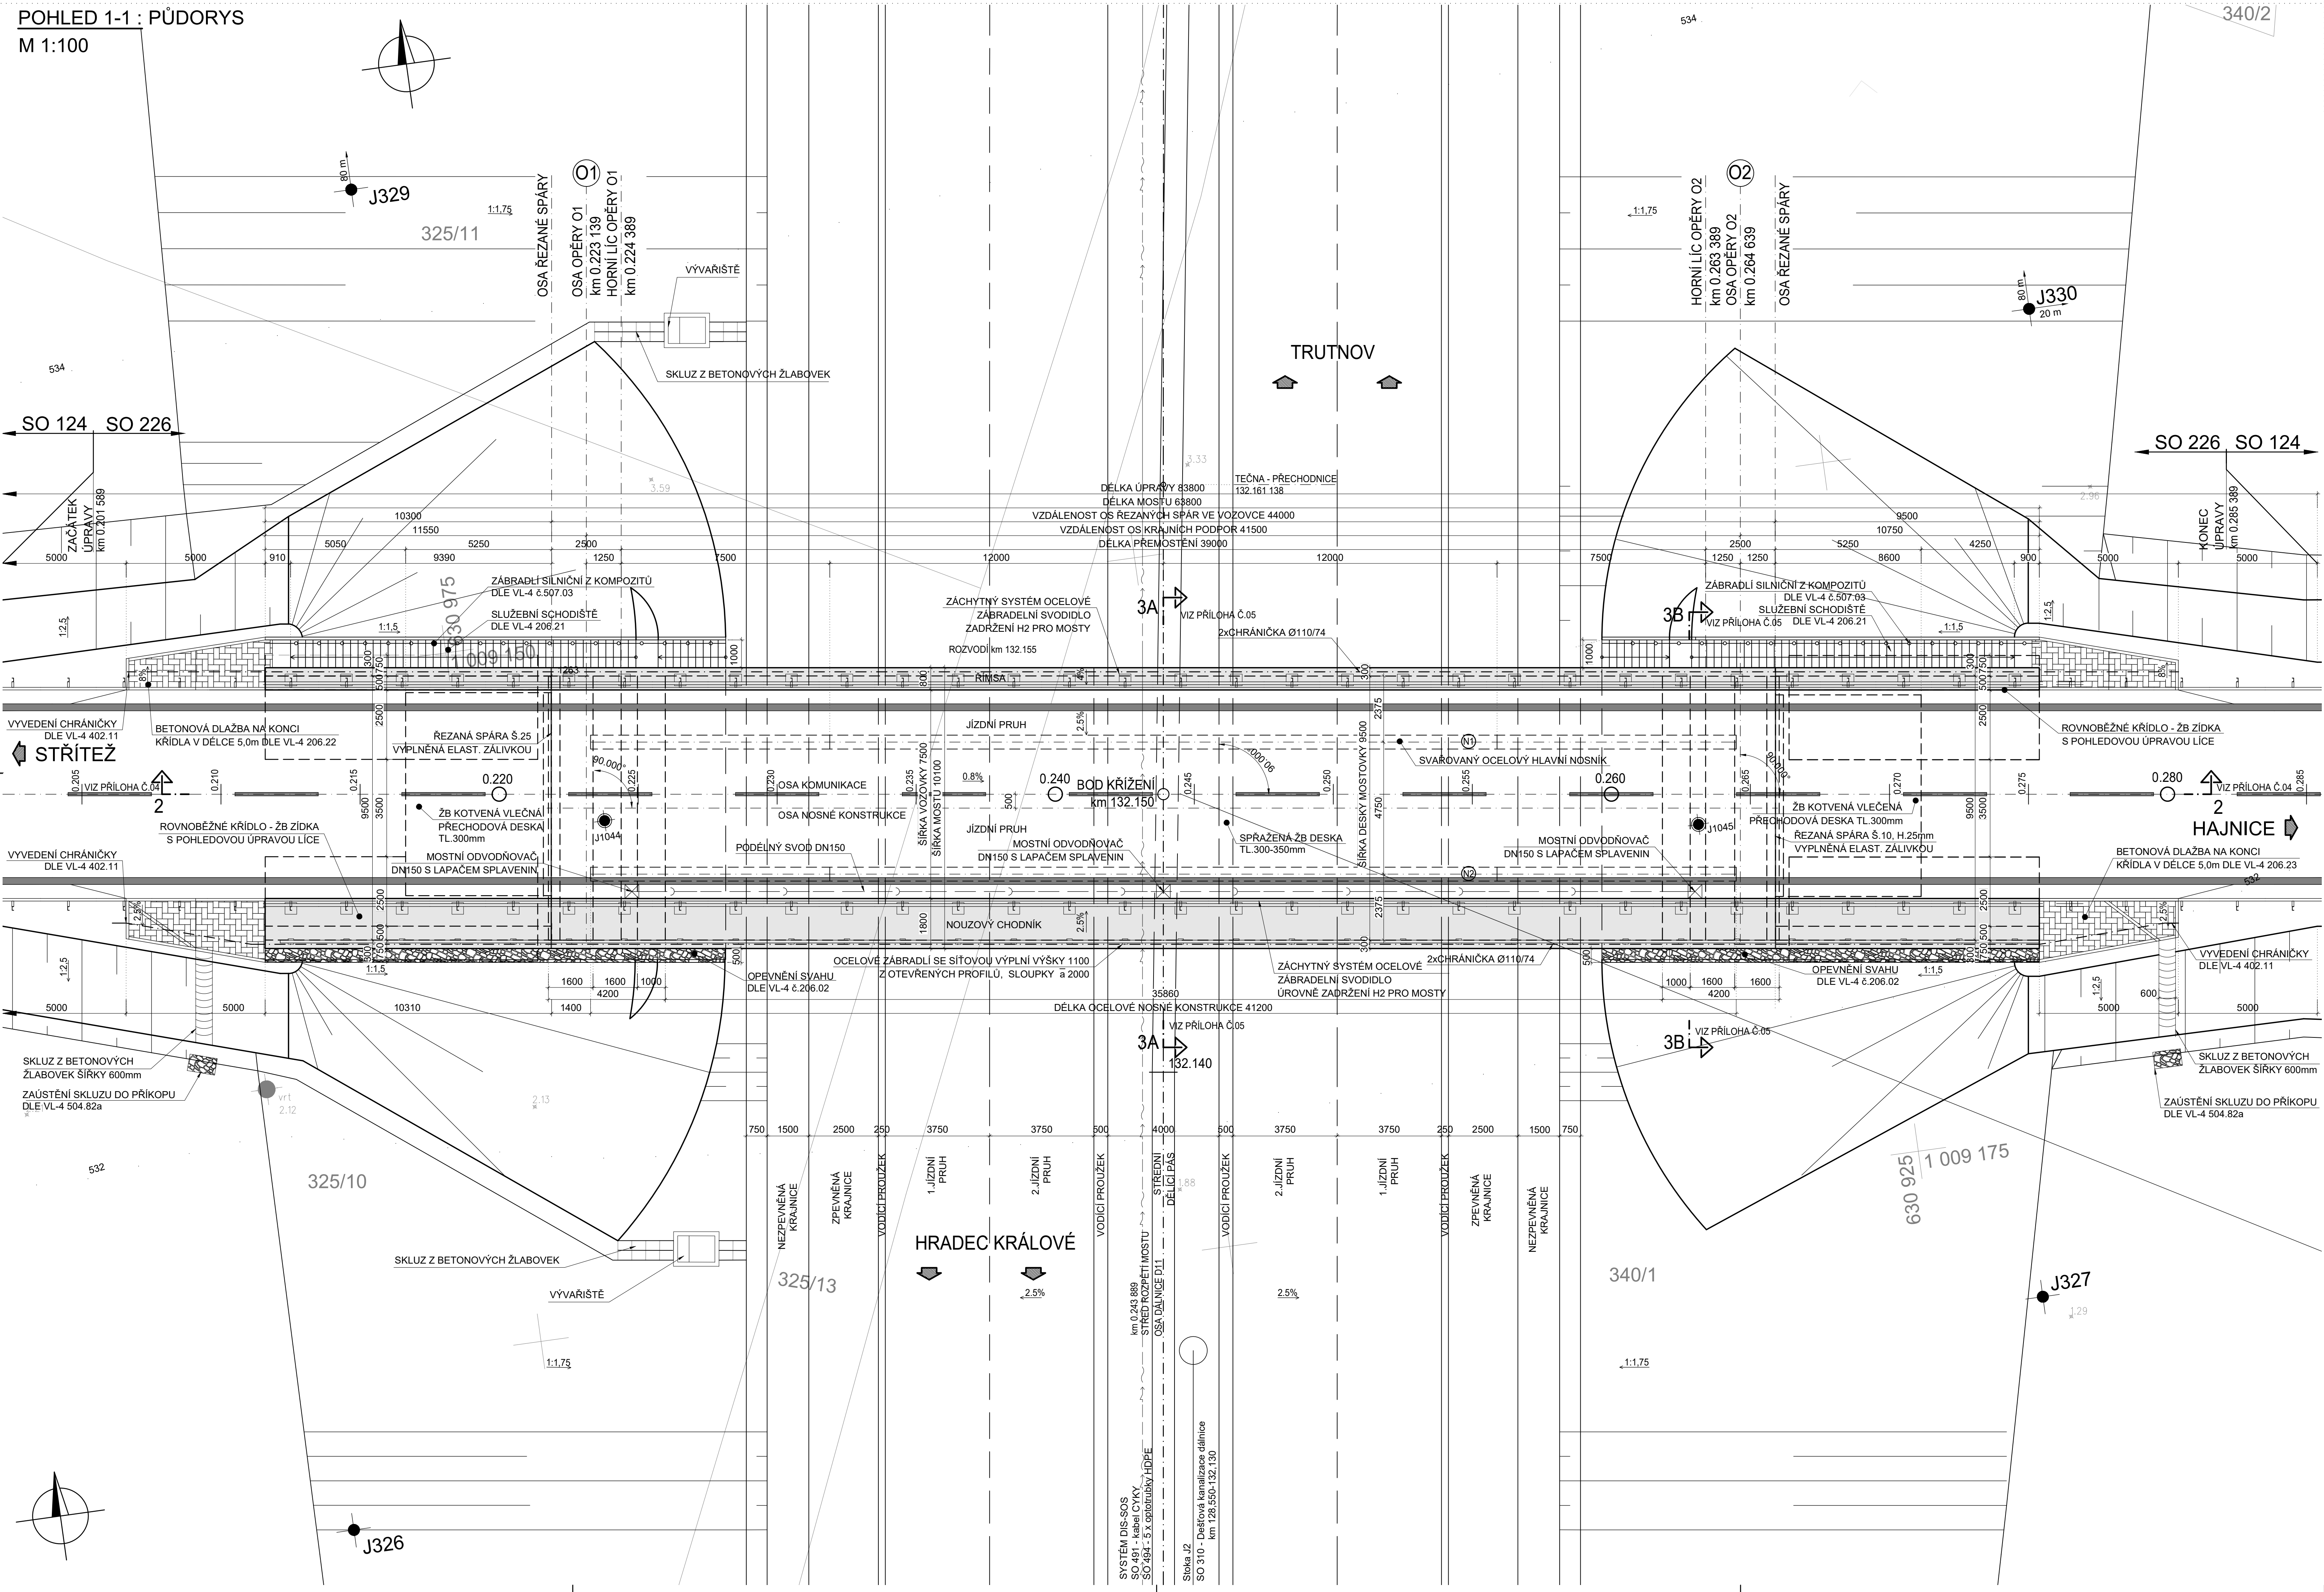

POZNÁMKY:
1. MATERIÁLY VIZ TECHNICKÁ ZPRÁVA

SO 226
D.1.2

VÝŠKOVÝ SYSTÉM Bvp SOUŘADNICOVÝ SYSTÉM S-JTSK

Číslo změny:	Obsah změny:	Datum změny:
01	-	-
02	-	-
03	-	-

Objednatel:	Roditelství silnic a dálnic s. p. Na Pankraci 546/56, 140 00 Praha 4 Stavbu zajišťuje Závod Praha Na Pankraci 546/56, 140 00 Praha 4
-------------	---

Zhotovitel: Společnosti ve sdružení	SG_Velké projekty BIM 2020 zastoupené
SUDOP PRAHA a.s. Hlavní inženýr projektu: Ing. Roman Petřík	Olšanská 1a, 130 80 Praha 3 telefon: +420 267 094 111

SUDOP PRAHA	PUDIS	SUDOP EU	OPRAVOPROJEKT BRNO	OPRAVOPROJEKT
-------------	-------	----------	--------------------	---------------

Správc:	SUDOP PRAHA a.s. Olšanská 1a, 130 80 Praha 3 tel.: +420 267 094 111 e-mail: praha@sudop.cz	Vedoucí týmu:	ING. ROMAN PETŘÍK	Asistent vedoucího týmu:	ING. PAVEL MICHL Specialista profese: ING. PAVEL JIŘÍČEK, Ph.D.
---------	---	---------------	-------------------	--------------------------	---

Zpracovatel část:	projektová, průzkumná a konzultační společnost PUDIS a.s., Podbabská 1014/20, 160 00 Praha 6 tel.: +420 267 004 111, www.pudis.cz, info@pudis.cz
-------------------	--

Vedoucí střediska:	Odpovědný projektant SO, IO, PS:	Vypracoval:	Kontroloval:
ING. MIROSLAV KROUPAR	ING. LUDVÍK KOLPÁSKÝ	TOMÁŠ POKORNÝ	ING. LUDVÍK KOLPÁSKÝ

Název akce:	Číslo smlouvy:
D11 1108 Jaroměř - Trutnov VD-ZDS + TP + AD	22-014.250

Část:	Projektový stupeň:
D.1.2 MOSTNÍ OBJEKTY A ZDI SO 226 NADJEZD NA PŘELOŽCE SILNICE III/30015 V KM 132,150	VD-ZDS

Datum:	Číslo části:
05/2024	D.1.2

Název přílohy:	Mřítko:	Podobí formátu:
PŮDORYS	1:100	10xA4

Číslo přílohy:	03
----------------	----