


# SO 226 NADJEZD NA PŘELOŽCE SILNICE III/30015 V KM 132,150

## VZOROVÝ PŘÍČNÝ ŘEZ NOSNOU KONSTRUKCÍ

ŘEZ 3A-3A : PŘÍČNÝ - STŘEDEM ROZPĚTÍ NADJEZDU  
M 1:50 KM 0.243 889

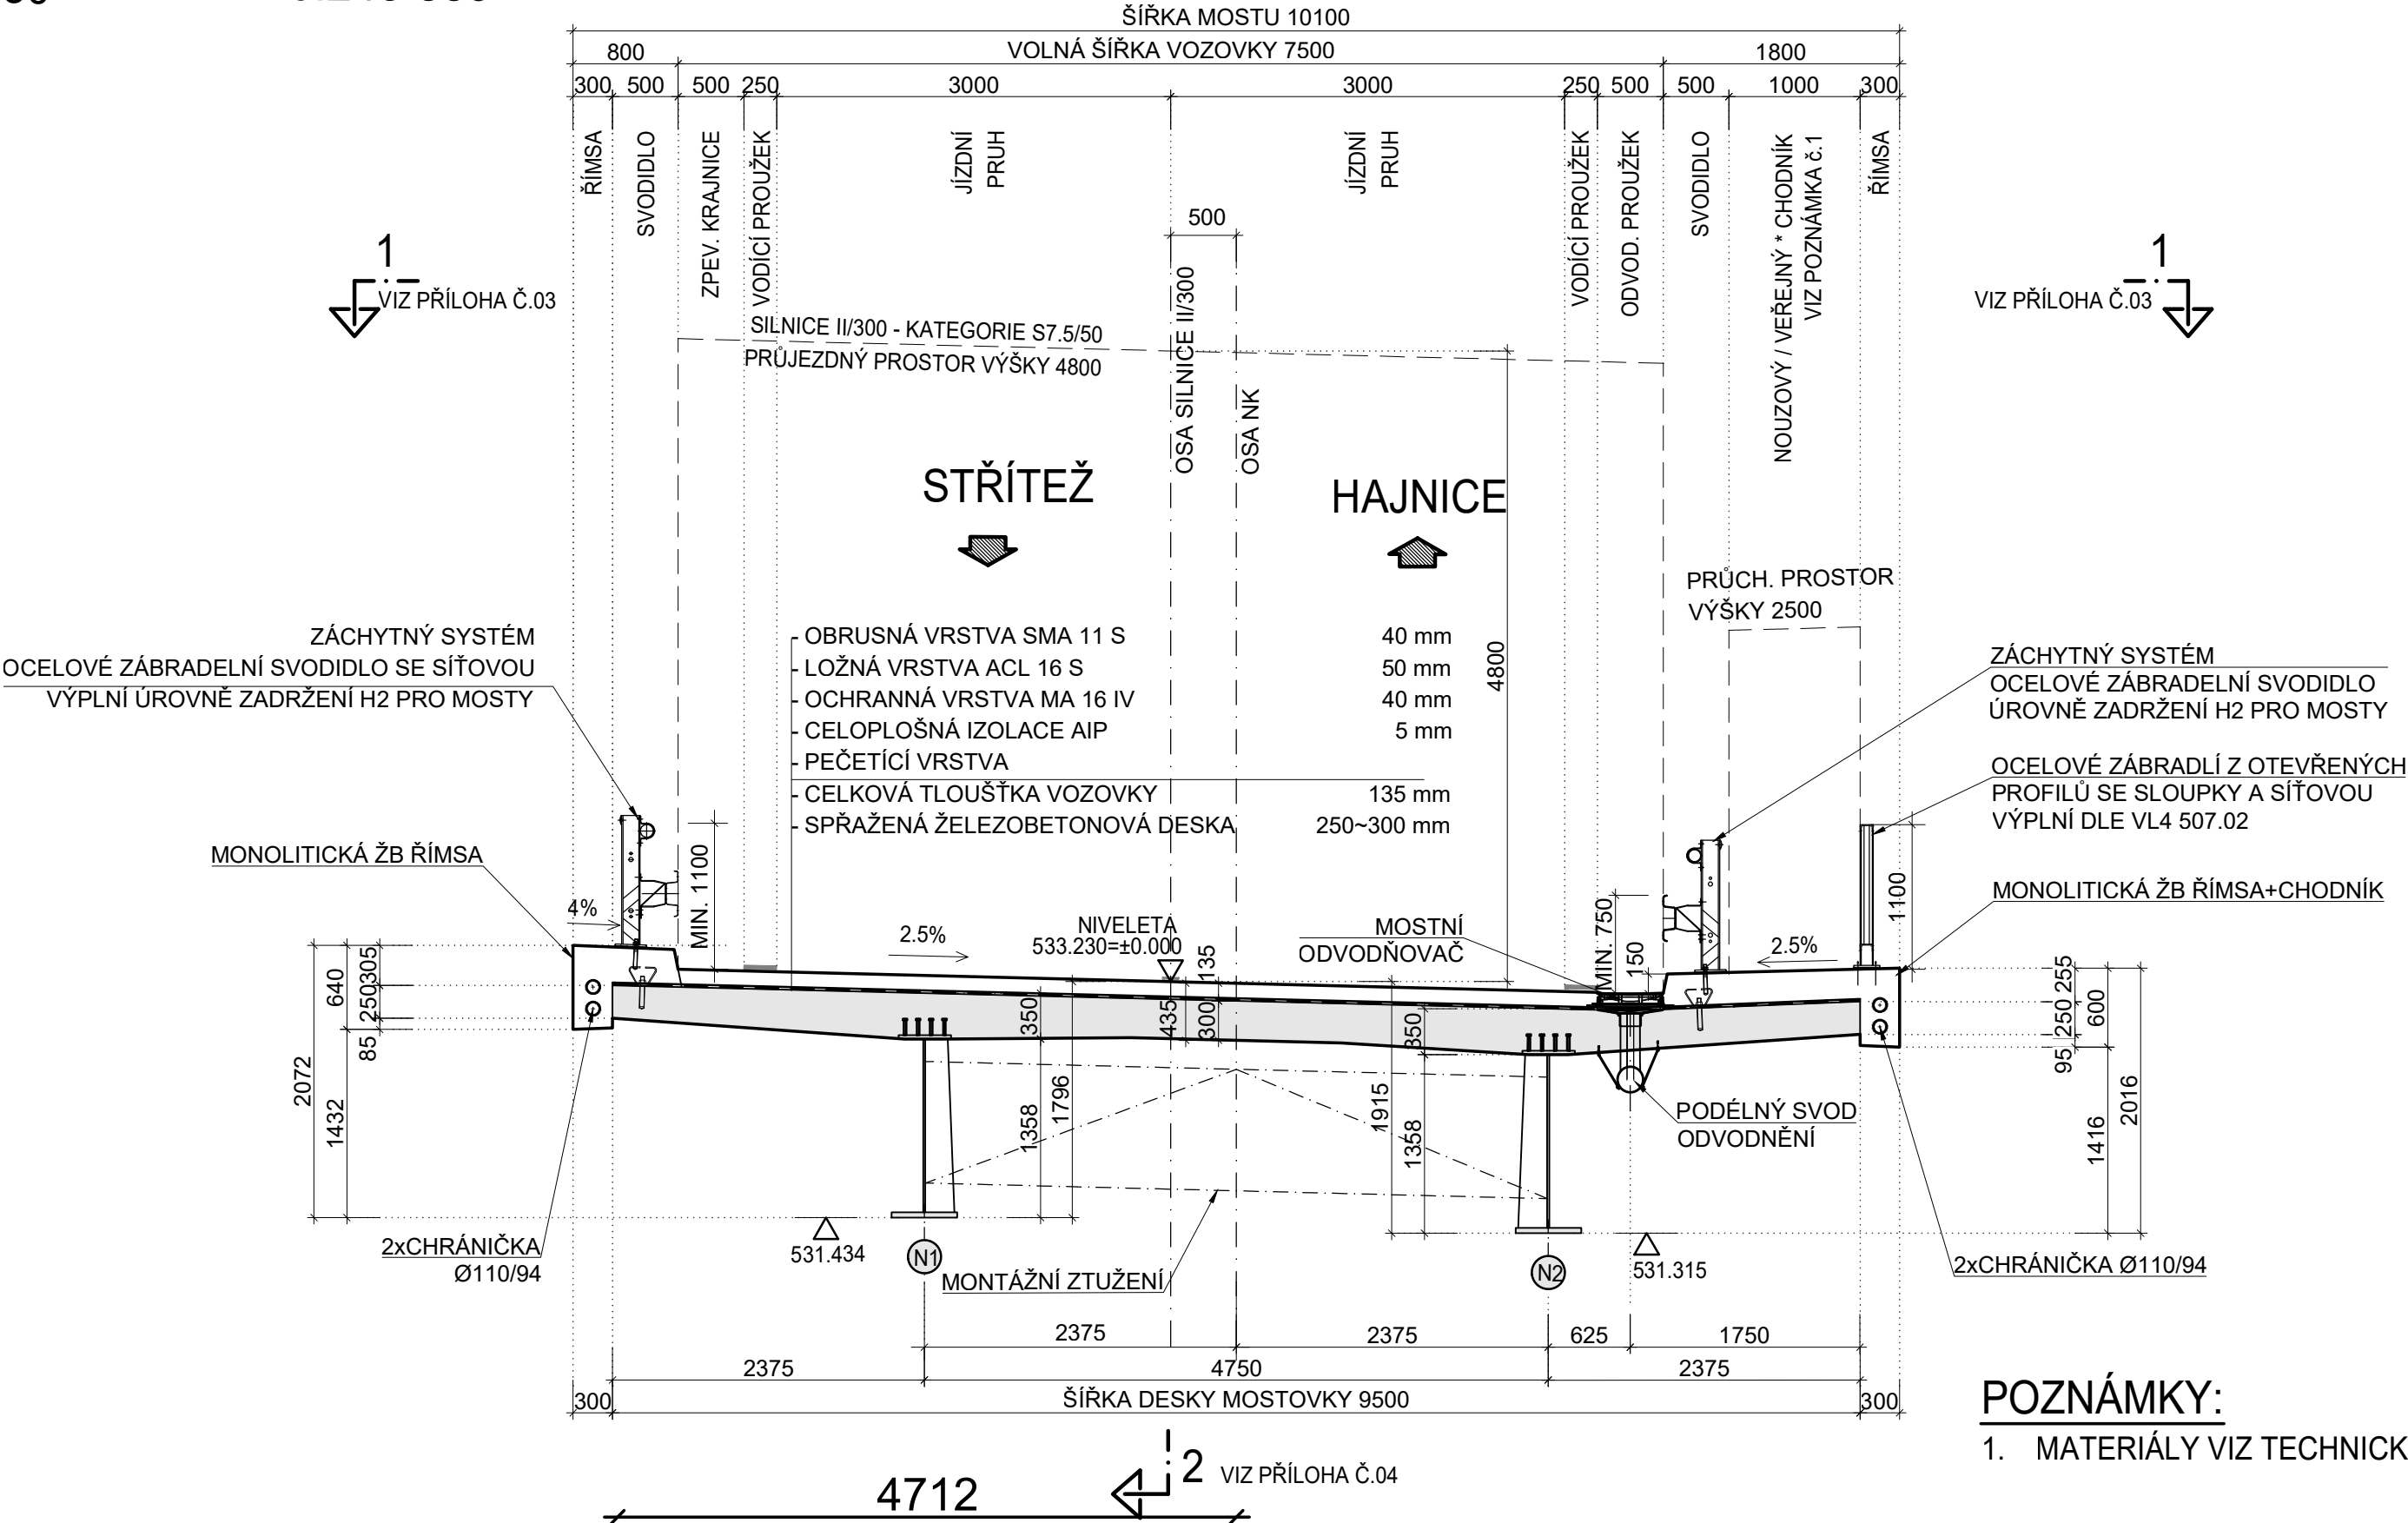

### SO 226

### D.1.2

VÝŠKOVÝ SYSTÉM Bpv SOUŘADNICOVÝ SYSTÉM S-JTSK

| Číslo změny: | Obsah změny: | Datum změny: |
|--------------|--------------|--------------|
| 01           | -            | -            |
| 02           | -            | -            |
| 03           | -            | -            |

|             |                                                                         |
|-------------|-------------------------------------------------------------------------|
| Objednatel: | Ředitelství silnic a dálnic s. p.<br>Na Pankráci 546/56, 140 00 Praha 4 |
|             | Stavbu zajišťuje Závod Praha<br>Na Pankráci 546/56, 140 00 Praha 4      |

|                                                                |                                                          |
|----------------------------------------------------------------|----------------------------------------------------------|
| Zhotovitel: Společníci ve sdružení                             | SG_Velké projekty_BIM 2020<br>zastoupené                 |
| SUDOP PRAHA a.s.<br>Hlavní inženýr projektu: Ing. Roman Petřík | Olšanská 1a, 130 80 Praha 3<br>telefon: +420 267 094 111 |

|  |  |  |  |  |
|--|--|--|--|--|
|  |  |  |  |  |
|--|--|--|--|--|

|          |   |                   |                           |
|----------|---|-------------------|---------------------------|
| Správce: | SUDOP PRAHA a.s.<br>Olšanská 1a, 130 80 Praha 3<br>tel.: +420 267 094 111<br>e-mail: praha@sudop.cz | Vedoucí týmu:     | Asistent vedoucího týmu:  |
|          |   | ING. ROMAN PETŘÍK | ING. PAVEL MICHL          |
|          |   |                   | Specialista profese:      |
|          |   |                   | ING. PAVEL JIŘÍČEK, PH.D. |

|                    |   |
|--------------------|---|
| Zpracovatel částí: | projektová, průzkumná a konzultační společnost                                                       |
|                    | PUDIS a.s., Podbabská 1014/20, 160 00 Praha 6<br>tel.: +420 267 004 111, www.pudis.cz, info@pudis.cz |

|                       |                                  |               |                      |
|-----------------------|----------------------------------|---------------|----------------------|
| Vedoucí střediska:    | Odpovědný projektant SO, IO, PS: | Vypracoval:   | Kontroloval:         |
| ING. MIROSLAV KROUPAR | ING. LUDVÍK KOLPASKÝ             | TOMÁŠ POKORNÝ | ING. LUDVÍK KOLPASKÝ |

|                                                           |                    |
|-----------------------------------------------------------|--------------------|
| Název akce:                                               | Číslo smlouvy:     |
| D11 1108 Jaroměř - Trutnov VD-ZDS + TP + AD               | 22-014.250         |
| Část:                                                     | Projektový stupeň: |
| D.1.2 MOSTNÍ OBJEKTY A ZDI                                | VD-ZDS             |
| SO 226 NADJEZD NA PŘELOŽCE SILNICE III/30015 V KM 132,150 | Datum:             |
|                                                           | 05/2024            |
| Název přílohy:                                            | Číslo části:       |
| VZOROVÝ PŘÍČNÝ ŘEZ NOSNOU KONSTRUKCÍ                      | D.1.2              |
|                                                           | Měřítko:           |
|                                                           | 1:50               |
|                                                           | Počet formátů:     |
|                                                           | 3xA4               |
|                                                           | Číslo přílohy:     |
|                                                           | 05                 |

DOKUMENT LZE UŽÍVAT POUZE VE SMYSLU PŘÍSLUŠNÉ SMLOUVY O DÍLO. ŽÁDNÁ JEHO ČÁST NEMŮŽE BYT DLE ZÁKONA č.121/2000 Sb. KOPÍROVÁNA NEBO JINÝM ZPŮSOBEM ROZŠÍŘOVÁNA BEZ SOUHLASU SUDOP PRAHA a.s.