


SO 226 NADJEZD NA PŘELOŽCE SILNICE III/30015 V KM 132,150

SCHÉMA TECHNOLOGIE VÝSTAVBY

FÁZE 1: PODÉLNÝ ŘEZ

M 1:250

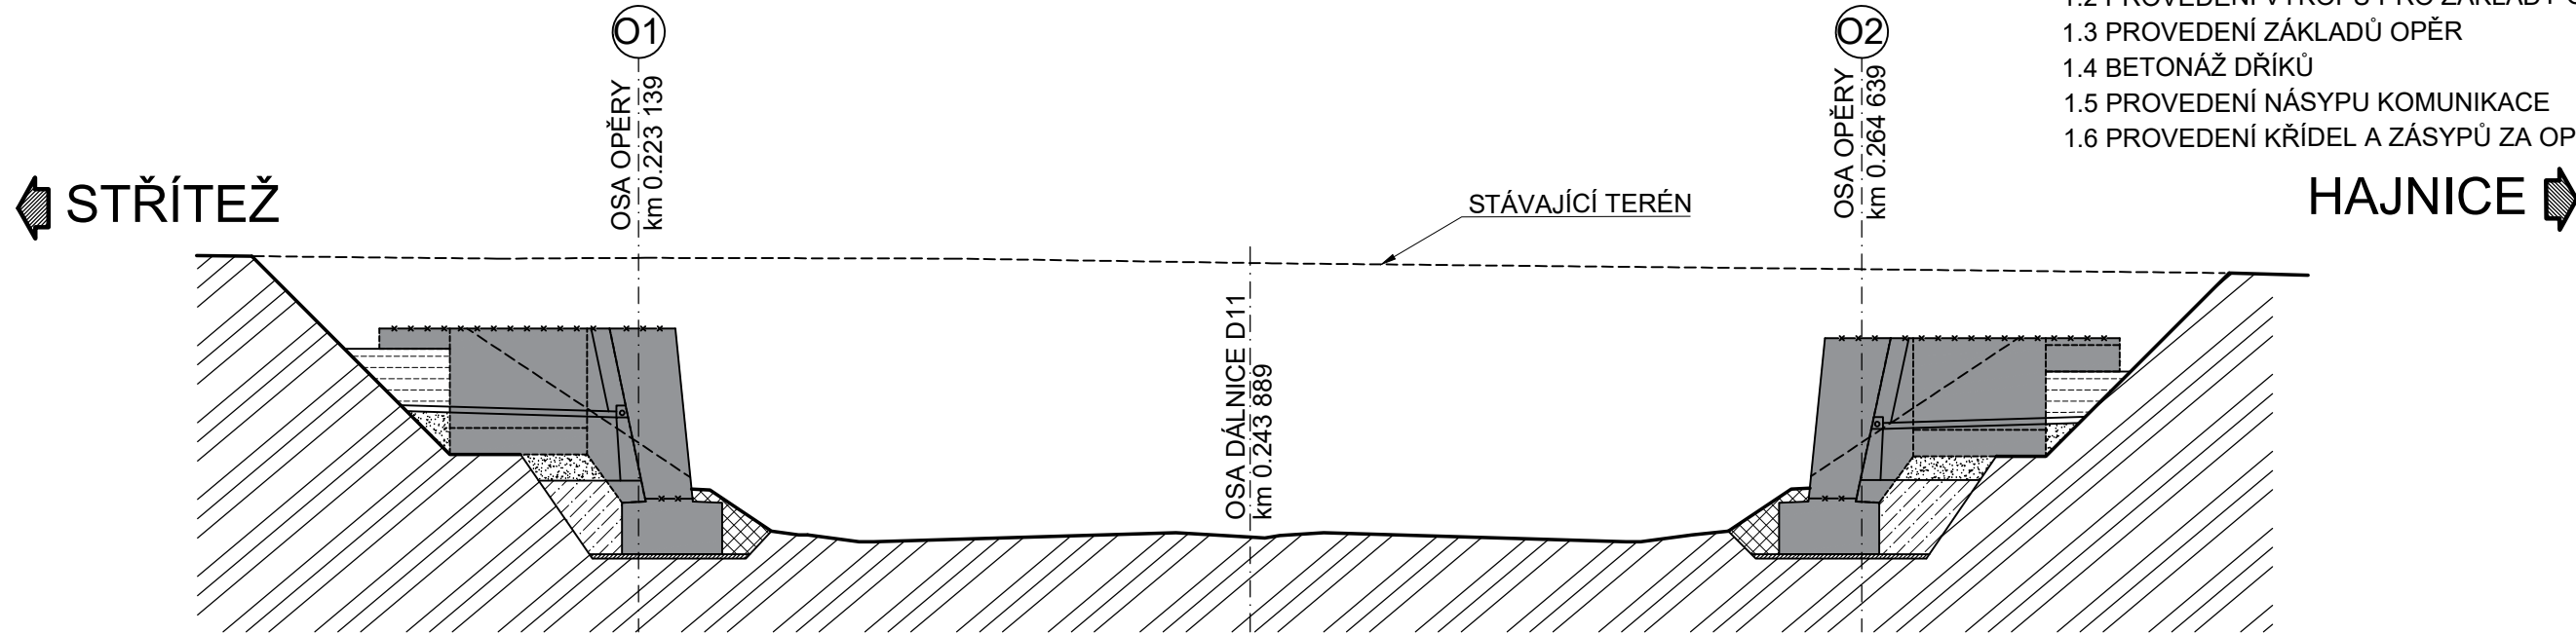


POPIS FÁZE

- 1.1 PROVEDENÍ VÝKOPŮ PRO TĚLESO DÁLNIČE
- 1.2 PROVEDENÍ VÝKOPŮ PRO ZÁKLADY OPĚR
- 1.3 PROVEDENÍ ZÁKLADŮ OPĚR
- 1.4 BETONÁŽ DŘÍKŮ
- 1.5 PROVEDENÍ NÁSYPŮ KOMUNIKACE
- 1.6 PROVEDENÍ KŘÍDEL A ZÁSYPŮ ZA OPĚRAMI

FÁZE 3:


STŘÍTEŽ

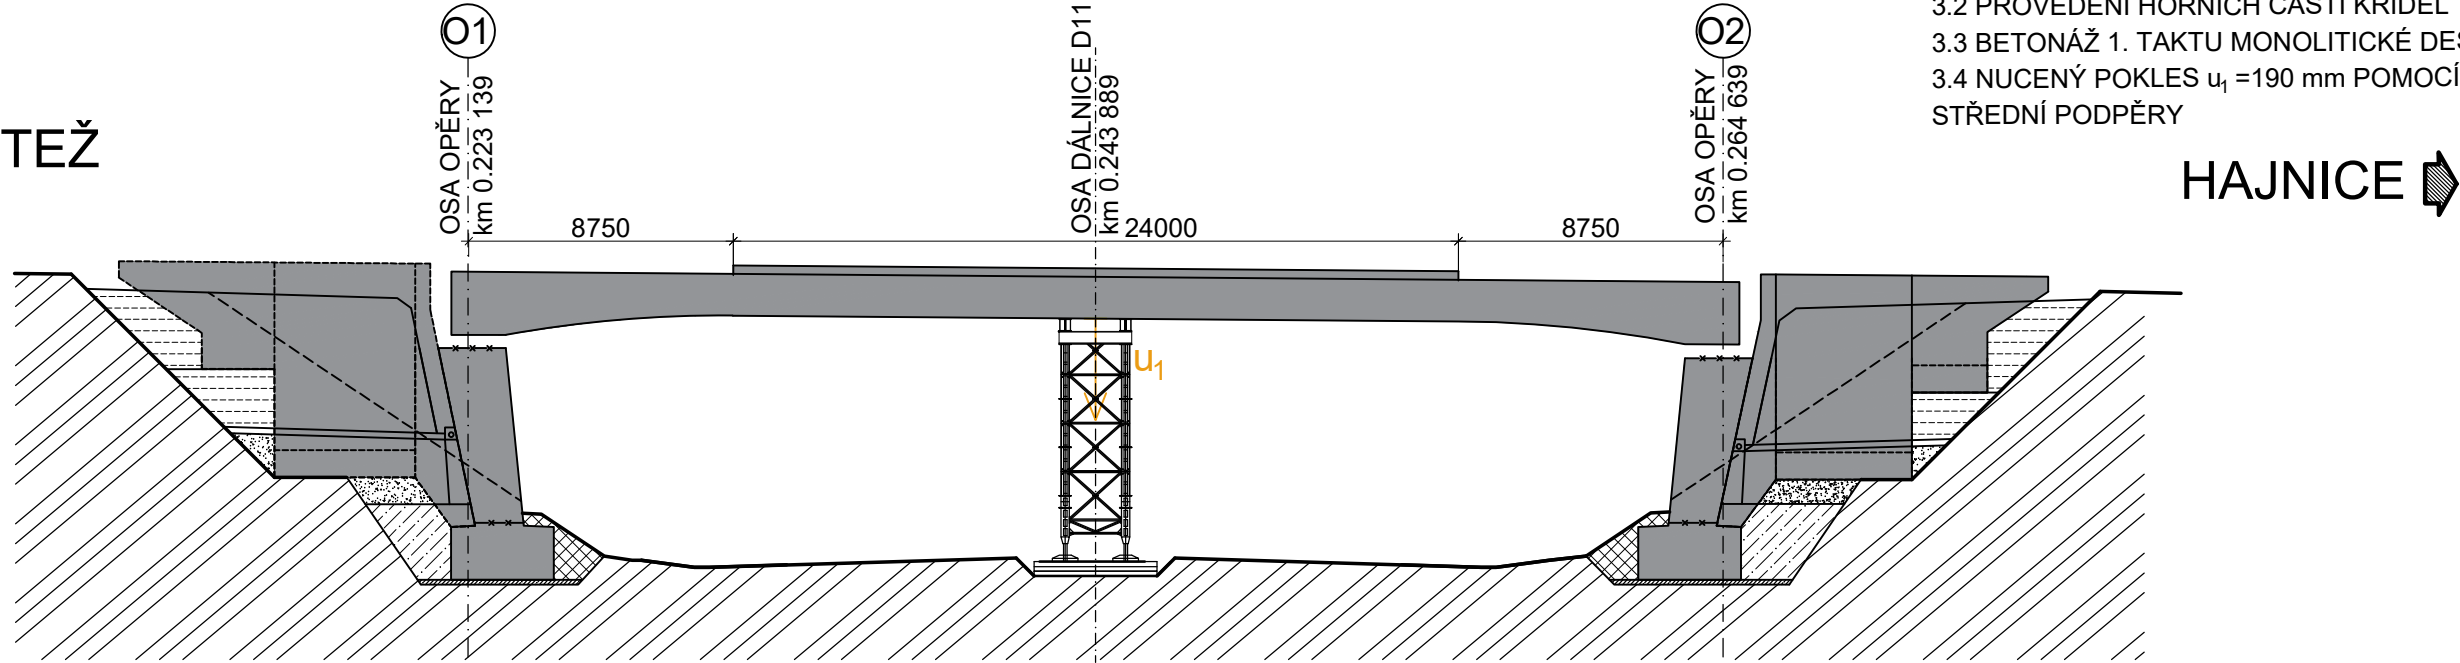

POPIS FÁZE

- 3.1 BETONÁŽ DESKY A RÁMOVÉHO ROHU
- 3.2 PROVEDENÍ HORNÍCH ČASTÍ KŘÍDEL
- 3.3 BETONÁŽ 1. TAKTU MONOLITICKÉ DESKY VE STŘEDU ROZPĚTÍ
- 3.4 NUCENÝ POKLES $u_1 = 190$ mm POMOCÍ REKTIFIKACE MONTÁŽNÍ STŘEDNÍ PODPĚRY

FÁZE 2:

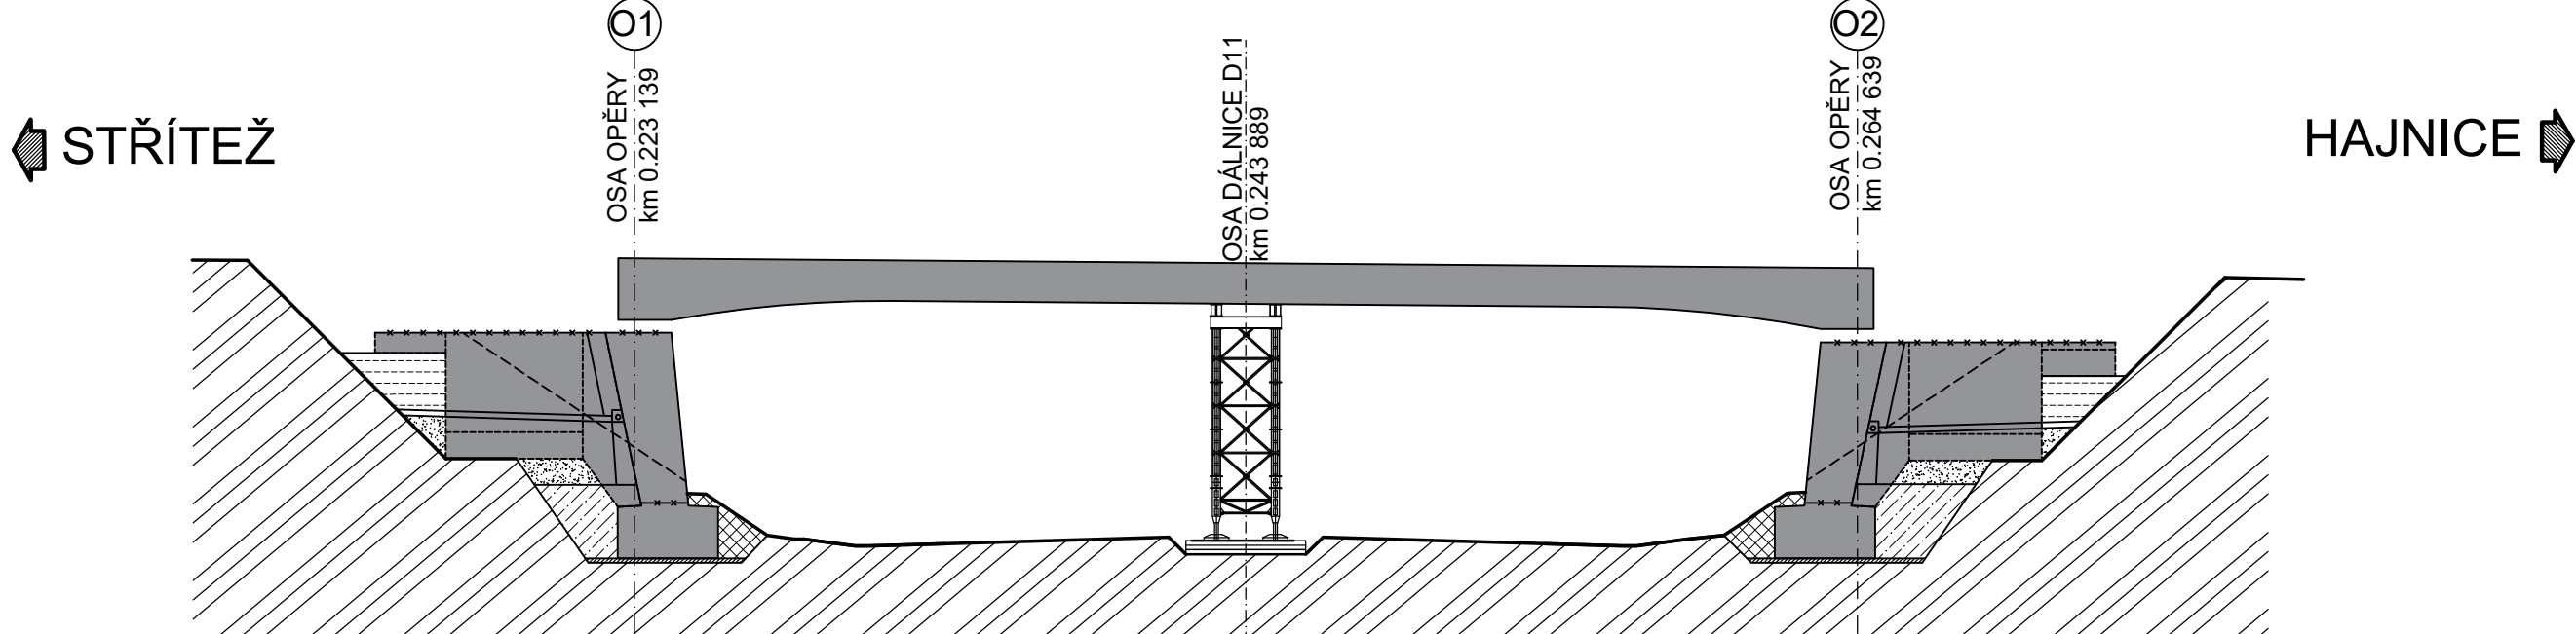


POPIS FÁZE

- 2.1 ZŘÍZENÍ PROVIZORNÍ PODPORY
- 2.2 MONTÁŽ OCELOVÝCH NOSNÍKŮ POMOCÍ JEŘÁBU NA OPĚRY

FÁZE 4:

STŘÍTEŽ

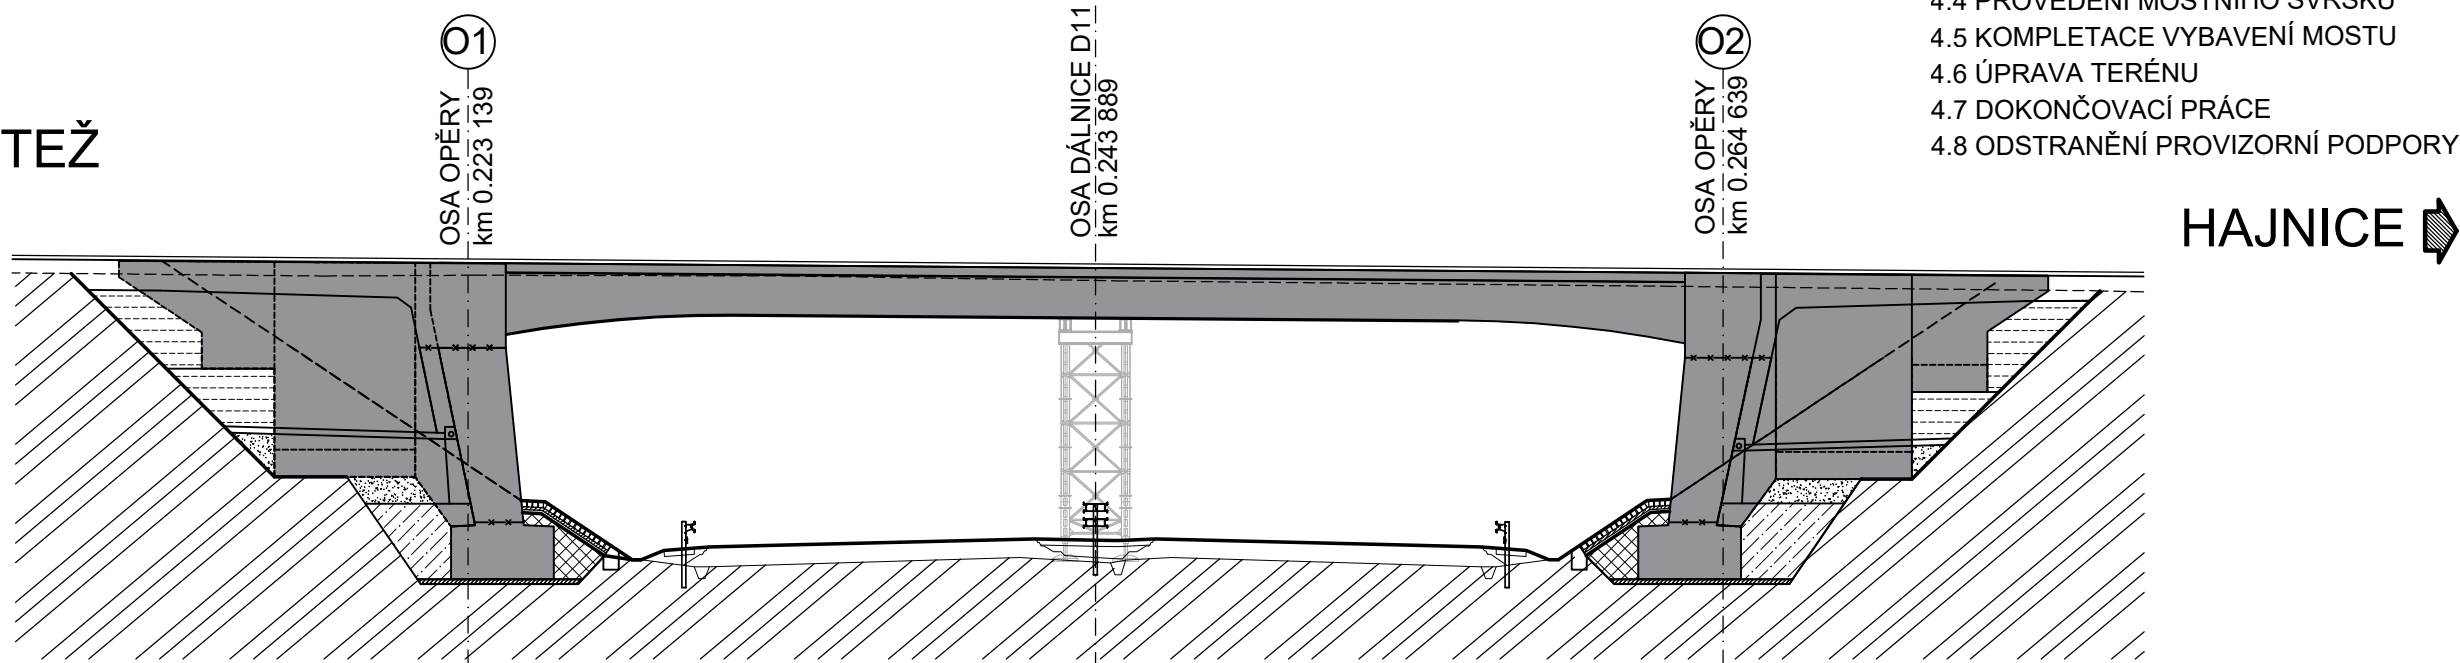

POPIS FÁZE

- 4.1 DOBETONOVÁNÍ 2. TAKTU DESKY
- 4.2 PROVEDENÍ ZÁSYPŮ ZA OPĚRAMI
- 4.3 BETONÁŽ ŘÍMS
- 4.4 PROVEDENÍ MOSTNÍHO SVRŠKU
- 4.5 KOMPLETACE VYBAVENÍ MOSTU
- 4.6 ÚPRAVA TERÉNU
- 4.7 DOKONČOVACÍ PRÁCE
- 4.8 ODSTRANĚNÍ PROVIZORNÍ PODPORY

SO 226
D.1.2

VÝŠKOVÝ SYSTÉM Bpv SOUŘADNICOVÝ SYSTÉM S-JTSK

Číslo změny:	Obsah změny:	Datum změny:
01	-	-
02	-	-
03	-	-

Objednatel:	Ředitelství silnic a dálnic s. p. Na Pankráci 546/56, 140 00 Praha 4
	Stavbu zajišťuje Závod Praha Na Pankráci 546/56, 140 00 Praha 4

Zhotovitel: Společníci ve sdružení	SG_Velké projekty_BIM 2020 zastoupené
SUDOP PRAHA a.s. Hlavní inženýr projektu: Ing. Roman Petřík	Olišanská 1a, 130 80 Praha 3 telefon: +420 267 094 111

--	--	--	--	--

Správce:	SUDOP PRAHA a.s. Olišanská 1a, 130 80 Praha 3 tel.: +420 267 094 111 e-mail: praha@sudop.cz	Vedoucí týmu:	ING. ROMAN PETŘÍK	Asistent vedoucího týmu:	ING. PAVEL MICHL Specialista profese: ING. PAVEL JIŘÍČEK, PH.D.
----------	--	---------------	-------------------	--------------------------	---

Zpracovatel částí:	projektová, průzkumná a konzultační společnost PUDIS a.s., Podbabská 1014/20, 160 00 Praha 6 tel.: +420 267 004 111, www.pudis.cz, info@pudis.cz
--------------------	--

Vedoucí střediska:	Odpovědný projektant SO, IO, PS:	Vypracoval:	Kontroloval:
ING. MIROSLAV KROUPAR	ING. LUDVÍK KOLPASKÝ	TOMÁŠ POKORNÝ	ING. LUDVÍK KOLPASKÝ

Název akce:		Číslo smlouvy:	
D11 1108 Jaroměř - Trutnov VD-ZDS + TP + AD		22-014.250	
		Projektový stupeň:	
		VD-ZDS	
Část:		Datum:	
D.1.2 MOSTNÍ OBJEKTY A ZDI		05/2024	
SO 226 NADJEZD NA PŘELOŽCE SILNICE III/30015 V KM 132,150		Číslo částí:	
		D.1.2	
Název přílohy:		Měřítko:	Počet formátů:
		1:100,1:50	4xA4
SCHÉMA TECHNOLOGIE VÝSTAVBY		Číslo přílohy:	
		07	

OKUMENT LZE UŽÍVAT POUZE VE SMYSLU PRÍSLUŠNÉ SMLOUVY O DÍLO. ŽÁDNÁ JEHO ČÁST NEMŮŽE BYT DLE ZÁKONA č. 121/2000 Sb. KOPÍROVÁNA NEBO JINÝM ZPŮSOBEM ROZŠÍŘOVÁNA. BEZ SOUHLASU SUDOP PRAHA a.s.