
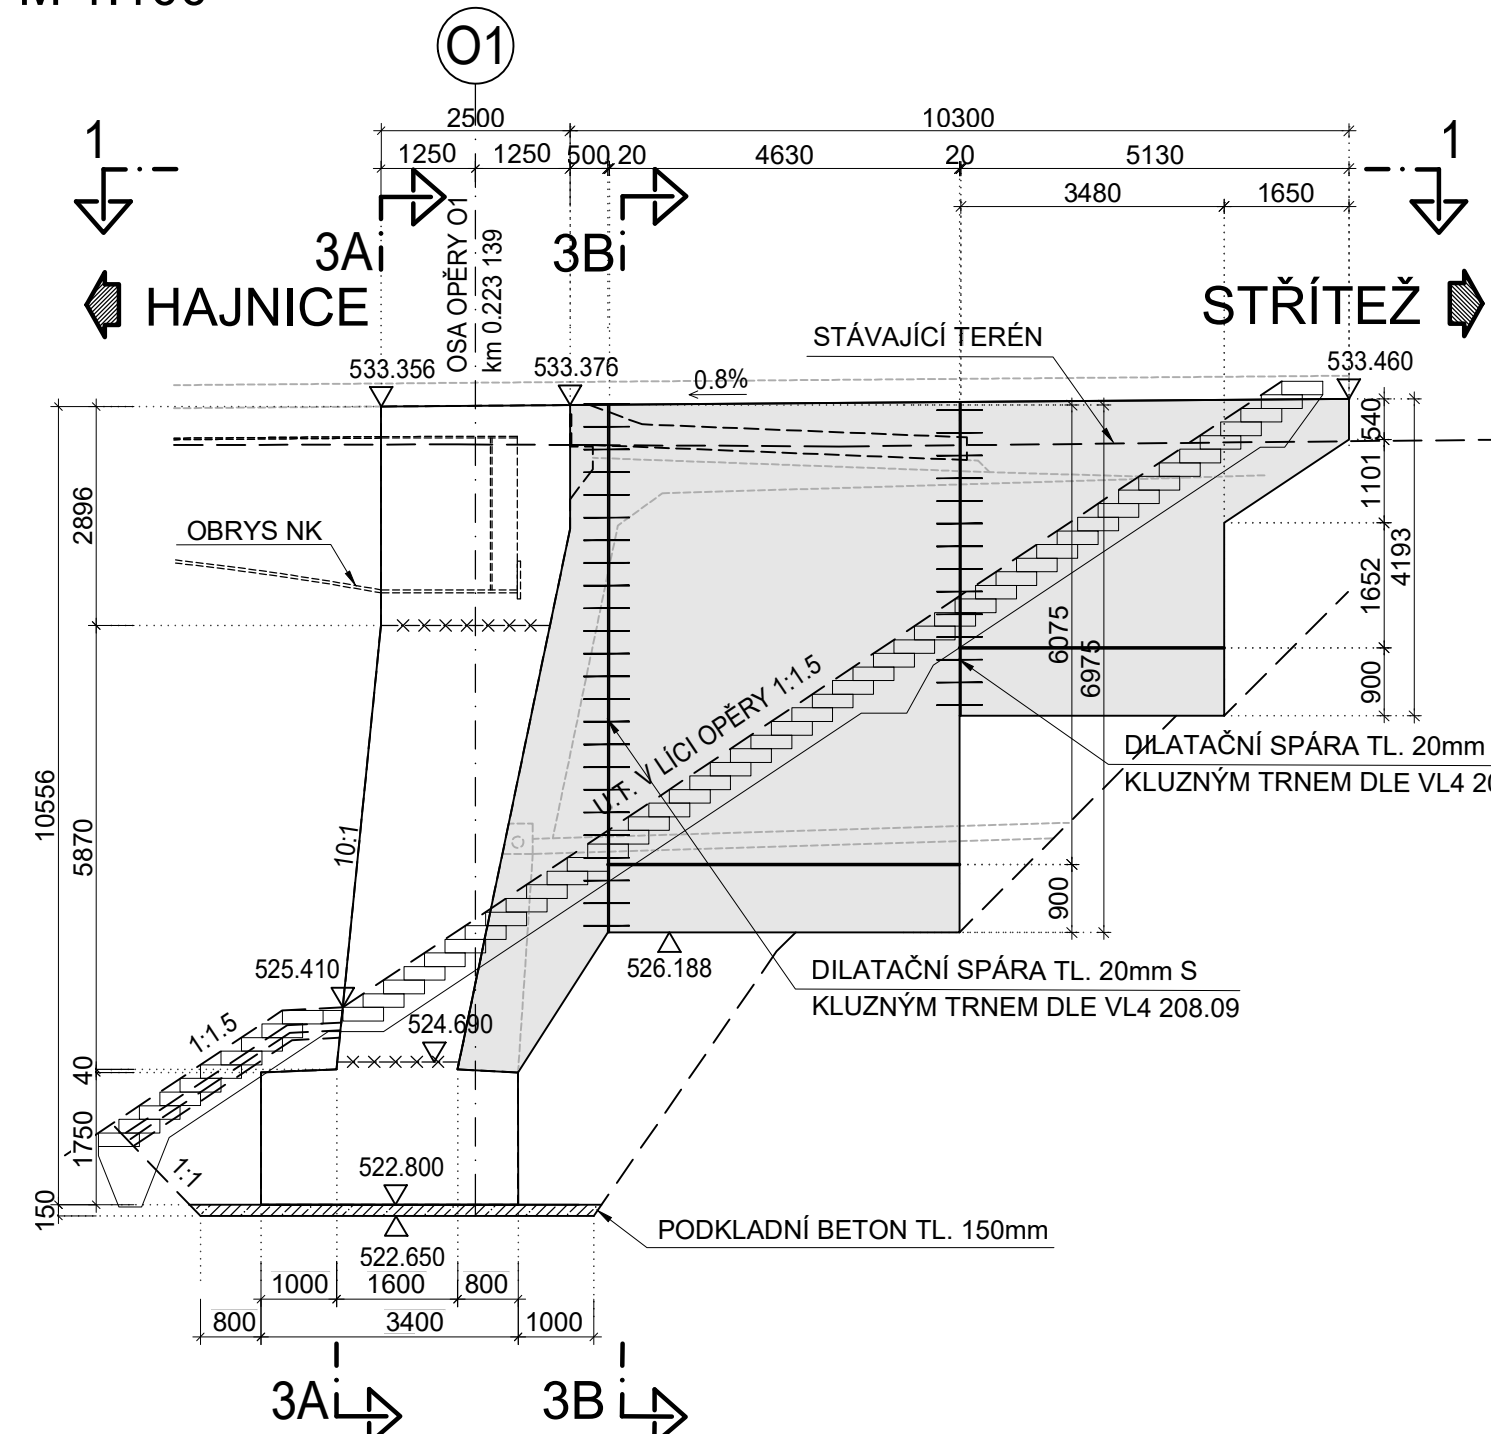


TVARTVAR OPĚ

ŘEZ 2A-2A : POHLED NA KŘÍDLO
M 1:100

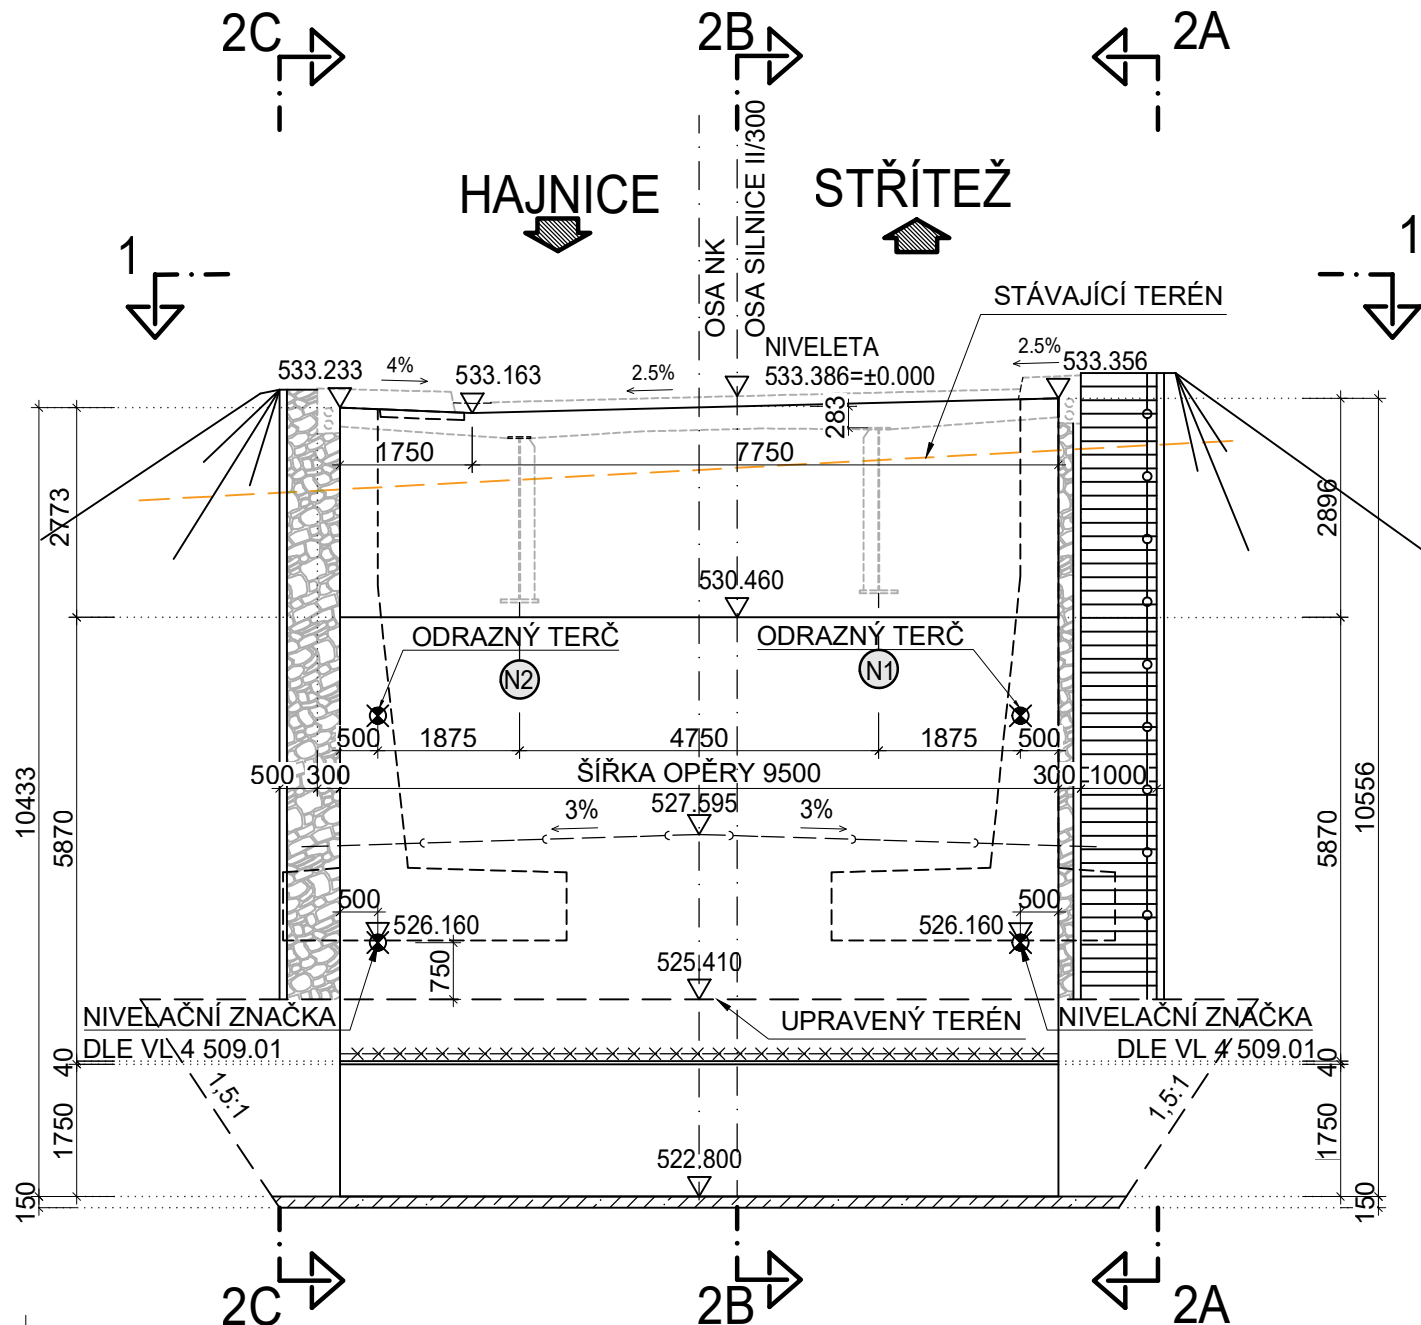

ŘEZ 3A-3A: PŘÍČNÝ - V LÍCI OPĚRY O1
M 1:100

[illegible]

1. MATERIÁLY VIZ TECHNICKÁ ZPRÁVA

D.1.2

SOUŘADNICOV

Objednatel:  ŘEDITELSTVÍ
SILNIC
A DÁLNIC

			
---	---	---	---

Zpracovatel částí:

 **PUDIS**

projektová, průzkumná a konzultační společnost

PUDIS a.s., Podbabská 1014/20, 160 00 Praha 6
tel.: +420 267 004 111, www.pudis.cz, info@pudis.cz

Název akce:	Číslo:
D11 1108 Jaroměř - Trutnov VD-ZDS + TP + AD	Projekt:
Část: D.1.2 MOSTNÍ OBJEKTY A ZDI SO 226 NADJEZD NA PŘELOŽCE SILNICE III/30015 V KM 132,150	Datum:
	Číslo:
Název přílohy:	Měřítko:
TVAR OPĚRY O1	Číslo:

DOKUMENT LZE UŽÍVAT POUZE VE SMYSLU PŘÍSLUŠNÉ SMLOUVY O DÍLO. ŽÁDNÁ JEHO ČÁST NEMŮŽE BÝT DLE ZÁKONA č. 121/2000 Sb. KOPIROVÁNA NEBO JINÝM ZPŮSOBEM ROZŠÍŘOVÁNA.