



TVAR OPĚ

ŘEZ 2B-2B : PODÉLNÝ - OSOU SILNICE III/30015
M 1:100

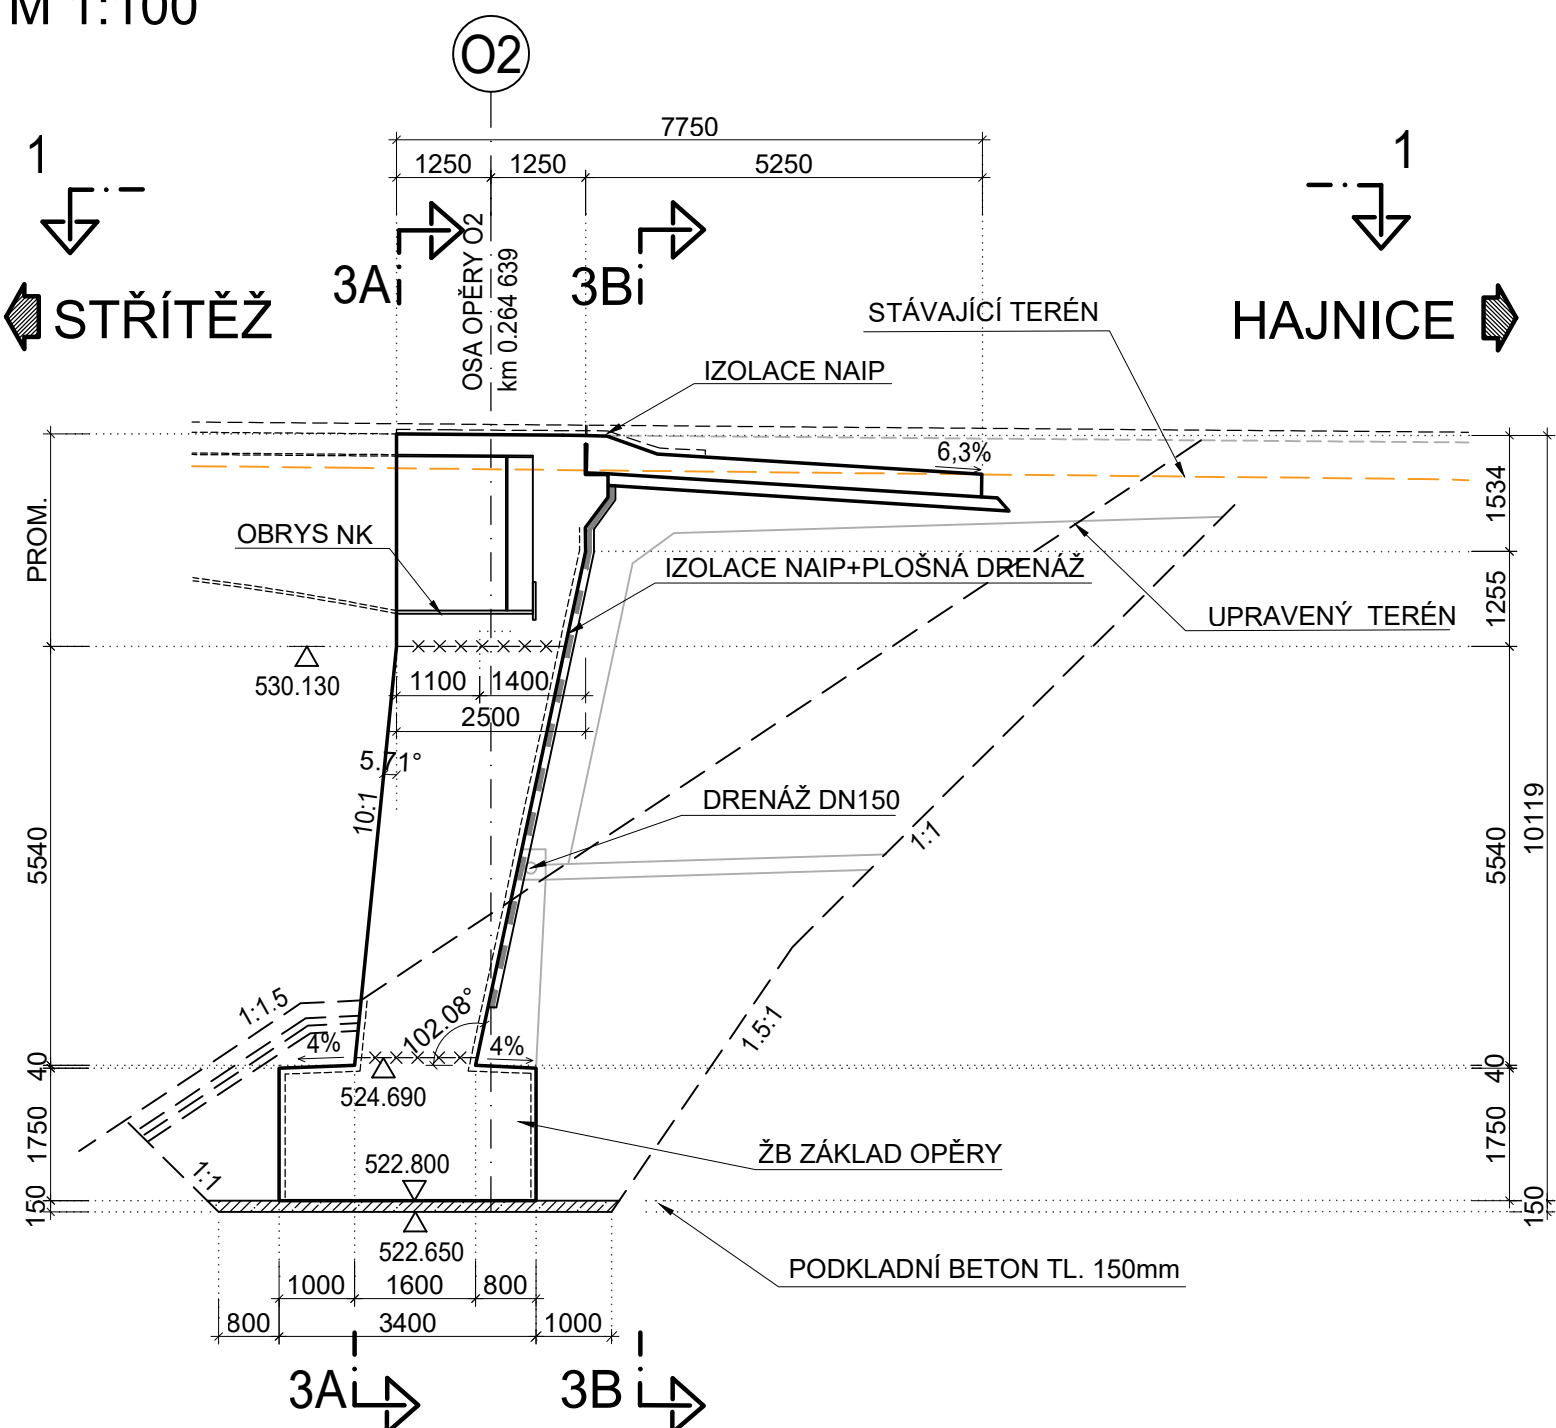

ŘEZ 2C-2C : POHLED NA KŘÍDLO
M 1:100

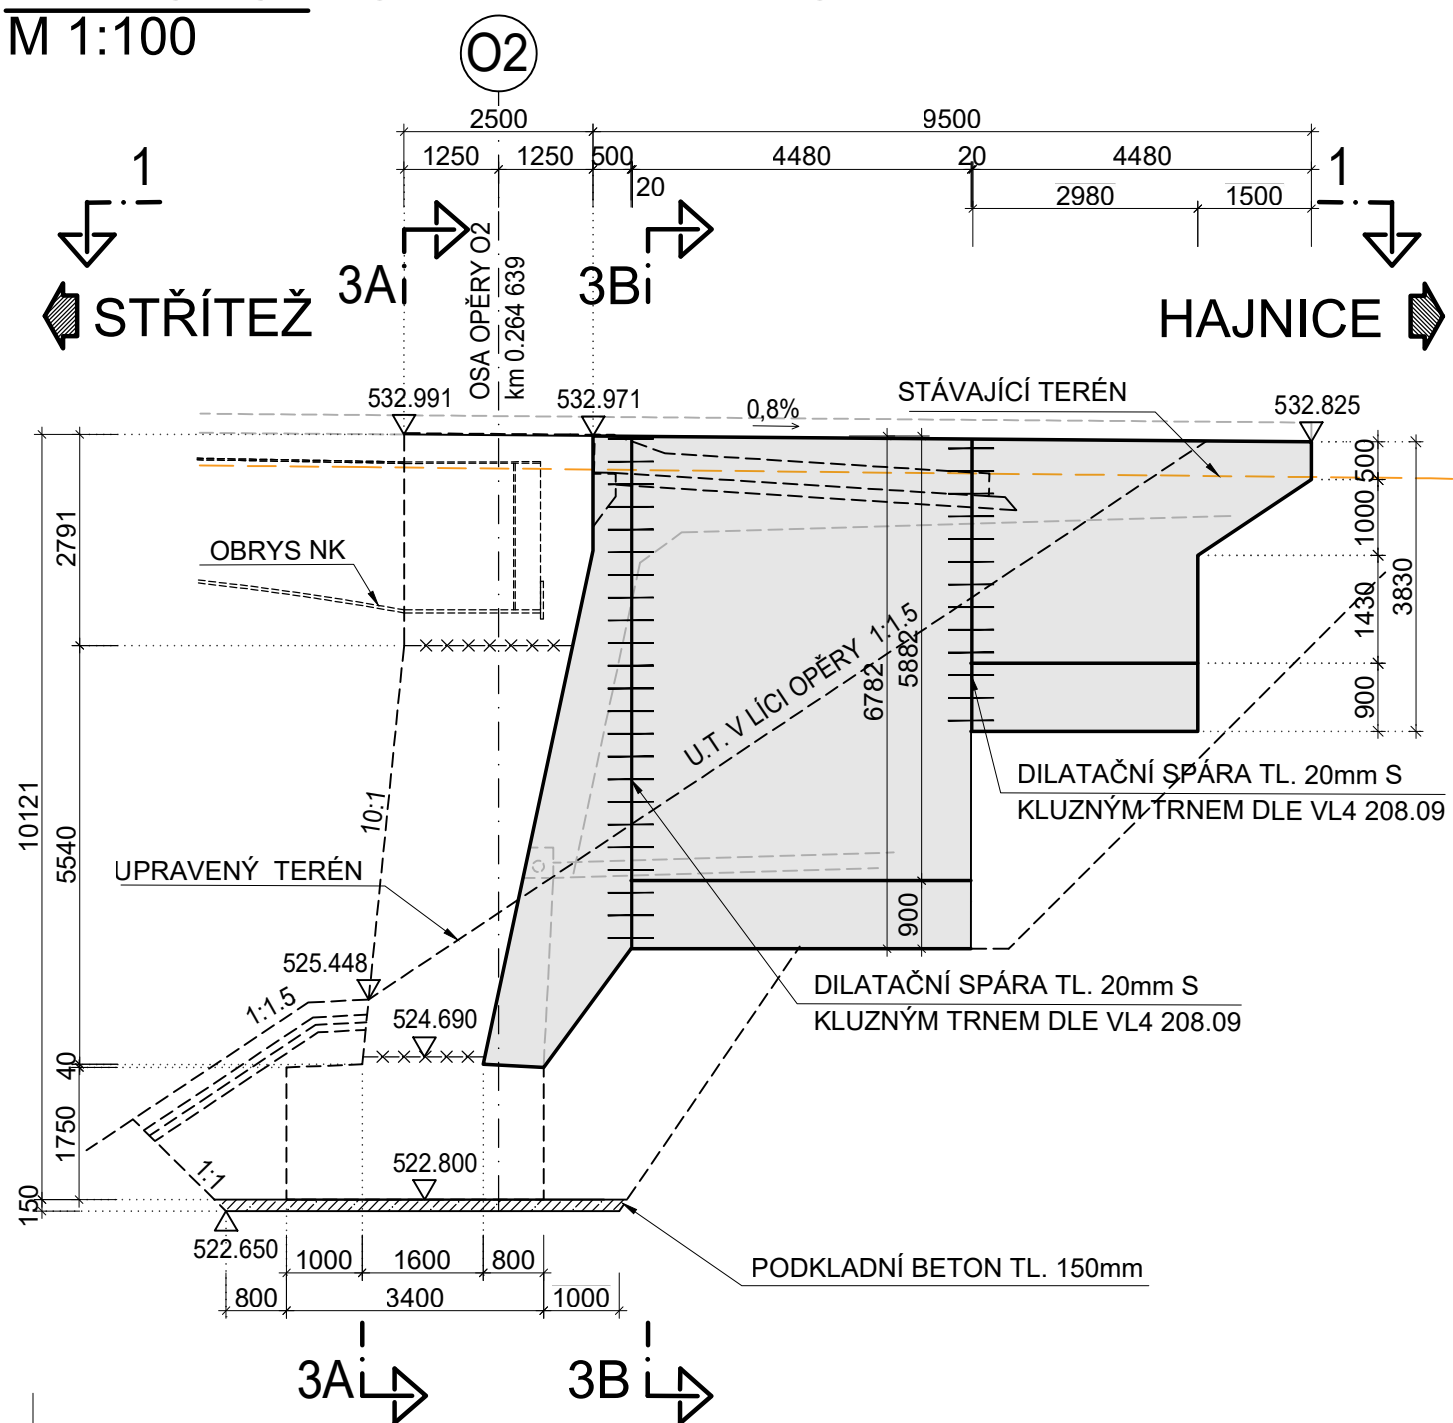

1. MATERIÁLY VIZ TECHNICKÁ ZPRÁVA
2. NAPOJENÍ SAMOSTATNÉHO KŘÍDLA A OPĚRY INTEGROVANÉHO MOSTU
VARIANTA: SPÁRA S KLUZNÝM TRNEM
3. NAPOJENÍ SAMOSTATNÝCH KŘÍDEL DLE VL4 208.09 VARIANTA: SPÁRA

VÝŠKOVÝ SYSTÉM Bpv SOUŘADNICOVÝ

Objednatel:  ŘEDITELSTVÍ SILNIC A DÁLNIC		Na Pank S Na Pank
---	--	--

Správce:  SUDOP PRAHA a.s. Olšanská 1a, 130 80 Praha 3 tel.: +420 267 094 111 e-mail: praha@sudop.cz	Vedoucí týmu: ING. ROMAN PETŘÍK	Asistent: ING. ... Specialista ... ING. ...
---	--	--

Vedoucí střediska:	Odpovědný projektant SO, IO, PS:	Vypracoval:	Kontrola:
ING. MIROSLAV KROUPAR	ING. LUDVÍK KOLPASKÝ	TOMÁŠ POKORNÝ	ING. ...

Název akce:	Číslo:
D11 1108 Jaroměř - Trutnov VD-ZDS + TP + AD	Projekt:
Část: D.1.2 MOSTNÍ OBJEKTY A ZDI SO 226 NADJEZD NA PŘELOŽCE SILNICE III/30015 V KM 132,150	Datum:
	Číslo:
Název přílohy:	Měřítko:
TVAR OPĚRY O2	1:1
	Číslo:

DOKUMENT LZE UŽÍVAT POUZE VE SMYSLU PŘÍSLUŠNÉ SMLOUVY O DÍLO. ŽÁDNÁ JEHO ČÁST NEMŮŽE BÝT DLE ZÁKONA č. 121/2000 Sb. KOPÍROVÁNA NEBO JINÝM ZPŮSOBEM ROZŠÍŘOVÁNA.