

SO 226 NADJEZD NA PŘELOŽCE SILNICE III/30015 V KM 132,150

SCHÉMA VÝZTUŽE: OPĚRA

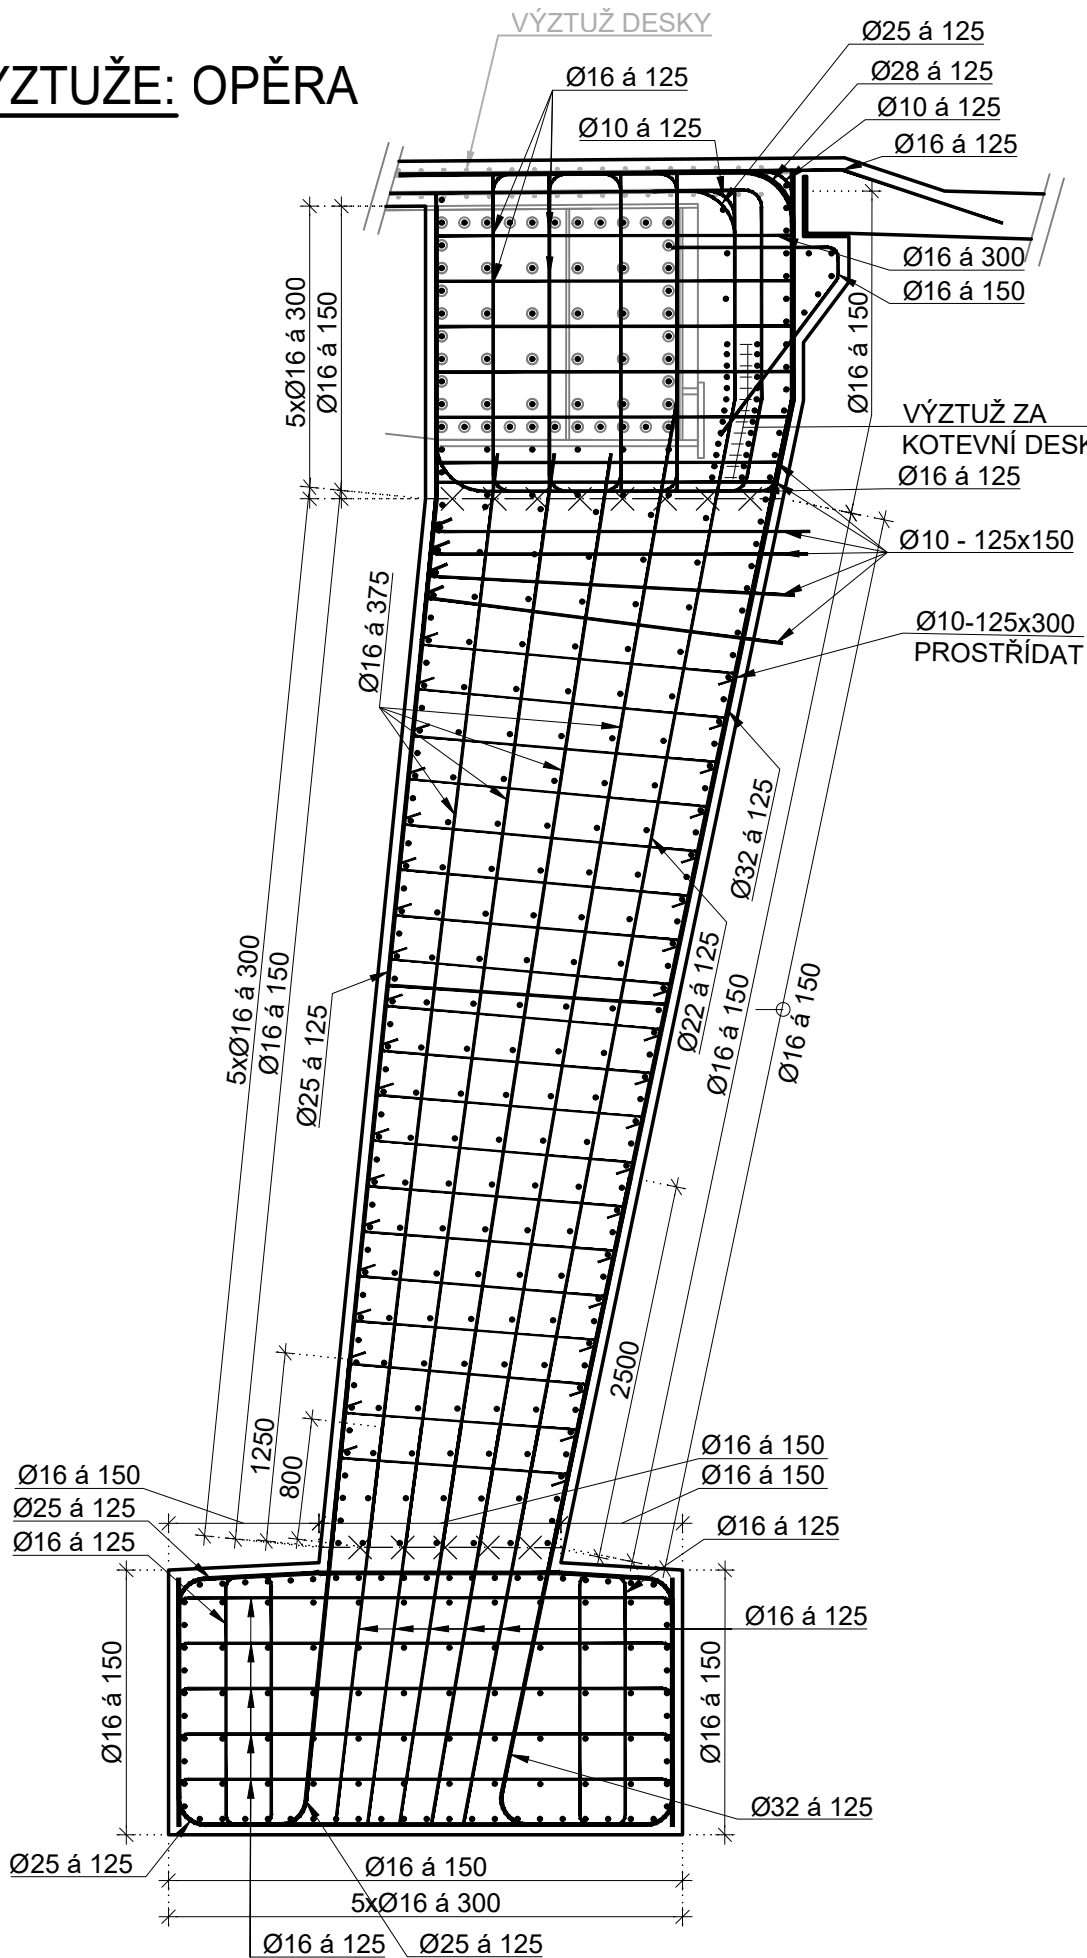


SCHÉMA VÝZTUŽE: PŘECHODOVÁ DESKA

M 1:50

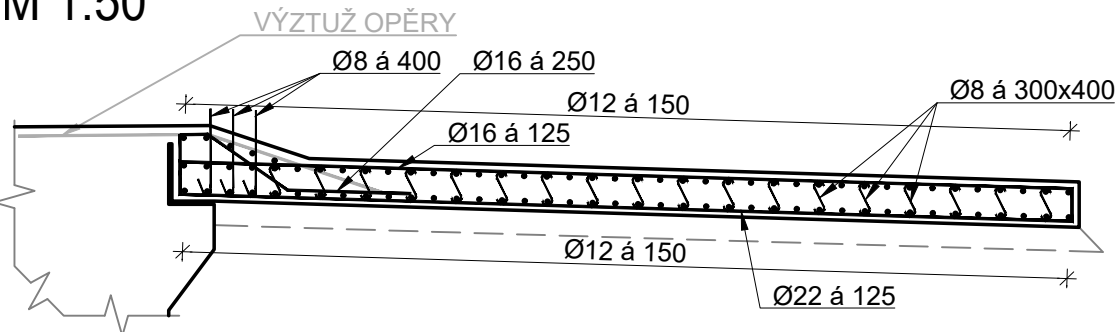


SCHÉMA VÝZTUŽE: DESKA MOSTOVKY V POLI

M 1:50


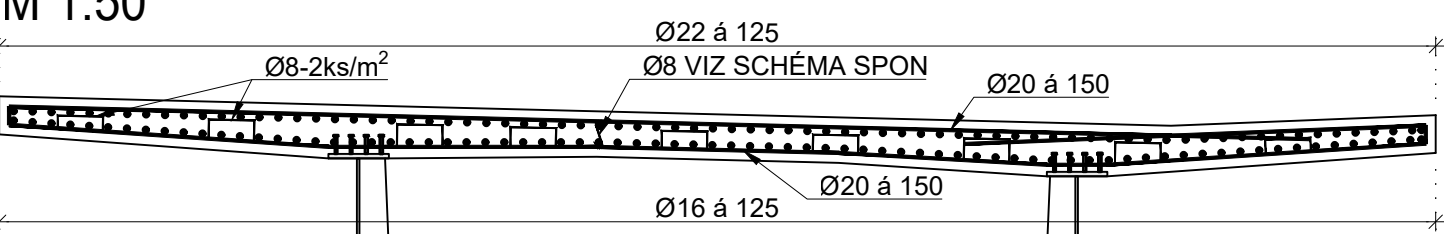


SCHÉMA VÝZTUŽE: DESKA MOSTOVKY V PODPOŘE

M 1:50

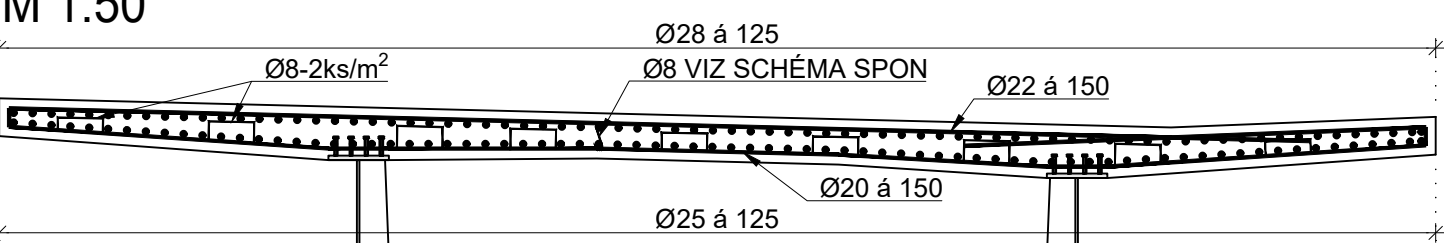

POZNÁMKY:

1. MATERIÁLY VIZ TECHNICKÁ ZPRÁVA

DETAILY DLE VL:

1. ULOŽENÍ PŘECHODOVÉ DESKY


-DLE VL 302.04

2. TĚSNĚNÍ DILATAČNÍ, PRACOVNÍ

A SMRŠŤOVACÍ SPÁRY OPĚR A ZDÍ

-DLE VL 208.01, 208.03, 208.04

SCHÉMA ROZMÍSTĚNÍ SPON:

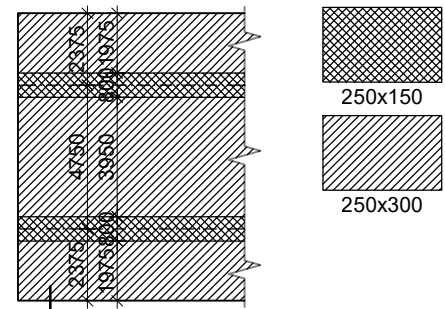

KRYTÍ:

NOSNÁ KONSTRUKCE:

MINIMÁLNÍ: 45 mm

JMENOVITÉ: 55 mm

SPODNÍ STAVBA:

MINIMÁLNÍ: 50 mm

JMENOVITÉ: 60 mm

PŘECHODOVÁ DESKA:

PŘI HORNÍM POVRCHU

MINIMÁLNÍ: 50 mm

JMENOVITÉ: 60 mm


PŘI DOLNÍM POVRCHU

MINIMÁLNÍ: 30 mm

JMENOVITÉ: 40 mm

OHÝBÁNÍ VÝZTUŽE dle ČSN EN1992-1-1

PRŮMĚR ZAKŘIVENÍ dbr

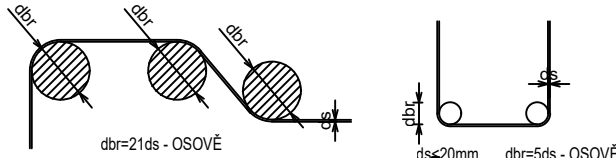

průměr výztuže d<16mm - průměr ohybu d=4dr

průměr výztuže d>16mm - průměr ohybu d=7dr

rozměry úseku položek jsou uvažovány na vnější okraje prutu

SCHÉMA VÝZTUŽE

SO 226

D.1.2

VÝŠKOVÝ SYSTÉM Bpv

SOUŘADNICOVÝ SYSTÉM S-JTSK

Číslo změny:	Obsah změny:	Datum změny:
01	-	-
02	-	-
03	-	-

Objednatel:	Ředitelství silnic a dálnic s. p. Na Pankráci 546/56, 140 00 Praha 4
	Stavbu zajišťuje Závod Praha Na Pankráci 546/56, 140 00 Praha 4

Zhotovitel: Společníci ve sdružení	SG_Velké projekty_BIM 2020 zastoupené
SUDOP PRAHA a.s. Hlavní inženýr projektu: Ing. Roman Petřík	Olšanská 1a, 130 80 Praha 3 telefon: +420 267 094 111

SUDOP PRAHA	PUDIS	SUDOP PRAHA	DOPRAVOPROJEKT BRNO	DOPRAVOPROJEKT
-------------	-------	-------------	---------------------	----------------

Správce:	SUDOP PRAHA a.s. Olšanská 1a, 130 80 Praha 3 tel.: +420 267 094 111 e-mail: praha@sudop.cz	Vedoucí týmu:	Asistent vedoucího týmu:
	ING. ROMAN PETŘÍK		ING. PAVEL MICHL
			Specialista profese:
			ING. PAVEL JIŘÍČEK, PH.D.

Zpracovatel částí:	projektová, průzkumná a konzultační společnost
	PUDIS a.s., Podbabská 1014/20, 160 00 Praha 6 tel.: +420 267 004 111, www.pudis.cz, info@pudis.cz

Vedoucí střediska:	Odpovědný projektant SO, IO, PS:	Vypracoval:	Kontroloval:
ING. MIROSLAV KROUPAR	ING. LUDVÍK KOLPASKÝ	TOMÁŠ POKORNÝ	ING. LUDVÍK KOLPASKÝ

Název akce:	Číslo smlouvy:
D11 1108 Jaroměř - Trutnov VD-ZDS + TP + AD	22-014.250

Část:	Projektový stupeň:
D.1.2 MOSTNÍ OBJEKTY A ZDI	VD-ZDS
SO 226 NADJEZD NA PŘELOŽCE SILNICE III/30015 V KM 132,150	Datum:
	05/2024
	Číslo části:
	D.1.2

Název přílohy:	Měřítko:	Počet formátů:
SCHÉMA VÝZTUŽE	1:50	4xA4
	Číslo přílohy:	09