


PŘECHODOVÉ OBLASTI A DESKY

M 1:50

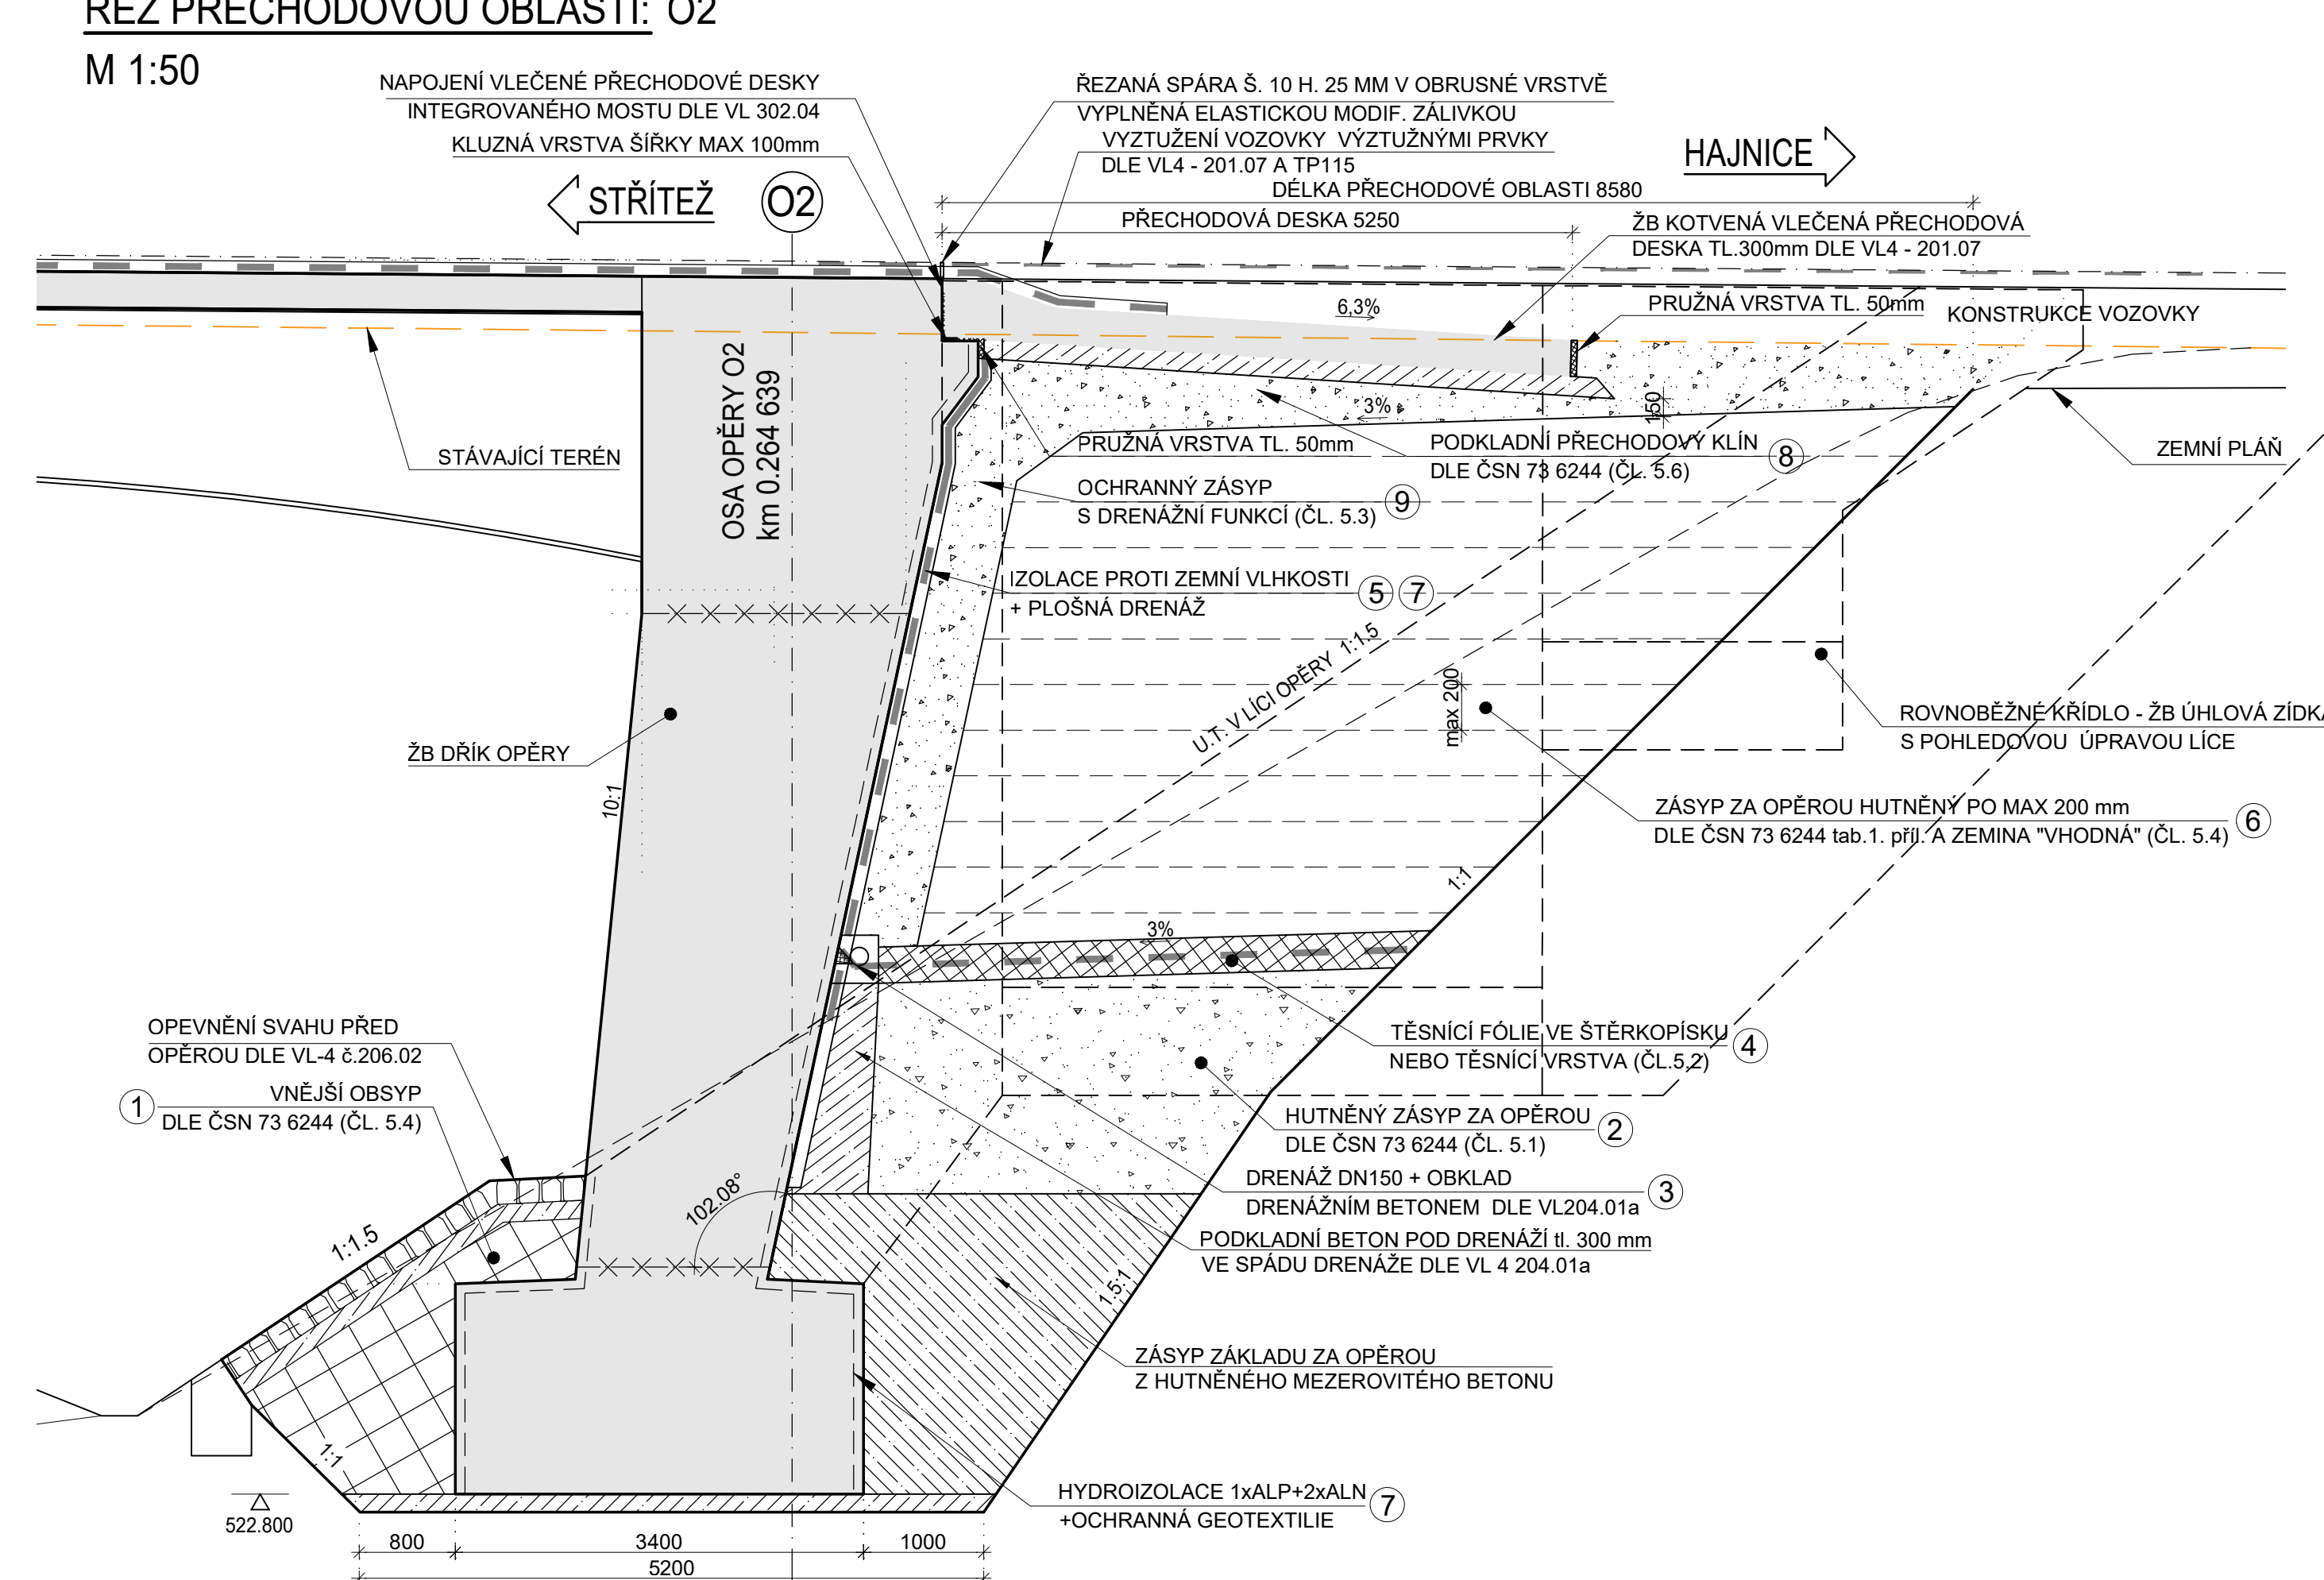

Podkladní Ochranný zásyp rubu opěry bude proveden dle ČSN 73 6244 ze ŠD
0-32,ŠP,GW,GP,SW,SP. Tloušťka zásypu min. 600 mm od rubu opěry. Min. míra zhutnění je dle ČSN
73 6244 I=0.85 nebo D=100%, po vrstvách max. 200 mm.

PRECHODOVE OBLASTI A DESKY 10

DOKUMENT LZE UŽÍVAT POUZE VE SMYSLU PŘÍSLUŠNÉ SMLOUVY O DÍLO. ŽÁDNÁ JEHO ČÁST NEMŮŽE BYT DÍLE ZÁKONA č. 121/2000 Sb. KOPIJOVÁNA NEBO JINÝM ZPŮSOBEM ROZŠÍŘOVÁNA. BEZ SOUHLASU SUDOP PRAHA a.