



SO 226 NADJEZD NA PŘELOŽCE SILNICE III/30015 V KM 132,150

PŮDORYS: TVAR OK
M 1:100

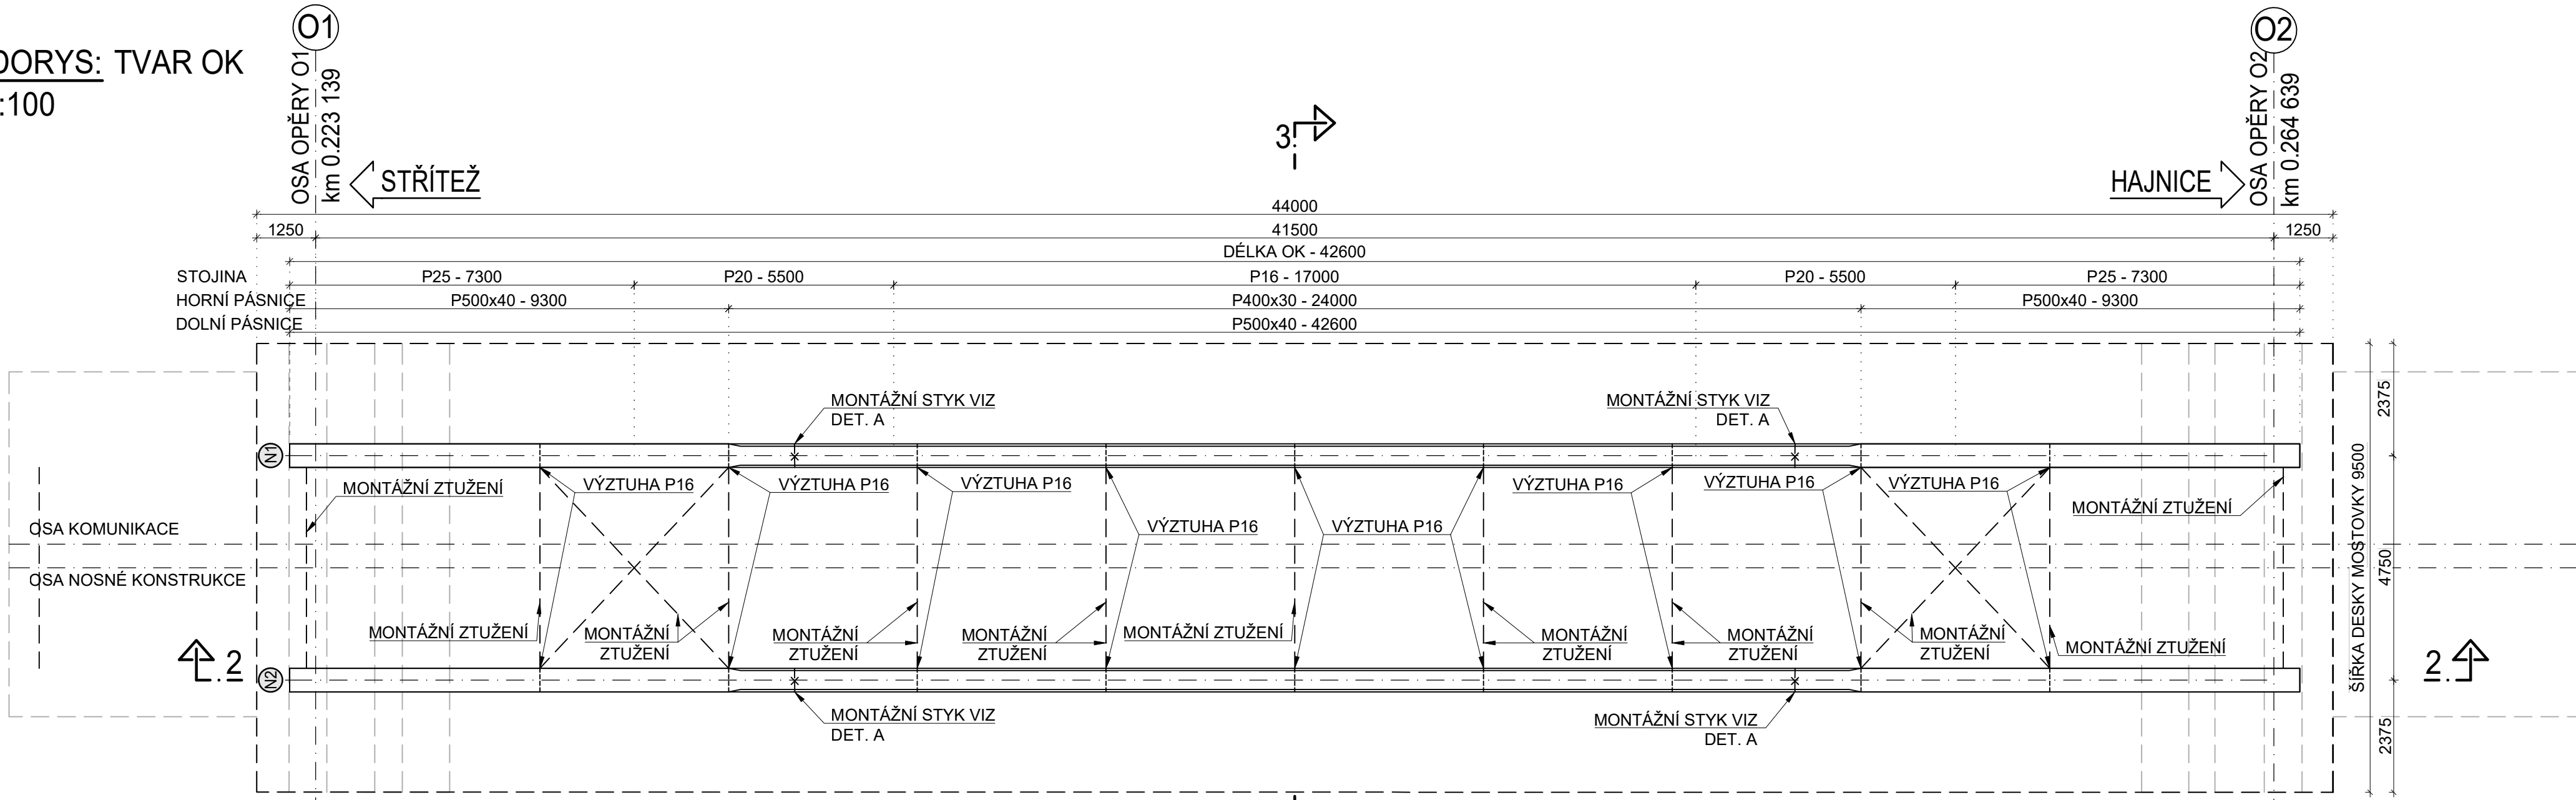


PODÉLNÝ ŘEZ: ŘEZ 2-2
M 1:100

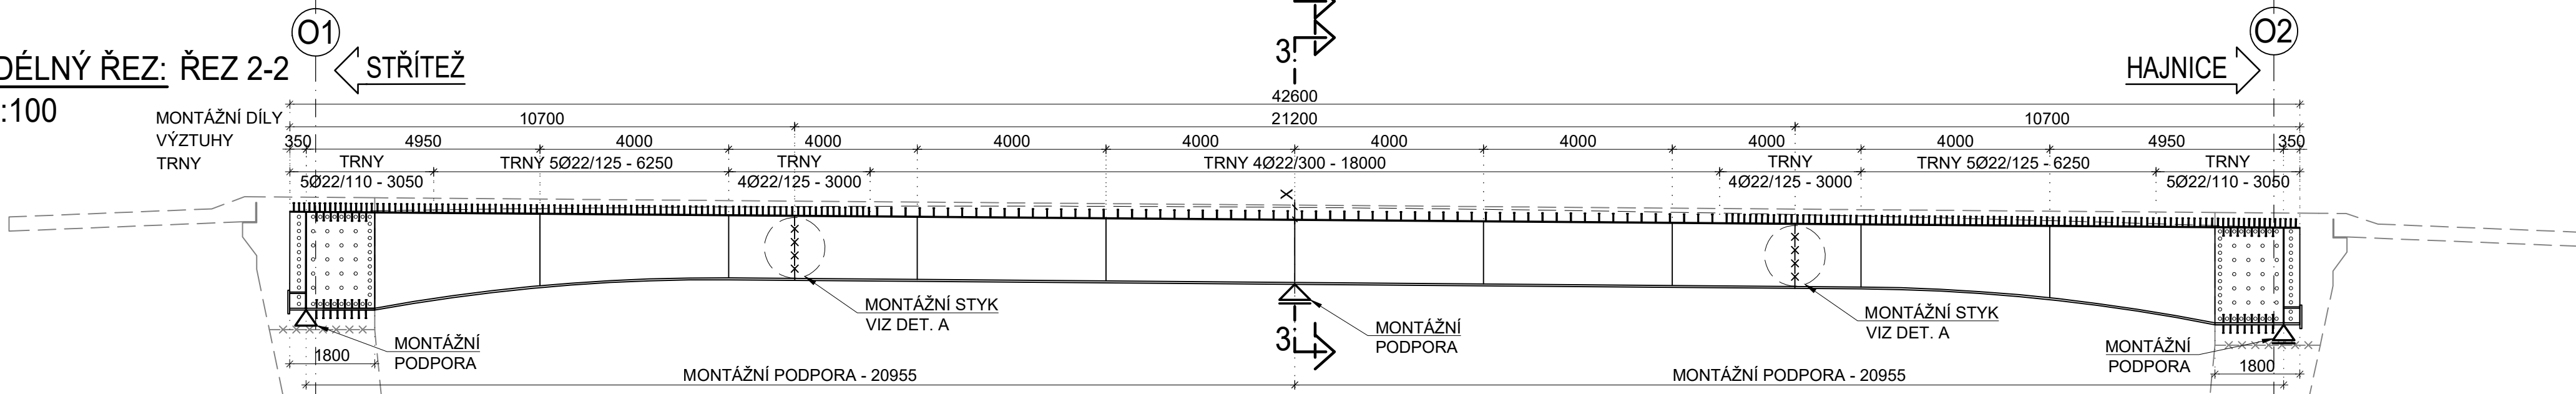


NOSNÁ OCELOVÁ KONSTRUKCE - TVAR


PŘÍČNÝ ŘEZ: ŘEZ 3-3
M 1:50

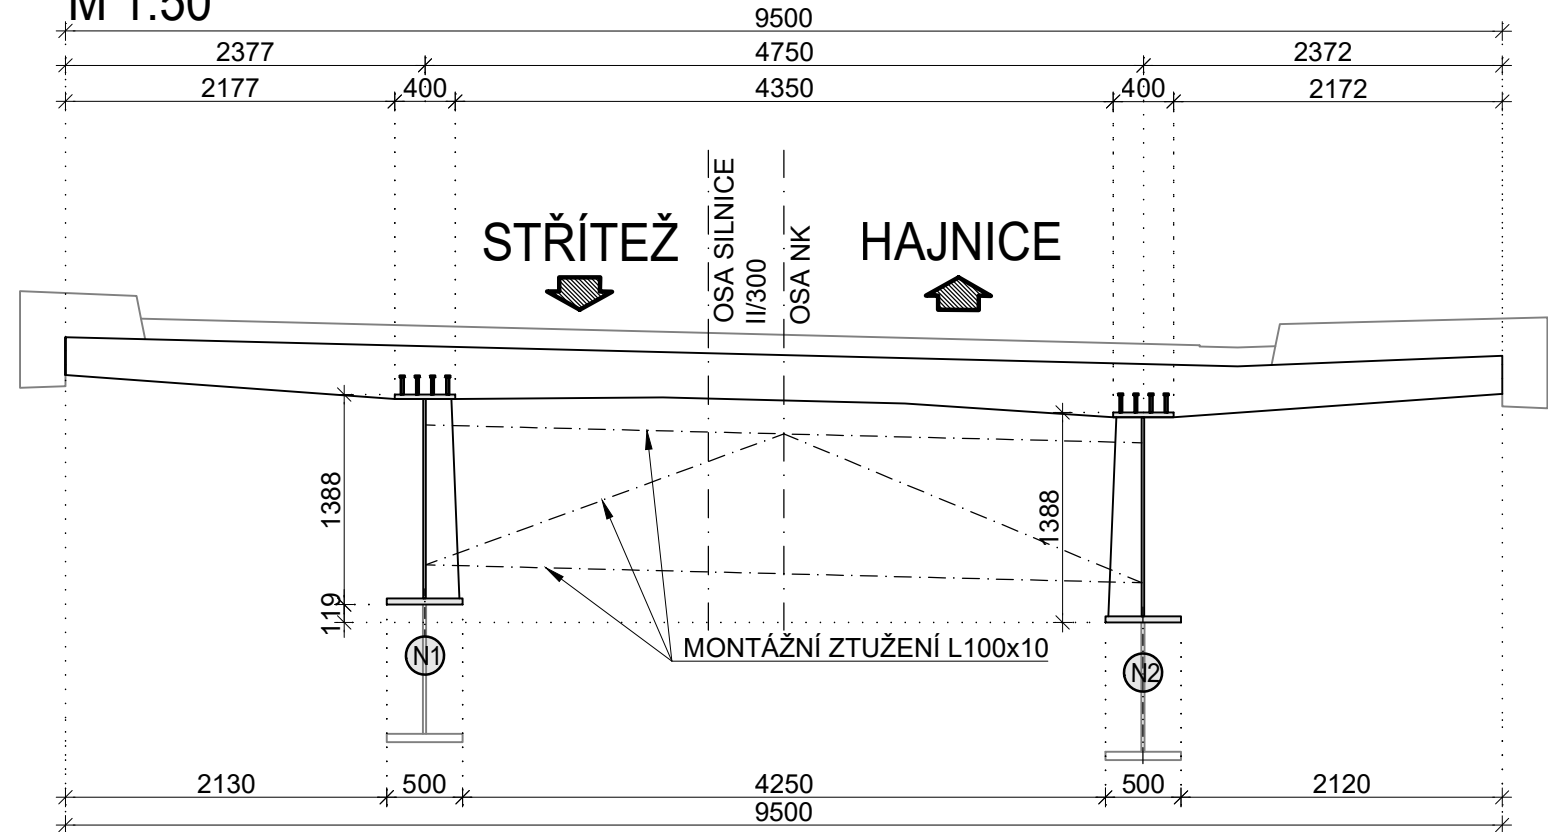

DETAIL A: MONTÁŽNÍ STYK
M 1:20

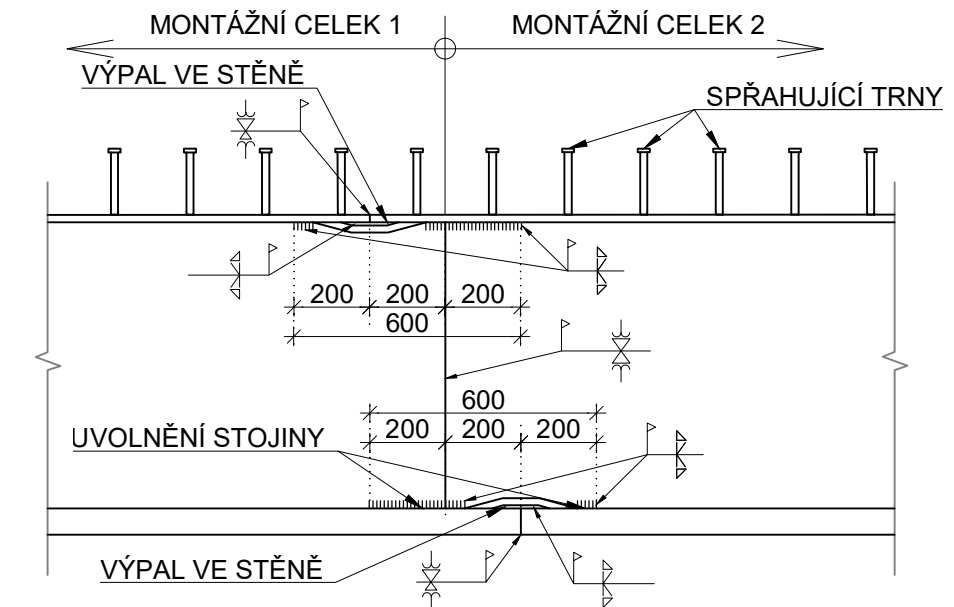

DETAIL B: ZMĚNA TLOUŠTKY PÁSNIC
M 1:20

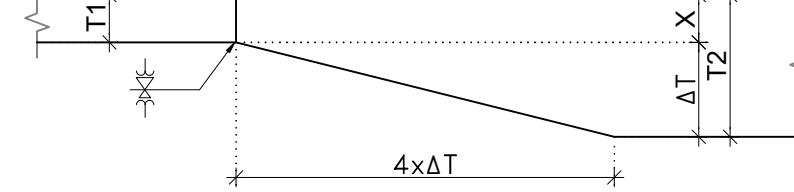

SO 226
D.1.2

VÝŠKOVÝ SYSTÉM Bpv SOUŘADNICOVÝ SYSTÉM S-JTSK

Číslo změny:	Obsah změny:	Datum změny:
01	-	-
02	-	-
03	-	-

Objednatel:	Ředitelství silnic a dálnic s. p. Na Pankráci 546/56, 140 00 Praha 4
Stavbu zajišťuje:	Závod Praha Na Pankráci 546/56, 140 00 Praha 4

Zhotovitel: Společnosti ve sdružení	SG_Velké projekty BIM 2020 zastoupené
SUDOP PRAHA a.s. Hlavní inženýr projektu: Ing. Roman Petřík	Olšanská 1a, 130 80 Praha 3 telefon: +420 267 094 111

SUDOP PRAHA	PUDIS	SUDOP PRAHA	DOPRAVOVÝ PROJEKT BRNO	DOPRAVOVÝ PROJEKT
-------------	-------	-------------	------------------------	-------------------

Správce:	SUDOP PRAHA a.s. Olšanská 1a, 130 80 Praha 3 tel.: +420 267 094 111 e-mail: praha@sudop.cz	Vedoucí týmu:	ING. ROMAN PETŘÍK	Asistent vedoucího týmu:	ING. PAVEL MICHL Specialista profese: ING. PAVEL JIŘÍČEK, PH.D.
----------	---	---------------	-------------------	--------------------------	---

Zpracovatel částí:	projektová, průzkumná a konzultační společnost PUDIS a.s., Podbabská 1014/20, 160 00 Praha 6 tel.: +420 267 004 111, www.pudis.cz, info@pudis.cz
--------------------	--

Vedoucí střediska:	Odpovědný projektant SO, IO, PS:	Vypracoval:	Kontroloval:
ING. MIROSLAV KROUPAR	ING. LUDVÍK KOLPASKÝ	TOMÁŠ POKORNÝ	ING. LUDVÍK KOLPASKÝ

Název akce:	Číslo smlouvy:
D11 1108 Jaroměř - Trutnov VD-ZDS + TP + AD	22-014.250

Část:	Datum:
D.1.2 MOSTNÍ OBJEKTY A ZDI SO 226 NADJEZD NA PŘELOŽCE SILNICE III/30015 V KM 132,150	05/2024

Název přílohy:	Měřítko:	Počet formátů:
NOSNÁ OCELOVÁ KONSTRUKCE - TVAR	1:100, 1:50	5x A4
	Číslo přílohy:	11.1

OKUMENT LZE UŽÍVAT POUZE VE SMYSLU PRÍSLUŠNÉ SMLOUVY O DÍLO. ŽÁDNÁ JEHO ČÁST NEMŮŽE BYT DÍLE ŽÁKONA 121/2000 Sb. KOPÍROVÁNÁ NEBO JINÝM ZPŮSOBEM ROZŠÍŘOVÁNÁ. BEZ SOUHLASU SUDOP PRAHA a.s.