


TVAR DESKY MOSTOVKY

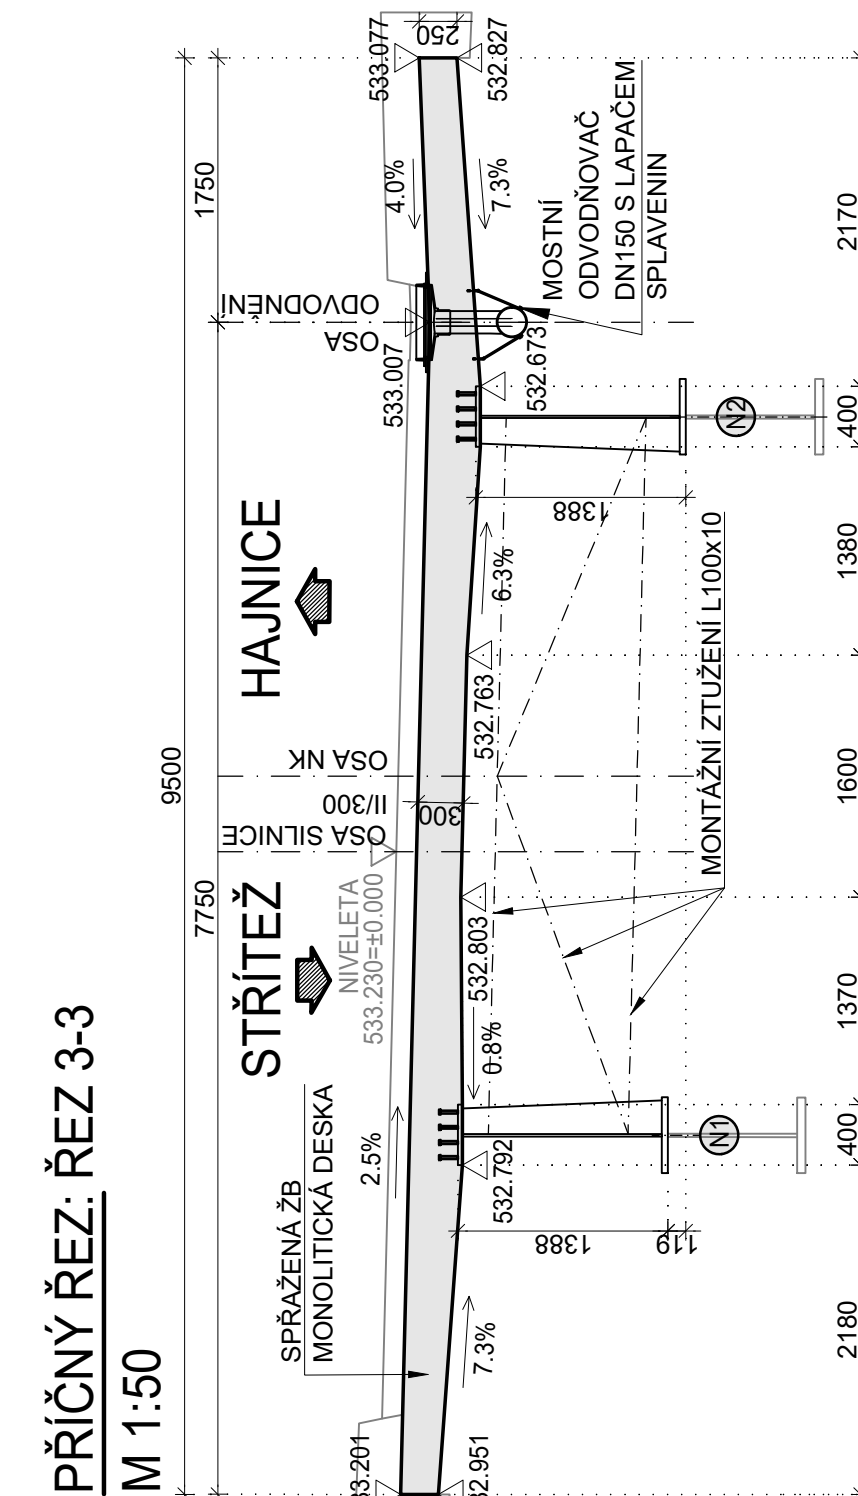

1. MATERIÁLY VIZ TZ
2. POHLEDOVÉ PLOCHY BETONU VIZ TZ
3. HRANY BETONU BUDOU ZKOSENY 20/20 mm

Název akce:	Číslo smlouvy:	
	22-014.250	
D11 1108 Jaroměř - Trutnov VD-ZDS + TP + AD	Projektový stupeň:	
	VD-ZDS	
Část: D.1.2 MOSTNÍ OBJEKTY A ZDI SO 226 NADJEZD NA PŘELOŽCE SILNICE III/30015 V KM 132,150	Datum:	
	05/2024	
Název přílohy:	Číslo části:	
	D.1.2	
	Měřítko:	Počet formátů:
TVAR DESKY MOSTOVKY	1:100,1:50	4xA4
	Číslo přílohy:	
	12	

DOKUMENT LZE UŽÍVAT POUZE VE SMYSLU PŘÍSLUŠNÉ SMLOUVY O DÍLO. ŽÁDNÁ JEHO ČÁST NEMŮŽE BÝT DLE ZÁKONA č. 121/2000 Sb. KOPÍROVÁNA NEBO JINÝM ZPŮSOBEM ROZŠÍŘOVÁNA BEZ SOUHLASU SUDOP PRAHA a.s.