


SO 226 NADJEZD NA PŘELOŽCE SILNICE III/30015 V KM 132,150

TVAR ŘÍMS, SVODIDLA A ZÁBRADLÍ


PŮDORYS

M 1:200

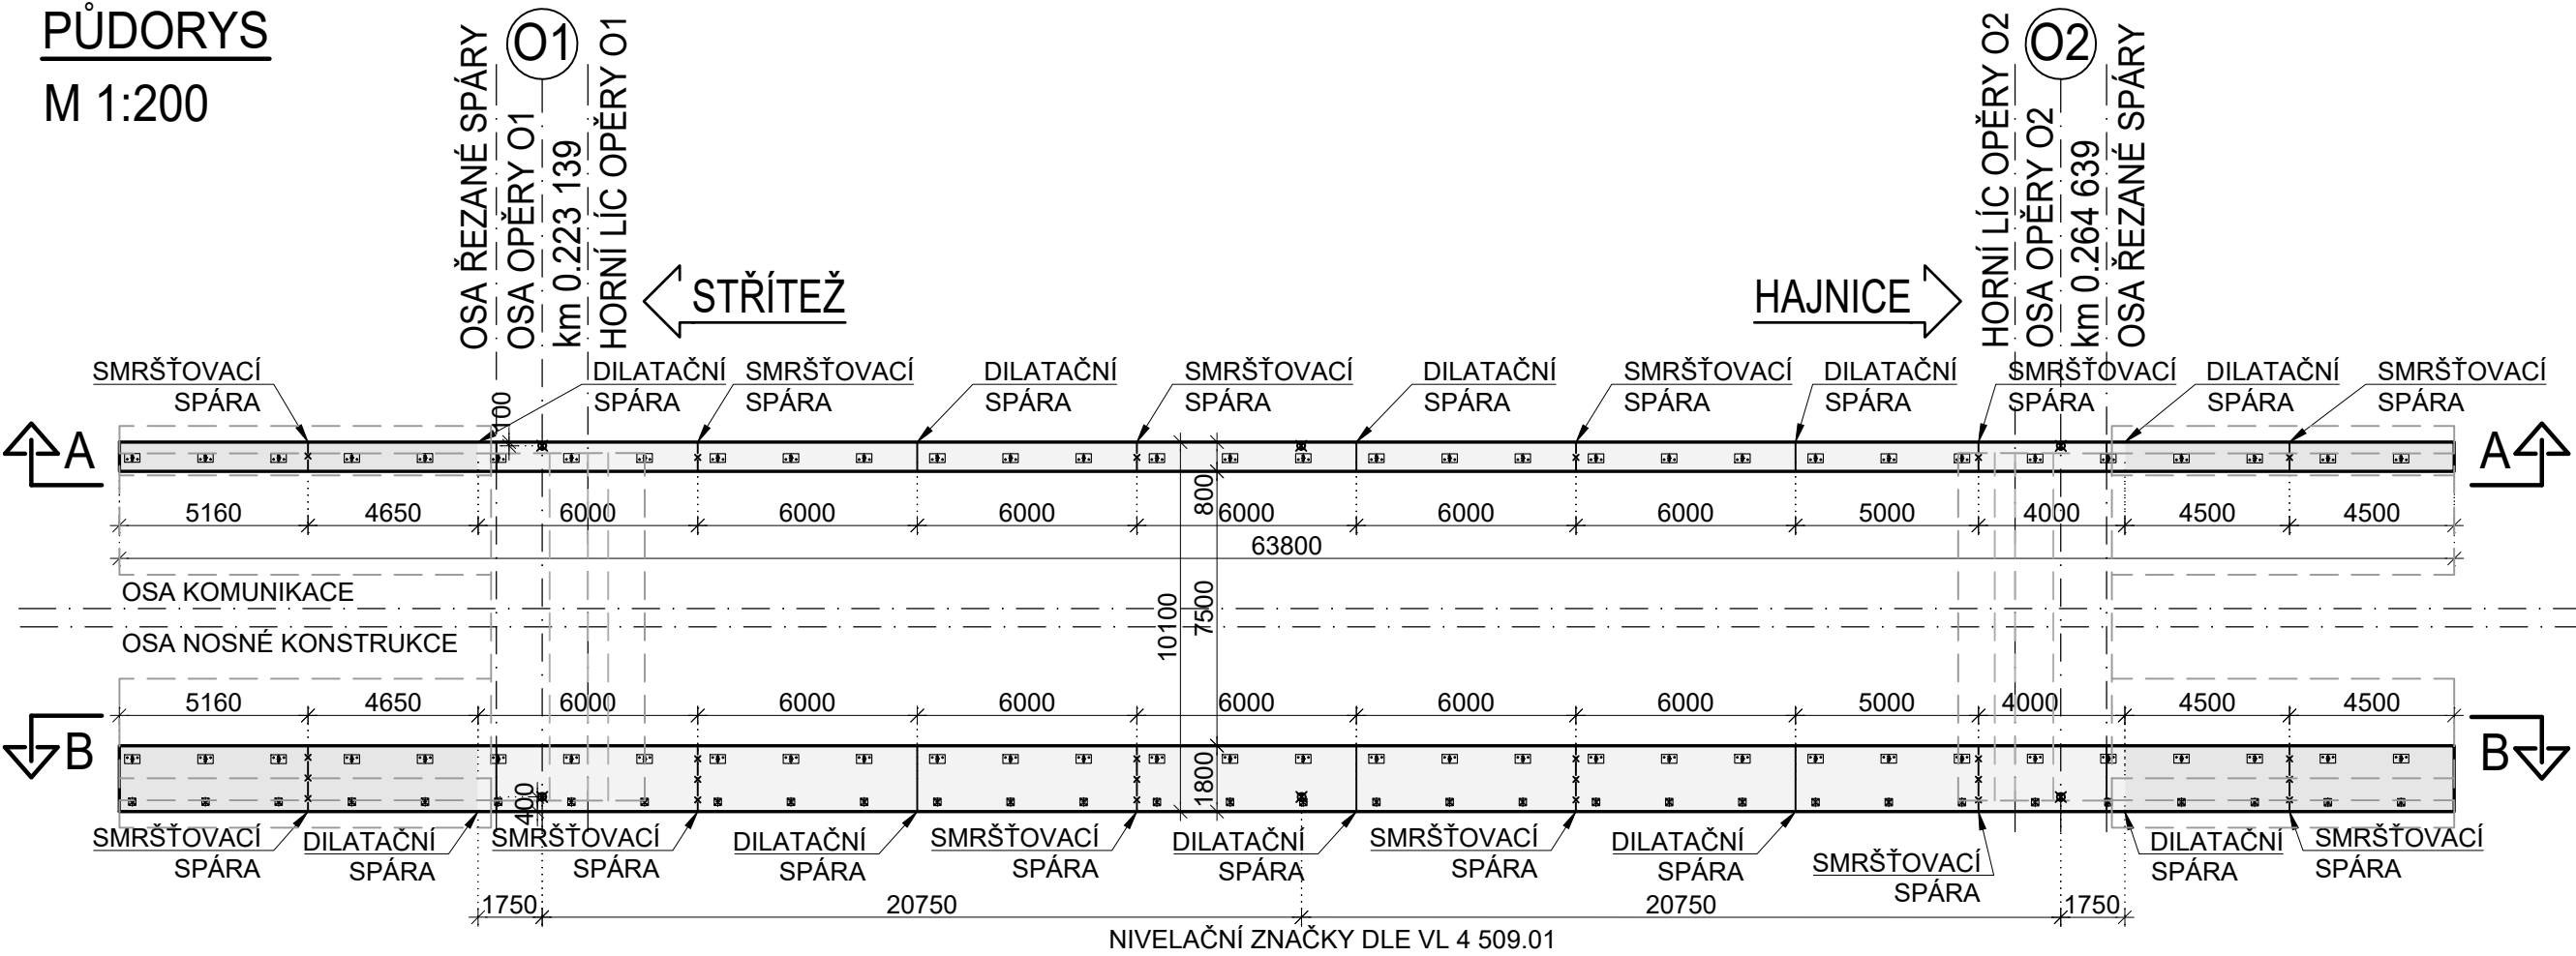

PŘÍČNÝ ŘEZ MOSTEM : TVAR ŘÍMS


M 1:25

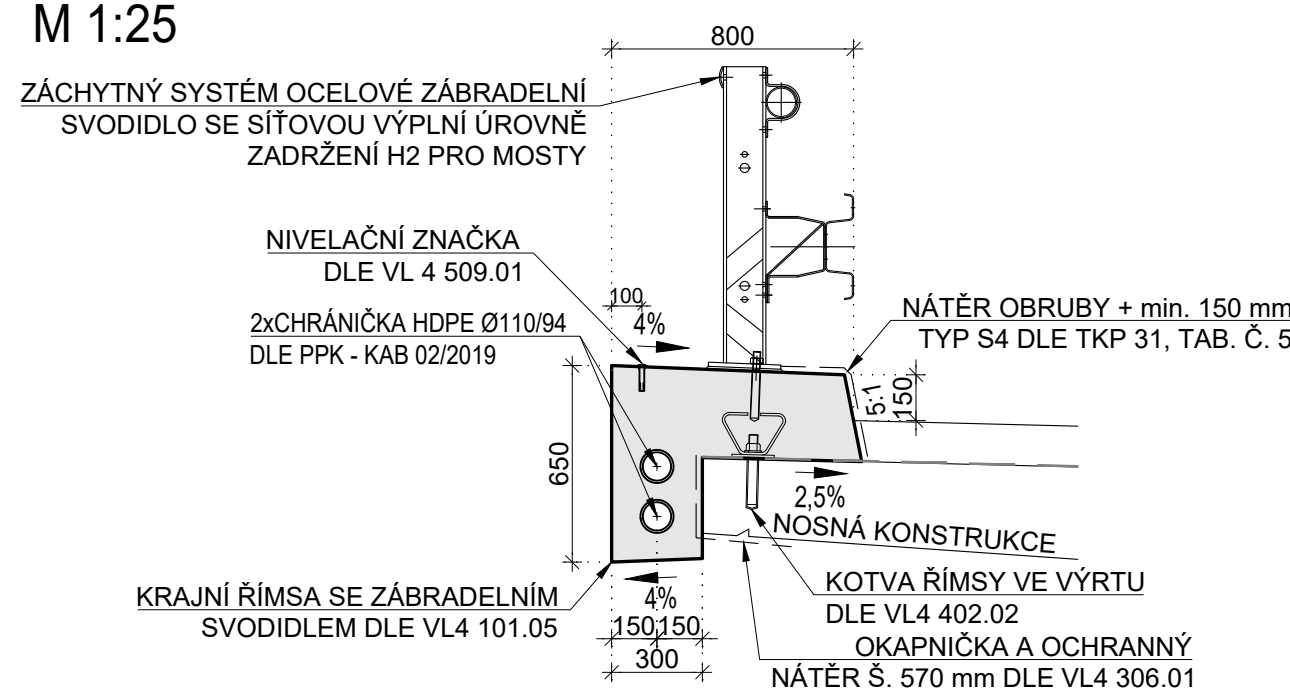

ZÁCHYTNÝ SYSTÉM OCELOVÉ ZÁBRADELNÍ SVODIDLO ÚROVNĚ ZADRŽENÍ H2 PRO MOSTY

NÁTĚR OBRUBY + min. 150 mm TYP S4 DLE TKP 31, TAB. Č. 5


HAJNICE

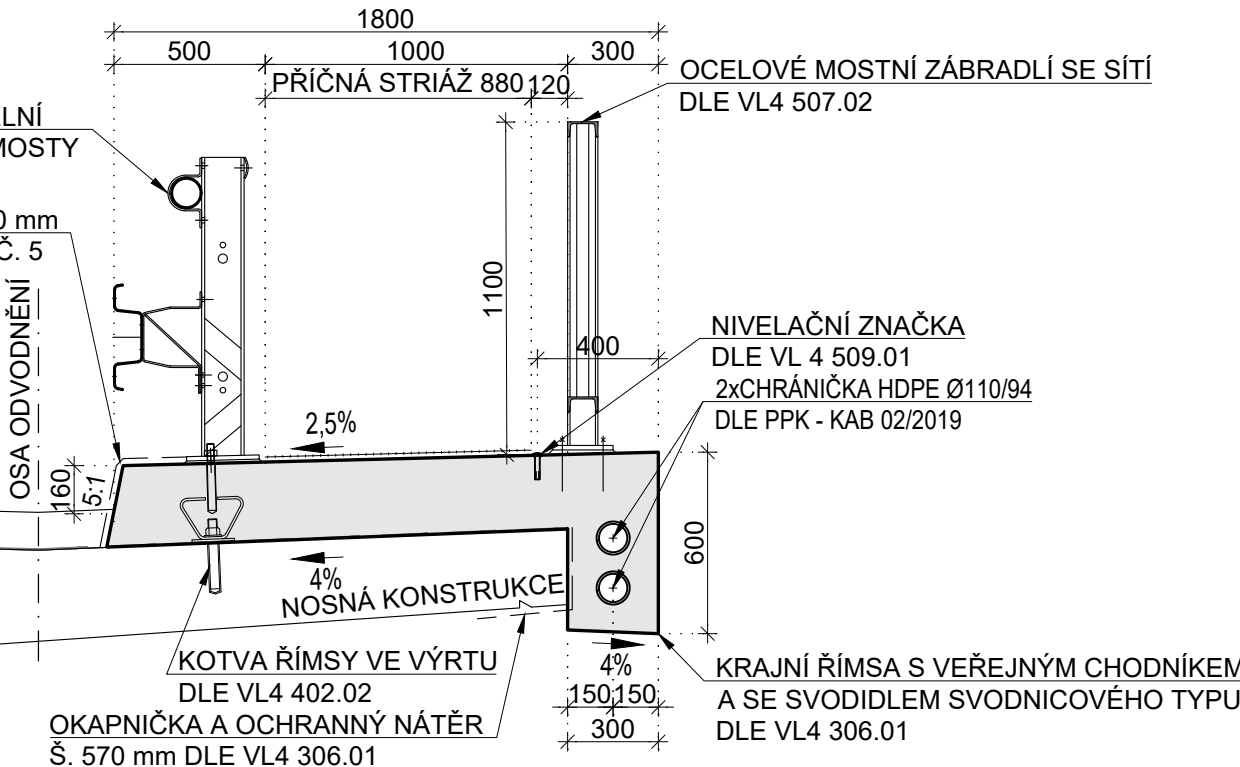

POHLED A-A

M 1:100


STRÍTEŽ HAJNICE

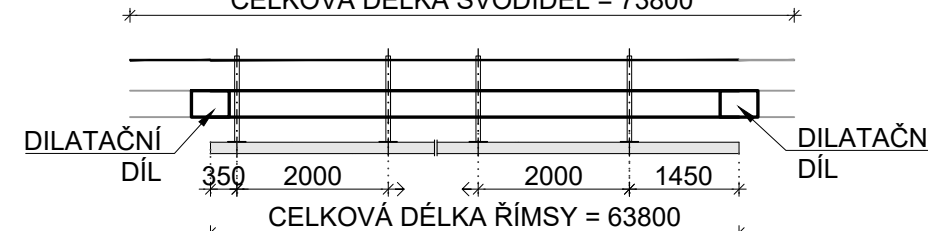

POHLED B-B

M 1:100

HAJNICE STRÍTEŽ

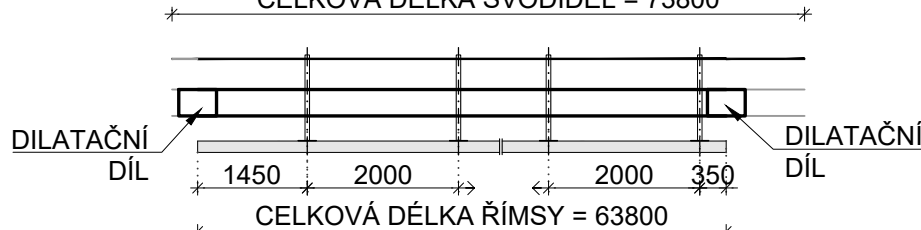


KRYTÍ:

Cmin = 45 mm / Cnom = 55 mm

OHÝBÁNÍ VÝZTUŽE dle ČSN EN1992-1-1

PRŮMĚR ZAKŘIVENÍ dbr

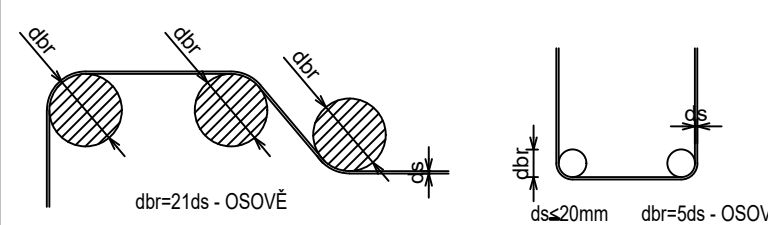

průměr výztuže d<16mm - průměr ohybu d=4dr
průměr výztuže d>16mm - průměr ohybu d=7dr
rozměry úseku položek jsou uvažovány na vnější okraje prutu

POZNÁMKY:

- MATERIÁLY VIZ TECHNICKÁ ZPRÁVA
- ZKOSENÍ HRAN ŘÍMS U OBRUB DLE CERTIFIKOVANÉHO ZÁDRŽNÉHO SYSTÉMU SVODIDLA, OSTATNÍ HRANY ŘÍMS 15/15mm
- DILATAČNÍ DÍLY SVODIDEL BUDOU UMÍSTĚNY V MÍSTĚ ŘEZANÉ SPÁRY VE VOZOVCE A NA KONCÍCH KŘÍDEL
- DILATACE SVODIDLA PŘED A ZA MOSTEM (SOUČÁST SO 101)

DETAILY:

- TĚSNĚNÍ SPÁR ŘÍMSY
- ODVODŇOVACÍ PROUŽEK Z LITÉHO ASFALTU
- TĚSNĚNÍ SPÁRY PODÉL OBRUBNÍKU
- NAPOJENÍ IZOLACE U ŘÍMSY
- VYVEDENÍ KABELOVÝCH CHRÁNIČEK U OPĚR
- NIVELAČNÍ ZNAČKY
- VÝZTUŽ ŘÍMS
- KOTVA ŘÍMSY VE VÝVRTU
- OKAPNIČKA A OCHRANNÝ NÁTĚR KONCŮ NK
- KRAJNÍ ŘÍMSA S VEŘEJNÝM CHODNÍKEM A SE SVODIDLEM SVODNICOVÉHO TYPU
- KRAJNÍ ŘÍMSA SE ZÁBRADELNÍM SVODIDLEM

DLE VL 402.21, 402.22, 402.23

DLE VL 403.41

DLE VL 403.42

DLE VL 403.45

DLE VL 402.11

DLE VL 509.01

DLE VL 402.31

DLE VL 402.02

DLE VL 306.01

DLE VL4 306.01

DLE VL4 101.05

SO 226

D.1.2

VÝŠKOVÝ SYSTÉM BpV

SOUŘADNICOVÝ SYSTÉM S-JTSK

Číslo změny:	Obsah změny:	Datum změny:
01	-	-
02	-	-
03	-	-

Objednatel:	Ředitelství silnic a dálnic s. p. Na Pankráci 546/56, 140 00 Praha 4
	Stavbu zajišťuje Závod Praha Na Pankráci 546/56, 140 00 Praha 4

Zhotovitel: Společníci ve sdružení	SG_Velké projekty BIM 2020 zastoupené
SUDOP PRAHA a.s. Hlavní inženýr projektu: Ing. Roman Petřík	Olšanská 1a, 130 80 Praha 3 telefon: +420 267 094 111

Správce:	SUDOP PRAHA a.s. Olšanská 1a, 130 80 Praha 3 tel.: +420 267 094 111 e-mail: praha@sudop.cz	Vedoucí týmu:	ING. ROMAN PETŘÍK	Asistent vedoucího týmu:	ING. PAVEL MICHL Specialista profese: ING. PAVEL JIŘÍČEK, PH.D.
----------	---	---------------	-------------------	--------------------------	---

Zpracovatel části:	projektová, průzkumná a konzultační společnost PUDIS a.s., Podbabská 1014/20, 160 00 Praha 6 tel.: +420 267 004 111, www.pudis.cz, info@pudis.cz
--------------------	--

Vedoucí střediska:	Odpovědný projektant SO, IO, PS:	Vypracoval:	Kontroloval:
ING. MIROSLAV KROUPAR	ING. LUDVÍK KOLPASKÝ	TOMÁŠ POKORNÝ	ING. LUDVÍK KOLPASKÝ

Název akce:	Číslo smlouvy:
	22-014.250
D11 1108 Jaroměř - Trutnov VD-ZDS + TP + AD	Projektový stupeň:
	VD-ZDS
Část:	Datum:
D.1.2 MOSTNÍ OBJEKTY A ZDI	11/2024
SO 226 NADJEZD NA PŘELOŽCE SILNICE III/30015 V KM 132,150	Číslo části:
	D.1.2
Název přílohy:	Měřítko: 1:25 1:100,1:200 Číslo přílohy:
	Počet formátů: 4xA4
TVAR ŘÍMS, SVODIDLA A ZÁBRADLÍ	13