



VÝKRES ODVODNĚNÍ


PODÉLNÝ ŘEZ OSOU ODVODNĚNÍ:
M 1:100

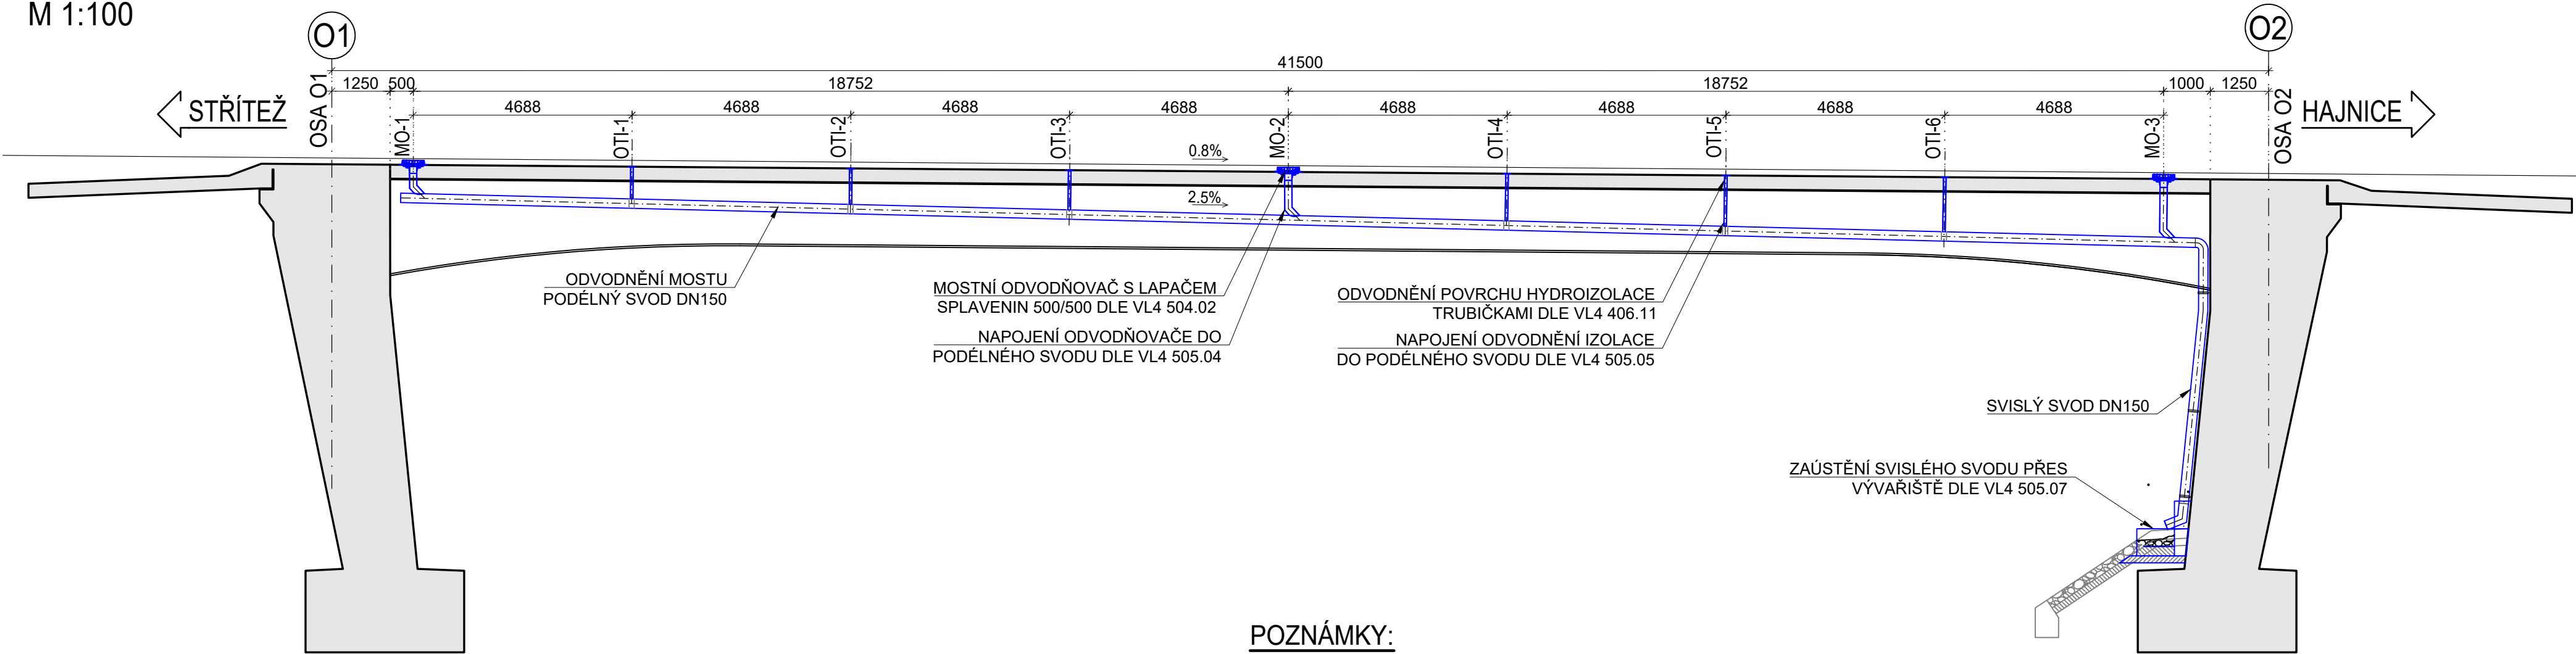

PŘÍČNÝ ŘEZ V MÍSTĚ ODVODŇOVAČE:
M 1:50

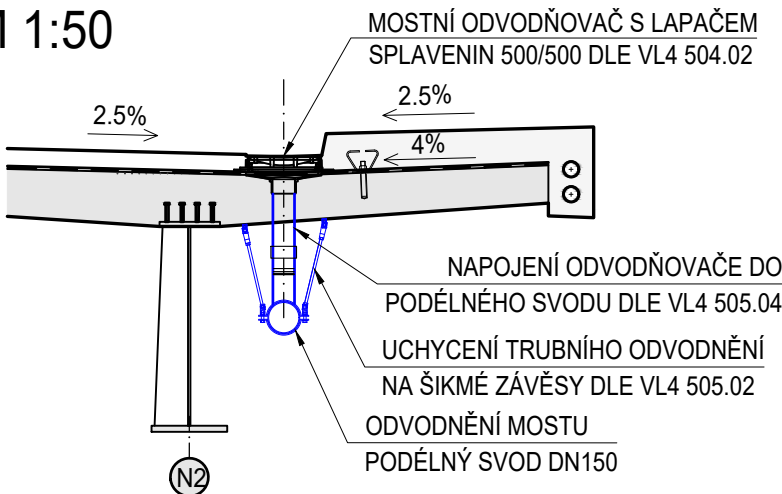

PŘÍČNÝ ŘEZ V MÍSTĚ OTI:
M 1:50

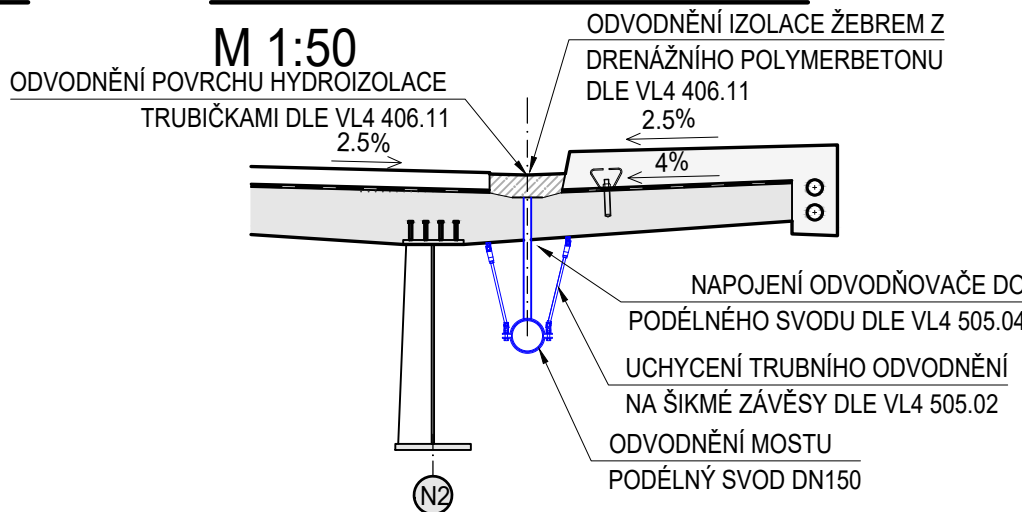

POZNÁMKY:

- OCELOVÉ PŘÍSLUŠENSTVÍ ODVODNĚNÍ (ZÁVĚSY POTRUBÍ, KOTEVNÍ PRVKY, OBJÍMKY) BUDOU NAVRŽENY Z KOROZIVZDORNÉ OCELI 1.4401, 1.4404, 1.4406 NEBO 1.4571 DLE TKP 19A. VŠECHNY SOUČÁSTI ODVODŇOVAČŮ VČETNĚ SPOJOVACÍHO MATERIÁLU BUDOU VYROBENY Z NEREZÁVĚJÍCÍHO MATERIÁLU.
- PROTIKOROZNÍ ÚPRAVA OCELOVÝCH ČÁSTÍ ODVODNĚNÍ BUDE REALIZOVÁNA DLE TKP SPK 19N, TP 107 A VL4
- NAVŘH ODVODNĚNÍ A MATERIÁL TRUB JE DLE TP 107.
- DODANÝ SYSTÉM ODVODNĚNÍ MUSÍ BÝT CERTIFIKOVANÝ.
- PODÉLNÉ SBĚRNÉ POTRUBÍ DN150 JE SVEDENÉ SVISLÝM SVODEM PŘED OPĚROU DO VÝVĚŘÍŠTĚ, NÁSLEDNĚ DO PŘÍKOPU SILNICE.

MATERIÁLY:

- | | |
|---------------------------------------|--------|
| 1. SKLOLAMINÁT | |
| PODÉLNÝ SVOD DN150 | 38,8 m |
| SVISLÝ SVOD DN150 | 6 m |
| 2. KOROZIVZDORNÁ OCEL | |
| TRUBIČKA ODVODNĚNÍ IZOLACE 1.4401, A4 | 6 ks |
| 3. ODVODŇOVAČE | |
| MOSTNÍ ODVODŇOVAČ S LAPAČEM NEČISTOT | 3 ks |

SO 226
D.1.2

VÝŠKOVÝ SYSTÉM Bpv

SOUŘADNICOVÝ SYSTÉM S-JTSK

Číslo změny:	Obsah změny:	Datum změny:
01	-	-
02	-	-
03	-	-

Objednatel:	Ředitelství silnic a dálnic s. p. Na Pankráci 546/56, 140 00 Praha 4
	Stavbu zajišťuje Závod Praha Na Pankráci 546/56, 140 00 Praha 4

Zhotovitel: Společníci ve sdružení	SG_Velké projekty BIM 2020 zastoupené
SUDOP PRAHA a.s. Hlavní inženýr projektu: Ing. Roman Petřík	Olšanská 1a, 130 80 Praha 3 telefon: +420 267 094 111

--	--	--	--	--

Správce:	SUDOP PRAHA a.s. Olšanská 1a, 130 80 Praha 3 tel.: +420 267 094 111 e-mail: praha@sudop.cz	Vedoucí týmu:	Asistent vedoucího týmu:
		ING. ROMAN PETŘÍK	ING. PAVEL MICHL Specialista profese: ING. PAVEL JIŘÍČEK, PH.D.

Zpracovatel částí:	projektová, průzkumná a konzultační společnost PUDIS a.s., Podbabská 1014/20, 160 00 Praha 6 tel.: +420 267 004 111, www.pudis.cz, info@pudis.cz
--------------------	--

Vedoucí střediska:	Odpovědný projektant SO, IO, PS:	Vypracoval:	Kontroloval:
ING. MIROSLAV KROUPAR	ING. LUDVÍK KOLPASKÝ	TOMÁŠ POKORNÝ	ING. LUDVÍK KOLPASKÝ

Název akce:	Číslo smlouvy:
D11 1108 Jaroměř - Trutnov VD-ZDS + TP + AD	22-014.250
Část:	Projektový stupeň:
D.1.2 MOSTNÍ OBJEKTY A ZDI SO 226 NADJEZD NA PŘELOŽCE SILNICE III/30015 V KM 132,150	VD-ZDS
Název přílohy:	Datum:
	11/2024
	Číslo částí:
	D.1.2
	Měřítko:
	1:100, 1:50
	Počet formátů:
	4xA4
	Číslo přílohy:
	14