

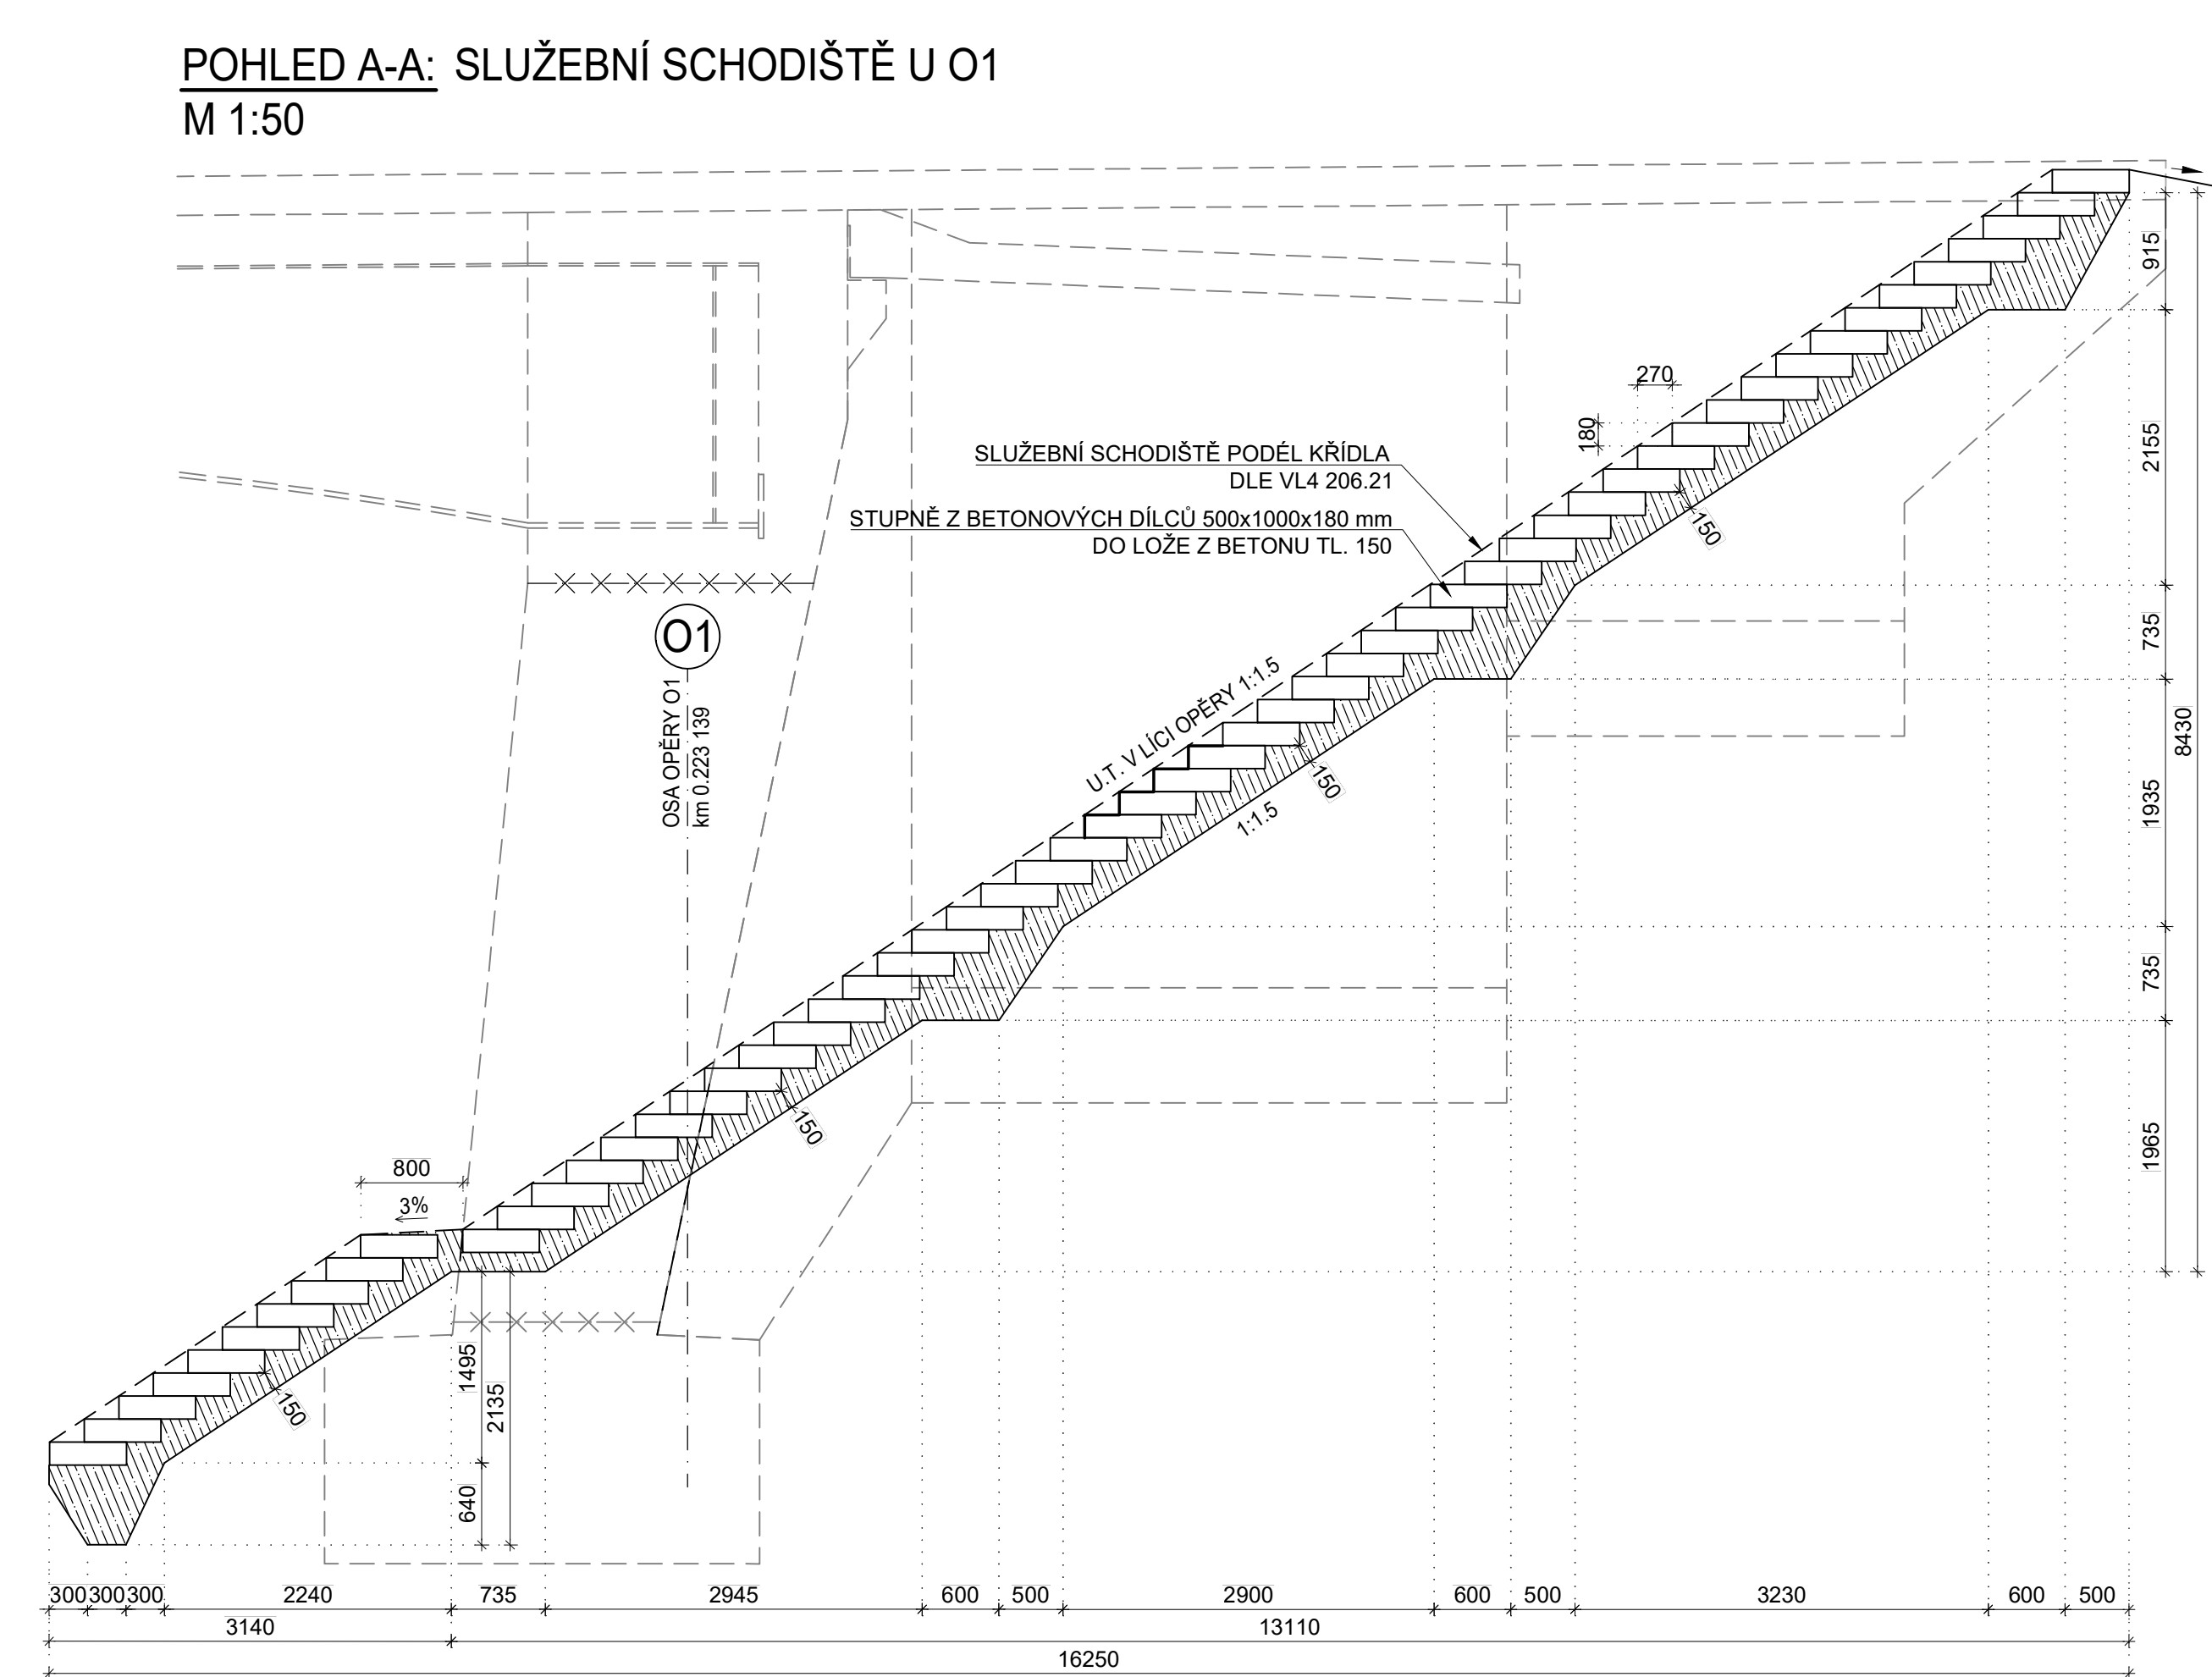


ÚPRAVY POD A KOLEM MOSTU

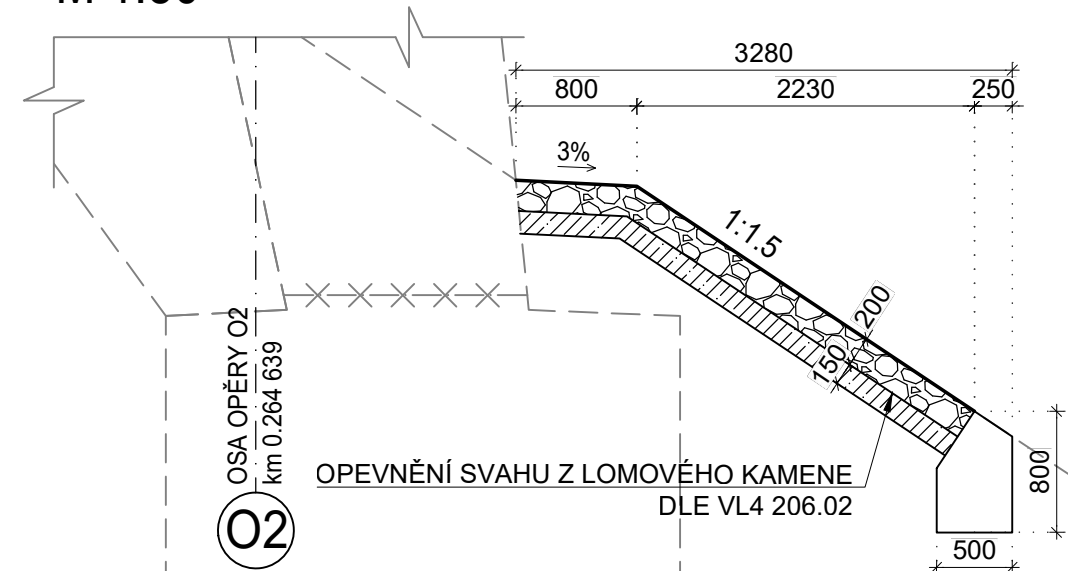

POHLED C-C: SLUŽEBNÍ SCHODIŠTĚ U O2
M 1:50

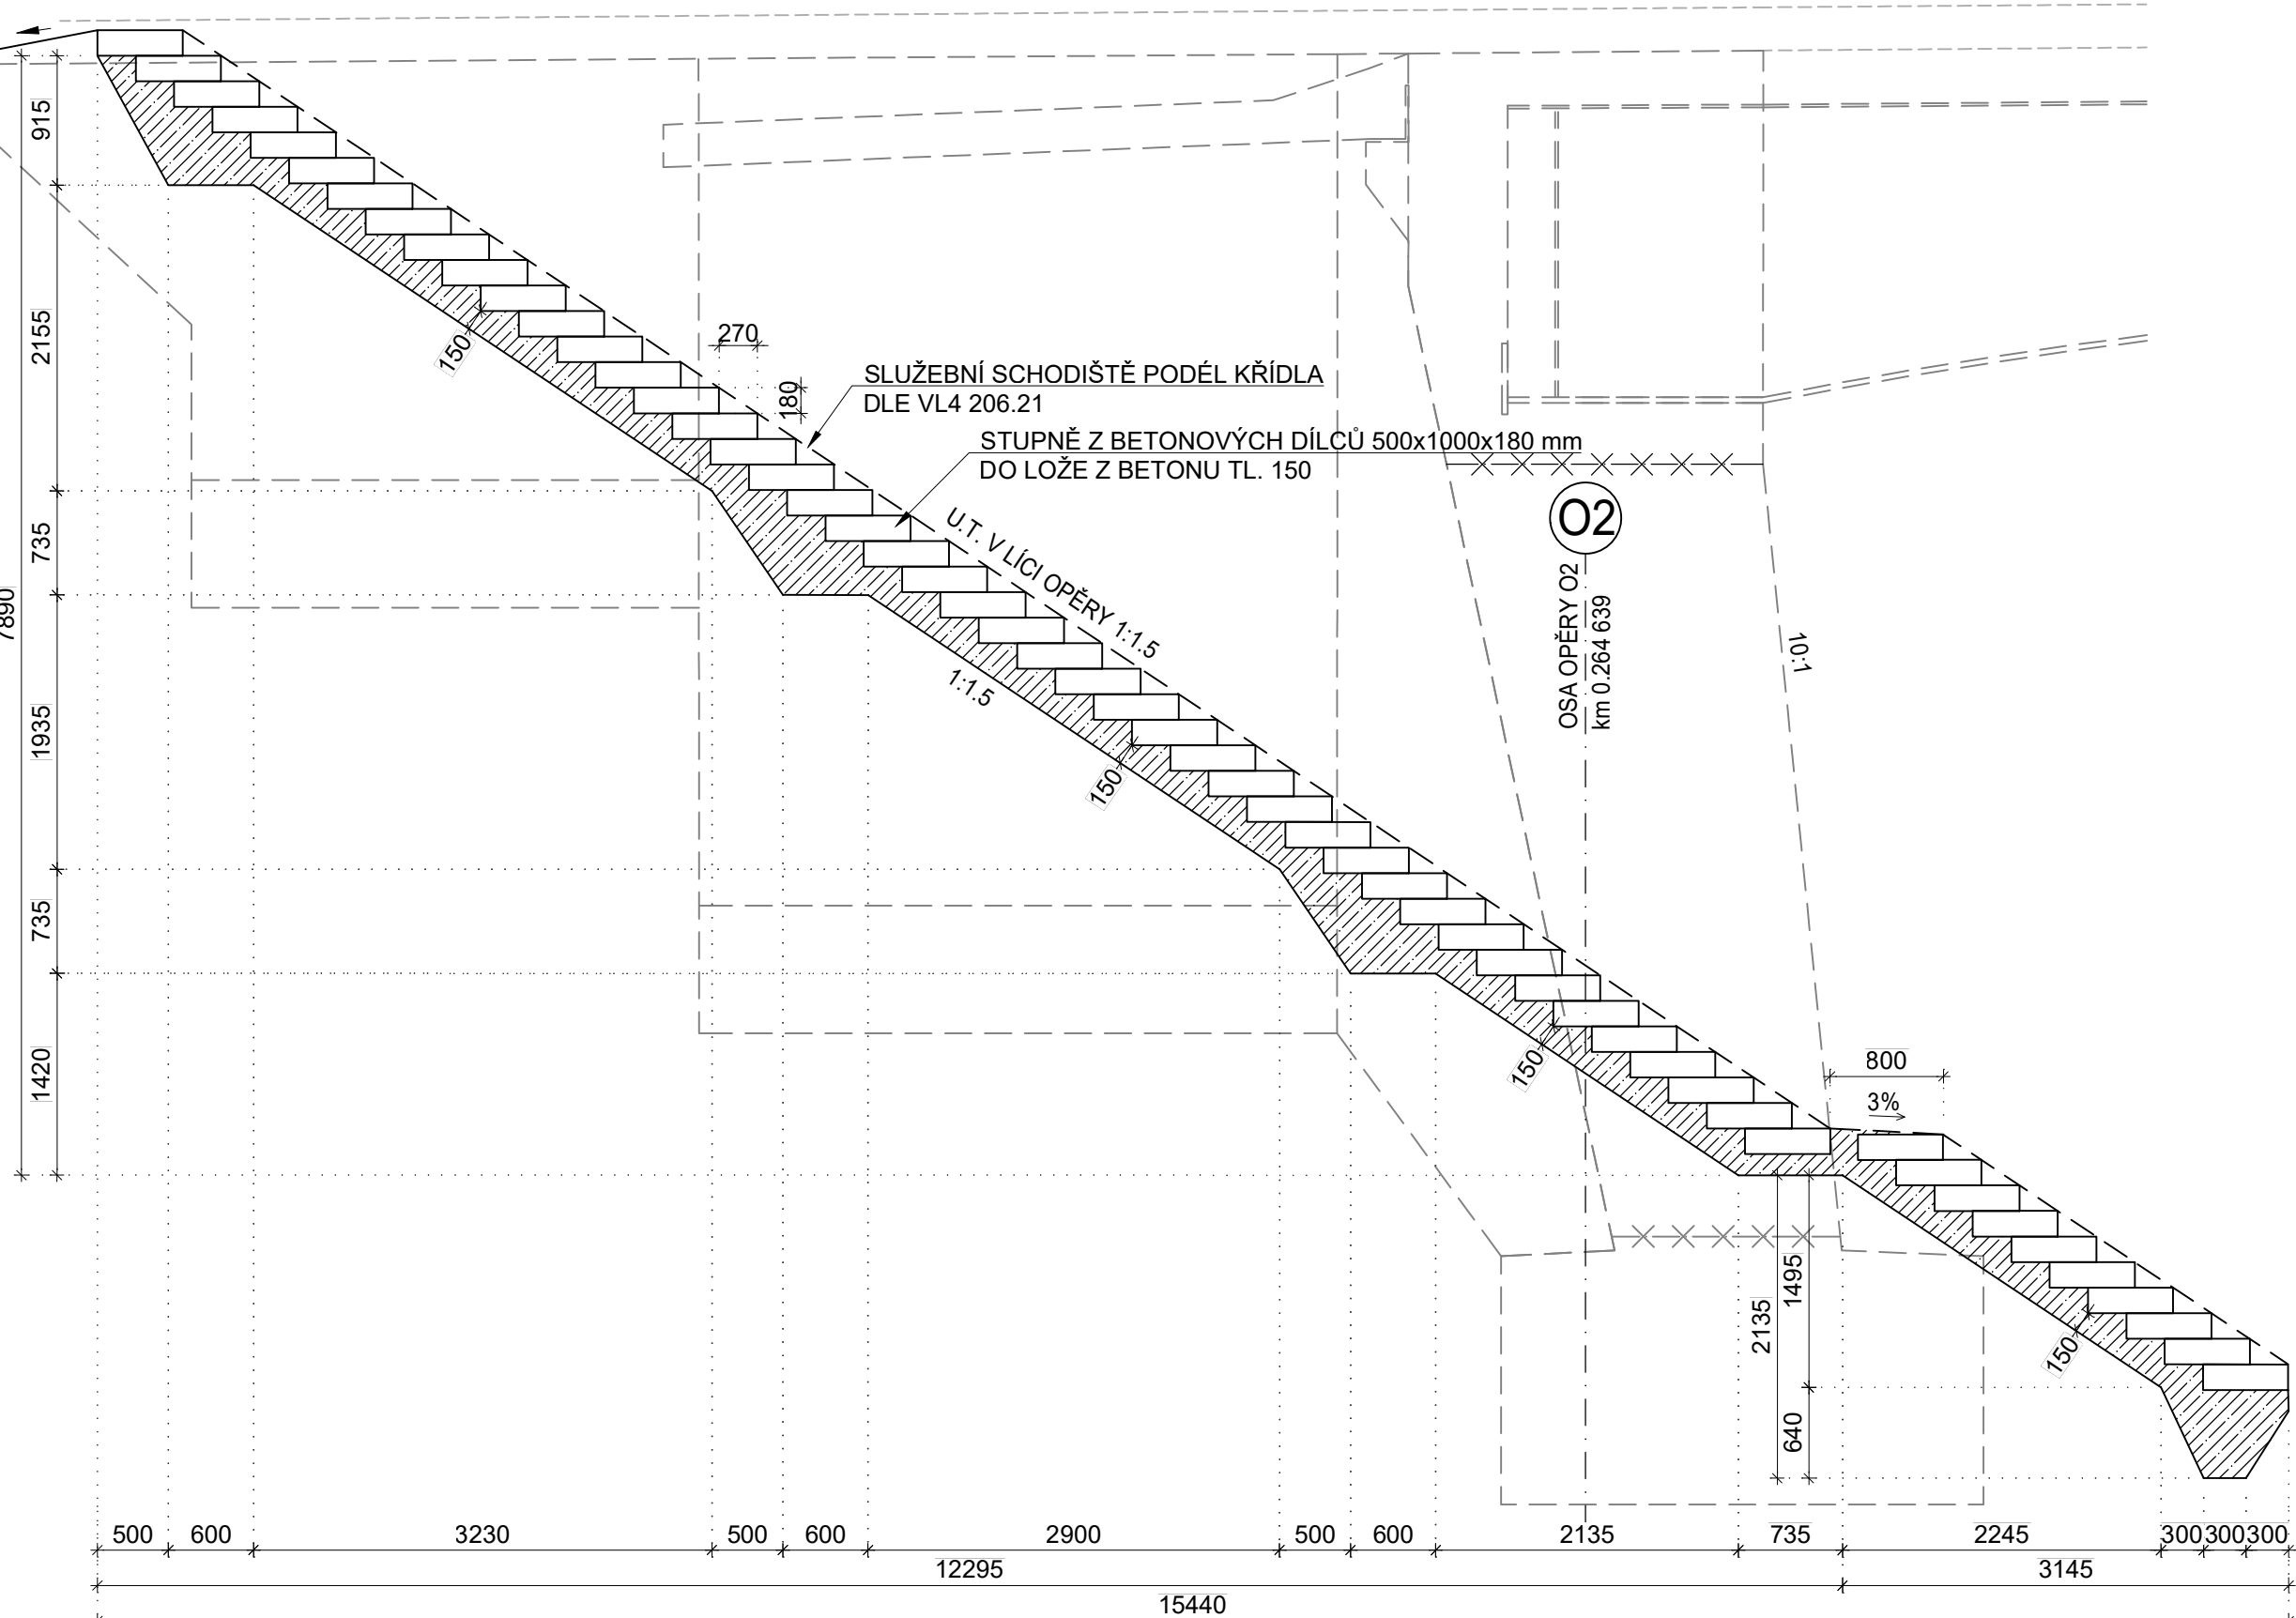

1. MATERIÁLY VIZ TECHNICKÁ ZPRÁVA
2. SCHODIŠŤOVÉ STUPNĚ BUDOU OPATŘENY STRIÁŽÍ
3. OPEVNĚNÍ A SCHODIŠŤE JSOU LEMOVÁNY BETONOVÝMI OBRUBNÍKY, OPEVNĚNÍ JE UKONČENO BETONOVÝM PRAHEM
4. POVRCH SCHODIŠŤOVÝCH STUPŇŮ BUDE ZDRSNĚN STRIÁŽÍ, ODOLNOST PROTI SKLZLNOSTI DLE ČSN 73 4130.

1. SLUŽEBNÍ SCHODIŠTĚ U OPĚRY
-DLE VL 206.21
2. ZADLAŽBA NA KONCI KŘIDLA A ROZŠÍŘENÍ NÁSYPOVÉHO TĚLESA PŘED/ZA MOSTEN
-DLE VL 206.22, 206.23
3. OPEVNĚNÍ SVAHU Z LOMOVÉHO KAMENE
-DLE VL 206.02

D.1.2

SOUŘADNICOVÝ SYSTÉM S-JTSK

Objednatel:  ŘEDITELSTVÍ SILNIC A DÁLNIC	Ředitelství silnic a dálnic s. p. Na Pančárci 546/56, 140 00 Praha 4 Stavbu zajišťuje Závod Praha Na Pančárci 546/56, 140 00 Praha 4
--	--

Správce:  SUDOP PRAHA Olišanská 1a, 130 60 Praha 3 tel.: +420 267 094 111 e-mail: praha@sudop.cz	Vedoucí týmu: ING. ROMAN PETŘÍK	Asistent vedoucího týmu: ING. PAVEL MIČEL Specialista profe: ING. PAVEL JIŘÍČEK, Ph.D.
---	--	---

Vedoucí střediska:	Odpovědný projektant SO, IO, PS:	Vypracoval:	Kontroloval:
ING. MIROSLAV KROUPAR	ING. LUDVÍK KOLPASKÝ	TOMÁŠ POKORNÝ	ING. LUDVÍK KOLPASKÝ

Název akce:	Úsebk smůvny:		22-014.250
D11 1108 Jaroměř - Trutnov VD-ZDS + TP + AD	Projektový stupeň:		VD-ZDS
Část:	Datum:		05/2024
D.1.2 MOSTNÍ OBJEKTY A ZDI	Číslo části:		D. 1.2
SO 226 NADJEZD NA PŘELOŽCE SILNICE III/30015 V KM 132,150			
Název přílohy:	Mřížka:	Počet formulí:	
	1:50, 1:100	10xA4	
	Číslo přílohy:		

15