


SO 226 NADJEZD NA PŘELOŽCE SILNICE III/30015 V KM 132,150

POHLED 1-1 : PŮDORYS
M 1:100

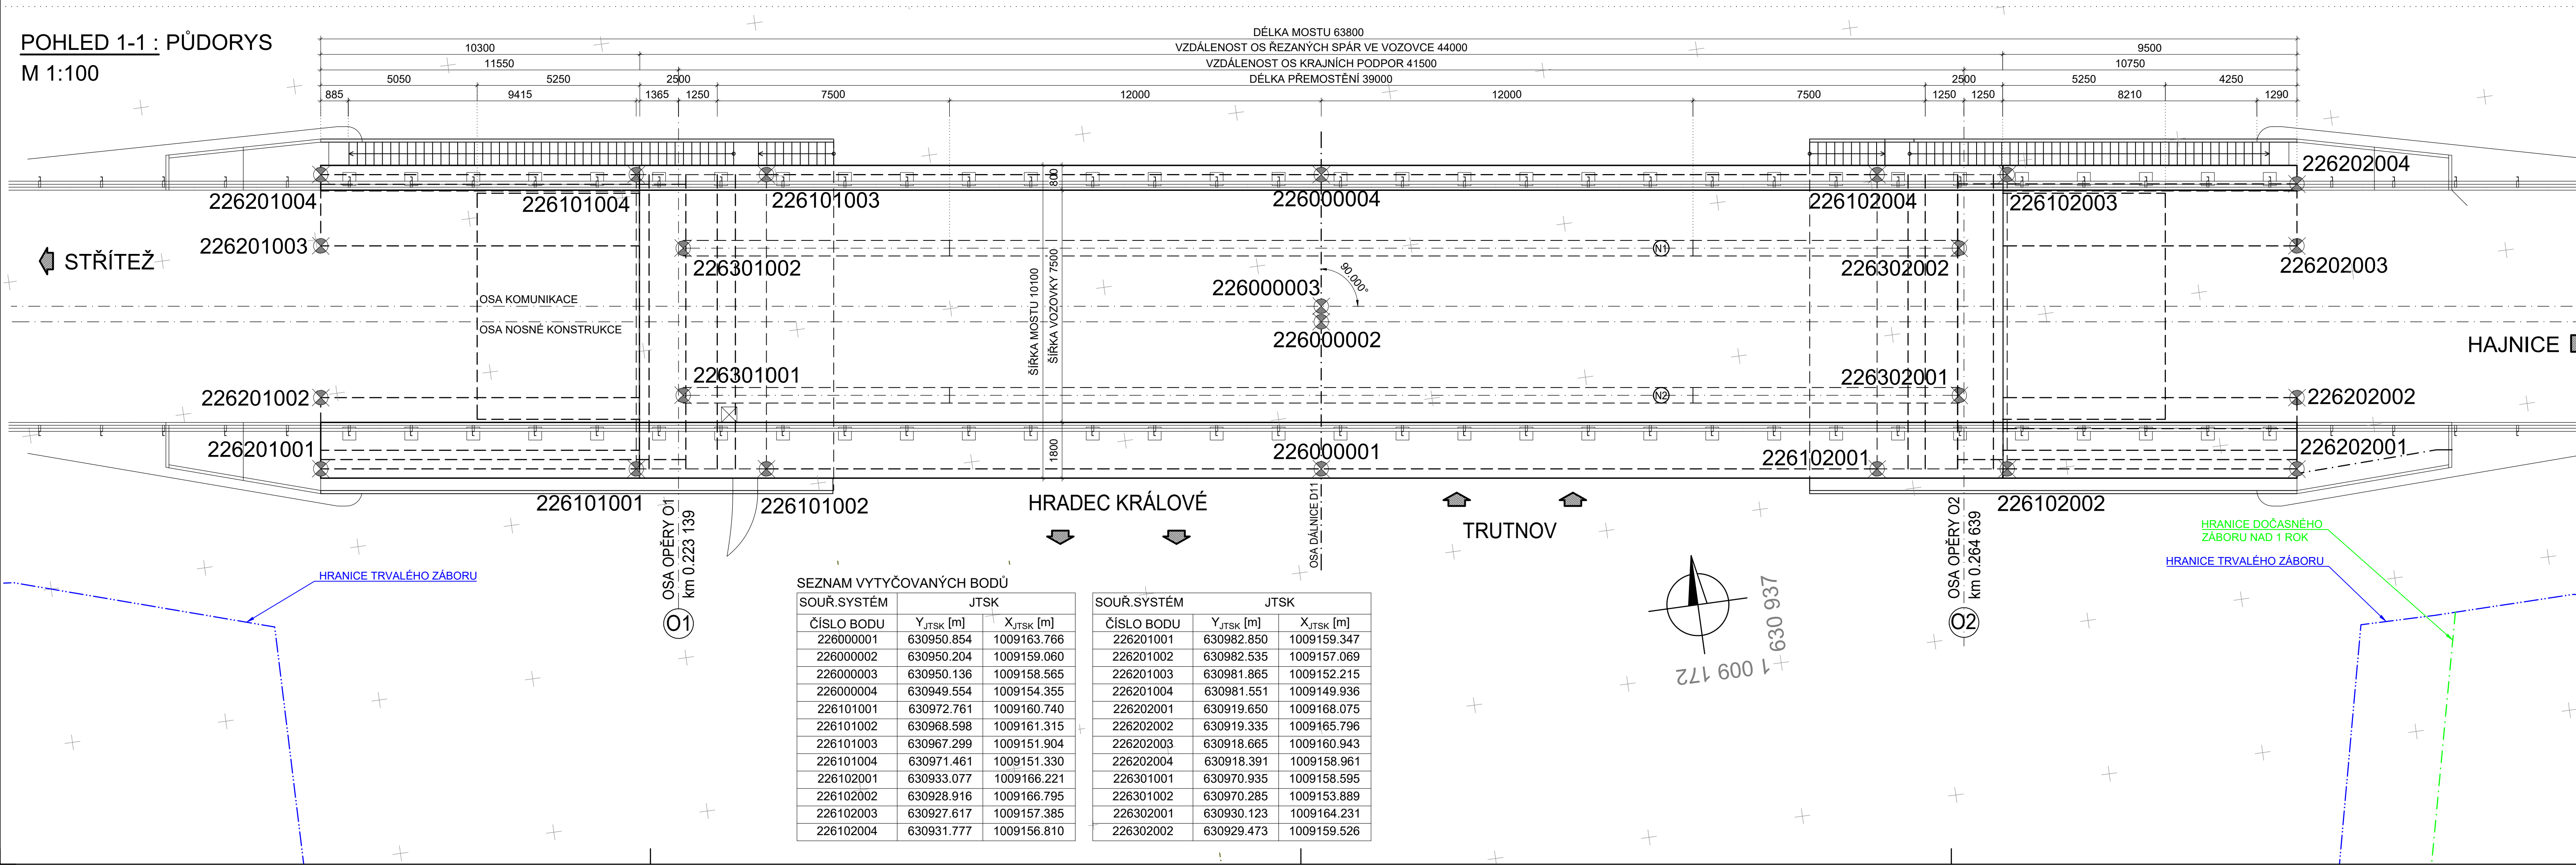

SEZNAM VYTYČOVANÝCH BODŮ

ČÍSLO BODU	JTSK	
	Y _{JTSK} [m]	X _{JTSK} [m]
226000001	630950.854	1009163.766
226000002	630950.204	1009159.060
226000003	630950.136	1009158.565
226000004	630949.554	1009154.355
226101001	630972.761	1009160.740
226101002	630968.598	1009161.315
226101003	630967.299	1009151.904
226101004	630971.461	1009151.330
226102001	630933.077	1009166.221
226102002	630928.916	1009166.795
226102003	630927.617	1009157.385
226102004	630931.777	1009156.810

ČÍSLO BODU	JTSK	
	Y _{JTSK} [m]	X _{JTSK} [m]
226201001	630982.850	1009159.347
226201002	630982.535	1009157.069
226201003	630981.865	1009152.215
226201004	630981.551	1009149.936
226202001	630919.650	1009168.075
226202002	630919.335	1009165.796
226202003	630918.665	1009160.943
226202004	630918.391	1009158.961
226301001	630970.935	1009158.595
226301002	630970.285	1009153.889
226302001	630930.123	1009164.231
226302002	630929.473	1009159.526

POZNÁMKY:

- SOUŘADNICOVÝ SYSTÉM S-JTSK; VÝŠKOVÝ SYSTÉM BpV
- VYTYČENÍ MOSTU BUDE ZE ZÁKLADNÍ VYTYČOVACÍ SÍTĚ ZŘÍZENÉ PRO STAVBU A MIKROSÍTĚ VYBUDOVANÉ ZHOTOVITELEM V PŘEDSTIHU PŘED ZAHÁJENÍM STAVEBNÍCH PRACÍ
- PRO VYTYČENÍ BUDE POUŽITA PLATNÁ A OVĚŘENÁ VYTYČOVACÍ SÍŤ
- NORMAMI ČSN 73 0420-1 A ČSN 73 0420-2
- PŘEDPISY TKP KAPITOLA 1, PŘÍLOHA Č. 9 (OBECNÉ), DÁLE TKP KAPITOLA 16, 18 A DALŠÍ SOUVISEJÍCÍ
- 226ABBCCC (SEZNAM BODŮ), ABBCCC (VÝKRES):
A - ČÁST (0 - OSA KOMUNIKACE, 1 - ZALOŽENÍ, 2 - SPODNÍ STAVBA, 3 - NOSNÁ KONSTRUKCE)
BB - ČÍSLO SPODNÍ STAVBY (01 - OPĚRA 01, 02 - PILÍŘ 02,...)
CCC - ČÍSLO BODU
- VÝŠKOVÁ POLOHA BODŮ:
000001,...,000004 - NIVELETA DÁLNIČE
101001,...,101004 102001,...,102004 - DOLNÍ POVRCH ZALOŽENÍ
201001,...,201004 202001,...,202004 - HORNÍ POVRCH KŘÍDLA
301001,...,301004 302001,...,302004 - ULOŽENÍ NOSNÍKŮ - DOLNÍ POVRCH SPODNÍ PÁSNIČE

Mezní vytyčovací odchylky vytyčení vzájemné prostorové polohy CHB osy mostu a HVB mostu [mm]				
Druh nosné konstrukce mostu	mezní vytyčovací odchylka δx_m vodorovné vzdálenosti d sousedních CHB osy mostu			mezní vytyčovací výšková odchylka (sousedních HVB) δx_m
	d ≤ 50m	50m < d ≤ 150m	150m < d ≤ 300m	d > 300m
ocelová	±30	±40	±50	±80
betonová monolitická na skruži nebo letmo betonovaná	±30	±50	±60	±100
betonová prefabrikovaná včetně letmo montovaných	±20	±40	±60	±100

Mezní vytyčovací odchylky vytyčení podrobných bodů mostu z CHB a z HVB mostu			
Stavební etapa	Mezní vytyčovací odchylka δx_m		
	podélná	příčná	výšková
zemní práce	±100	±100	±50
zemní konstrukce	±70	±50	±30
spodní stavby	±30	±20	±15
nosná konstrukce	±20	±15	±10
svršek mostu	±15	±10	±4

Mezi mezní vytyčovací odchylkou δ_{xm} a směrodatnou vytyčovací odchylkou σ platí vztah $\delta_{xm} = 2\sigma$

Mezní vytyčovací odchylky vytyčení přemostění		
Přemostovaná liniová stavba	Mezní vytyčovací podélná odchylka δx_m	
	dráha, pozemní komunikace	ostatní
	± 40 mm	± 60 mm

Poznámka: mezní podélné vytyč. odchylky CHB osy mostu, měřené na mostě vzhledem k ose přemostované stavby.

Mezní vytyčovací odchylka δx_m vzájemné polohy CHB a HVB mostu a HB a HVB liniové stavby		
podélná	příčná	výšková
±20 [mm]	±15 [mm]	±4 [mm]

Poznámka: uvedená kritéria se použijí, pokud poloha CHB osy mostu není totožná s HB liniové stavby (obdobně u výškové složky).

VYTYČOVACÍ VÝKRES

SO 226
D.1.2

VÝŠKOVÝ SYSTÉM BpV SOUŘADNICOVÝ SYSTÉM S-JTSK

Číslo změny:	Obsah změny:	Datum změny:
01	-	-
02	-	-
03	-	-

Objednatel:

Ředitelství silnic a dálnic s. p.
Na Pankráci 546/56, 140 00 Praha 4

Stavbu zajišťuje Závod Praha
Na Pankráci 546/56, 140 00 Praha 4

Zhotovitel: Společníci ve sdružení SG_Velké projekty_BIM 2020 zastoupené

SUDOP PRAHA a.s.
Hlavní inženýr projektu: Ing. Roman Petřík

Olšanská 1a, 130 80 Praha 3
telefon: +420 267 094 111

Správce:

SUDOP PRAHA a.s.
Olšanská 1a, 130 80 Praha 3
tel.: +420 267 094 111
e-mail: praha@sudop.cz

Vedoucí týmu:
ING. ROMAN PETŘÍK

Asistent vedoucího týmu:
ING. PAVEL MICHL
Specialista profese:
ING. PAVEL JIŘÍČEK, PH.D.

Zpracovatel částí:

projektová, průzkumná a konzultační společnost
PUDIS a.s., Podbabská 1014/20, 160 00 Praha 6
tel.: +420 267 004 111, www.pudis.cz, info@pudis.cz

Vedoucí střediska:
ING. MIROSLAV KROUPAR

Odpovědný projektant SO, IO, PS:
ING. LUDVÍK KOLPASKÝ

Vypracoval:
TOMÁŠ POKORNÝ

Kontroloval:
ING. LUDVÍK KOLPASKÝ

Název akce:
D11 1108 Jaroměř - Trutnov VD-ZDS + TP + AD

Číslo smlouvy:
22-014.250

Projektový stupeň:
VD-ZDS

Část:
D.1.2 MOSTNÍ OBJEKTY A ZDI
SO 226 NADJEZD NA PŘELOŽCE SILNICE III/30015 V KM 132,150

Datum:
11/2024

Číslo části:
D.1.2

Název přílohy:
VYTYČOVACÍ VÝKRES

Měřítko:
1:100

Počet formátů:
6xA4

Číslo přílohy:
16