


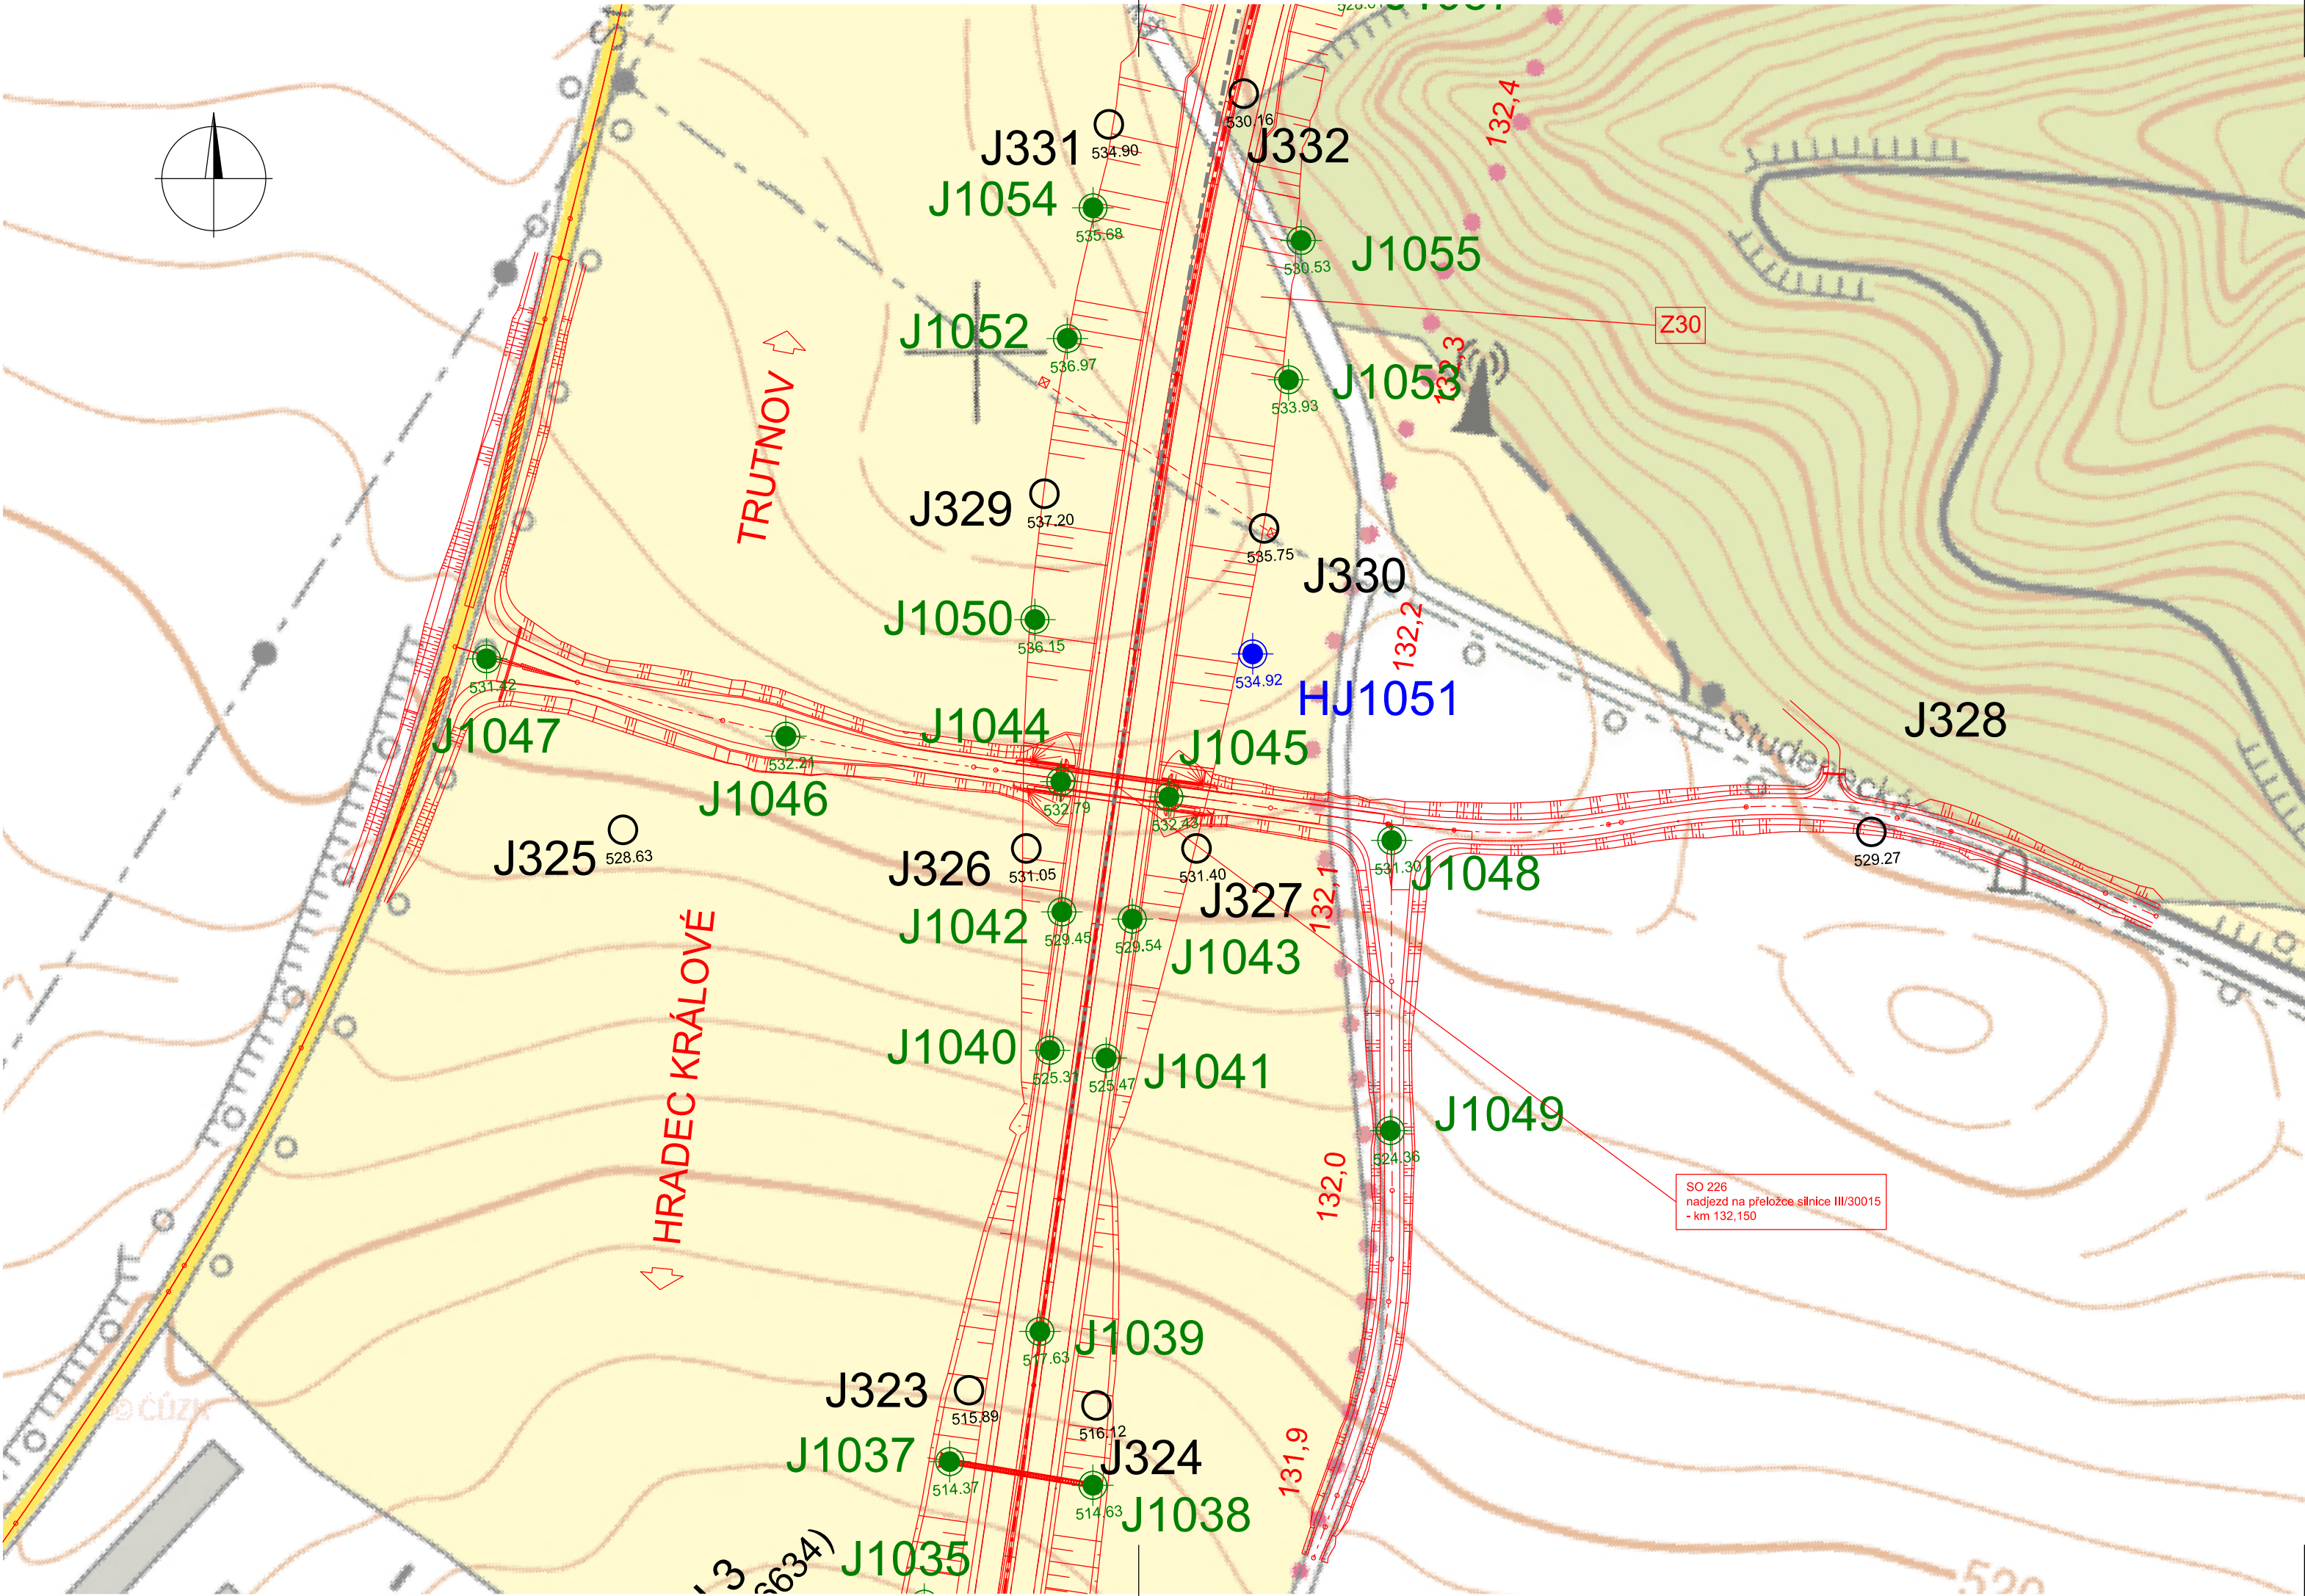

LEGENDA - PRÁCE PROVEDENÉ V RÁMCI PODROBNÉHO GTP:

- J526 jádrový IG vrt
- PJ524 jádrový vrt s presiomrickými zkouškami
- HJ540 jádrový hydrogeologický vrt
- SP520 statická penetrační zkouška (CPT)
- DP593 dynamická penetrační zkouška
- linie geotechnického profilu (výpočty)
- linie geofyzikálního profilu

ARCHIVNÍ GEOLOGICKÉ PRÁCE:

- J2 vrt provedený v rámci předběžného GTP
- CH-5 archivní sonda nesouvisející se stavbou dálnice (FZ 5525) (číslo posudku - klíč ČGS - Geofond)
- DP29 dynamická penetrace v rámci předběžného GTP
- geofyzikální profil v rámci předběžného GTP
- geotechnický profil v rámci předběžného GTP

Investor:
Ředitelství silnic a dálnic ČR
Správa Hradec Králové
Pouchovská 401
503 41 Hradec Králové



Zhotovitel: Společnost A - P GTP D11 1108

AZCONSULT spol s.r.o.



Vypracoval:

Erik Tomášek

Kontroloval:

Mgr. J. Šindelář

Odpovědný řešitel:

Mgr. J. Šindelář

Schválil:

Ing. Martina Štrosová

Číslo zakázky:
18/037

Datum:
11/2019

Zhotovitel částí:

AZCONSULT spol s.r.o.

Klíšská 1334/12, 400 01 Ústí nad Labem
tel. 475 240 888
www.azconsult.cz

Akce:

D11 1108 Jaroměř - Trutnov, podrobný geotechnický průzkum

Příloha:

Situace provedených sond pro SO 226

Měřítko:

1:2000

Formát:

3 x A4

Stupeň:

DSP

Souprava:

Číslo přílohy:

C24.1