



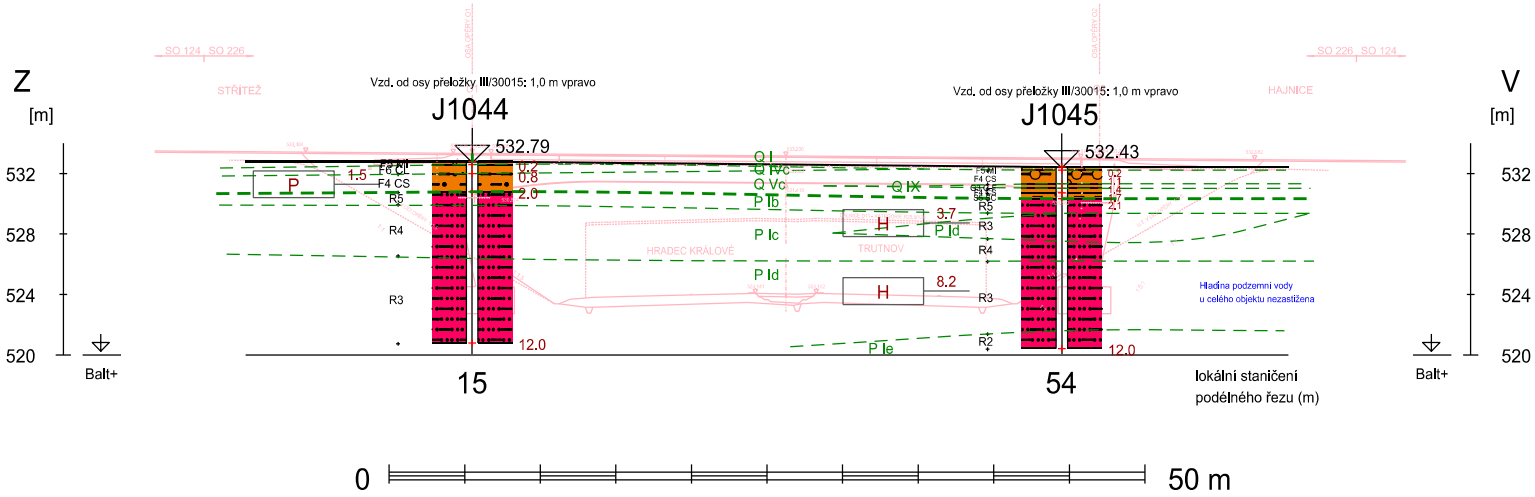

Geotechnické typy zemín			
označení	popis	konzistence, ulehlost	ČSN 73 6133
kvartér			
Q I	hlína organická, ornice, lesní hrabanka	-	F5 MI, F3 MS
Q II a	hlína sprašová	měkká	F6 CI, F6 CL, F8 CH
b	hlína sprašová	tuhá	F6 CI, F6 CL, F8 CH
c	hlína sprašová	pevná až tvrdá	F6 CI, F6 CL, F8 CH
Q III a	hlína, jíl s vysokou až velmi vysokou plasticitou	měkká	F7 MH, F8 CH, F7 MV, F8 CV
b	hlína, jíl s vysokou až velmi vysokou plasticitou	tuhá	F7 MH, F8 CH, F7 MV, F8 CV
c	hlína, jíl s vysokou až velmi vysokou plasticitou	pevná až tvrdá	F7 MH, F8 CH, F7 MV, F8 CV
Q IV a	hlína, jíl se střední plasticitou	měkká	F5 MI, F6 CI, F6 CL
b	hlína, jíl se střední plasticitou	tuhá	F5 MI, F6 CI, F6 CL
c	hlína, jíl se střední plasticitou	pevná až tvrdá	F5 MI, F6 CI, F6 CL
Q V a	hlína písčitá, jíl písčité	měkká	F3 MS, F4 CS
b	hlína písčitá, jíl písčité	tuhá	F3 MS, F4 CS
c	hlína písčitá, jíl písčité	pevná až tvrdá	F3 MS, F4 CS
Q VI a	hlína štěrkovitá, jíl štěrkovitý	měkká	F1 MG, F2 CG
b	hlína štěrkovitá, jíl štěrkovitý	tuhá	F1 MG, F2 CG
c	hlína štěrkovitá, jíl štěrkovitý	pevná až tvrdá	F1 MG, F2 CG
Q VII a	písek hlinitý, písek jílovitý	kyprý	S4 SM, S5 SC
b	písek hlinitý, písek jílovitý	středně ulehlý až ulehlý	S4 SM, S5 SC
Q VIII a	písek s příměsí jemnozrnné zeminy	kyprý	S3 S-F
b	písek s příměsí jemnozrnné zeminy	středně ulehlý až ulehlý	S3 S-F
Q IX	štěrk hlinitý, štěrk jílovitý	-	G4 GM, G5 GC
QX	štěrk s příměsí jemnozrnné zeminy	-	G3 G-F
křída			
K I	jíl písčité	tuhý až pevný	F4 CS
K II	písek jílovitý	ulehlý	S5 SC
K III a	prachovec vápnitý zcela zvětralý		R6
b	prachovec vápnitý silně zvětralý		R5
c	prachovec vápnitý mírně zvětralý		R4
d	prachovec vápnitý navětralý až zdravý		R3-R2
K IV a	eluvium pískovce		R6
b	pískovec zcela zvětralý		R5
c	pískovec silně zvětralý		R4
d	pískovec mírně zvětralý		R3
e	pískovec navětralý až zdravý		R3-R2; R2
K V a	slínovec zcela zvětralý		R6
b	slínovec silně zvětralý		R5
c	slínovec mírně zvětralý		R4
d	slínovec navětralý až zdravý		R4-R3; R3
perm			
P I a	eluvium prachovce až jílovitého pískovce		R6
b	jílovitý pískovec až prachovec zcela zvětralý		R5
c	jílovitý pískovec až prachovec silně zvětralý		R4
d	jílovitý pískovec až prachovec mírně zvětralý		R3
e	jílovitý pískovec až prachovec navětralý až zdravý		R3-R2
P II a	slepenec zcela zvětralý		R5
b	slepenec silně zvětralý		R4
c	slepenec mírně zvětralý až navětralý		R3
d	slepenec zdravý		R2

LEGENDA

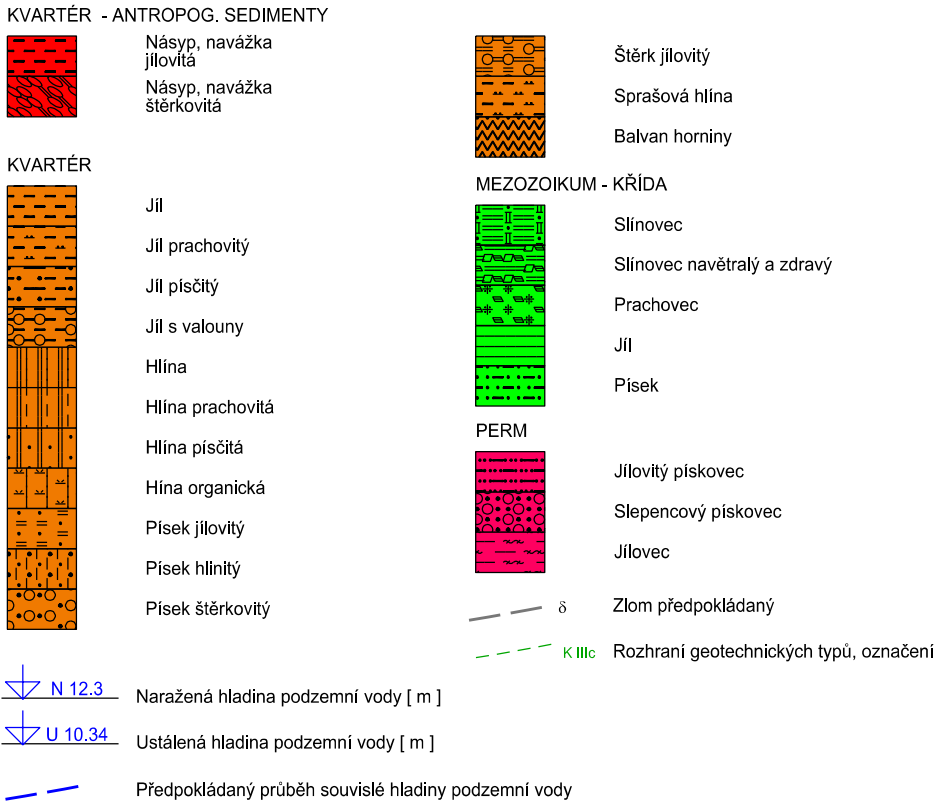

Investor:

Ředitelství silnic a dálnic ČR
Správa Hradec Králové
Pouchovská 401
503 41 Hradec Králové



ŘEDITELSTVÍ SILNIC A DÁLNIC ČR

Zhotovitel:

Společnost A - P GTP D11 1108



Vypracoval: V. Šimová	Kontroloval: Mgr. J. Šindelář	Zhotovitel částí:
Odpovědný řešitel: Mgr. J. Šindelář	Schválil: Ing. Martina Štrosová	
Číslo zakázky: 18/037	Datum: 11/2019	Klíšská 1334/12, 400 01 Ústí nad Labem tel. 475 240 888 www.azconsult.cz

Akce:	Měřítko: 1:500	Formát: 3 x A4
D11 1108 Jaroměř - Trutnov, podrobný geotechnický průzkum	Stupeň: DSP	Souprava:
Příloha:	Číslo přílohy:	
SO 226, podélný geologický řez	C24.2	