


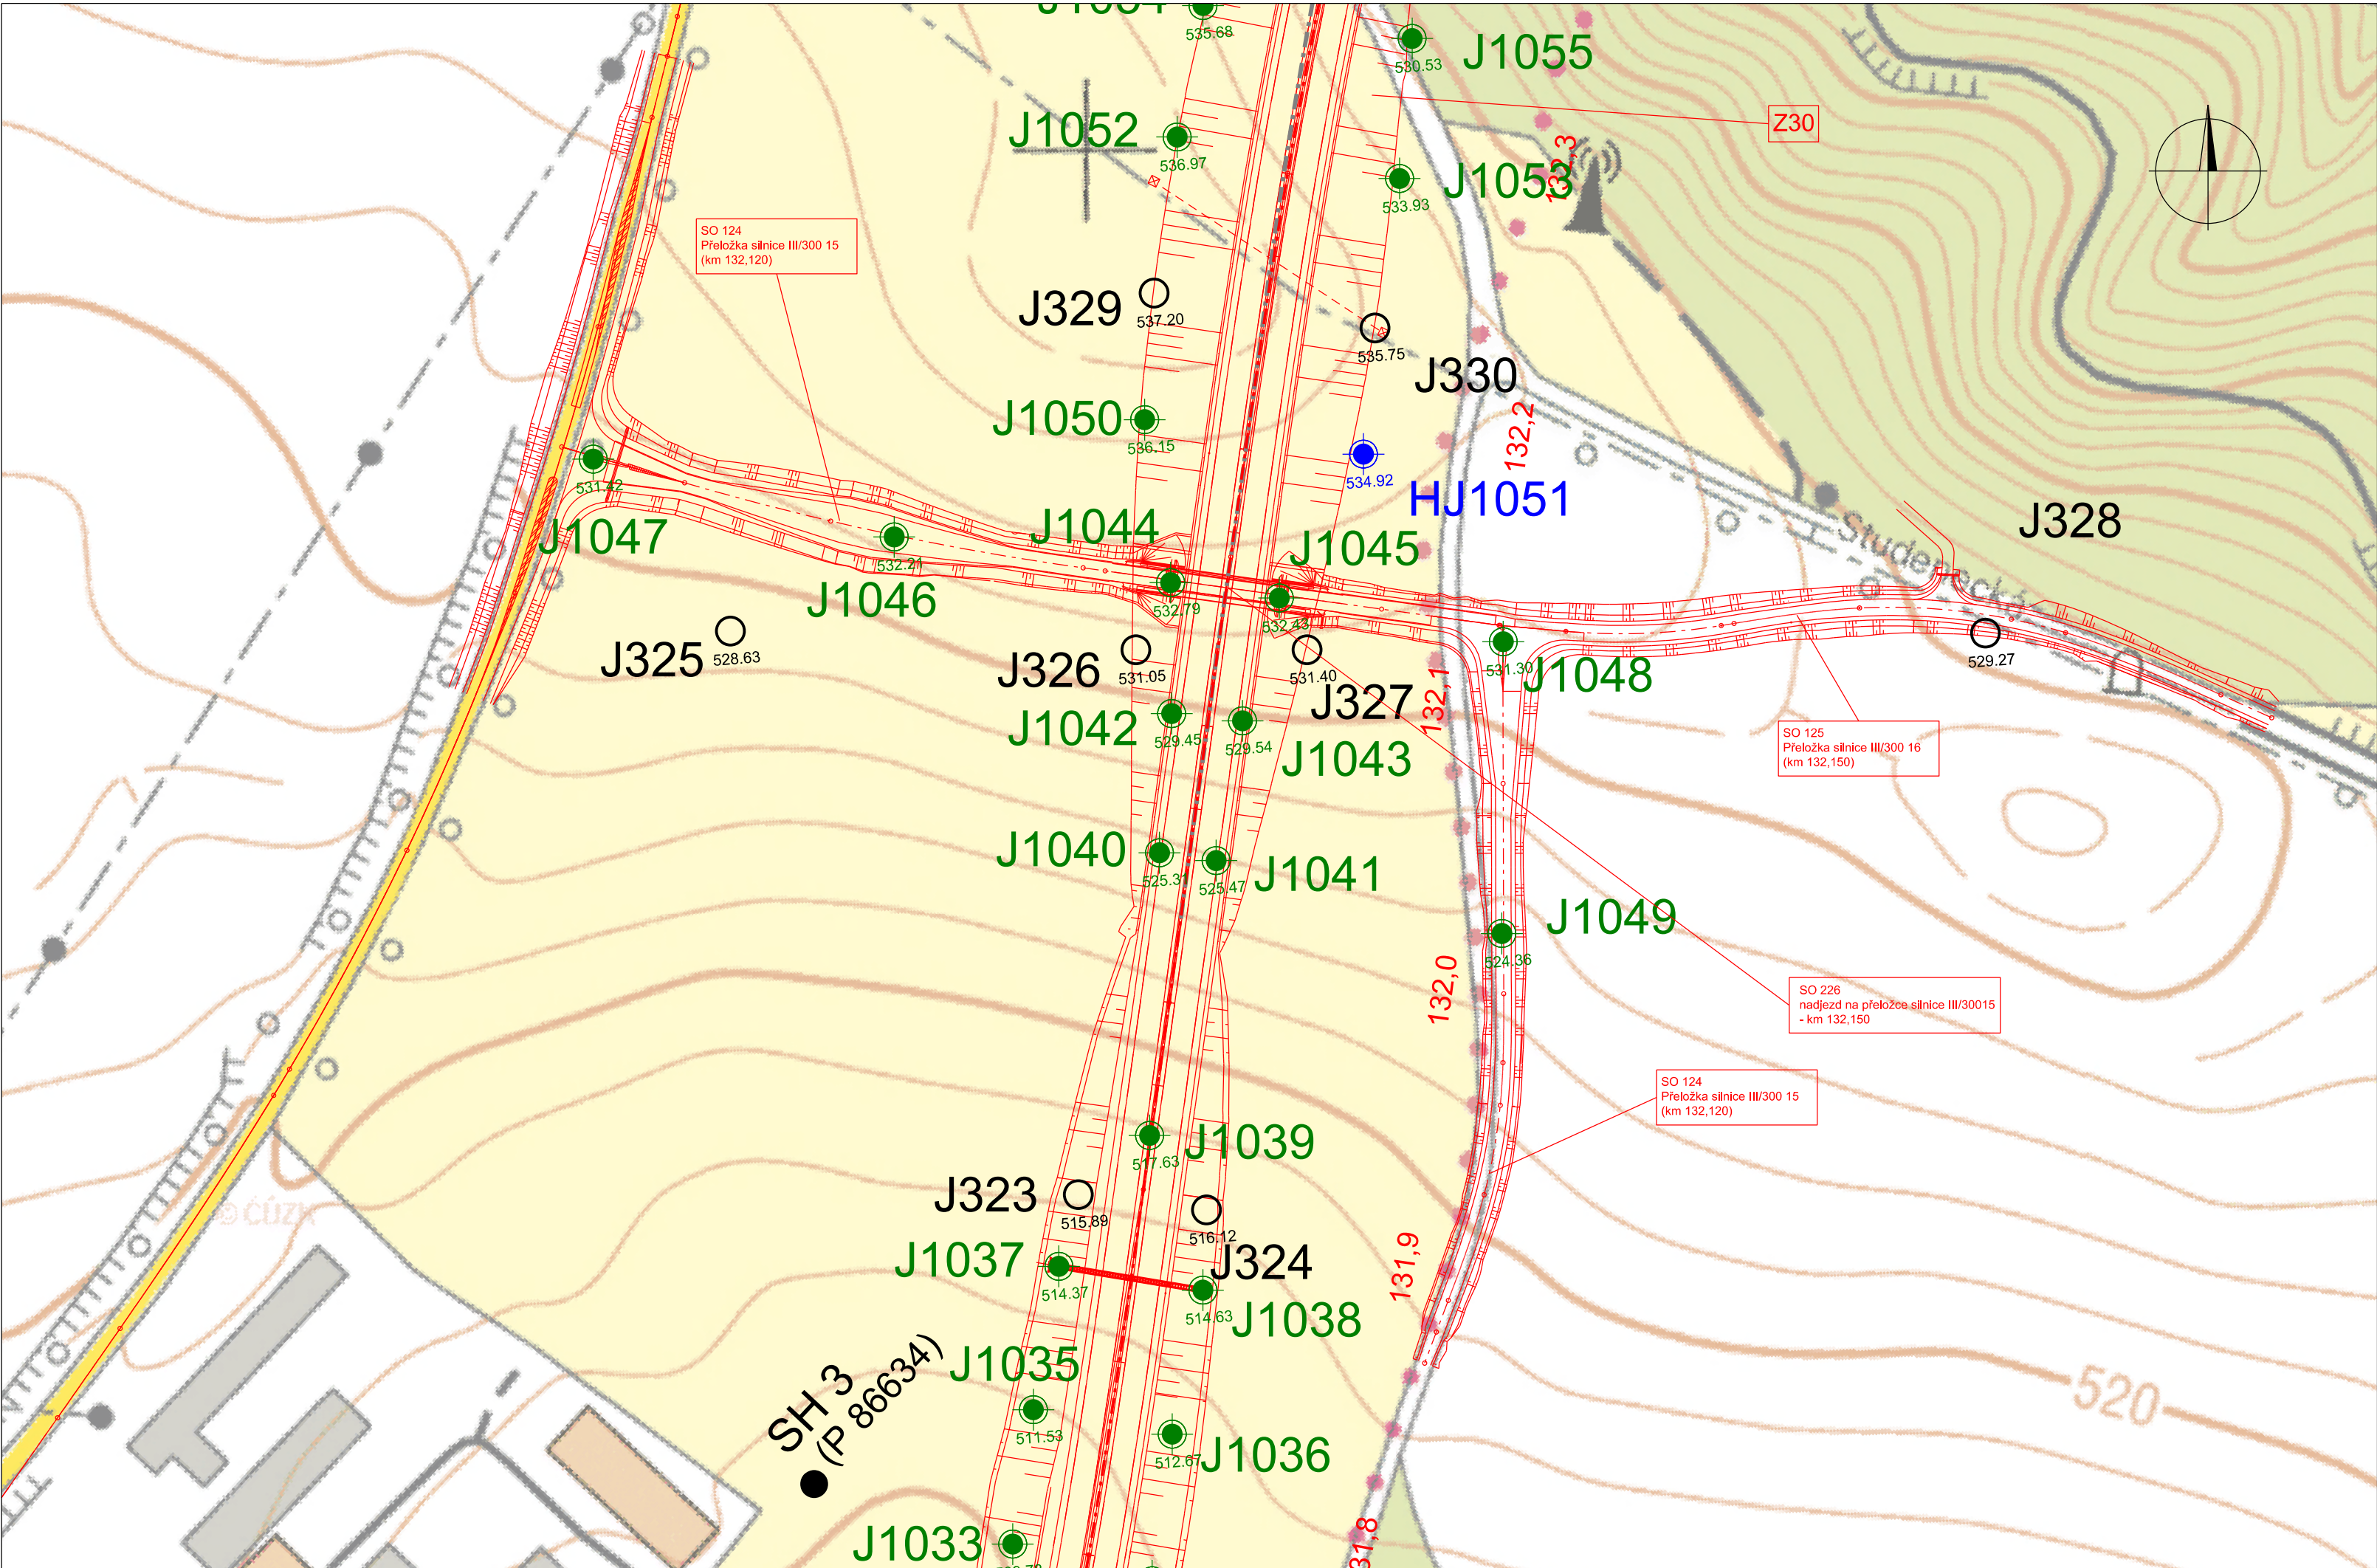

LEGENDA - PRÁCE PROVEDENÉ V RÁMCI PODROBNÉHO GTP:

- J526 jádrový IG vrt
- PJ524 jádrový vrt s presiometrickými zkouškami
- HJ540 jádrový hydrogeologický vrt
- SP520 statická penetrační zkouška (CPT)
- DP593 dynamická penetrační zkouška
- geotechnický profil (výpočty)
- - - linie geofyzikálního profilu

ARCHIVNÍ GEOLOGICKÉ PRÁCE:

- J2 vrt provedený v rámci předběžného GTP
- CH-5 (FZ 5525) archivní sonda nesouvisející se stavbou dálnice (číslo posudku - klíč ČGS - Geofond)
- DP29 dynamická penetrace v rámci předběžného GTP
- - - geofyzikální profil v rámci předběžného GTP
- geotechnický profil v rámci předběžného GTP

Investor:

Ředitelství silnic a dálnic ČR  
Správa Hradec Králové  
Pouchovská 401  
503 41 Hradec Králové



ŘEDITELSTVÍ SILNIC A DÁLNIC ČR

Zhotovitel:

Společnost A - P GTP D11 1108



|                                        |                                    |                                                                                       |
|----------------------------------------|------------------------------------|---------------------------------------------------------------------------------------|
| Vypracoval:<br>Erik Tomášek            | Kontroloval:<br>Mgr. J. Šindelář   | Zhotovitel částí:                                                                     |
| Odpovědný řešitel:<br>Mgr. J. Šindelář | Schválil:<br>Ing. Martina Štrosová |  |
| Číslo zakázky:<br>18/037               | Datum:<br>11/2019                  | Klíšská 1334/12, 400 01 Ústí nad Labem<br>tel. 475 240 888<br>www.azconsult.cz        |

|                                                                |                |           |
|----------------------------------------------------------------|----------------|-----------|
| Akce:                                                          | Měřítko:       | Formát:   |
| D11 1108 Jaroměř - Trutnov, podrobný geotechnický průzkum      | 1:2000         | 3 x A4    |
|                                                                | Stupeň:        | Souprava: |
|                                                                | DSP            |           |
| Příloha:                                                       | Číslo přílohy: |           |
| Situace provedených sond<br>SO 124 Přeložka silnice III/300 15 | E09.1          |           |