


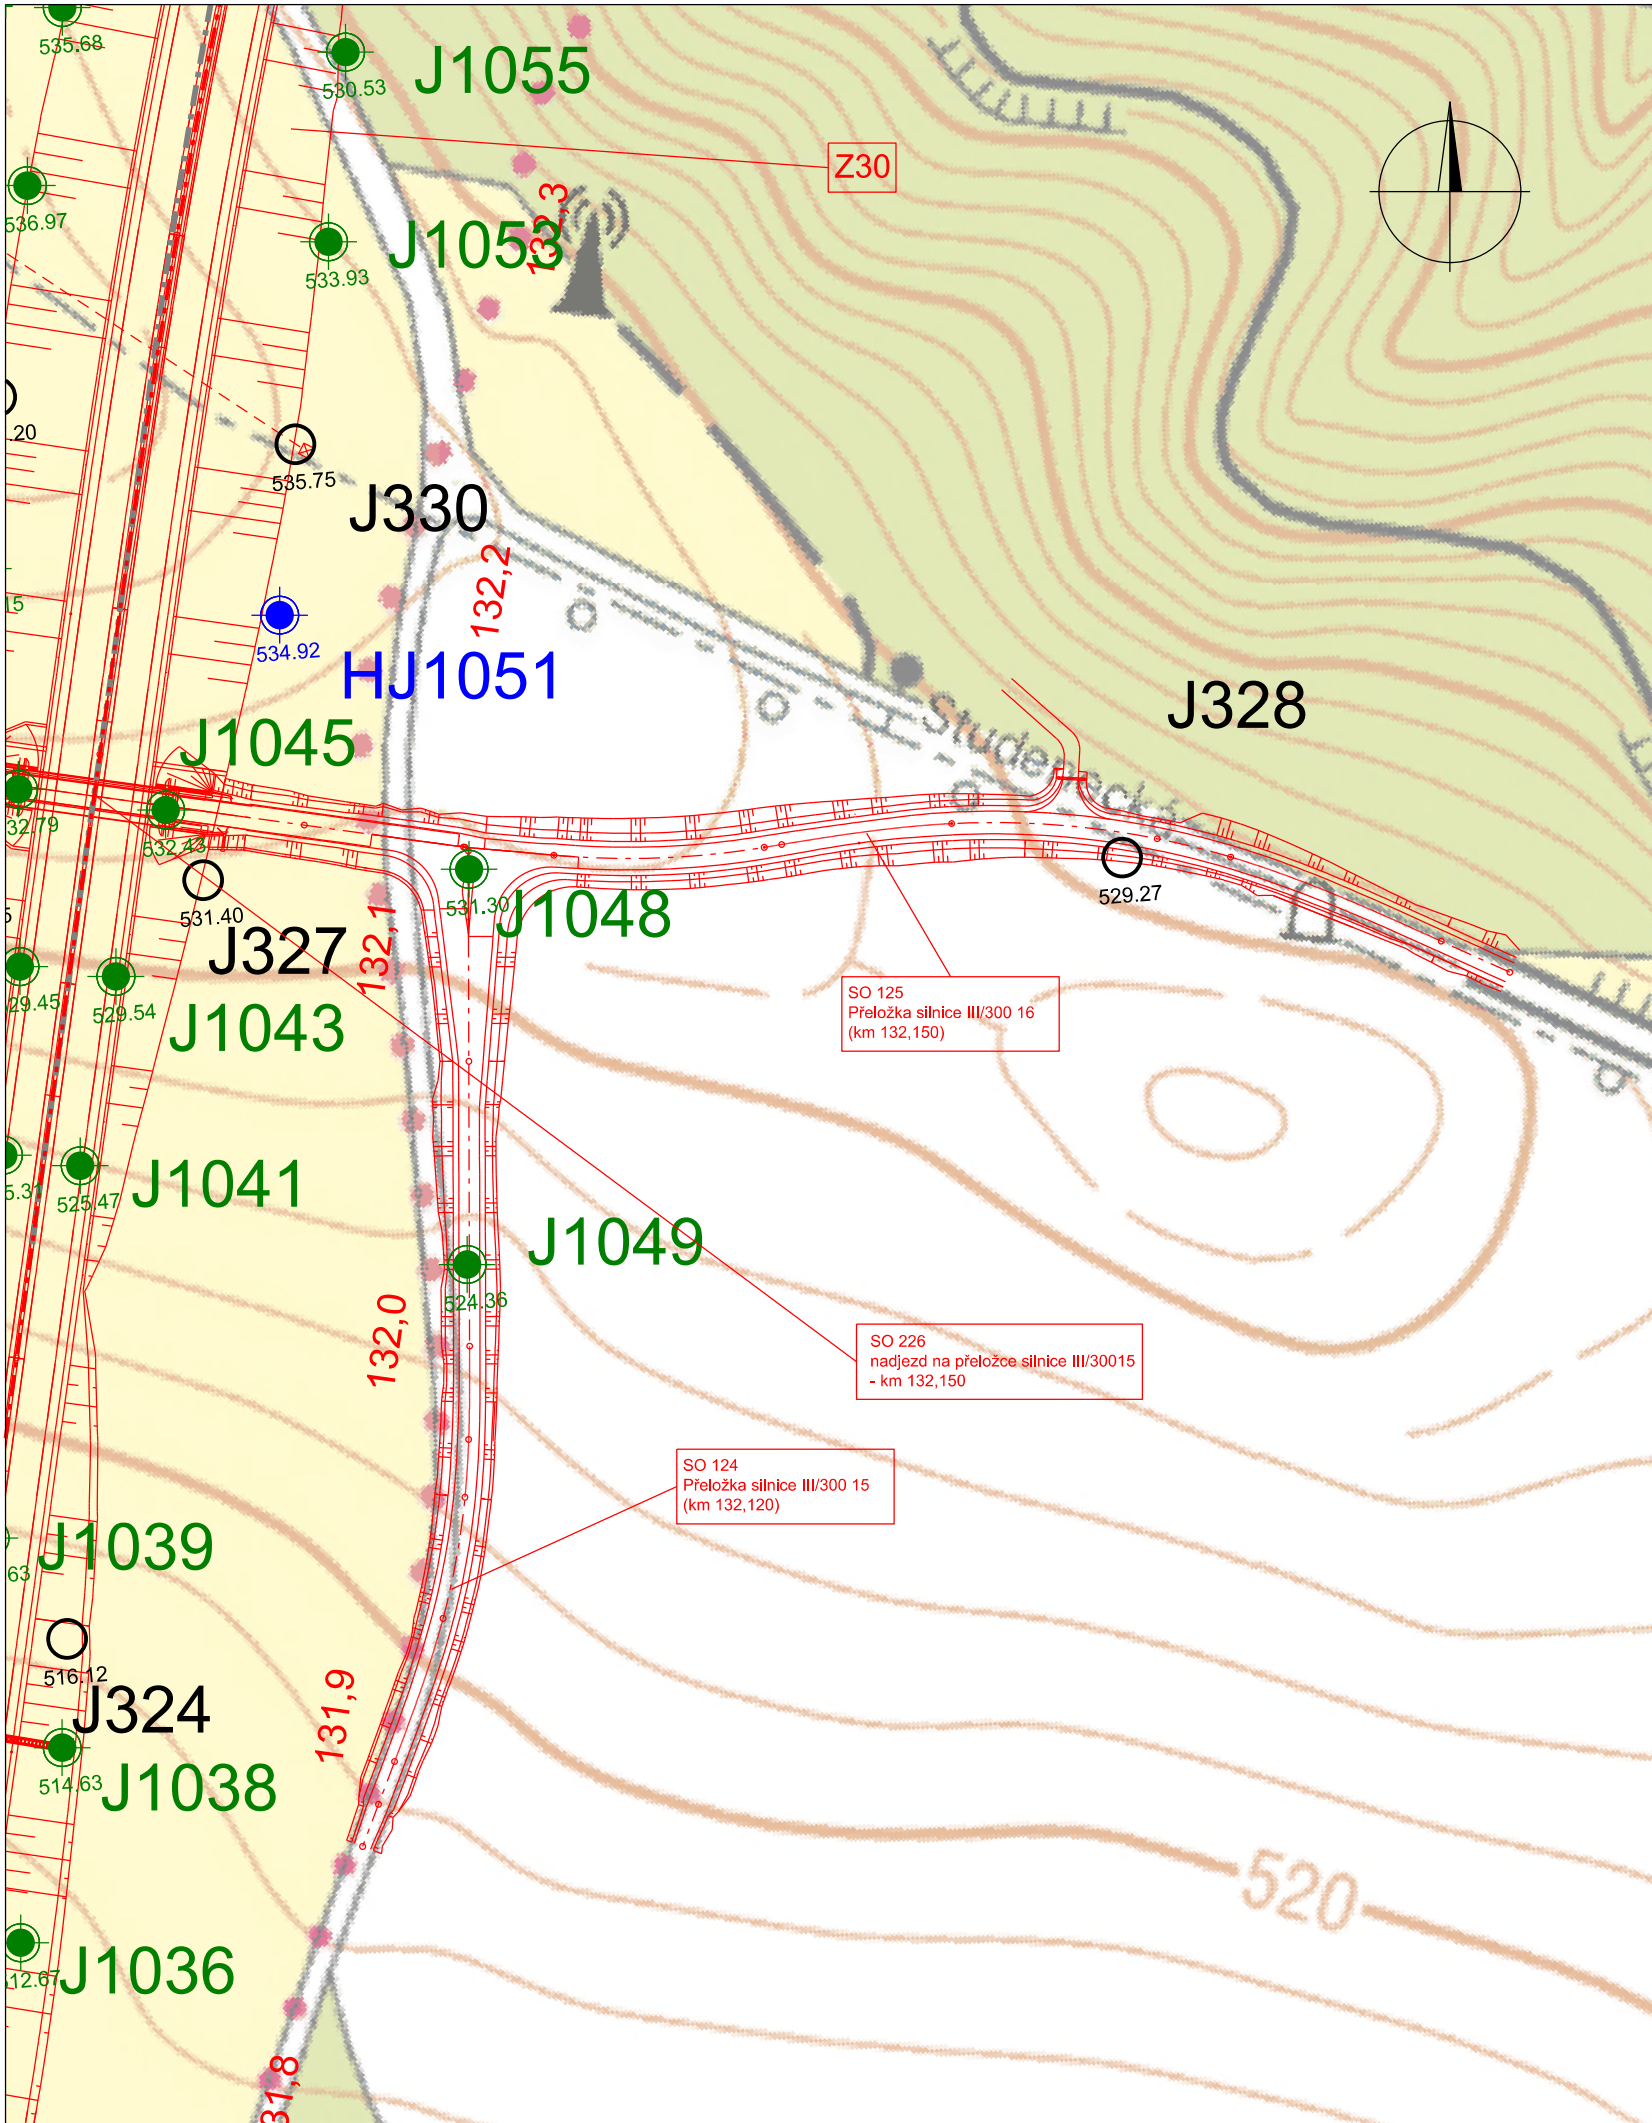

LEGENDA - PRÁCE PROVEDENÉ V RÁMCI PODROBNÉHO GTP:

- J526 jádrový IG vrt
- PJ524 jádrový vrt s presiometrickými zkouškami
- HJ540 jádrový hydrogeologický vrt
- SP520 statická penetrační zkouška (CPT)
- DP593 dynamická penetrační zkouška
- — — — — linie geotechnického profilu (výpočty)
- — — — — linie geofyzikálního profilu

ARCHIVNÍ GEOLOGICKÉ PRÁCE:

- J2 vrt provedený v rámci předběžného GTP
- CH-5 archivní sonda nesouvisející se stavbou dálnice (FZ 5525) (číslo posudku - klíč ČGS - Geofond)
- DP29 dynamická penetrace v rámci předběžného GTP
- — — — — geofyzikální profil v rámci předběžného GTP
- — — — — geotechnický profil v rámci předběžného GTP

Investor:

Ředitelství silnic a dálnic ČR
Správa Hradec Králové
Pouchovská 401
503 41 Hradec Králové



ŘEDITELSTVÍ SILNIC A DÁLNIC ČR

Zhotovitel:

Společnost A - P GTP D11 1108



Vypracoval: Erik Tomášek	Kontroloval: Mgr. J. Šindelář	Zhotovitel částí:
Odpovědný řešitel: Mgr. J. Šindelář	Schválil: Ing. Martina Štrosová	
Číslo zakázky: 18/037	Datum: 11/2019	Klišská 1334/12, 400 01 Ústí nad Labem tel. 475 240 888 www.azconsult.cz

Akce:	Měřítko:	Formát:
D11 1108 Jaroměř - Trutnov, podrobný geotechnický průzkum	1:2000	2 x A4
	Stupeň: DSP	Souprava:
Příloha: Situace provedených sond SO 125 Přeložka silnice III/300 16	Číslo přílohy:	E10.1