


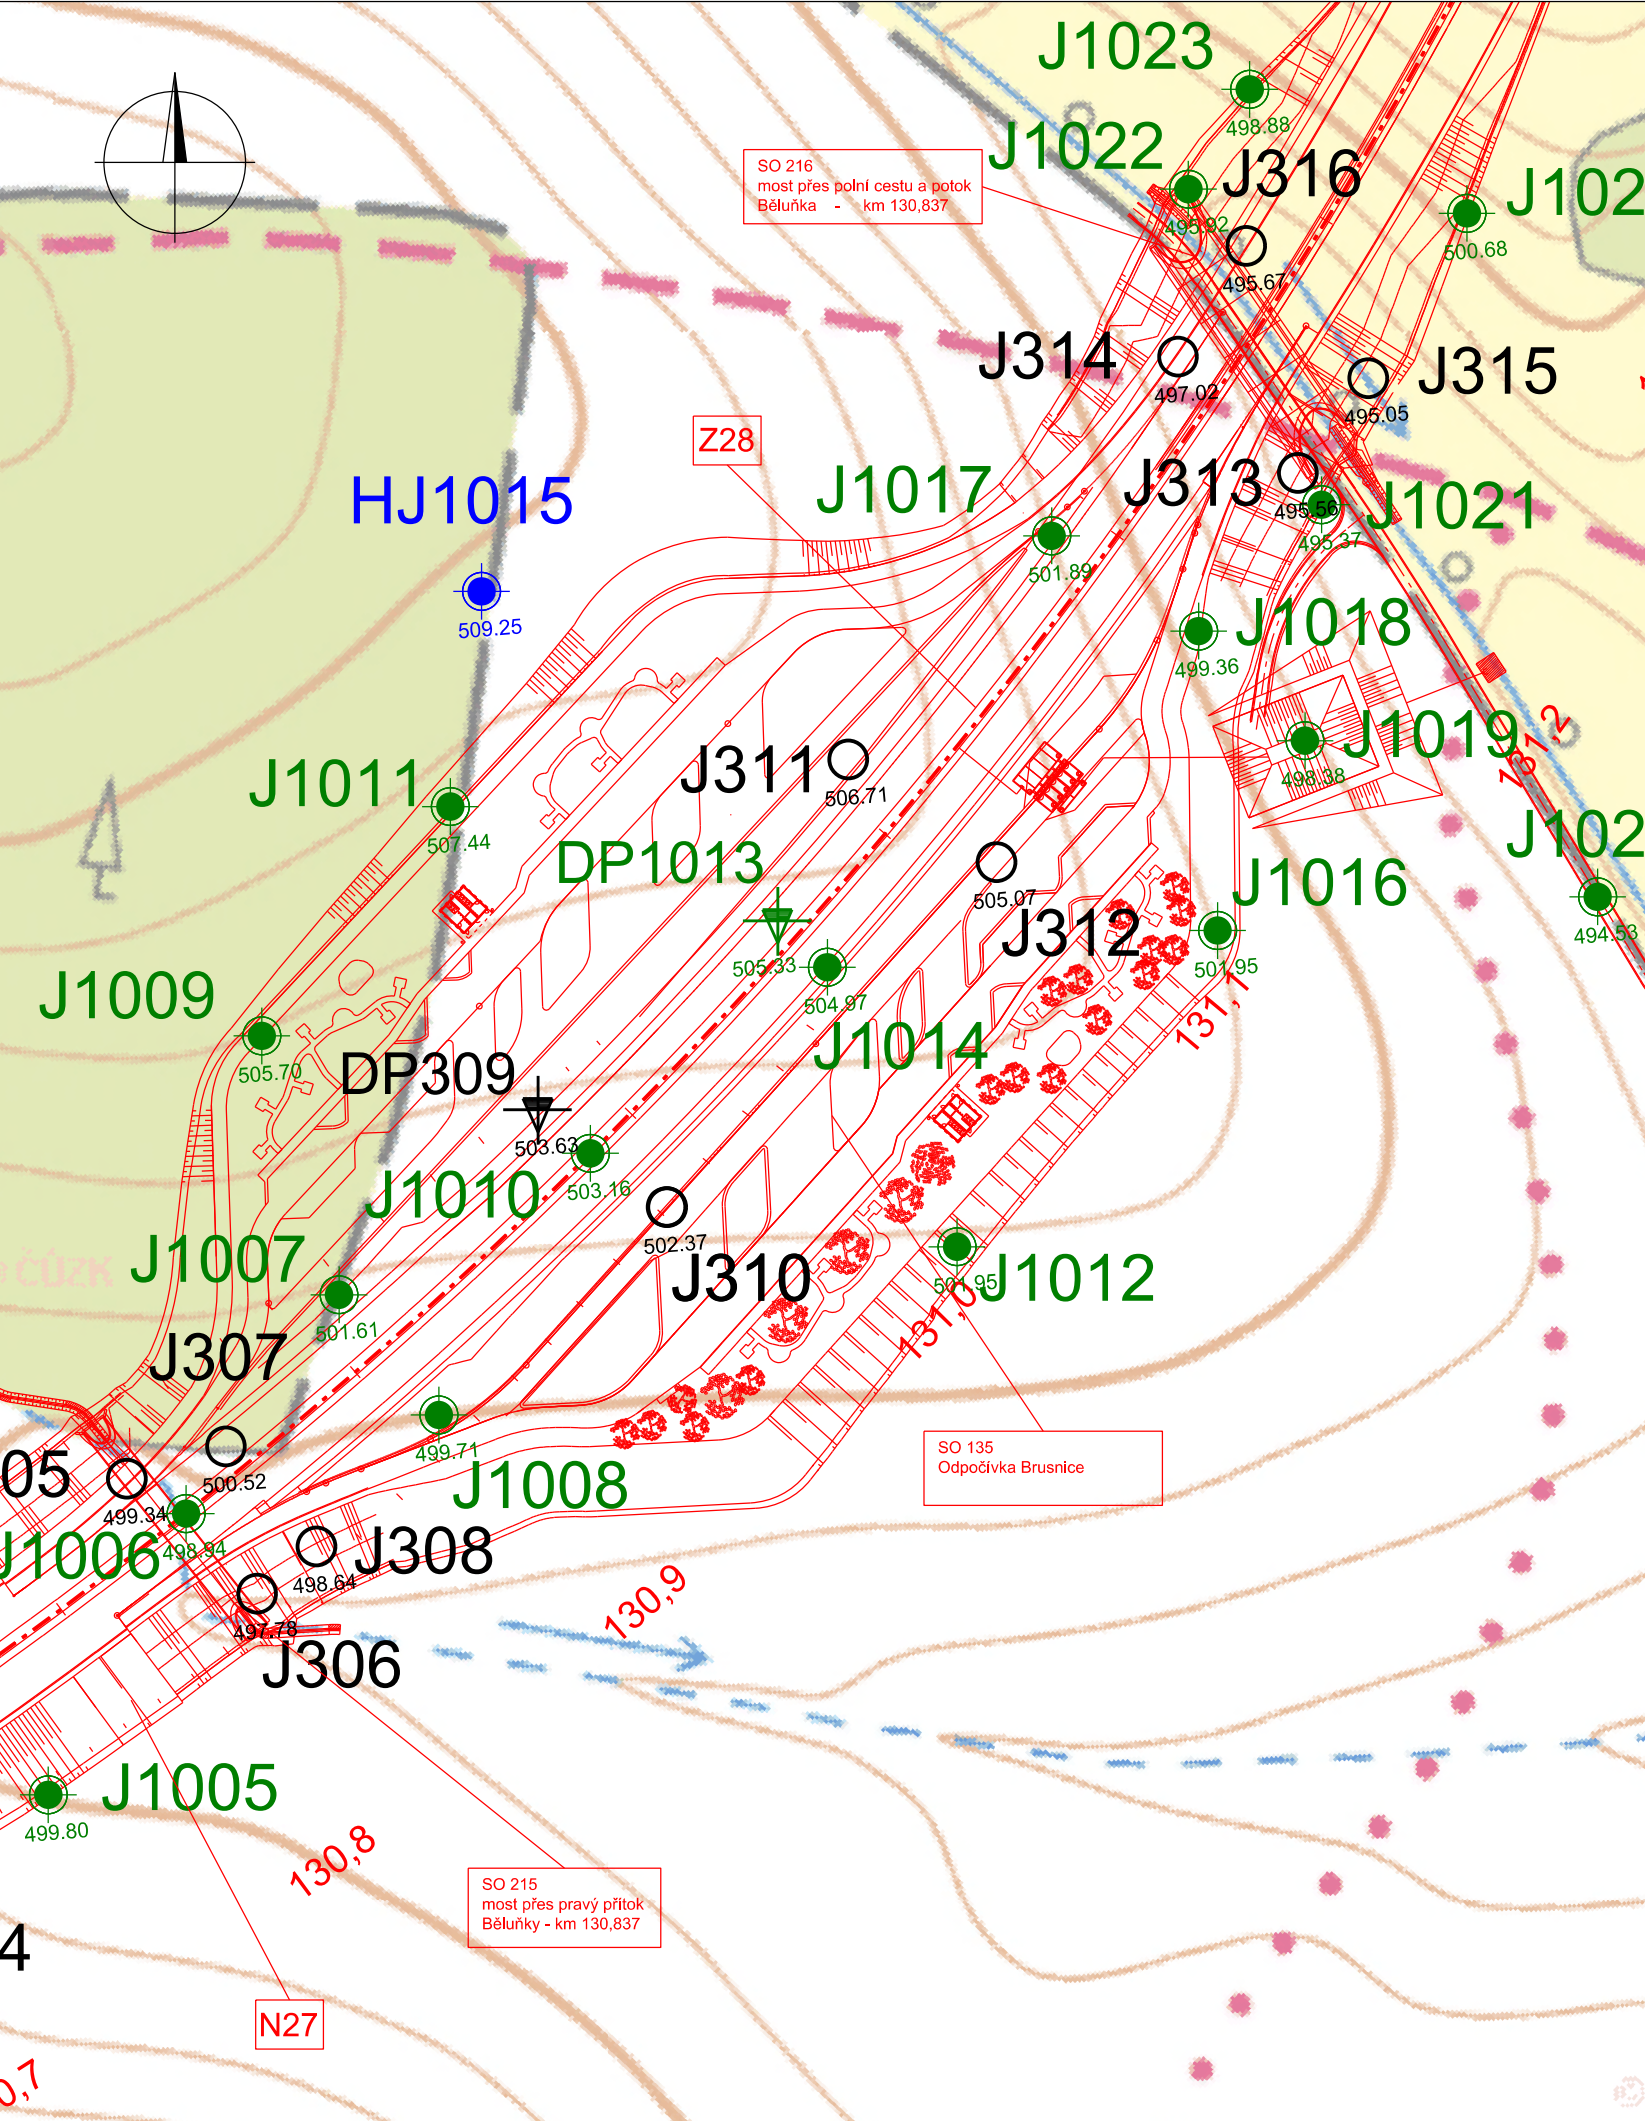

LEGENDA - PRÁCE PROVEDENÉ V RÁMCI PODROBNÉHO GTP:

- J526 jádrový IG vrt
- PJ524 jádrový vrt s presiometrickými zkouškami
- HJ540 jádrový hydrogeologický vrt
- SP520 statická penetrační zkouška (CPT)
- DP593 dynamická penetrační zkouška
- linie geotechnického profilu (výpočty)
- linie geofyzikálního profilu

ARCHIVNÍ GEOLOGICKÉ PRÁCE:

- J2 vrt provedený v rámci předběžného GTP
- CH-5 (FZ 5525) archivní sonda nesouvisející se stavbou dálnice (číslo posudku - klíč ČGS - Geofond)
- DP29 dynamická penetrace v rámci předběžného GTP
- geofyzikální profil v rámci předběžného GTP
- geotechnický profil v rámci předběžného GTP

Investor:

Ředitelství silnic a dálnic ČR
Správa Hradec Králové
Pouchovská 401
503 41 Hradec Králové



ŘEDITELSTVÍ SILNIC A DÁLNIC ČR

Zhotovitel:

Společnost A - P GTP D11 1108



Vypracoval: Erik Tomášek	Kontroloval: Mgr. J. Šindelář	Zhotovitel části: 
Odpovědný řešitel: Mgr. J. Šindelář	Schválil: Ing. Martina Štrosová	Klíšská 1334/12, 400 01 Ústí nad Labem tel. 475 240 888 www.azconsult.cz
Číslo zakázky: 18/037	Datum: 11/2019	

Akce:	Měřítko: 1:2000	Formát: 2 x A4
D11 1108 Jaroměř - Trutnov, podrobný geotechnický průzkum	Stupeň: DSP	Souprava:
Příloha: Situace provedených sond SO 135 Odpočívka Brusnice	Číslo přílohy: E13.1	