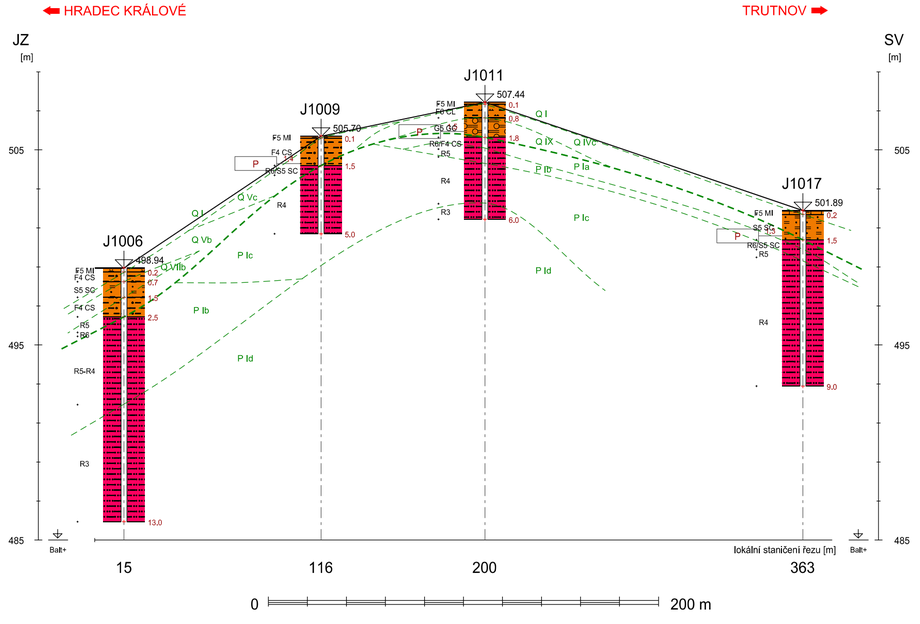


Geotechnické typy zemin				
označení		popis	konzistence, ulehlost	ČSN 73 6133
kvartér				
Q I		hlína organická, ornice, lesní hrabanka	-	F5 MI, F3 MS
Q II	**a**	hlína sprašová	měkká	F6 CI, F6 CL, F8 CH
	b	hlína sprašová	tuhá	F6 CI, F6 CL, F8 CH
	c	hlína sprašová	pevná až tvrdá	F6 CI, F6 CL, F8 CH
Q III	**a**	hlína, jíl s vysokou až velmi vysokou plasticitou	měkká	F7 MH, F8 CH, F7 MV, F8 CV
	b	hlína, jíl s vysokou až velmi vysokou plasticitou	tuhá	F7 MH, F8 CH, F7 MV, F8 CV
	c	hlína, jíl s vysokou až velmi vysokou plasticitou	pevná až tvrdá	F7 MH, F8 CH, F7 MV, F8 CV
Q IV	**a**	hlína, jíl se střední plasticitou	měkká	F5 MI, F6 CI, F6 CL
	b	hlína, jíl se střední plasticitou	tuhá	F5 MI, F6 CI, F6 CL
	c	hlína, jíl se střední plasticitou	pevná až tvrdá	F5 MI, F6 CI, F6 CL
Q V	**a**	hlína písčitá, jíl písčitý	měkká	F3 MS, F4 CS
	b	hlína písčitá, jíl písčitý	tuhá	F3 MS, F4 CS
	c	hlína písčitá, jíl písčitý	pevná až tvrdá	F3 MS, F4 CS
Q VI	**a**	hlína štěrkovitá, jíl štěrkovitý	měkká	F1 MG, F2 CG
	b	hlína štěrkovitá, jíl štěrkovitý	tuhá	F1 MG, F2 CG
	c	hlína štěrkovitá, jíl štěrkovitý	pevná až tvrdá	F1 MG, F2 CG
Q VII	**a**	písek hlinitý, písek jílovitý	kyprý	S4 SM, S5 SC
	b	písek hlinitý, písek jílovitý	středně ulehlý až ulehlý	S4 SM, S5 SC
Q VIII	**a**	písek s příměsí jemnozrnné zeminy	kyprý	S3 S-F
	b	písek s příměsí jemnozrnné zeminy	středně ulehlý až ulehlý	S3 S-F
Q IX		štěrk hlinitý, štěrk jílovitý	-	G4 GM, G5 GC
QX		štěrk s příměsí jemnozrnné zeminy	-	G3 G-F
křída				
K I		jíl písčitý	tuhý až pevný	F4 CS
K II		písek jílovitý	ulehlý	S5 SC
K III	**a**	prachovec vápnitý zcela zvětralý		R6
	b	prachovec vápnitý silně zvětralý		R5
	c	prachovec vápnitý mírně zvětralý		R4
	d	prachovec vápnitý navětralý až zdravý		R3-R2
K IV	**a**	eluvium pískovce		R6
	b	pískovec zcela zvětralý		R5
	c	pískovec silně zvětralý		R4
	d	pískovec mírně zvětralý		R3
	e	pískovec navětralý až zdravý		R3-R2; R2
K V	**a**	slínovec zcela zvětralý		R6
	b	slínovec silně zvětralý		R5
	c	slínovec mírně zvětralý		R4
	d	slínovec navětralý až zdravý		R4-R3; R3
perm				
P I	**a**	eluvium prachovce až jílovitého pískovce		R6
	b	jílovitý pískovec až prachovec zcela zvětralý		R5
	c	jílovitý pískovec až prachovec silně zvětralý		R4
	d	jílovitý pískovec až prachovec mírně zvětralý		R3
	e	jílovitý pískovec až prachovec navětralý až zdravý		R3-R2
P II	**a**	slepenec zcela zvětralý		R5
	b	slepenec silně zvětralý		R4
	c	slepenec mírně zvětralý až navětralý		R3
	d	slepenec zdravý		R2

LEGENDA

KVARTÉR - ANTROPOG. SEDIMENTY

- Násyp, navážka jílovitá
- Násyp, navážka štěrkovitá
- Štěrk jílovitý
- Sprašová hlína
- Balvan horniny

KVARTÉR

- Jíl
- Jíl prachovitý
- Jíl písčitý
- Jíl s valouny
- Hlína
- Hlína prachovitá
- Hlína písčitá
- Hlína organická
- Písek jílovitý
- Písek hlinitý
- Písek štěrkovitý

MEZOZOIKUM - KŘÍDA

- Slínovec
- Slínovec navětralý a zdravý
- Prachovec
- Jíl
- Písek

PERM

- Jílovitý pískovec
- Slepencový pískovec
- Jílovec

- δ — Zlom předpokládaný
- K IIIc — Rozhraní geotechnických typů, označení
- N 12,3 — Naražená hladina podzemní vody [m]
- U 10,34 — Ustálená hladina podzemní vody [m]
- Předpokládaný průběh souvislé hladiny podzemní vody

Investor:

Ředitelství silnic a dálnic ČR
Správa Hradec Králové
Pouchovská 401
503 41 Hradec Králové

ŘEDITELSTVÍ SILNIC A DÁLNIC ČR

Zhotovitel:

Společnost A - P GTP D11 1108

AZCONSULT spol s.r.o.

PUDIS

Vypracoval: V. Šímová	Kontroloval: Mgr. J. Šindelář	Zhotovitel části: AZCONSULT spol s.r.o. Klíšská 1334/12, 400 01 Ústí nad Labem tel. 475 240 888 www.azconsult.cz
Odpovědný řešitel: Mgr. J. Šindelář	Schválil: Ing. Martina Štrosová	
Číslo zakázky: 18/037	Datum: 11/2019	

Akce: D11 1108 Jaroměř - Trutnov, podrobný geotechnický průzkum	Měřítko: 1:2000 / 200	Formát: 3 x A4
	Stupeň: DSP	Souprava:
Příloha: Podélný geologický řez SO 135 Odpočívka Brusnice (vlevo)	Číslo přílohy: E.13.2.1	