


← HRADEC KRÁLOVÉ

TRUTNOV →

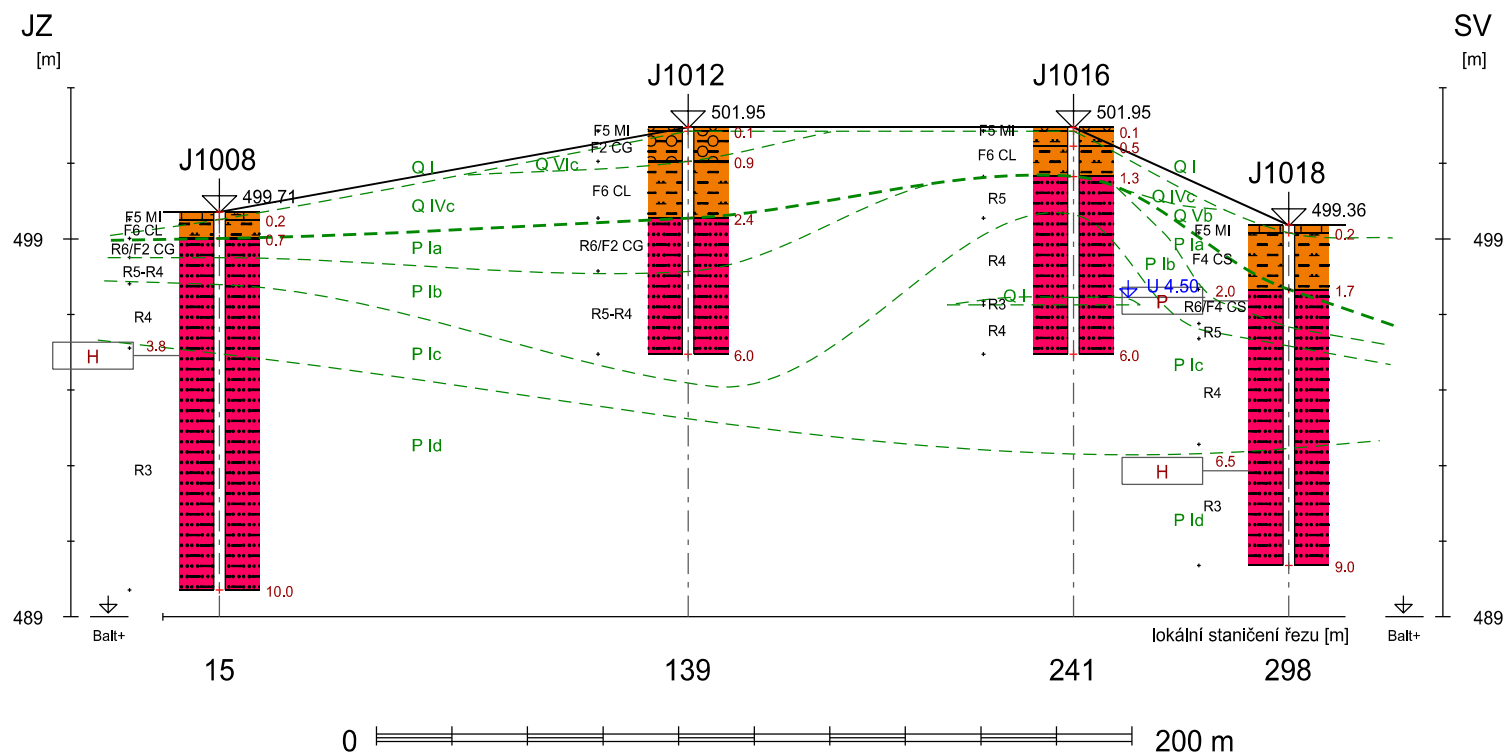


Geotechnické typy zemín			
označení	popis	konzistence, ulehlost	ČSN 73 6133
kvartér			
Q I	hlína organická, ornice, lesní hrabanka	-	F5 MI, F3 MS
Q II	a hlína sprašová	měkká	F6 CI, F6 CL, F8 CH
	b hlína sprašová	tuhá	F6 CI, F6 CL, F8 CH
	c hlína sprašová	pevná až tvrdá	F6 CI, F6 CL, F8 CH
Q III	a hlína, jíl s vysokou až velmi vysokou plasticitou	měkká	F7 MH, F8 CH, F7 MV, F8 CV
	b hlína, jíl s vysokou až velmi vysokou plasticitou	tuhá	F7 MH, F8 CH, F7 MV, F8 CV
	c hlína, jíl s vysokou až velmi vysokou plasticitou	pevná až tvrdá	F7 MH, F8 CH, F7 MV, F8 CV
Q IV	a hlína, jíl se střední plasticitou	měkká	F5 MI, F6 CI, F6 CL
	b hlína, jíl se střední plasticitou	tuhá	F5 MI, F6 CI, F6 CL
	c hlína, jíl se střední plasticitou	pevná až tvrdá	F5 MI, F6 CI, F6 CL
Q V	a hlína písčitá, jíl písčitý	měkká	F3 MS, F4 CS
	b hlína písčitá, jíl písčitý	tuhá	F3 MS, F4 CS
	c hlína písčitá, jíl písčitý	pevná až tvrdá	F3 MS, F4 CS
Q VI	a hlína štěrkovitá, jíl štěrkovitý	měkká	F1 MG, F2 CG
	b hlína štěrkovitá, jíl štěrkovitý	tuhá	F1 MG, F2 CG
	c hlína štěrkovitá, jíl štěrkovitý	pevná až tvrdá	F1 MG, F2 CG
Q VII	a písek hlinitý, písek jílovitý	kyprý	S4 SM, S5 SC
	b písek hlinitý, písek jílovitý	středně ulehlý až ulehlý	S4 SM, S5 SC
Q VIII	a písek s příměsí jemnozrnné zeminy	kyprý	S3 S-F
	b písek s příměsí jemnozrnné zeminy	středně ulehlý až ulehlý	S3 S-F
Q IX	štěrk hlinitý, štěrk jílovitý	-	G4 GM, G5 GC
QX	štěrk s příměsí jemnozrnné zeminy	-	G3 G-F
křída			
K I	jíl písčitý	tuhý až pevný	F4 CS
K II	písek jílovitý	ulehlý	S5 SC
K III	a prachovec vápnitý zcela zvětralý		R6
	b prachovec vápnitý silně zvětralý		R5
	c prachovec vápnitý mírně zvětralý		R4
	d prachovec vápnitý navětralý až zdravý		R3-R2
K IV	a eluvium pískovce		R6
	b pískovec zcela zvětralý		R5
	c pískovec silně zvětralý		R4
	d pískovec mírně zvětralý		R3
	e pískovec navětralý až zdravý		R3-R2; R2
K V	a slínovec zcela zvětralý		R6
	b slínovec silně zvětralý		R5
	c slínovec mírně zvětralý		R4
	d slínovec navětralý až zdravý		R4-R3; R3
perm			
P I	a eluvium prachovce až jílovitého pískovce		R6
	b jílovitý pískovec až prachovec zcela zvětralý		R5
	c jílovitý pískovec až prachovec silně zvětralý		R4
	d jílovitý pískovec až prachovec mírně zvětralý		R3
	e jílovitý pískovec až prachovec navětralý až zdravý		R3-R2
P II	a slepenec zcela zvětralý		R5
	b slepenec silně zvětralý		R4
	c slepenec mírně zvětralý až navětralý		R3
	d slepenec zdravý		R2

LEGENDA

KVARTÉR - ANTROPOG. SEDIMENTY




Násyp, navázka jílovitá
Násyp, navázka štěrkovitá

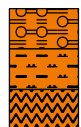


Štěrkl jílovitý
Sprašová hlína
Balvan horniny

KVARTÉR

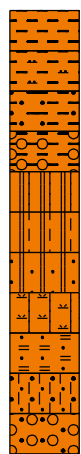


Jíl
Jíl prachovitý
Jíl písčitý
Jíl s valouny
Hlína
Hlína prachovitá
Hlína písčitá
Hlína organická
Písek jílovitý
Písek hlinitý
Písek štěrkovitý

MEZOZOIKUM - KŘÍDA

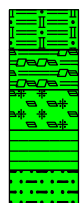

Slínovec
Slínovec navětralý a zdravý
Prachovec
Jíl
Písek

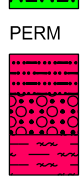

Jílovitý pískovec
Stěpcový pískovec
Jílovec



Zlom předpokládaný



Rozhraní geotechnických typů, označení



N 12.3 Naražená hladina podzemní vody [m]



U 10.34 Ustálená hladina podzemní vody [m]



Předpokládaný průběh souvislé hladiny podzemní vody

Investor:

Ředitelství silnic a dálnic ČR
Správa Hradec Králové
Pouchovská 401
503 41 Hradec Králové



ŘEDITELSTVÍ SILNIC A DÁLNIC ČR

Zhotovitel:

Společnost A - P GTP D11 1108

AZCONSULT[®] spol s.r.o.



Vypracoval:

V. Šimová

Kontroloval:

Mgr. J. Šindelář

Odpovědný řešitel:

Mgr. J. Šindelář

Schválil:

Ing. Martina Štrosová

Číslo zakázky:

18/037

Datum:

11/2019

Zhotovitel částí:

AZCONSULT[®] spol s.r.o.

Klíšská 1334/12, 400 01 Ústí nad Labem
tel. 475 240 888
www.azconsult.cz

Akce:

D11 1108 Jaroměř - Trutnov, podrobný geotechnický průzkum

Příloha:

Podélný geologický řez
SO 135 Odpočívka Brusnice (vpravo)

Měřítko:

1:2000 / 200

Formát:

3 x A4

Stupeň:

DSP

Číslo přílohy:

E.13.2.2