



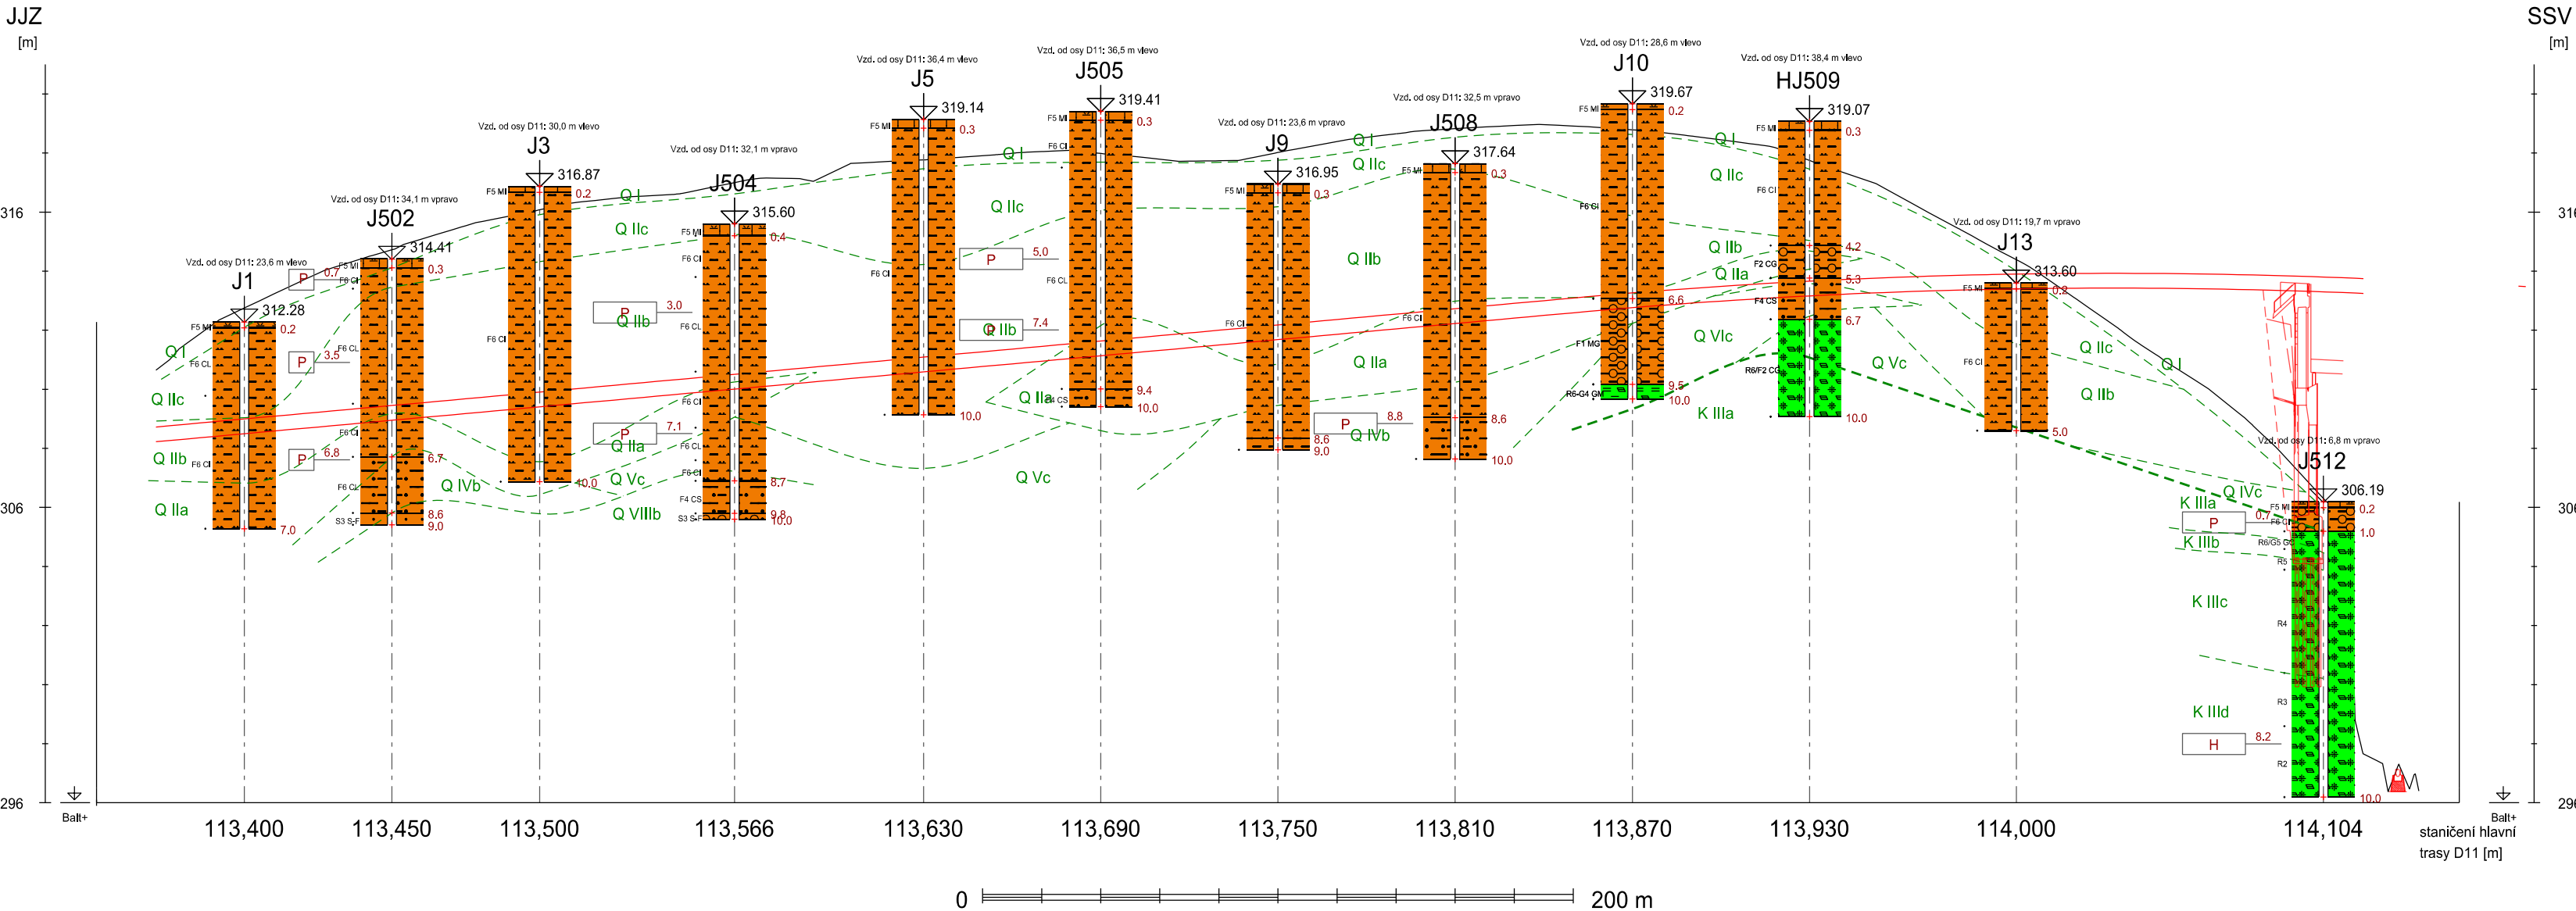

Geotechnické typy zemin			
označení	popis	konzistence, ulehlost	ČSN 73 6133
kvartér			
Q I	hlína organická, ornice, lesní hrabanka	-	F5 MI, F3 MS
Q II a	hlína sprašová	měkká	F6 CI, F6 CL, F8 CH
Q II b	hlína sprašová	tuhá	F6 CI, F6 CL, F8 CH
Q II c	hlína sprašová	pevná až tvrdá	F6 CI, F6 CL, F8 CH
Q III a	hlína, jíl s vysokou až velmi vysokou plasticitou	měkká	F7 MH, F8 CH, F7 MV, F8 CV
Q III b	hlína, jíl s vysokou až velmi vysokou plasticitou	tuhá	F7 MH, F8 CH, F7 MV, F8 CV
Q III c	hlína, jíl s vysokou až velmi vysokou plasticitou	pevná až tvrdá	F7 MH, F8 CH, F7 MV, F8 CV
Q IV a	hlína, jíl se střední plasticitou	měkká	F5 MI, F6 CI, F6 CL
Q IV b	hlína, jíl se střední plasticitou	tuhá	F5 MI, F6 CI, F6 CL
Q IV c	hlína, jíl se střední plasticitou	pevná až tvrdá	F5 MI, F6 CI, F6 CL
Q V a	hlína písčitá, jíl písčitý	měkká	F3 MS, F4 CS
Q V b	hlína písčitá, jíl písčitý	tuhá	F3 MS, F4 CS
Q V c	hlína písčitá, jíl písčitý	pevná až tvrdá	F3 MS, F4 CS
Q VI a	hlína štěrkovitá, jíl štěrkovitý	měkká	F1 MG, F2 CG
Q VI b	hlína štěrkovitá, jíl štěrkovitý	tuhá	F1 MG, F2 CG
Q VI c	hlína štěrkovitá, jíl štěrkovitý	pevná až tvrdá	F1 MG, F2 CG
Q VII a	písek hlinitý, písek jílovitý	kyprý	S4 SM, S5 SC
Q VII b	písek hlinitý, písek jílovitý	středně ulehlý až ulehlý	S4 SM, S5 SC
Q VIII a	písek s příměsí jemnozrnné zeminy	kyprý	S3 S-F
Q VIII b	písek s příměsí jemnozrnné zeminy	středně ulehlý až ulehlý	S3 S-F
Q IX	štěrk hlinitý, štěrk jílovitý	-	G4 GM, G5 GC
Q X	štěrk s příměsí jemnozrnné zeminy	-	G3 G-F
křída			
K I	jíl písčitý	tuhý až pevný	F4 CS
K II	písek jílovitý	ulehlý	S5 SC
K III a	prachovec vápnitý zcela zvětralý		R6
K III b	prachovec vápnitý silně zvětralý		R5
K III c	prachovec vápnitý mírně zvětralý		R4
K III d	prachovec vápnitý navětralý až zdravý		R3-R2
K IV a	eluvium pískovce		R6
K IV b	pískovec zcela zvětralý		R5
K IV c	pískovec silně zvětralý		R4
K IV d	pískovec mírně zvětralý		R3
K IV e	pískovec navětralý až zdravý		R3-R2; R2
K V a	slínovec zcela zvětralý		R6
K V b	slínovec silně zvětralý		R5
K V c	slínovec mírně zvětralý		R4
K V d	slínovec navětralý až zdravý		R4-R3; R3
perm			
P I a	eluvium prachovce až jílovitého pískovce		R6
P I b	jílovitý pískovec až prachovec zcela zvětralý		R5
P I c	jílovitý pískovec až prachovec silně zvětralý		R4
P I d	jílovitý pískovec až prachovec mírně zvětralý		R3
P I e	jílovitý pískovec až prachovec navětralý až zdravý		R3-R2
P II a	slepenec zcela zvětralý		R5
P II b	slepenec silně zvětralý		R4
P II c	slepenec mírně zvětralý až navětralý		R3
P II d	slepenec zdravý		R2

LEGENDA

KVARTÉR - ANTROPOG. SEDIMENTY

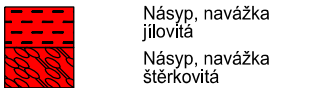

KVARTÉR



N 12,3
U 10,34

N 12,3
U 10,34

Předpokládaný průběh souvislé hladiny podzemní vody


H 3,7

Poloha odebraného vzorku:
H - hornina,
P - porušený,
N - neporušený,
T - technologický

MEZOZOIKUM - KŘÍDA



PERM

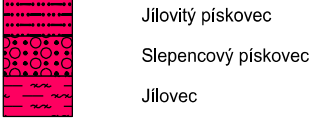

δ
K IIIc

Zlom předpokládaný
Rozhraní geotechnických typů, označení

Investor:

Ředitelství silnic a dálnic ČR
Správa Hradec Králové
Pouchovská 401
503 41 Hradec Králové



ŘEDITELSTVÍ SILNIC A DÁLNIC ČR

Zhotovitel:

Společnost A - P GTP D11 1108

AZCONSULT spol s.r.o.



Vypracoval:

V. Šimová

Odpovědný řešitel:

Mgr. J. Šindelář

Číslo zakázky:

18/037

Kontroloval:

Mgr. J. Šindelář

Schválil:

Ing. Martina Štrosová

Datum:

11/2019

Zhotovitel část:

AZCONSULT spol s.r.o.

Klíšská 1334/12, 400 01 Ústí nad Labem
tel. 475 240 888
www.azconsult.cz

Akce:

D11 1108 Jaroměř - Trutnov, podrobný geotechnický průzkum

Příloha:

Podélný geologický profil trasy

Měřítko:

1:2000 / 200

Stupeň:

DSP

Číslo přílohy:

A.3.1

Formát:

4 x A4

Souprava: