




Geotechnické typy zemín			
označení	popis	kvantor	konstancie, uhlasiost
			ČSN 73 6133
Q I	hlna organická, omace, lesná hrabanka	-	F3, M3, F3 M3
Q II	a hlna správoš	máka	F6, F6, C6, F8 CH
	b hlna správoš	túha	F6, C6, F6, C6, F8 CH
	c hlna správoš	penia z túrd	F6, C6, F6, C6, F8 CH
Q III	a hlna, je v ysoctu až veľmi vysokou plastickou	máka	F7 M4, F3, CH, F7, M4, F8 CH
	b hlna, je v ysoctu až veľmi vysokou plastickou	túha	F7 M4, F3, CH, F7, M4, F8 CH
	c hlna, je v ysoctu až veľmi vysokou plastickou	penia z túrd	F7 M4, F3, CH, F7, M4, F8 CH
Q IV	a hlna, je sa sfedni plastickou	máka	F5 M, F6, C6, F6, C6
	b hlna, je sa sfedni plastickou	túha	F5 M, F6, C6, F6, C6
	c hlna, je sa sfedni plastickou	penia z túrd	F5 M, F6, C6, F6, C6
Q V	a hlna písotá, j písioty	máka	F3 M5, F4 C5
	b hlna písotá, j písioty	túha	F3 M5, F4 C5
	c hlna písotá, j písioty	penia z túrd	F3 M5, F4 C5
Q VI	a hlna sférkovitá, j sférkovitú	máka	F1 M2, G2 C6
	b hlna sférkovitá, j sférkovitú	túha	F1 M2, G2 C6
	c hlna sférkovitá, j sférkovitú	penia z túrd	F1 M2, G2 C6
Q VII	a písek hliný, písek jlový	kyprý	S4 M5, S5 C5
	b písek hliný, písek jlový	středni uleňtý až uleňtý	S4 M5, S5 C5
Q VIII	a písek s písmi jerné zeminy	kyprý	S3 S5 F
	b písek s písmi jerné zeminy	středni uleňtý až uleňtý	S3 S5 F
Q IX	a hliné hliný, sférk jlový	-	G4 GM, G5 C6
Q X	sférk s písmi jerné zeminy	-	G3 G F
křida			
K I	j písioty	hňh až zemny	F4 C5
K II	pisok jlový	uleňtý	S5 C5
K III	a prachove vápnyty zela zřatý	R6	
	b prachove vápnyty sílné zřatý	R5	
	c prachove vápnyty sílné zřatý	R4	
	d prachove vápnyty sílné zřatý	R3	
	e prachove vápnyty sílné zřatý	R2	
K IV	a eluvium písokove	R6	
	b písokove zela zřatý	R5	
	c písokove sílné zřatý	R4	
	d písokove sílné zřatý	R3	
	e písokove sílné zřatý	R2	
K V	a sílnokove zela zřatý	R6	
	b sílnokove sílné zřatý	R5	
	c sílnokove sílné zřatý	R4	
	d sílnokove sílné zřatý	R3	
	e sílnokove sílné zřatý	R2	
perm			
P I	a eluvium prachove až jlovitě písokove	R6	
	b jlovitě písokove až prachove zela zřatý	R5	
	c jlovitě písokove až prachove sílné zřatý	R4	
	d jlovitě písokove až prachove sílné zřatý	R3	
	e jlovitě písokove až prachove sílné zřatý	R2	
P II	a slepenec zela zřatý	R6	
	b slepenec sílné zřatý	R5	
	c slepenec sílné zřatý až sílné zřatý	R4	
	d slepenec sílné zřatý až sílné zřatý	R3	
	e slepenec sílné zřatý až sílné zřatý	R2	

Investor: Režebřetiví sílnic: a.d.č.n.r. Správa Hradec Králové Pouchovská 481 503 41 Hradec Králové	 ŘEDITELSTVÍ SILNIC A DÁLNIC ČR	
Projevitel: Společnost A - P GTP D11 1108		
AZCOCONSULT spol.s.r.o. Výpočetní: V. Šimová Opisovatelé: Mgr. J. Šindler Číslo zakázky: 18037	Kontrolní: Mgr. J. Šindler Směrník: Ing. Jarmila Štrousová Datum: 11/2019	Zpracoval: azcoconsult spol.s.r.o. Hláská 1234/1 420 01 Ost nad Labem tel. 477-264 810 www.azcoconsult.cz
Ac: D11 1108 Jaroměř - Trutnov, podrobný geotechnický průřez Wfka: Podélný geologický profil trasy	MMfko: 1:2000 / 200 Skupst: DSP Číslo přílohy:	Formát: A3 Skupstevná: A.3.3