


označení		popis	konzistence, ulehlost	Č
kváter				
Q I		hlína organická, omice, lesní hrabanka	-	F
Q II	a	hlína sprašová	měkká	F6 C
	b	hlína sprašová	tuhá	F6 C
	c	hlína sprašová	pevná až tvrdá	F6 C
Q III	a	hlína, jíl s vysokou až velmi vysokou plasticitou	měkká	F7 MF, F
	b	hlína, jíl s vysokou až velmi vysokou plasticitou	tuhá	F7 MF, F
	c	hlína, jíl s vysokou až velmi vysokou plasticitou	pevná až tvrdá	F7 MF, F
Q IV	a	hlína, jíl se střední plasticitou	měkká	F5 F
	b	hlína, jíl se střední plasticitou	tuhá	F5 F
	c	hlína, jíl se střední plasticitou	pevná až tvrdá	F5 F
Q V	a	hlína písčitá, jíl písčité	měkká	F
	b	hlína písčitá, jíl písčité	tuhá	F
	c	hlína písčitá, jíl písčité	pevná až tvrdá	F
Q VI	a	hlína štěrkovitá, jíl šterkovitý	měkká	F
	b	hlína štěrkovitá, jíl šterkovitý	tuhá	F
	c	hlína štěrkovitá, jíl šterkovitý	pevná až tvrdá	F
Q VII	a	písek hlinitý, písek jílovitý	kyprý	S
	b	písek hlinitý, písek jílovitý	středně ulehly až ulehly	S
Q VIII	a	písek s příměsí jemnozrnné zeminy	kyprý	S
	b	písek s příměsí jemnozrnné zeminy	středně ulehly až ulehly	G
Q IX		štěrk hlinitý, šterk jílovitý	-	
Q X		štěrk s příměsí jemnozrnné zeminy	-	
křída				
K I		jíl písčité	tuhý až pevný	
K II		písek jílovitý	ulehly	
K III	a	prachovec vápnitý zcela zvětralý		
	b	prachovec vápnitý silně zvětralý		
	c	prachovec vápnitý mírně zvětralý		
	d	prachovec vápnitý navětřlý až zdravý		
K IV	a	eluvium pískovce		
	b	pískovec zcela zvětralý		
	c	pískovec silně zvětralý		
	d	pískovec mírně zvětralý		
	e	pískovec navětřlý až zdravý		
K V	a	silinovec zcela zvětralý		
	b	silinovec silně zvětralý		
	c	silinovec mírně zvětralý		
	d	silinovec navětřlý až zdravý		
perm				
P I	a	eluvium prachovce až jílovitého pískovce		
	b	jílovitý pískovec až prachovce zcela zvětralý		
	c	jílovitý pískovec až prachovce silně zvětralý		
	d	jílovitý pískovec až prachovce mírně zvětralý		
	e	jílovitý pískovec až prachovce navětřlý až zdravý		
P II	a	slépenec zcela zvětralý		
	b	slépenec silně zvětralý		
	c	slépenec mírně zvětralý až navětřlý		
	d	slépenec zdravý		

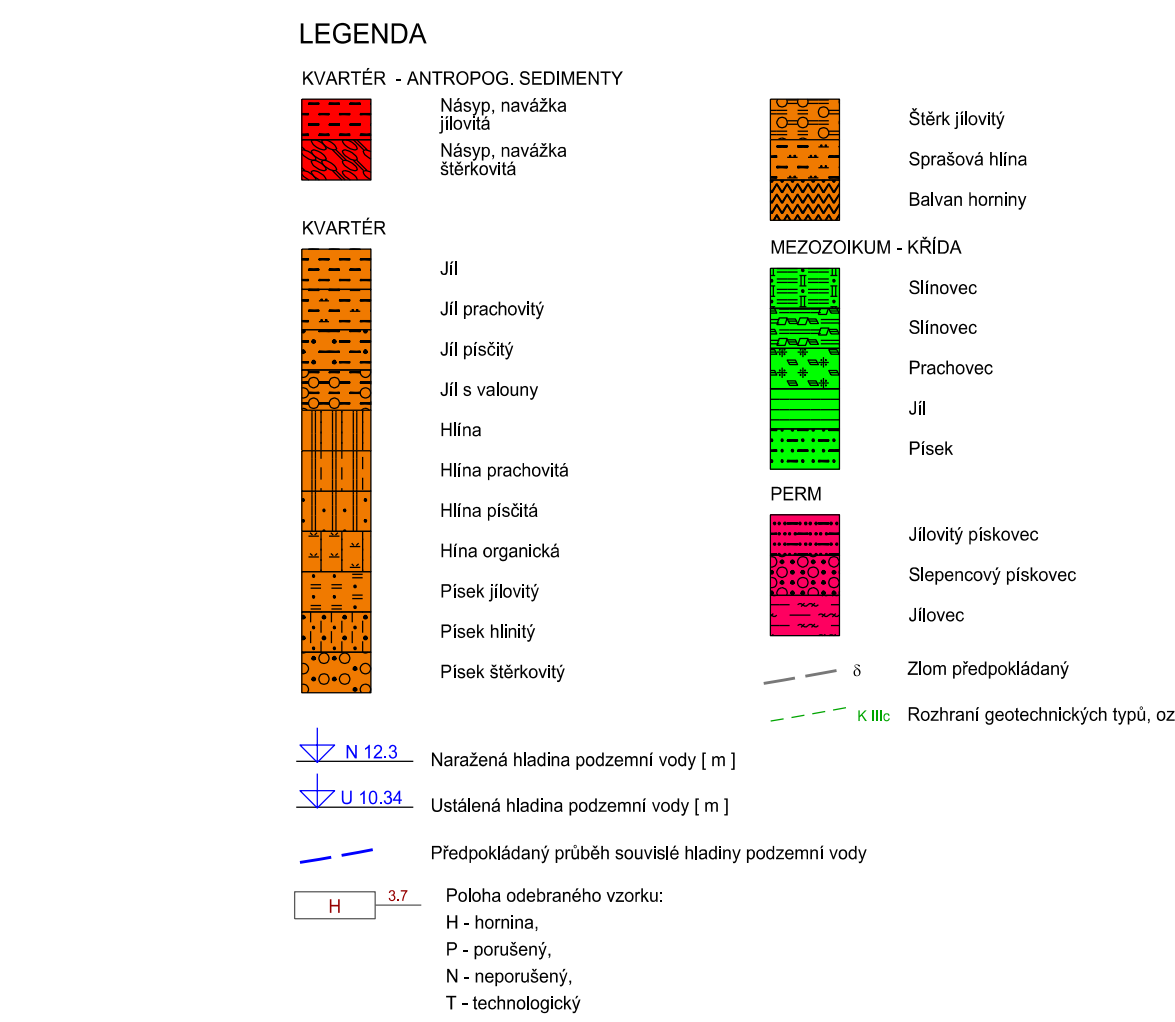

Investor: Ředitelství silnic a dálnic ČR
 Správa Hradec Králové
 Poučkovská 401
 503 41 Hradec Králové

 ŘEDITELSTVÍ SILNIC A DÁLNIC ČR

Zhotovitel: Společnost A - P GTP D11 1108

AZCONSULT[®] spol.s.r.o. **ap PUD**

Vypracoval: V. Šimová	Kontroloval: Mgr. J. Šindelář	Zhotovil část:
Odpovědný ředitel: Mgr. J. Šindelář	Ing. Ševčík: Ing. Martina Štросová	 Kilišská 1334/12, 400 01 Ústí nad tel. 475 240 888 www.azconsul.cz
Číslo zakázky: 18/037	Datum: 10/2019	

Akce: D11 1108 Jaroměř - Trutnov, podrobný geotechnický průzkum	Měřítko: 1:2000 / 200 Škála: DSP
Přihlas: Podélný geologický profil trasy	Číslo přihlas: A.3.7