






Lokalita	D11 1108 Jaroměř - Trutnov
Zákazník	
Poznámka	použito snížovače
Operátor	
Sonda	SP520
Hloubka pažení	

Datum	9.8.2019
HI vody naražené	
HI vody ustálené	suchá
X	
Y	
Z	

hi	QST	QT	0	—	QT	—	200 [kN]
[m]	[Mpa]	[kN]	0	—	qc	—	50 [Mpa]

Rf	FS	0	—	Fs	—	1 [Mpa]
%	[Mpa]	0	—	Rf	—	25 [%]

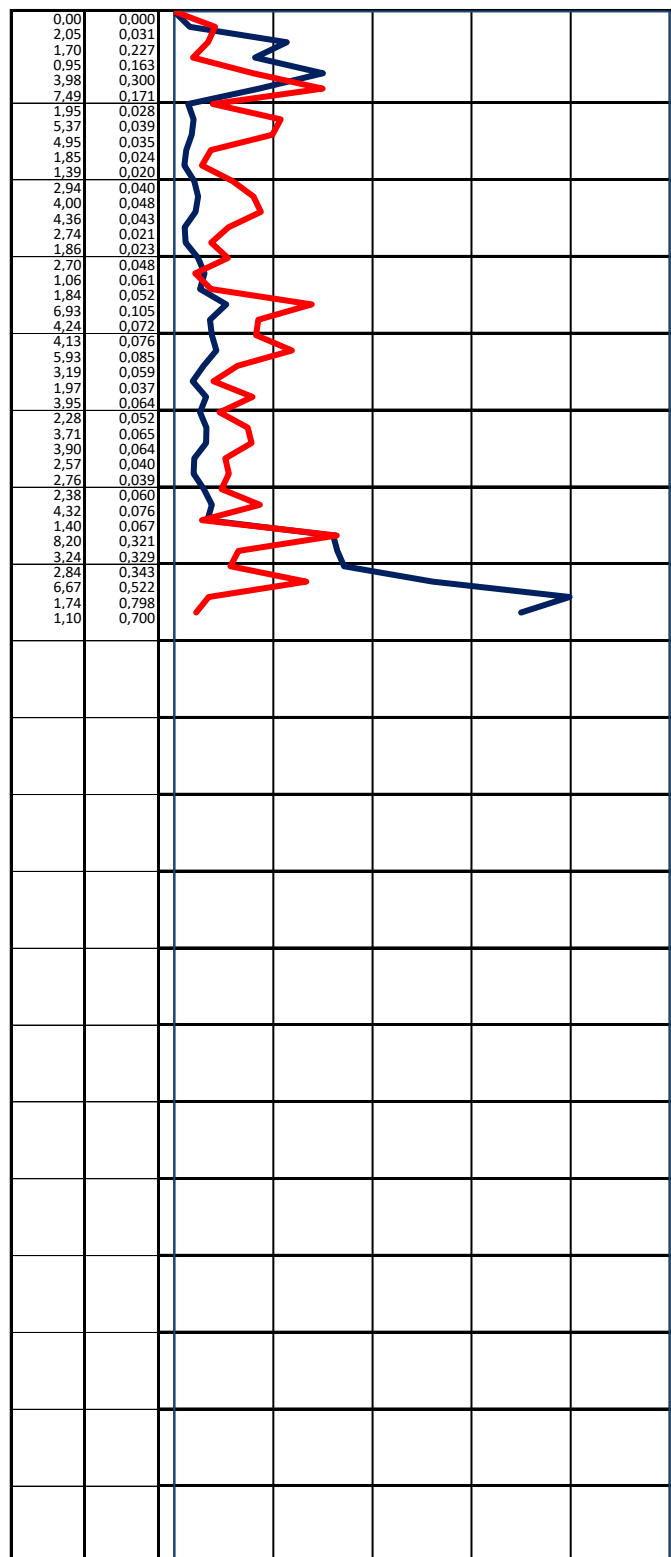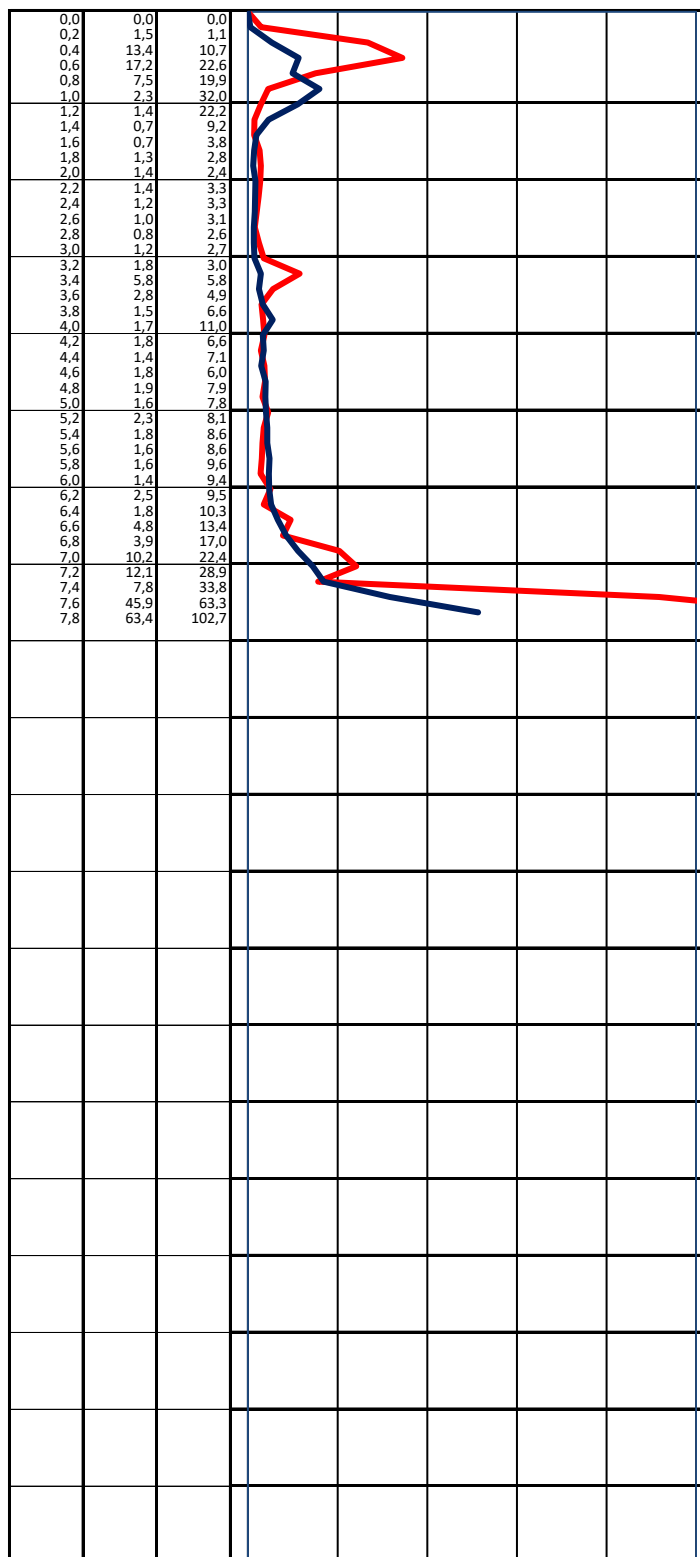

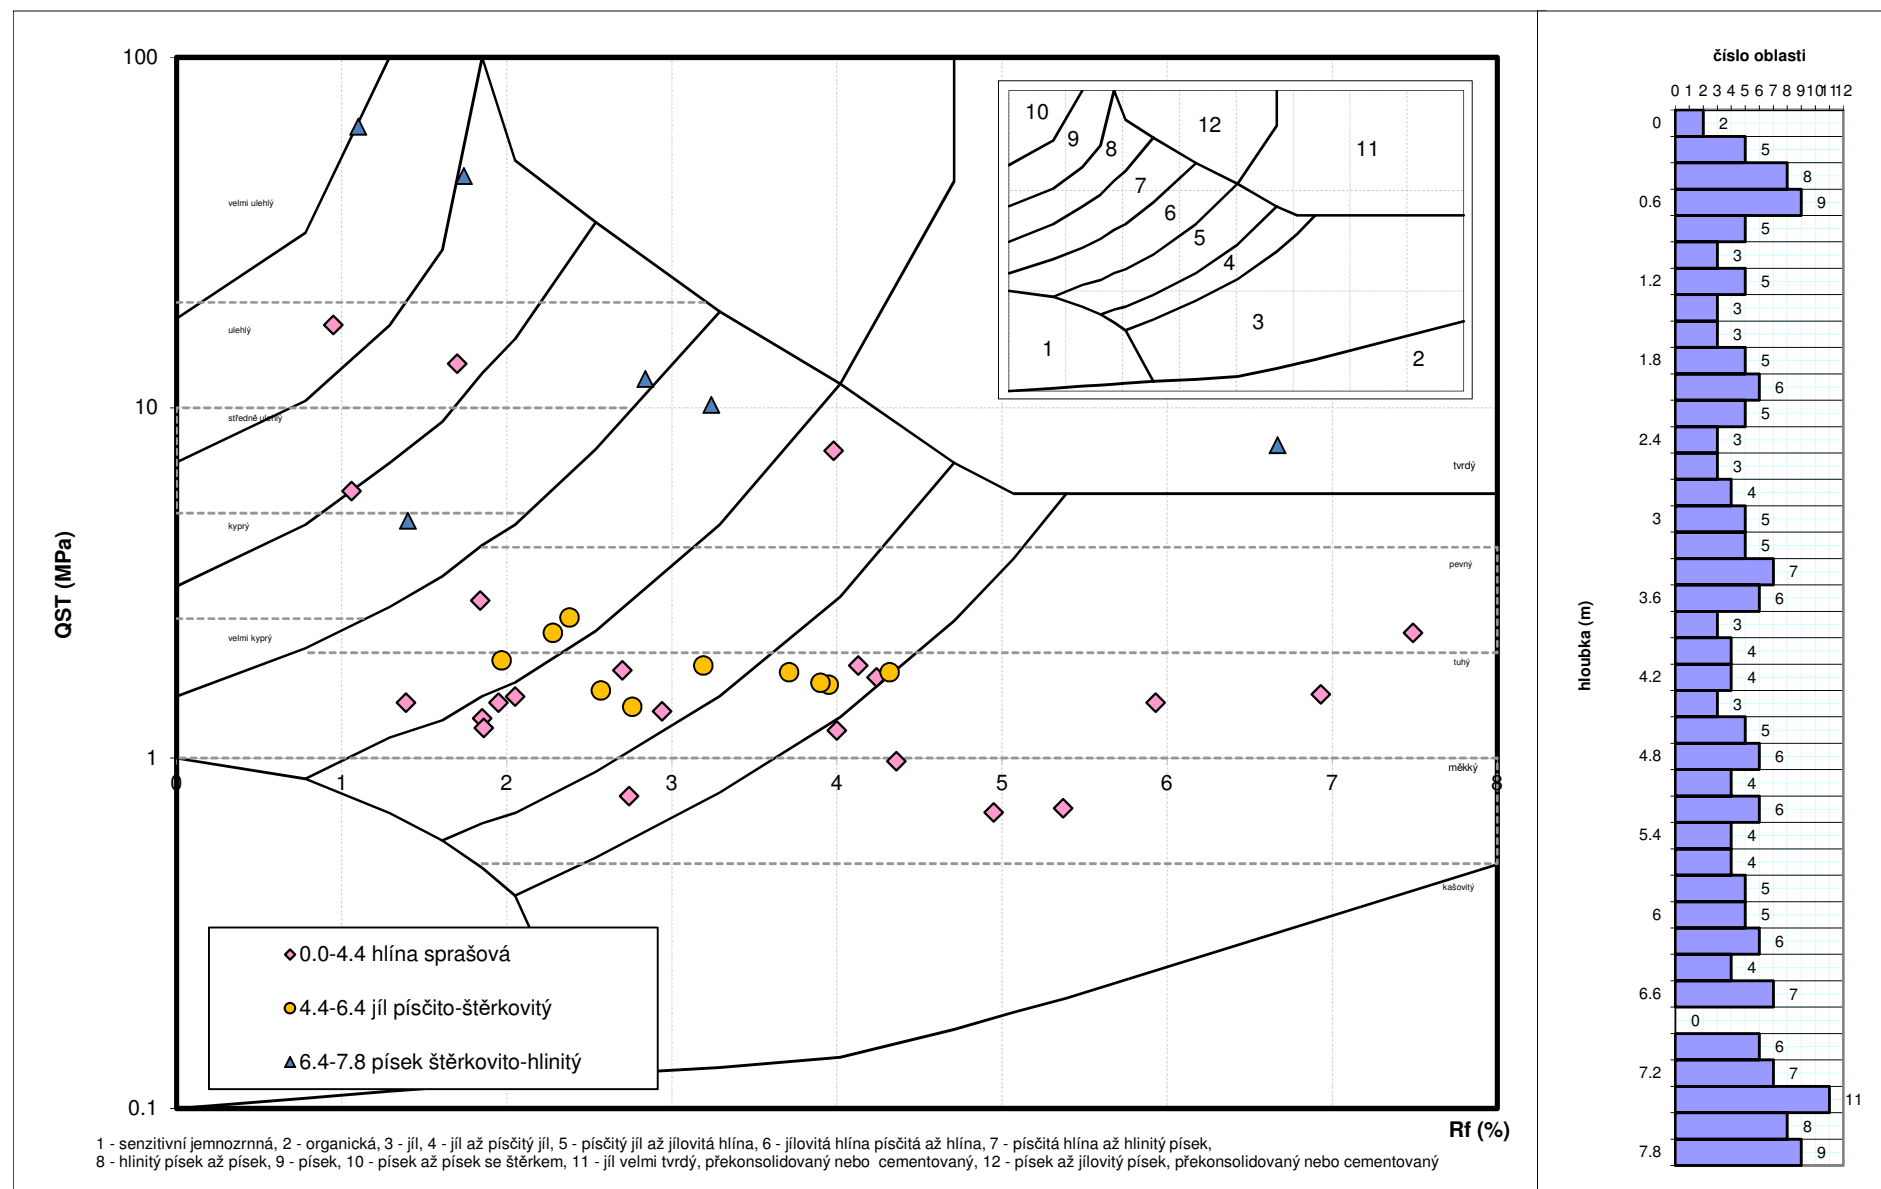






Lokalita	D11 1108 Jaroměř - Trutnov
Zákazník	
Poznámka	použito snížovače
Operátor	
Sonda	SP549
Hloubka pažení	

Datum	9.8.2019
Hl vody naražené	
Hl vody ustálené	18,0 m zavaleno
X	
Y	
Z	

hl	QST	QT	0	—	QT	—	200 [kN]
[m]	[Mpa]	[kN]	0	—	qc	—	50 [Mpa]

Rf	FS	0	—	Fs	—	1 [Mpa]
%	[Mpa]	0	—	Rf	—	25 [%]

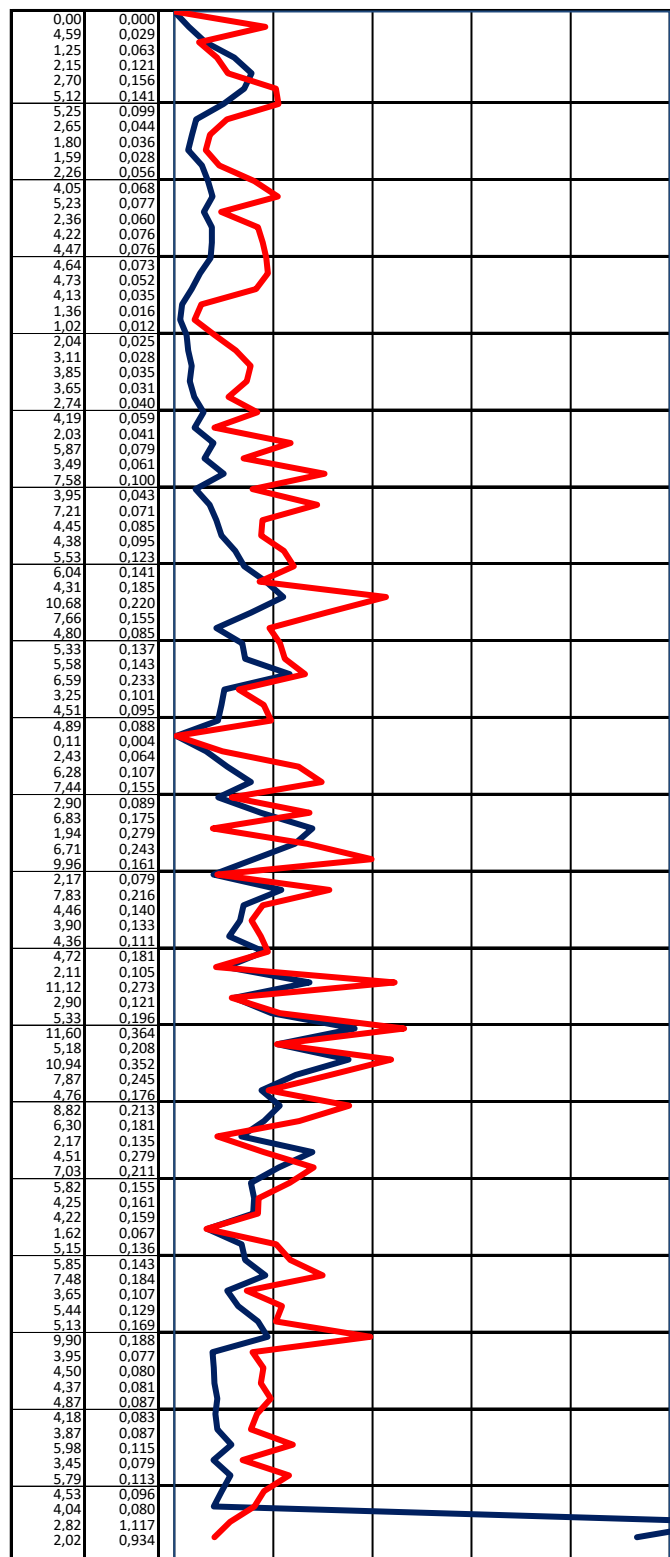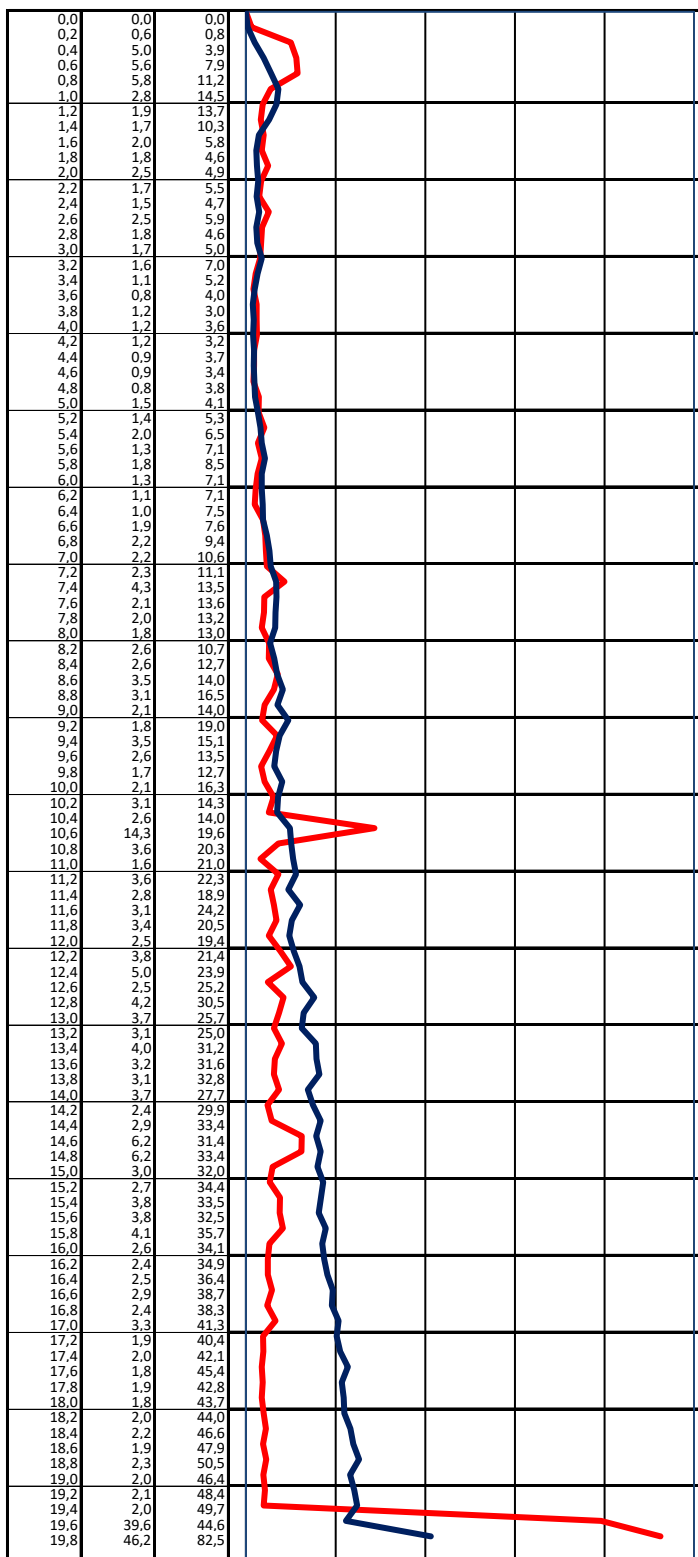

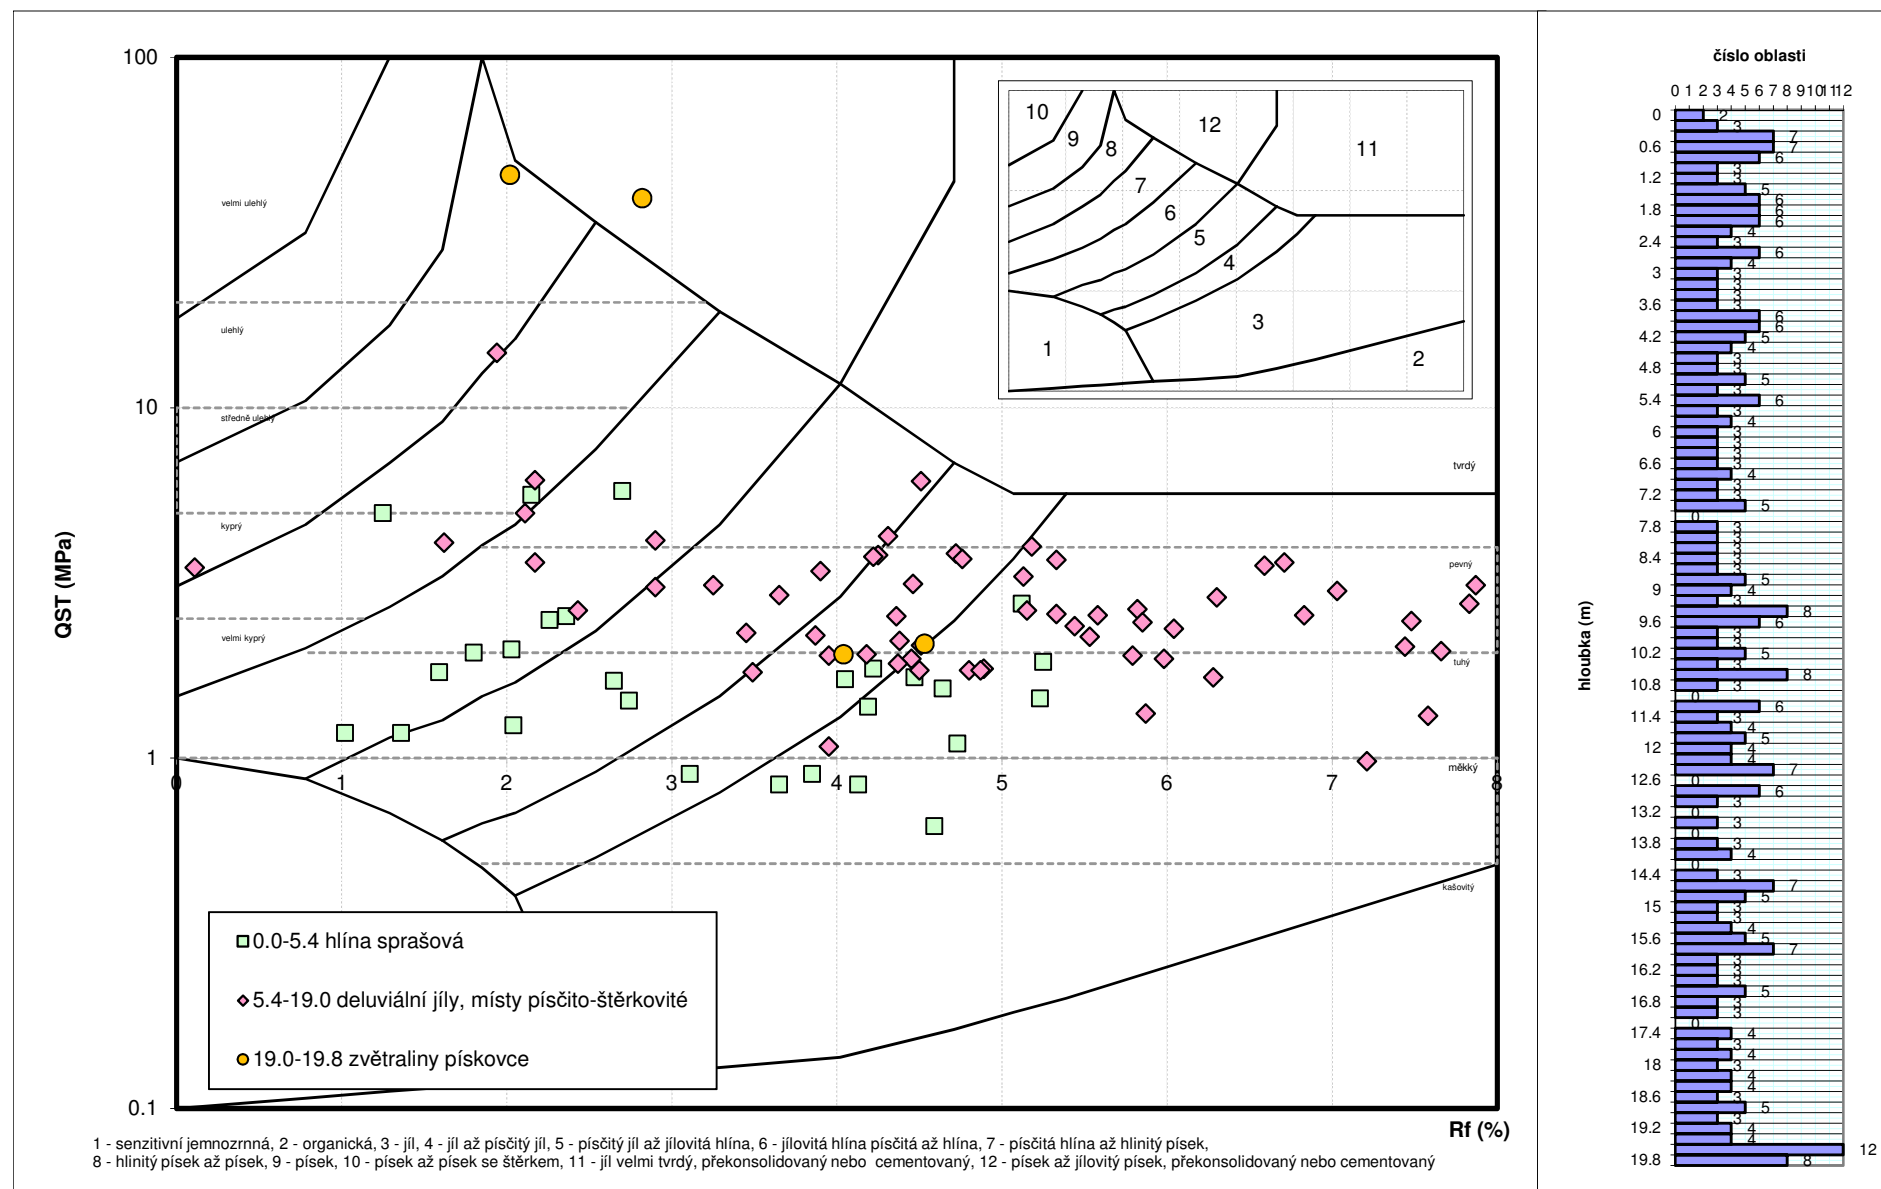





Lokalita	D11 1108 Jaroměř - Trutnov
Zákazník	
Poznámka	použito snížovače
Operátor	
Sonda	SP586
Hloubka pažení	

Datum	9.8.2019
HI vody naražené	
HI vody ustálené	1,8 m
X	
Y	
Z	

hi	QST	QT	0		QT		200 [kN]
[m]	[Mpa]	[kN]	0		qc		50 [Mpa]

Rf	FS	0		Fs		1 [Mpa]
%	[Mpa]	0		Rf		25 [%]

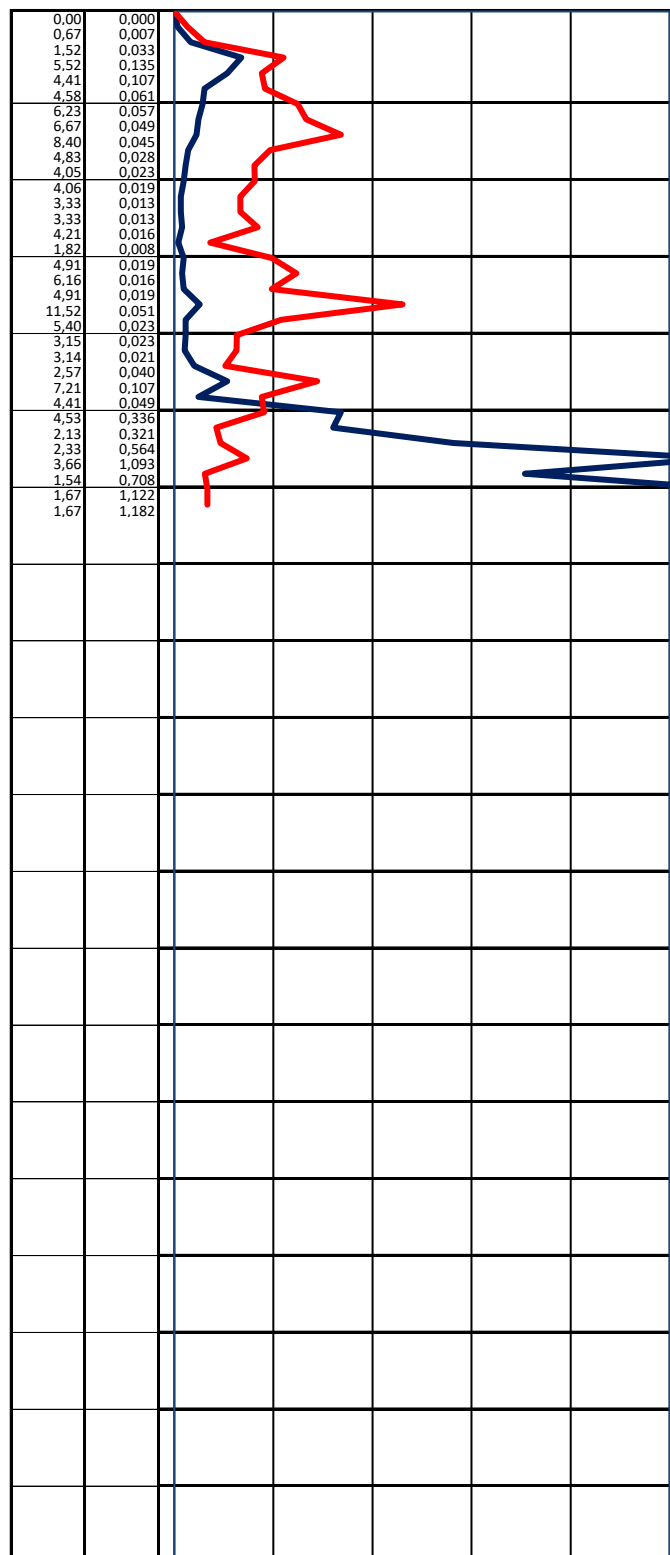

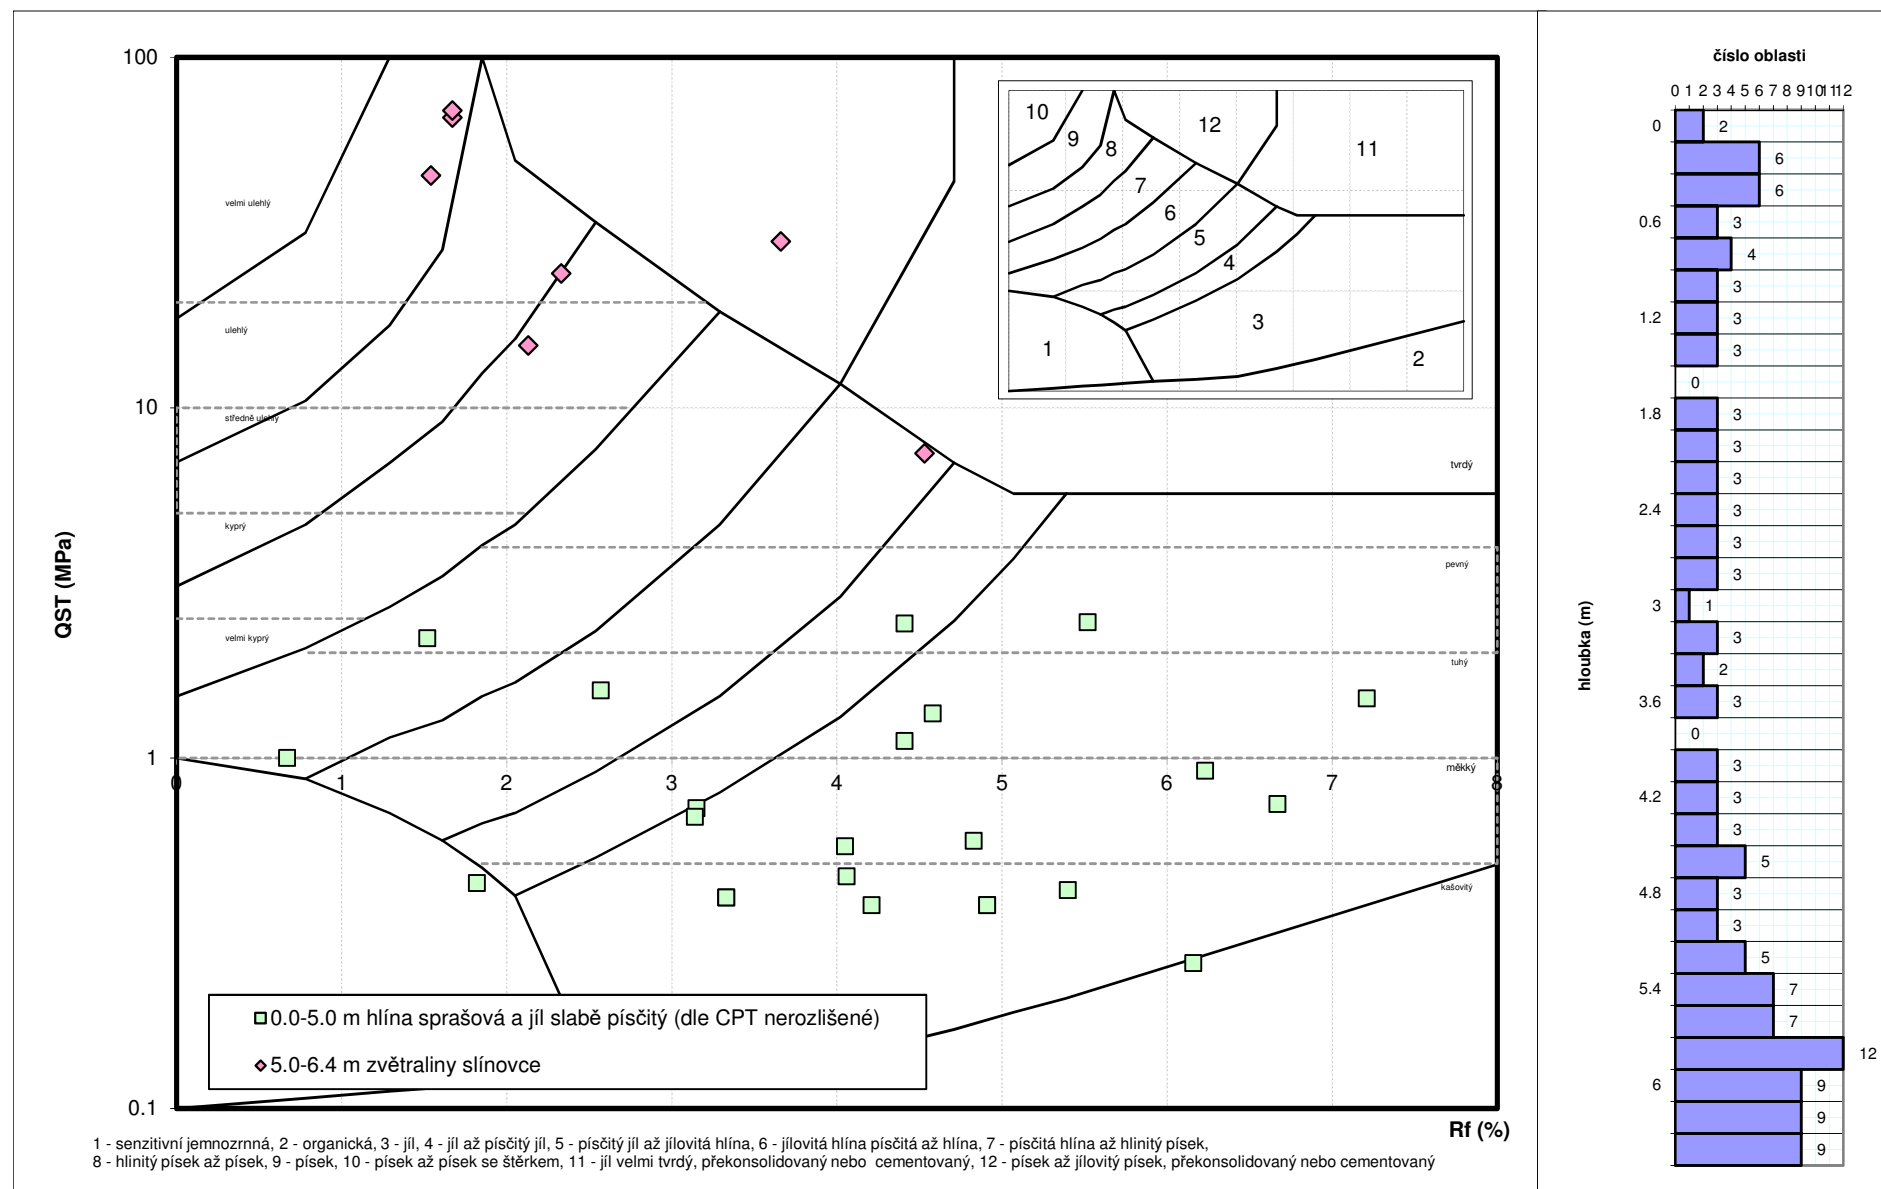






Lokalita	D11 1108 Jaroměř - Trutnov
Zákazník	
Poznámka	použito snížovače
Operátor	
Sonda	SP589
Hloubka pažení	

Datum	9.8.2019
HI vody naražené	
HI vody ustálené	1,9 m
X	
Y	
Z	

hi	QST	QT	0	—	QT	—	200 [kN]
[m]	[Mpa]	[kN]	0	—	qc	—	50 [Mpa]

Rf	FS	0	—	Fs	—	1 [Mpa]
%	[Mpa]	0	—	Rf	—	25 [%]

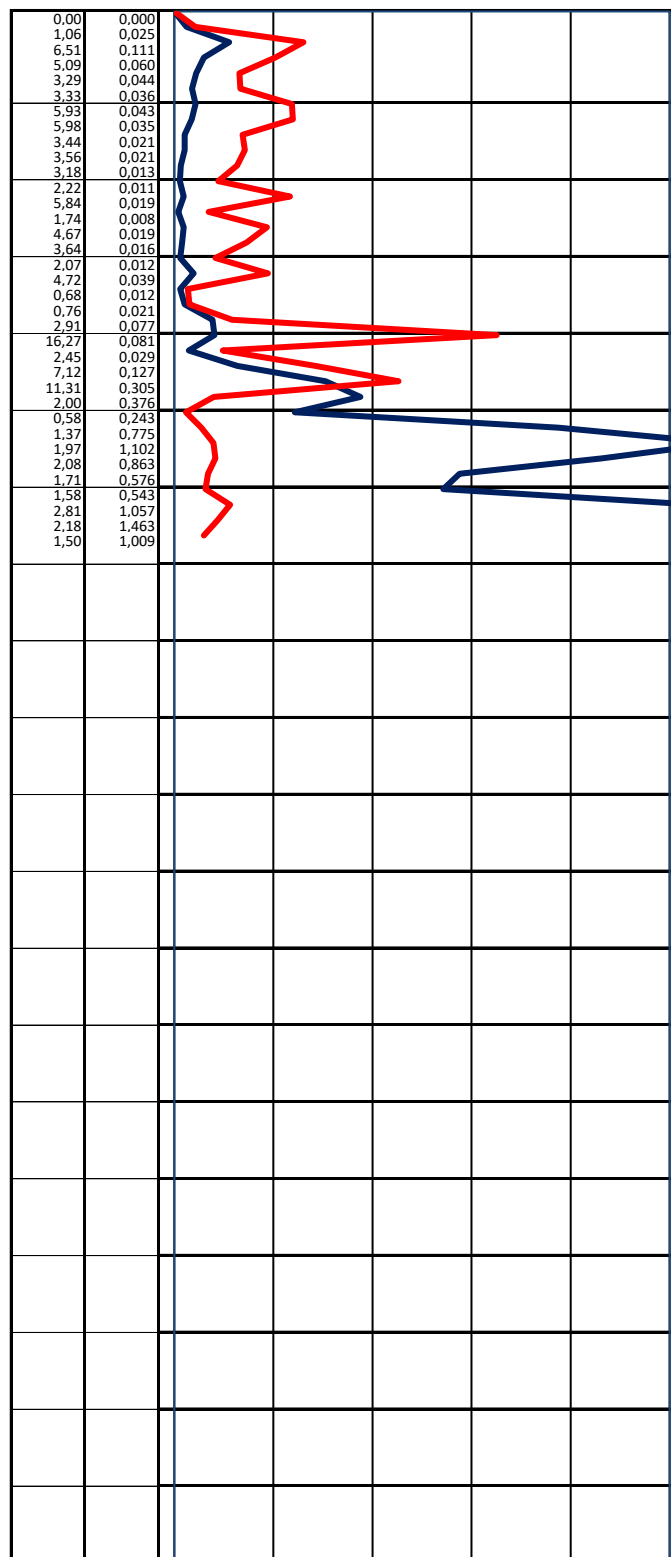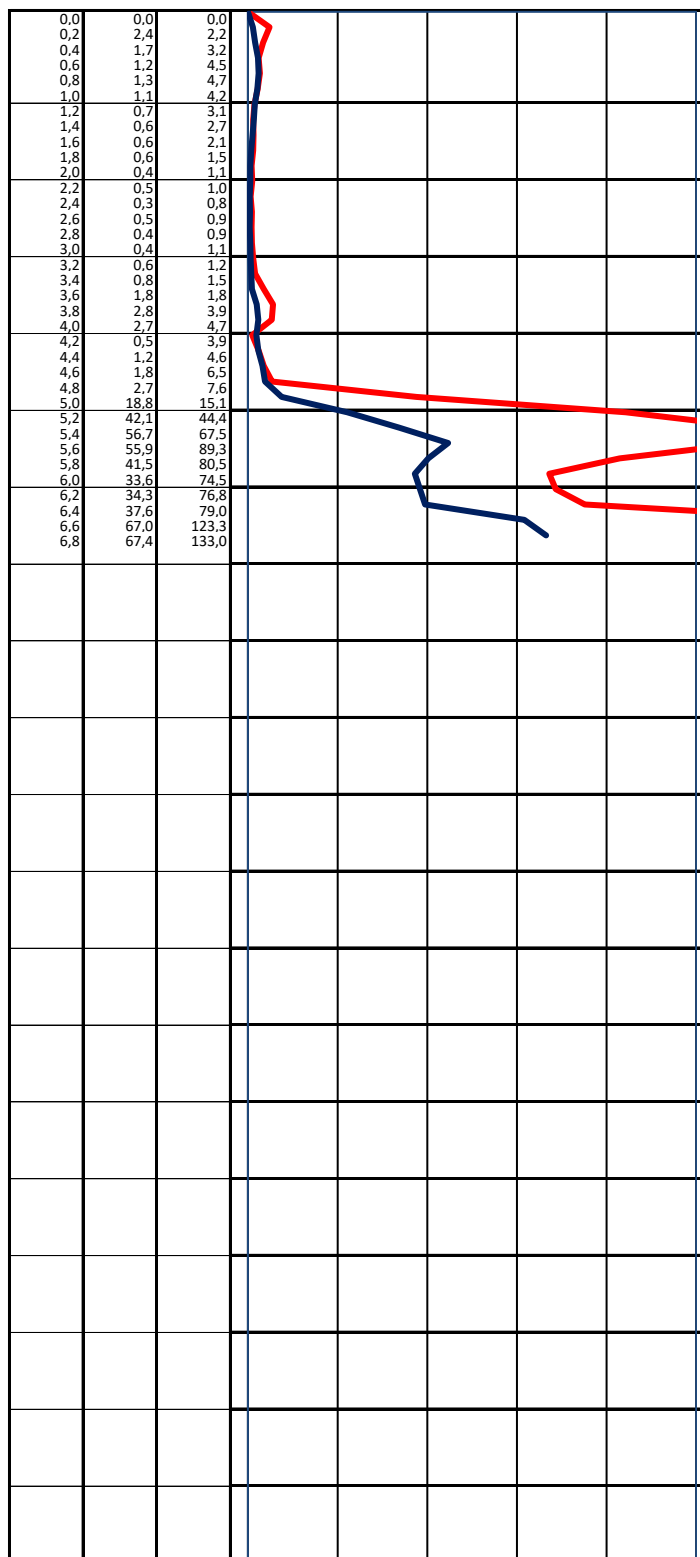

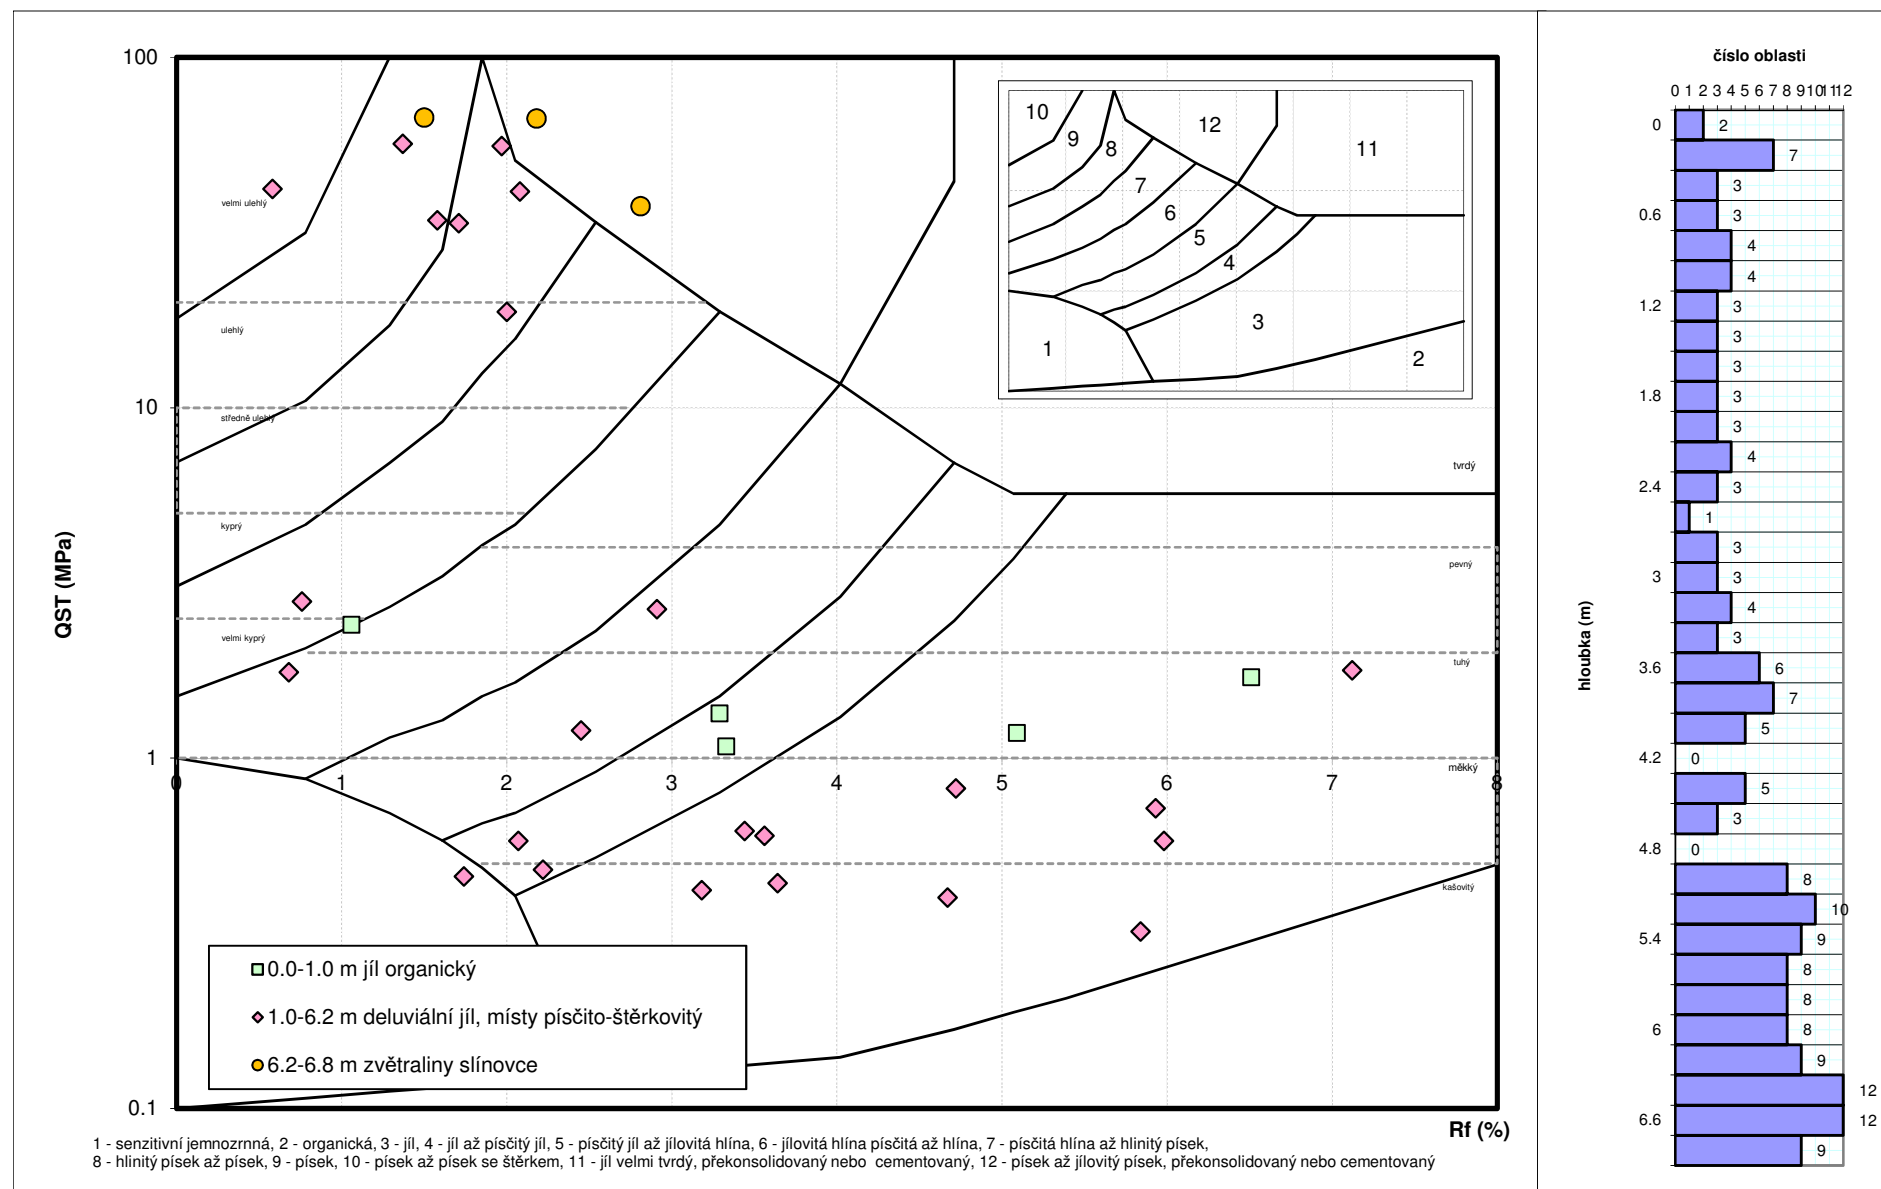






Lokalita	D11 1108 Jaroměř - Trutnov
Zákazník	
Poznámka	použito snižovače
Operátor	
Sonda	SP606
Hloubka pažení	

Datum	9.8.2019
HI vody naražené	
HI vody ustálené	3,7 m
X	
Y	
Z	

hi	QST	QT	0	—	QT	—	200 [kN]
[m]	[Mpa]	[kN]	0	—	qc	—	50 [Mpa]

Rf	FS	0	—	Fs	—	1 [Mpa]
%	[Mpa]	0	—	Rf	—	25 [%]

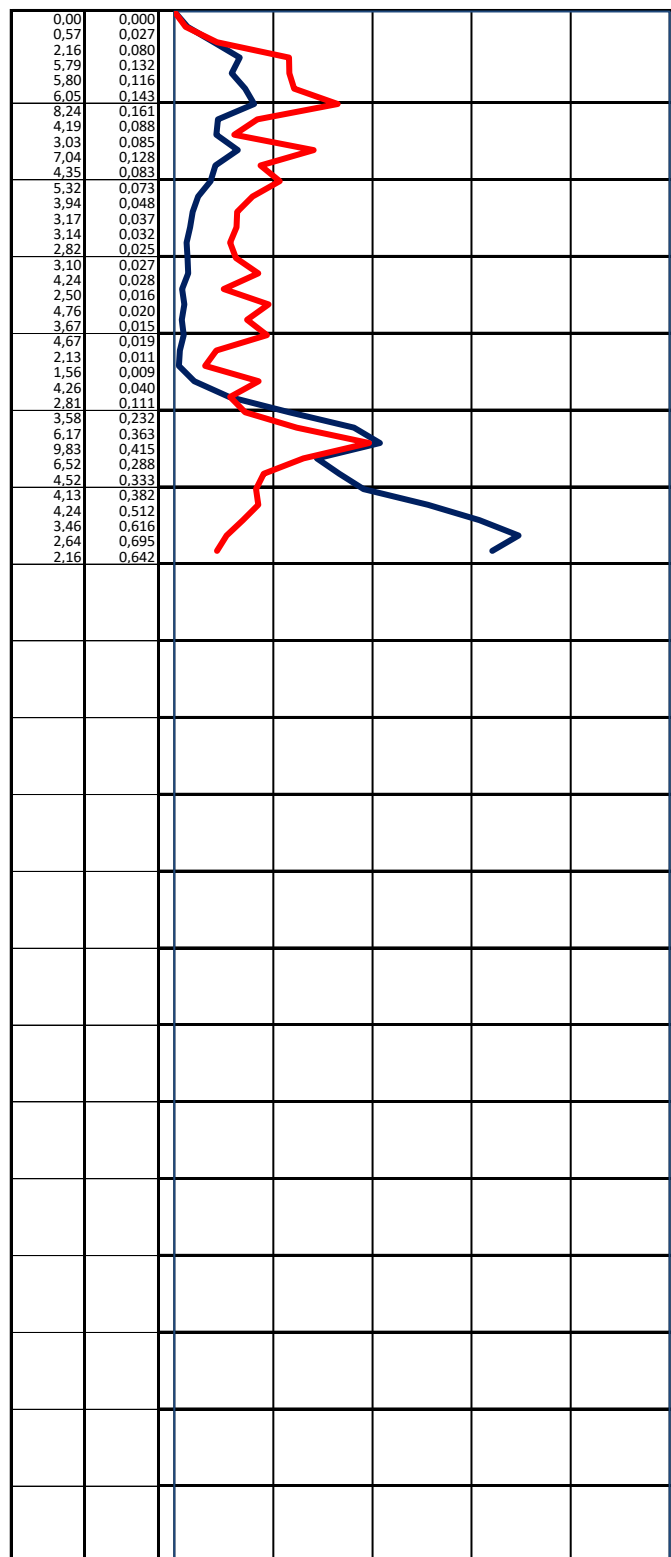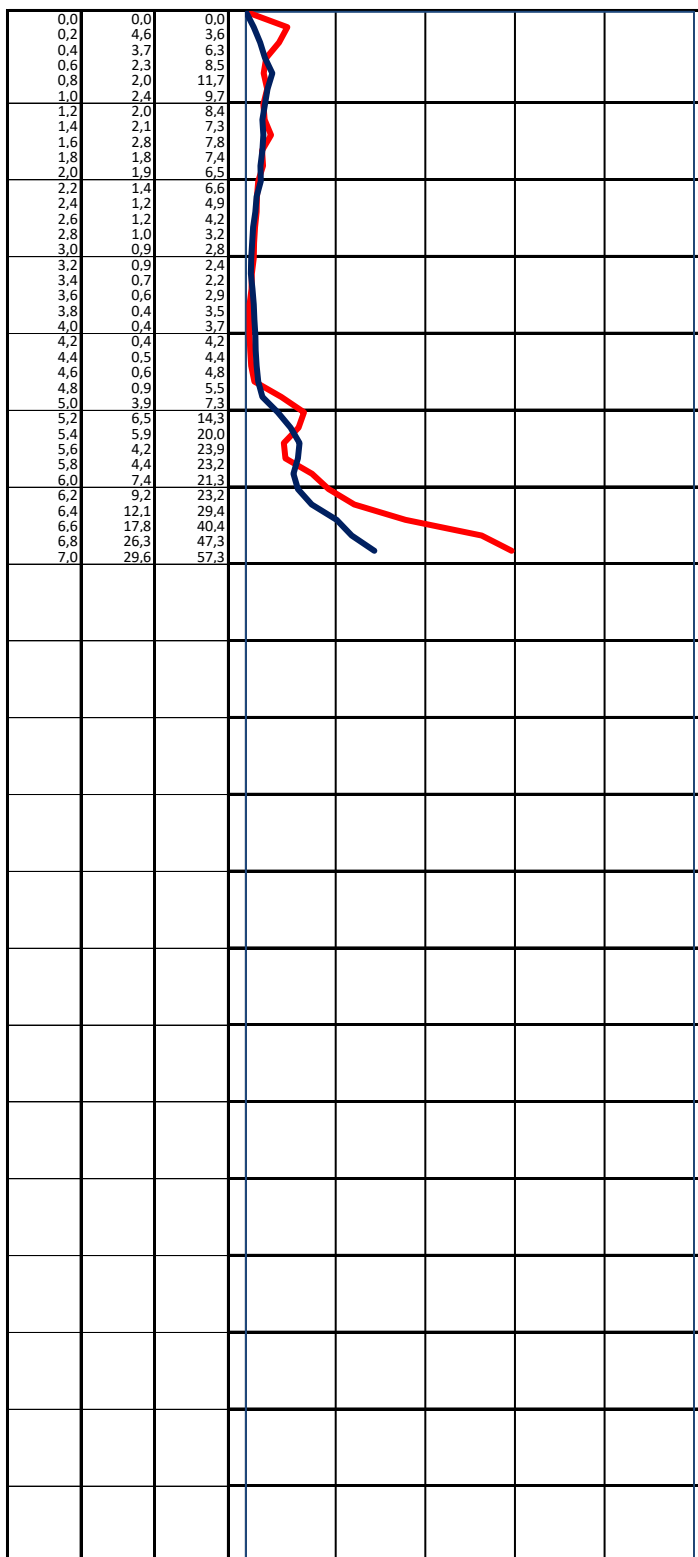

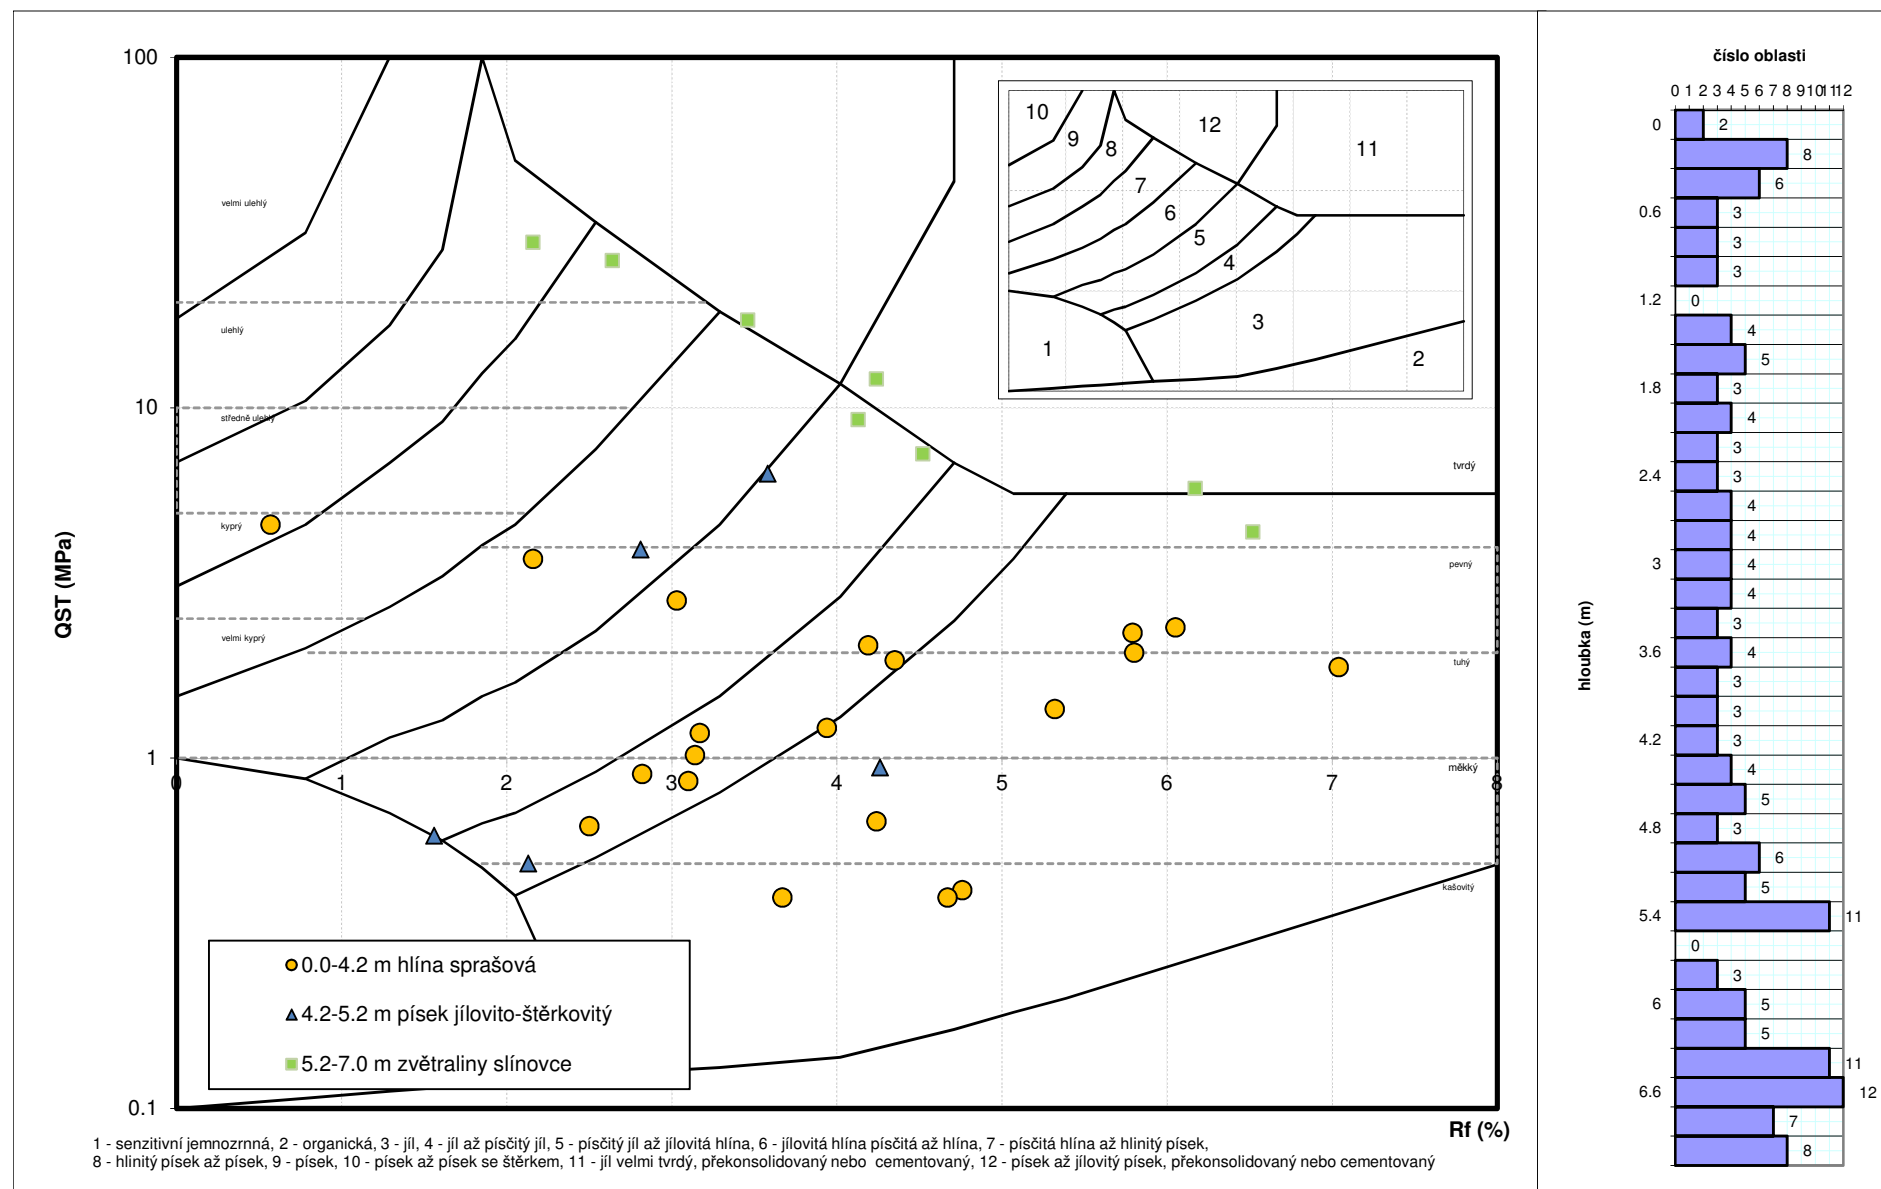






Lokalita	D11 1108 Jaroměř - Trutnov
Zákazník	
Poznámka	použito snížovače
Operátor	
Sonda	SP611
Hloubka pažení	

Datum	9.8.2019
HI vody naražené	
HI vody ustálené	suchá
X	
Y	
Z	

hi	QST	QT	0	—	QT	—	200 [kN]
[m]	[Mpa]	[kN]	0	—	qc	—	50 [Mpa]

Rf	FS	0	—	Fs	—	1 [Mpa]
%	[Mpa]	0	—	Rf	—	25 [%]

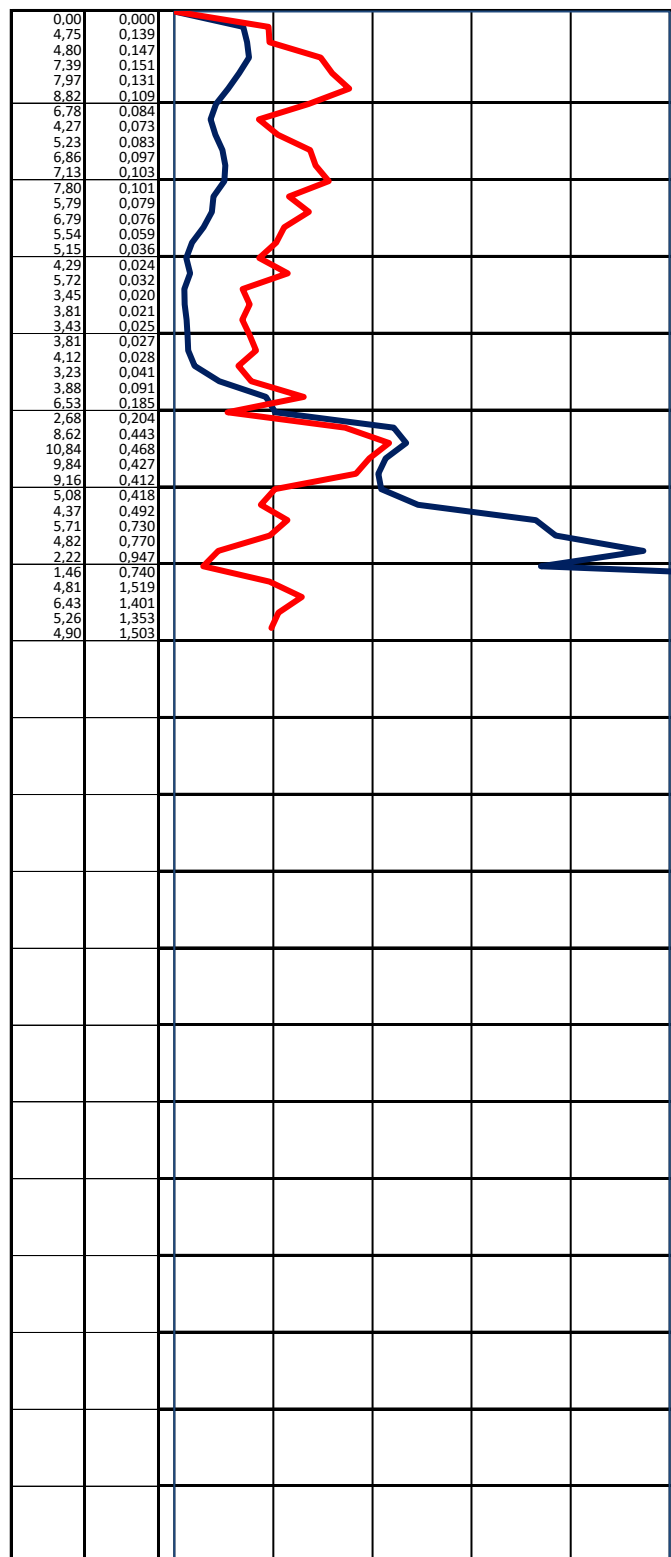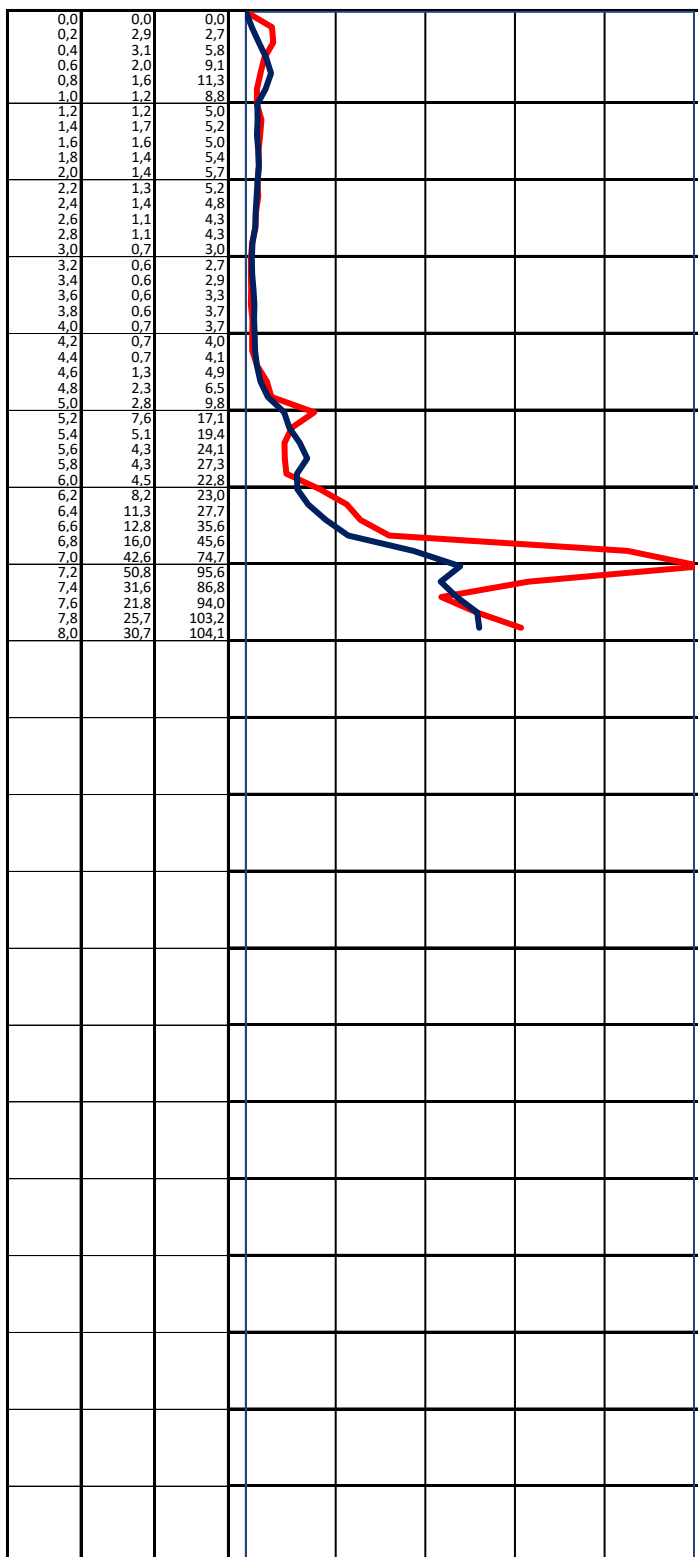

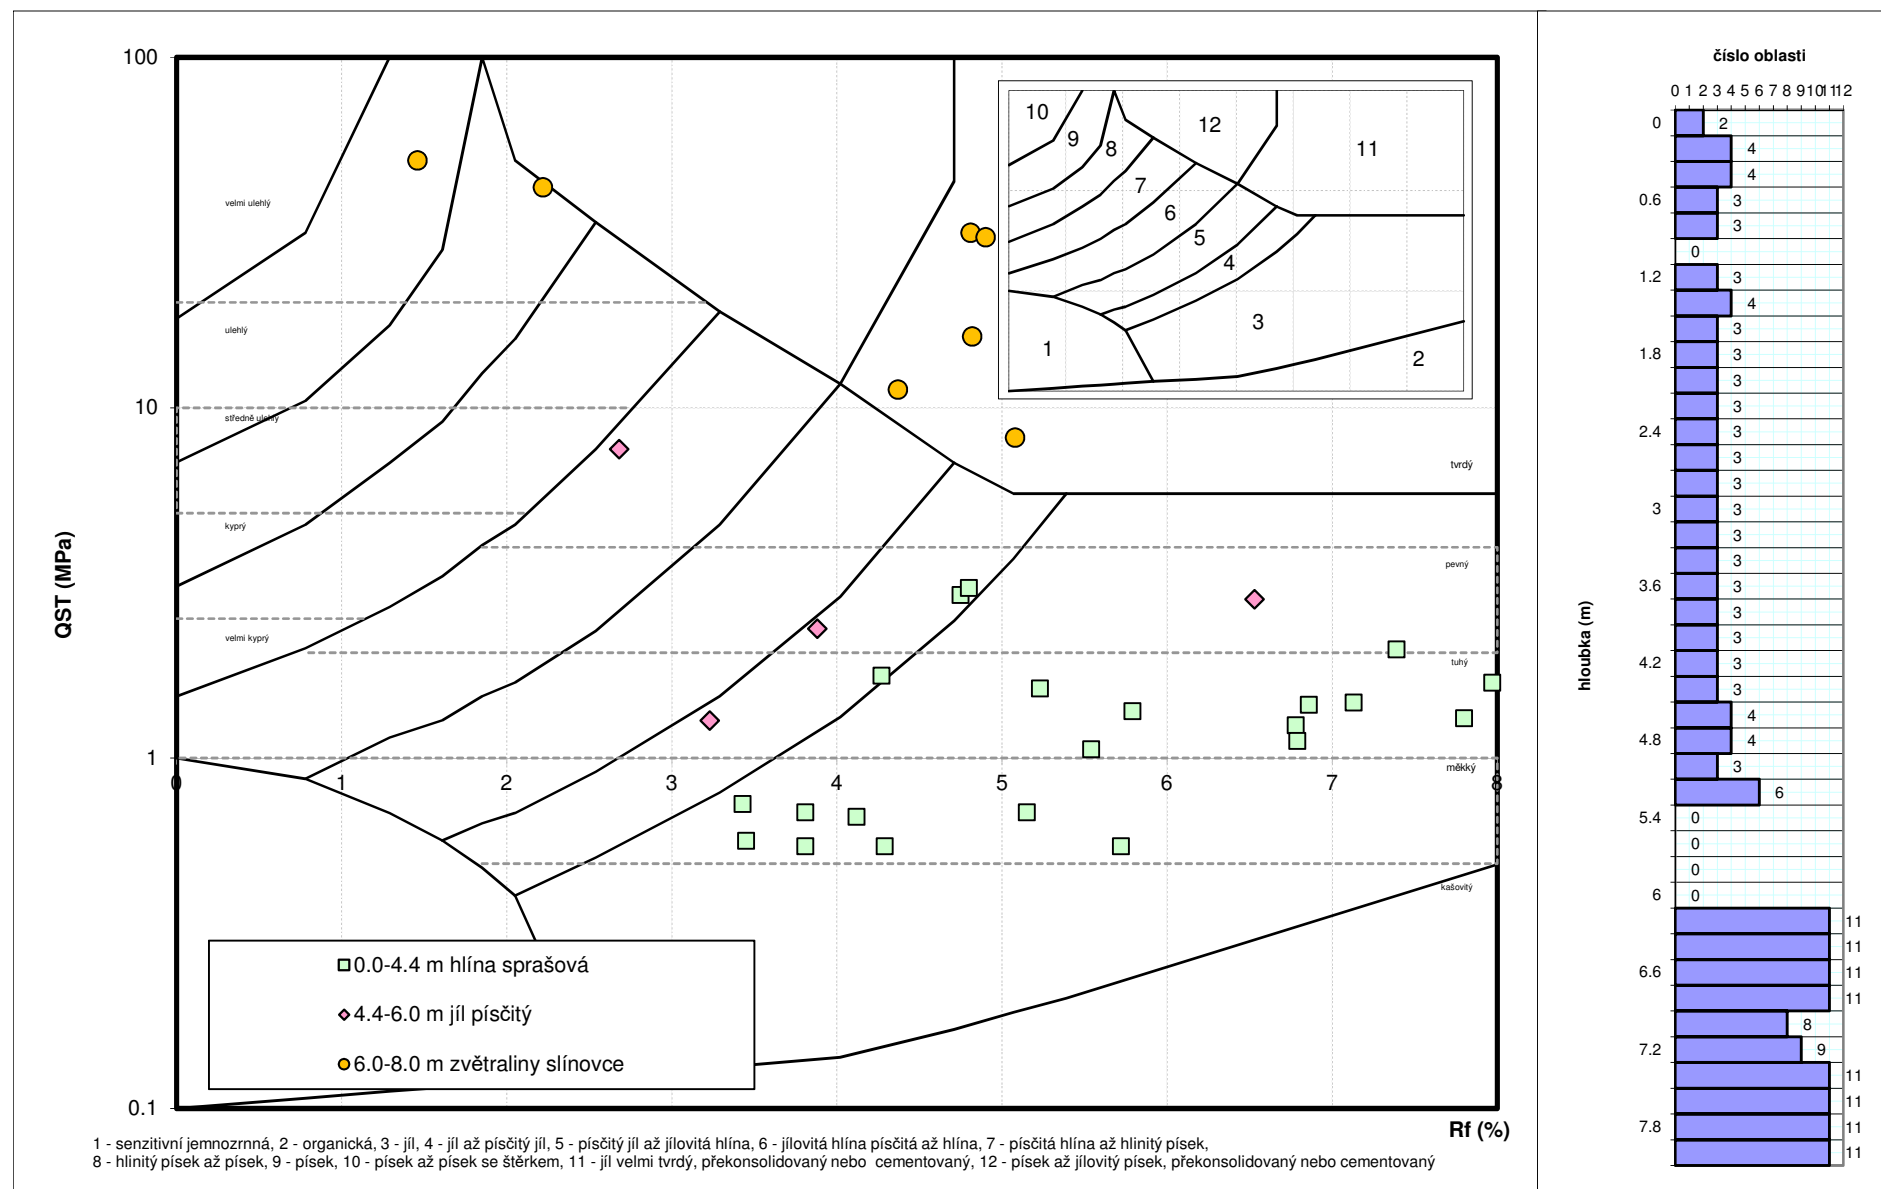






Lokalita	D11 1108 Jaroměř - Trutnov
Zákazník	
Poznámka	použito snížovače
Operátor	
Sonda	SP616
Hloubka pažení	

Datum	9.8.2019
HI vody naražené	
HI vody ustálené	1,6 m zavaleno
X	
Y	
Z	

hi	QST	QT	0		QT		200 [kN]
[m]	[Mpa]	[kN]	0		qc		50 [Mpa]

Rf	FS	0		Fs		1 [Mpa]
%	[Mpa]	0		Rf		25 [%]

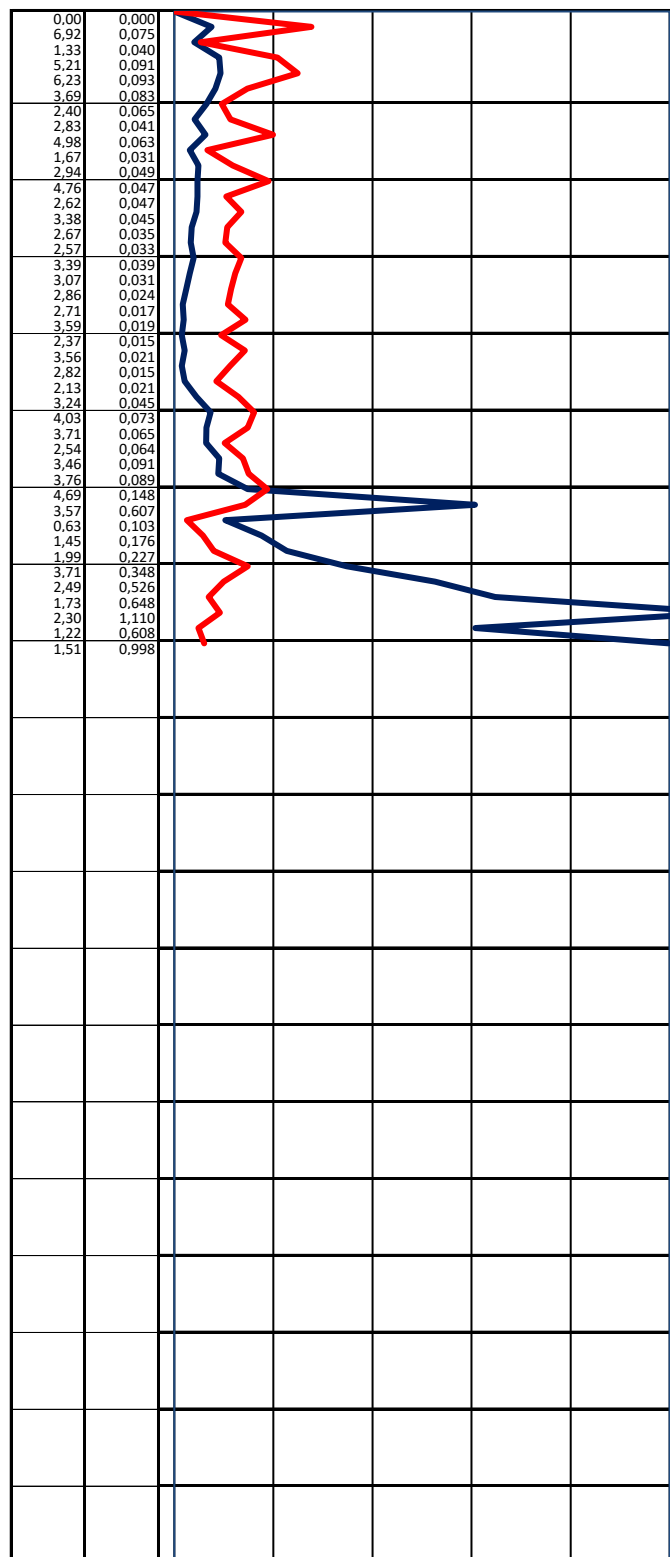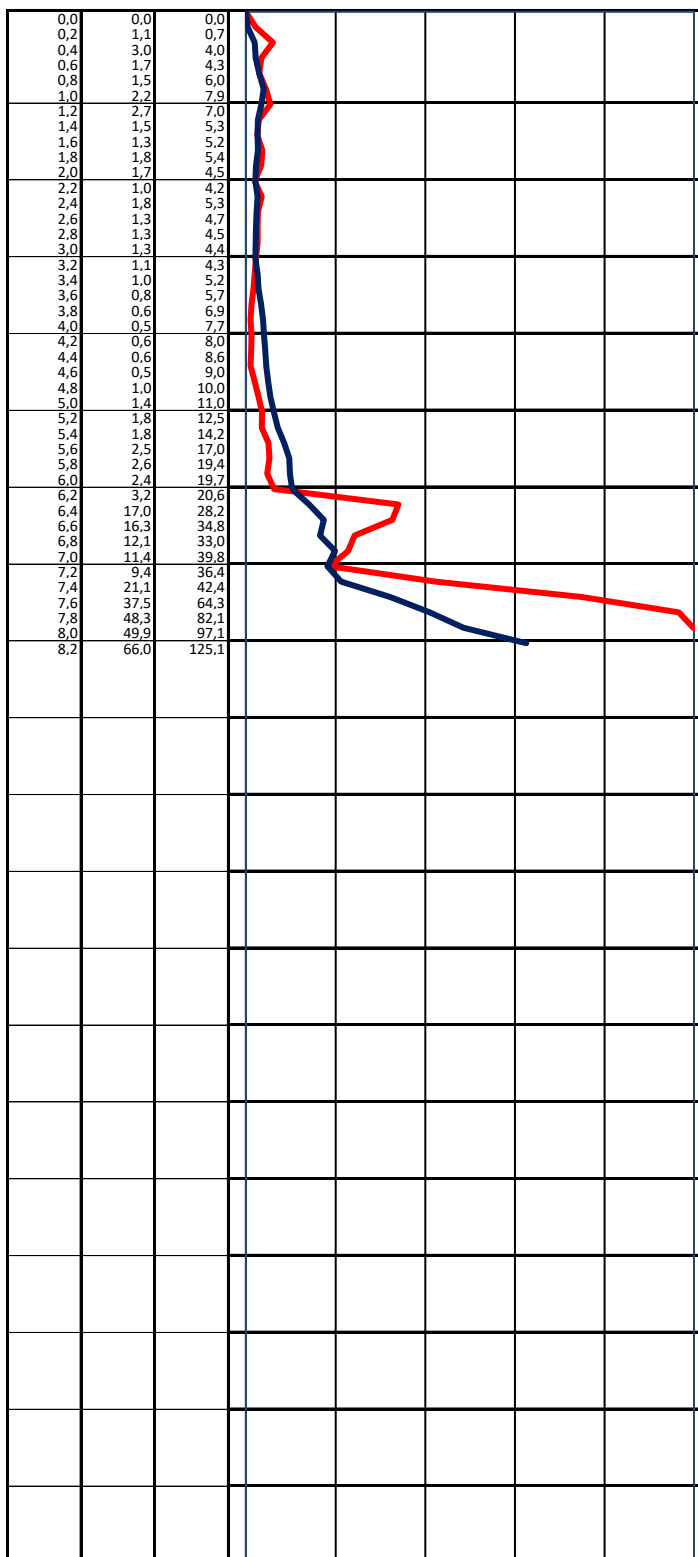

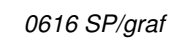






Lokalita	D11 1108 Jaroměř - Trutnov
Zákazník	
Poznámka	použito snížovače
Operátor	
Sonda	SP624
Hloubka pažení	

Datum	9.8.2019
Hl vody naražené	
Hl vody ustálené	3,9 m
X	
Y	
Z	

hl	QST	QT	0	—	QT	—	200 [kN]
[m]	[Mpa]	[kN]	0	—	qc	—	50 [Mpa]

Rf	FS	0	—	Fs	—	1 [Mpa]
%	[Mpa]	0	—	Rf	—	25 [%]

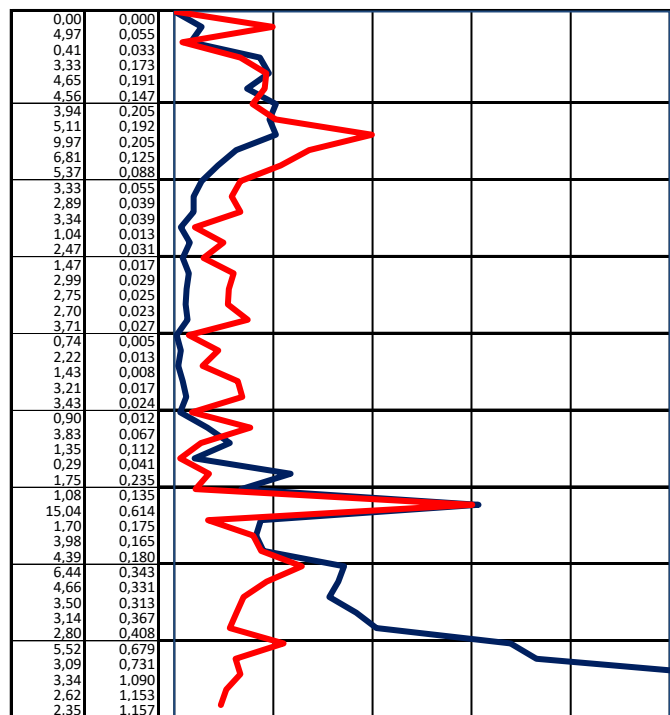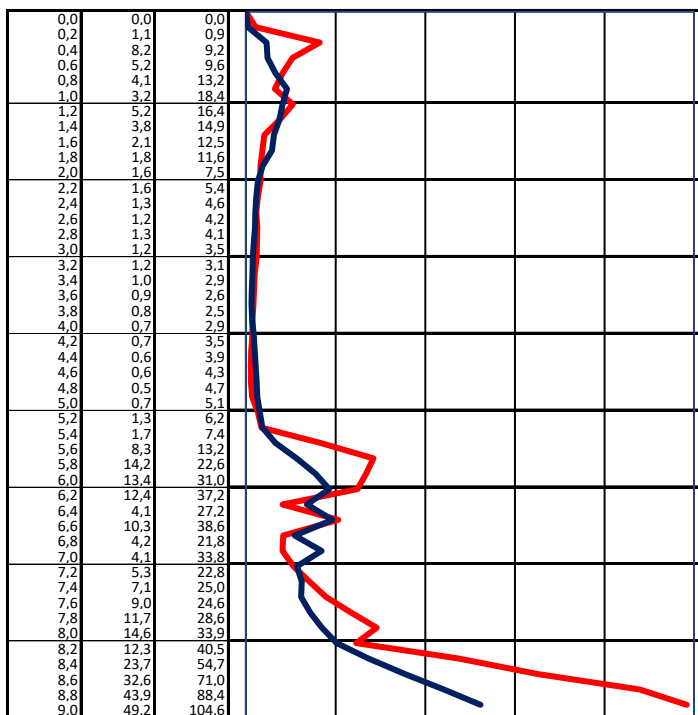

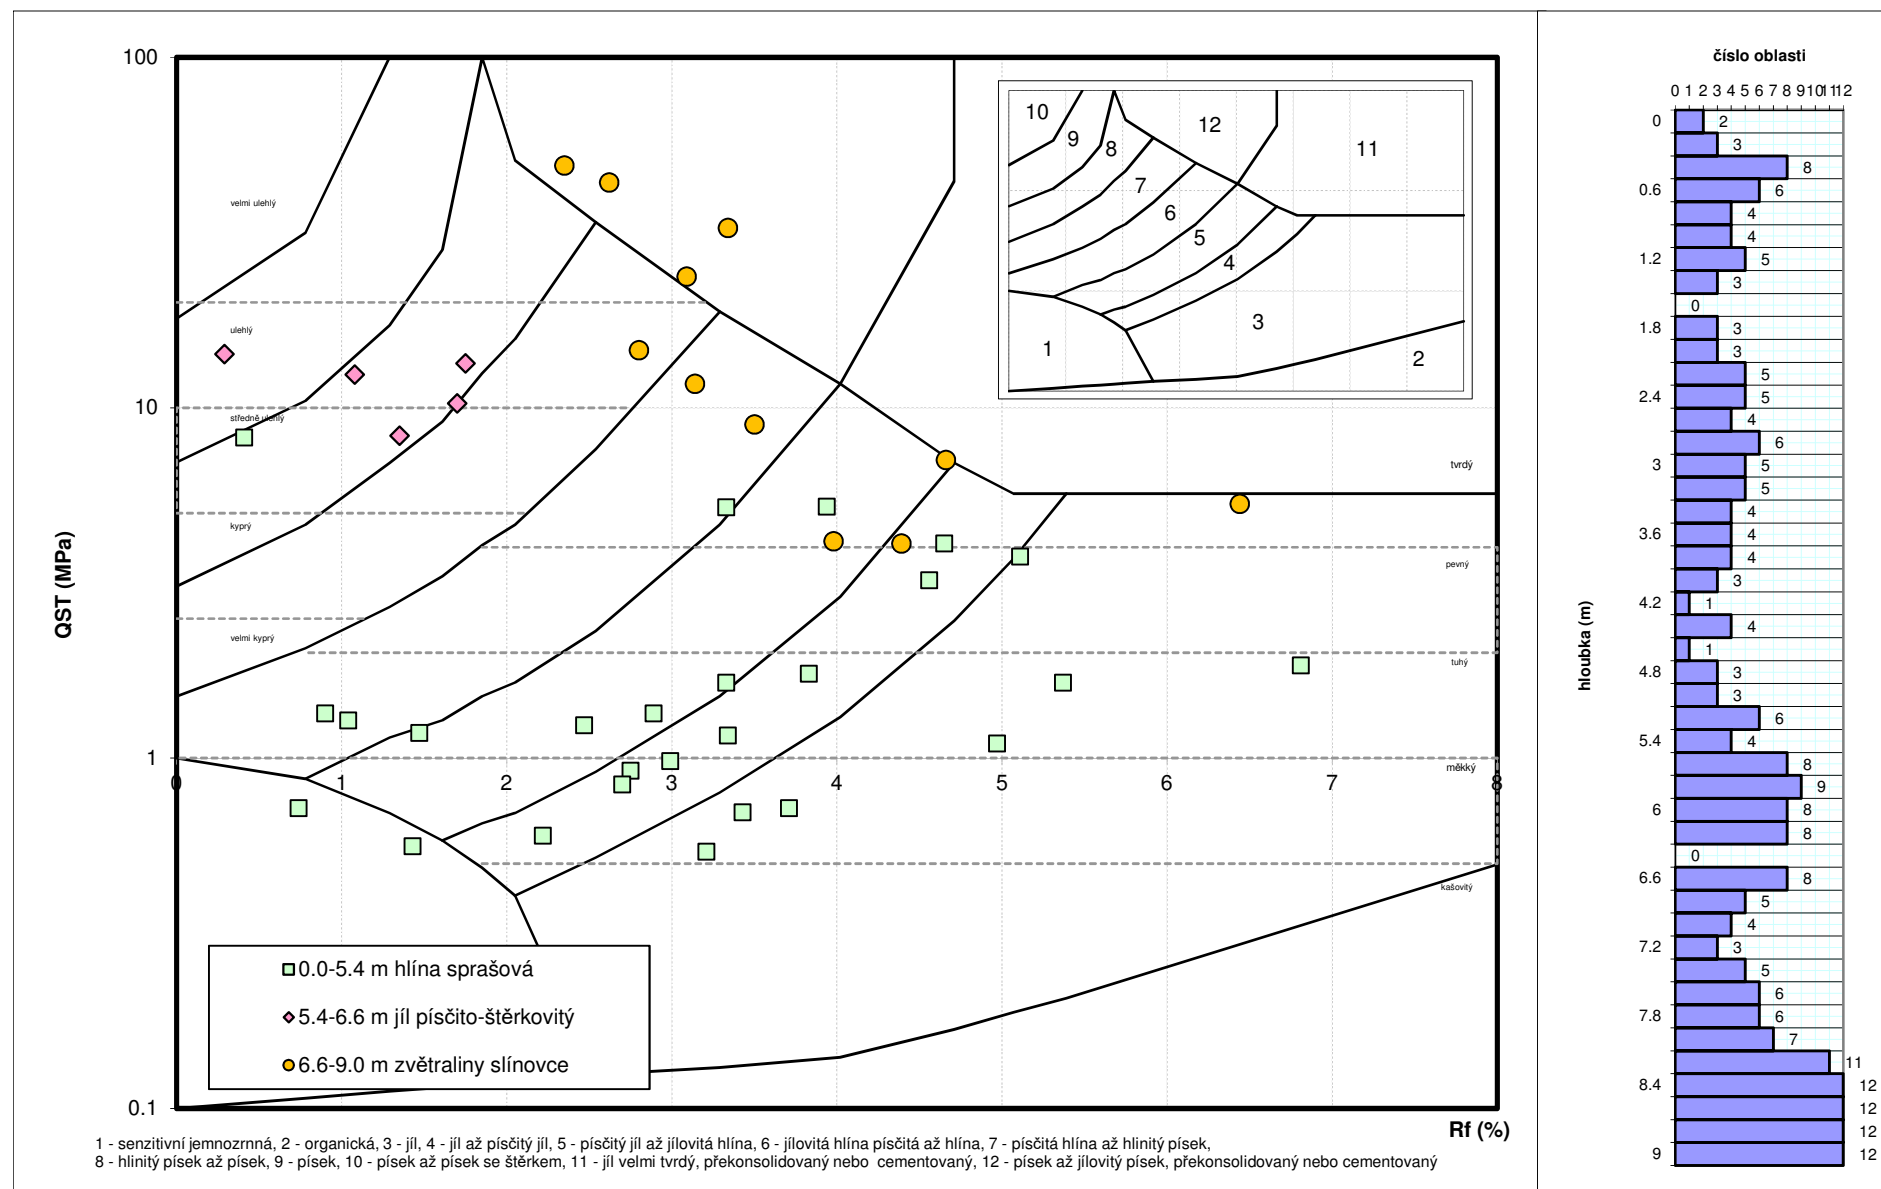






Lokalita	D11 1108 Jaroměř - Trutnov
Zákazník	
Poznámka	použito snížovače
Operátor	
Sonda	SP633
Hloubka pažení	

Datum	9.8.2019
Hl vody naražené	
Hl vody ustálené	8,7 m
X	
Y	
Z	

hl	QST	QT	0	—	QT	—	200 [kN]
[m]	[Mpa]	[kN]	0	—	qc	—	50 [Mpa]

Rf	FS	0	—	Fs	—	1 [Mpa]
%	[Mpa]	0	—	Rf	—	25 [%]

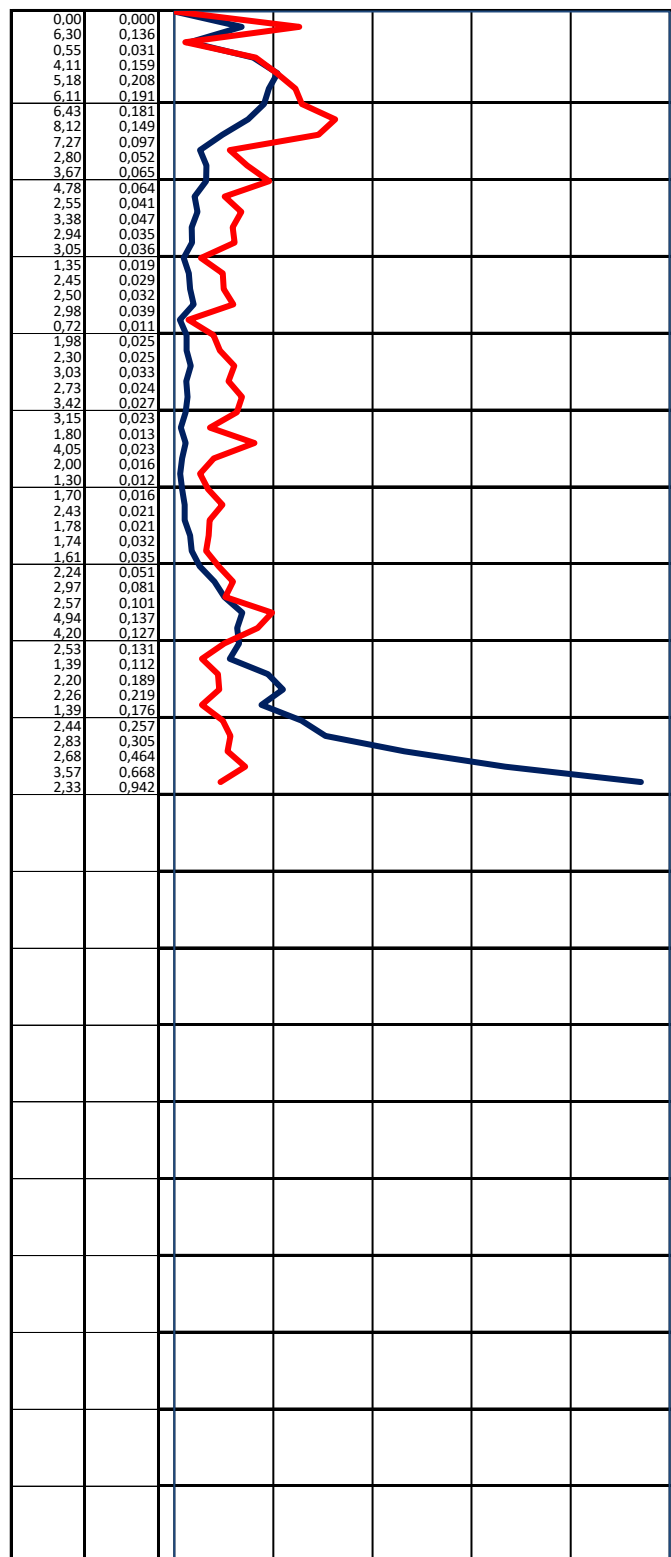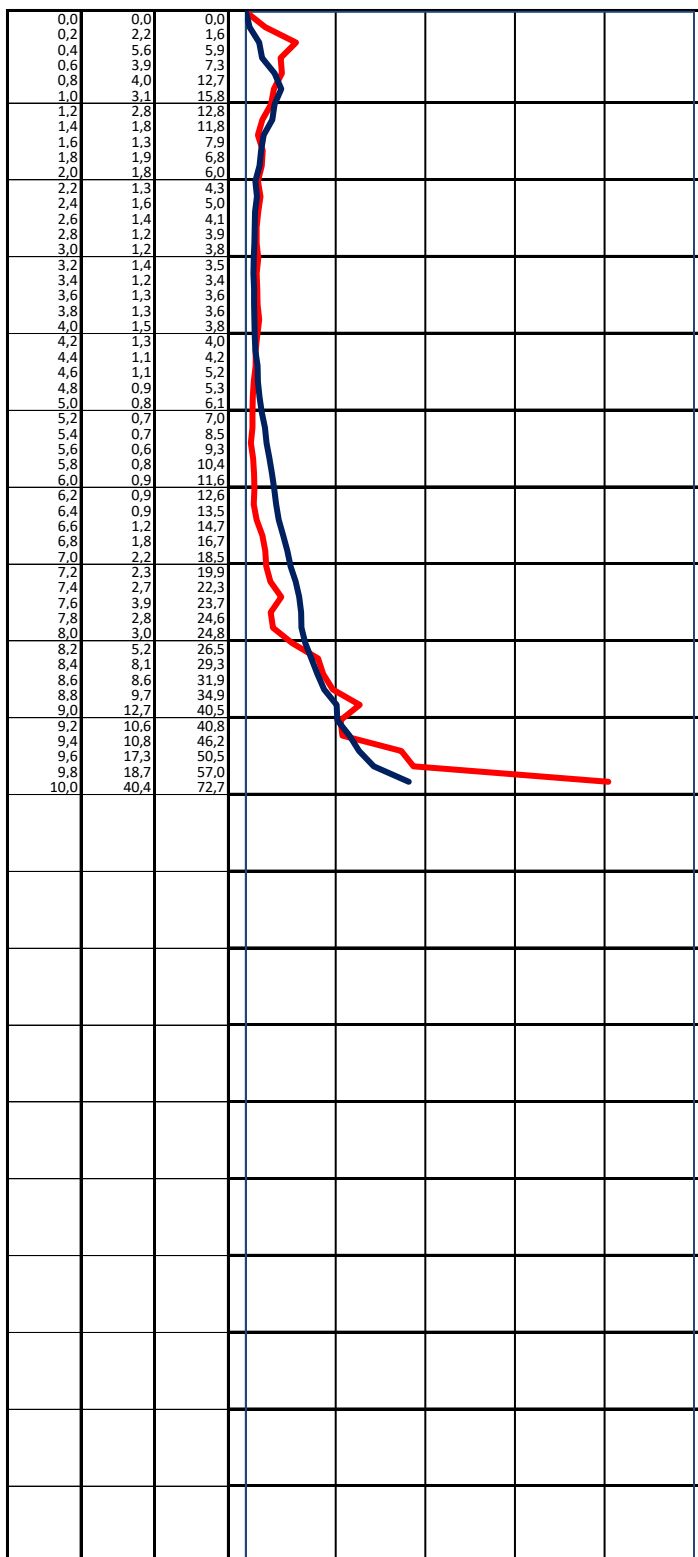

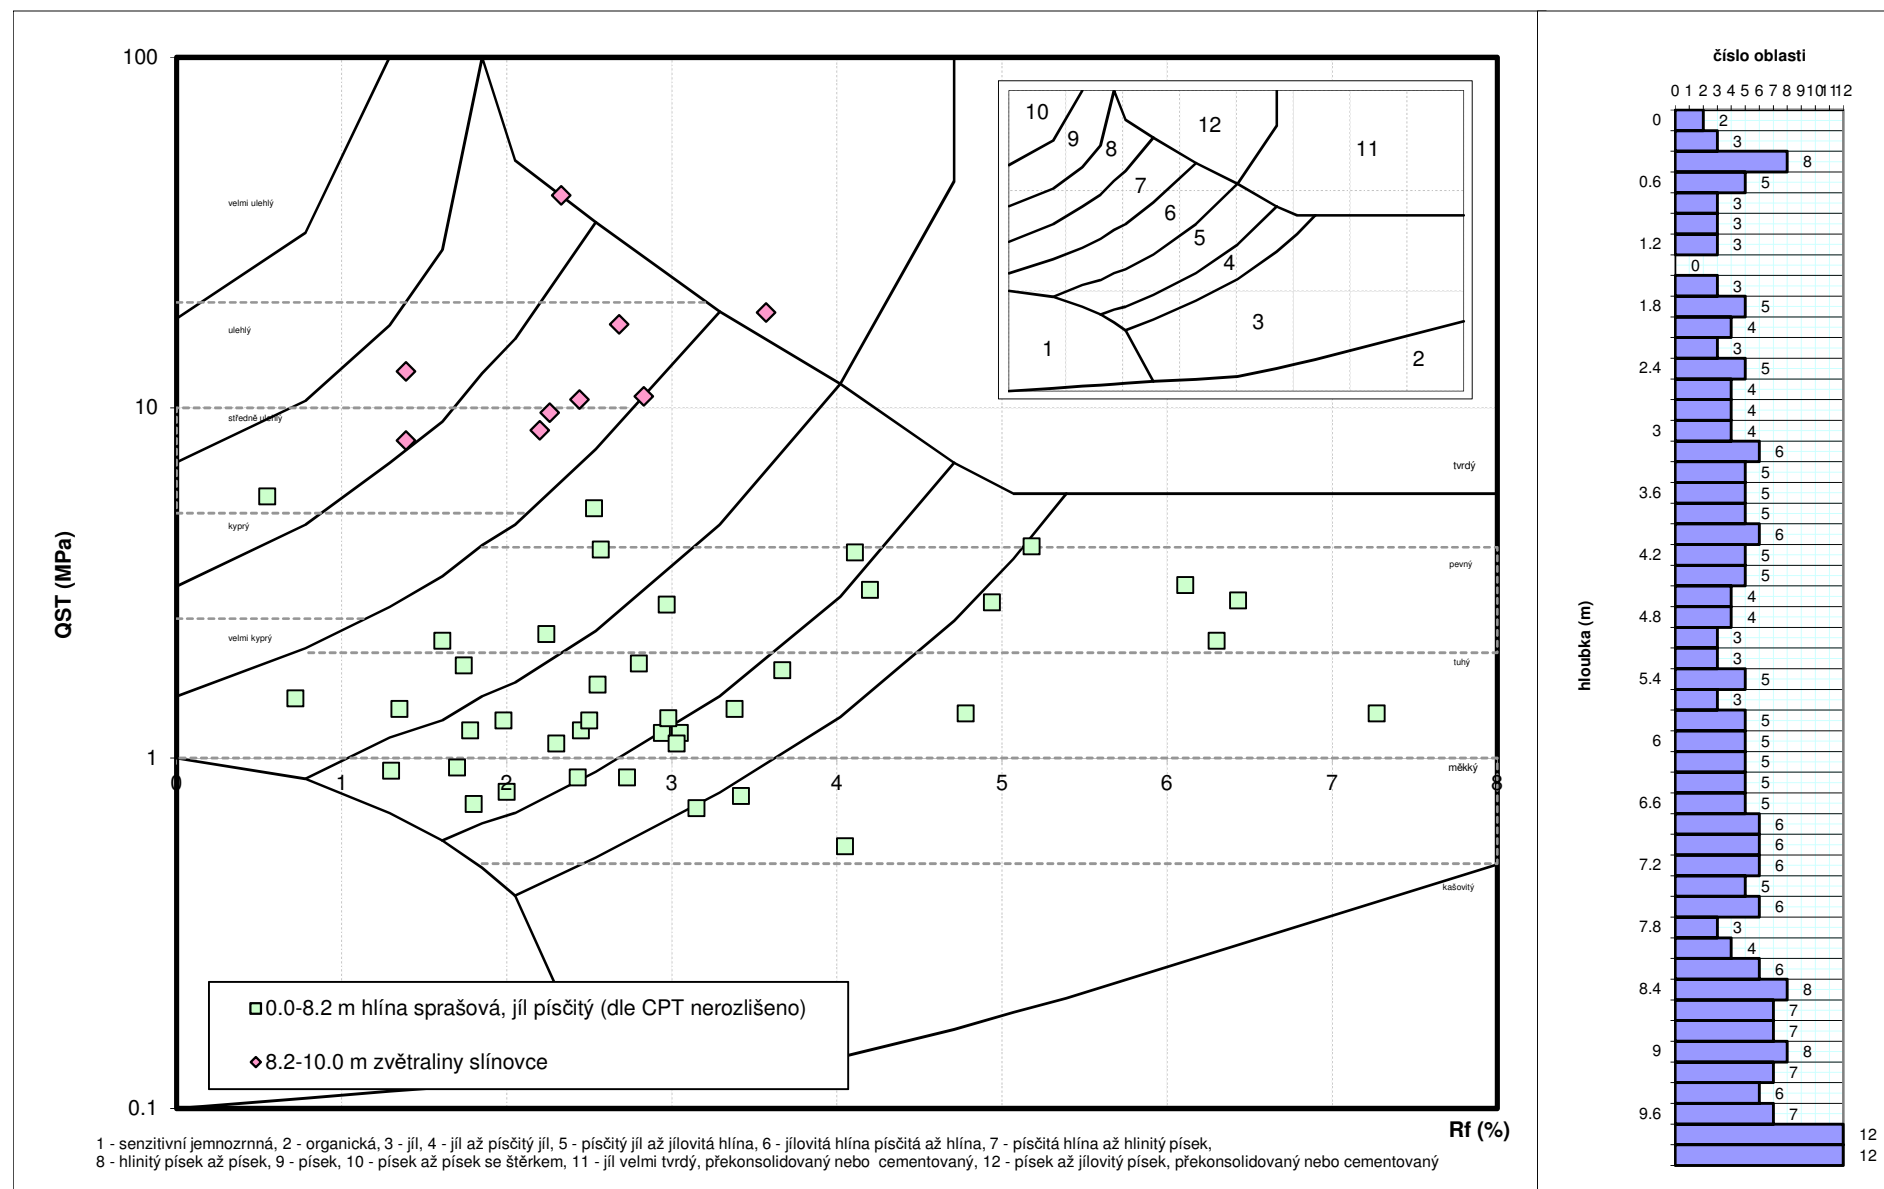






Lokalita	D11 1108 Jaroměř - Trutnov
Zákazník	
Poznámka	použito snížovače
Operátor	
Sonda	SP644
Hloubka pažení	

Datum	9.8.2019
HI vody naražené	
HI vody ustálené	3,7 m zavaleno
X	
Y	
Z	

hi	QST	QT	0		QT		200 [kN]
[m]	[Mpa]	[kN]	0		qc		50 [Mpa]

Rf	FS	0		Fs		1 [Mpa]
%	[Mpa]	0		Rf		25 [%]

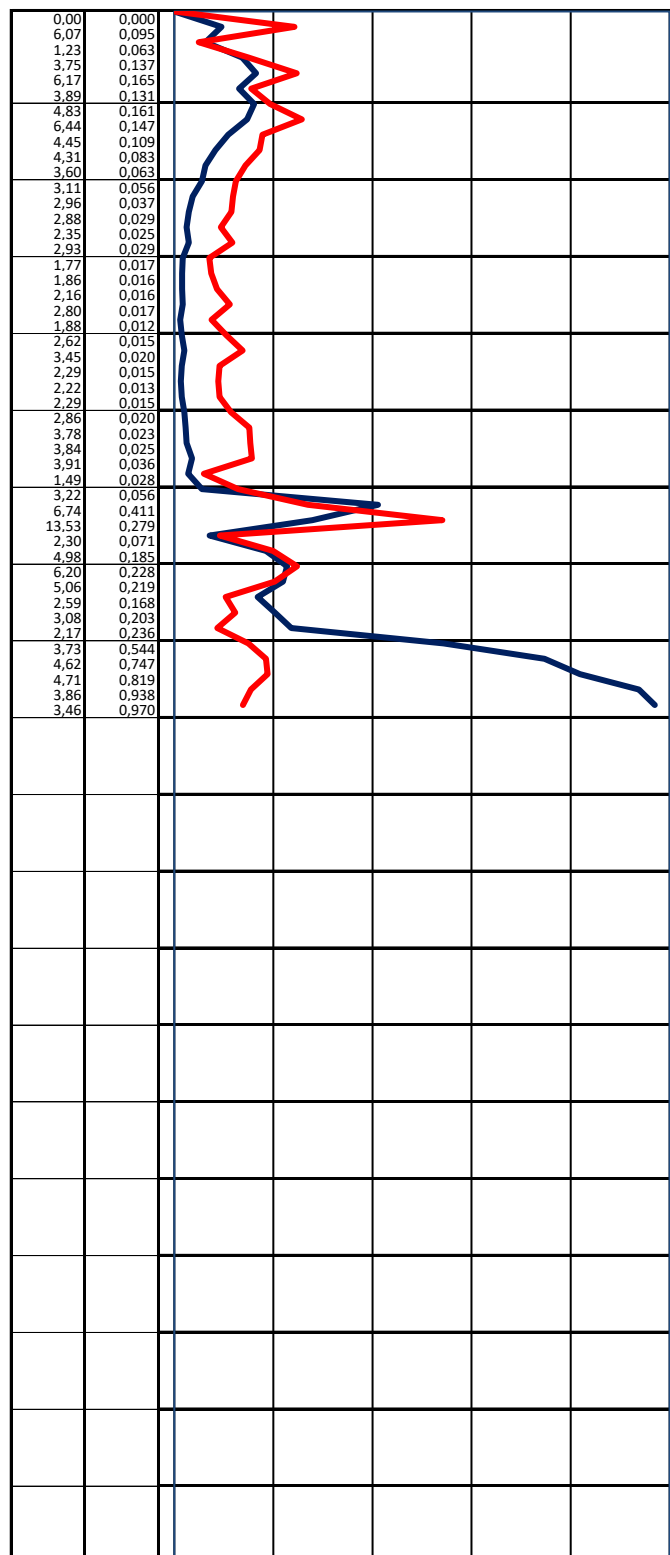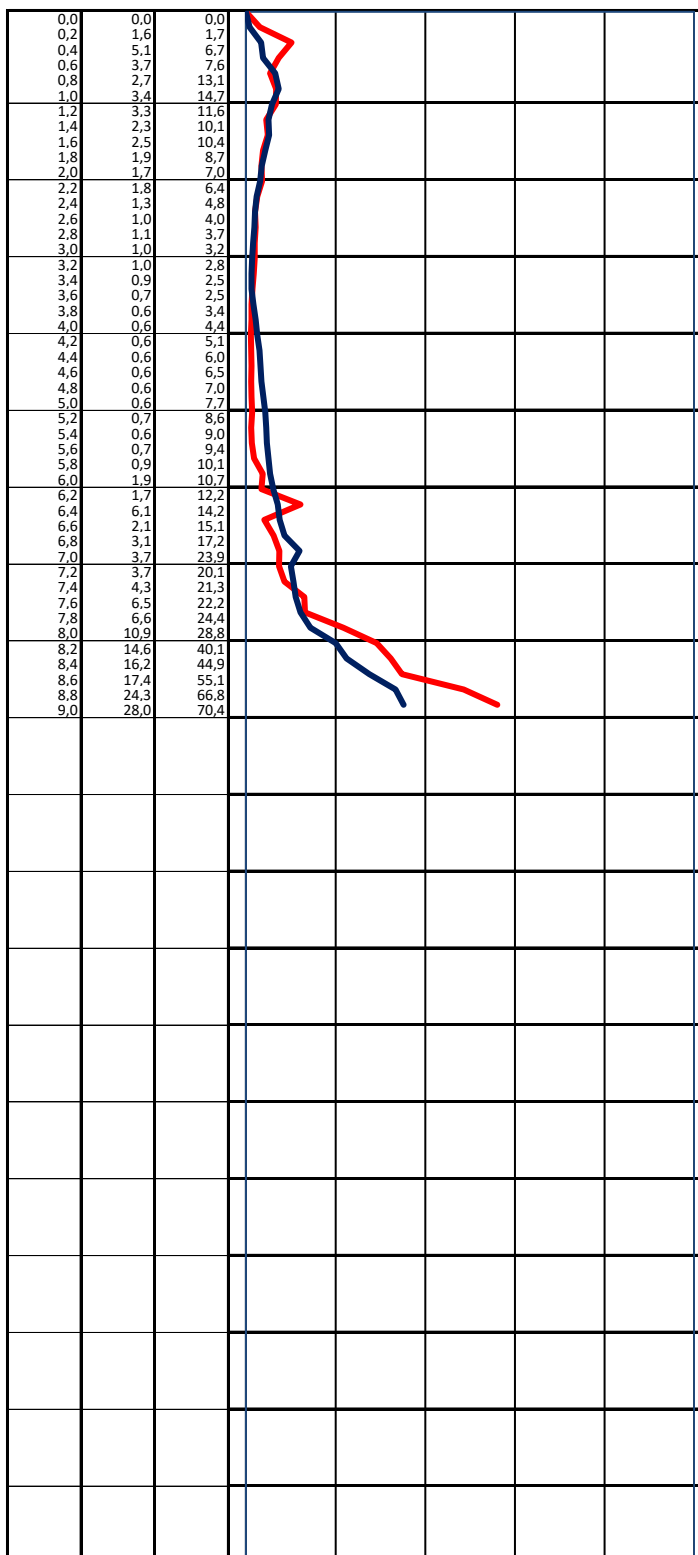

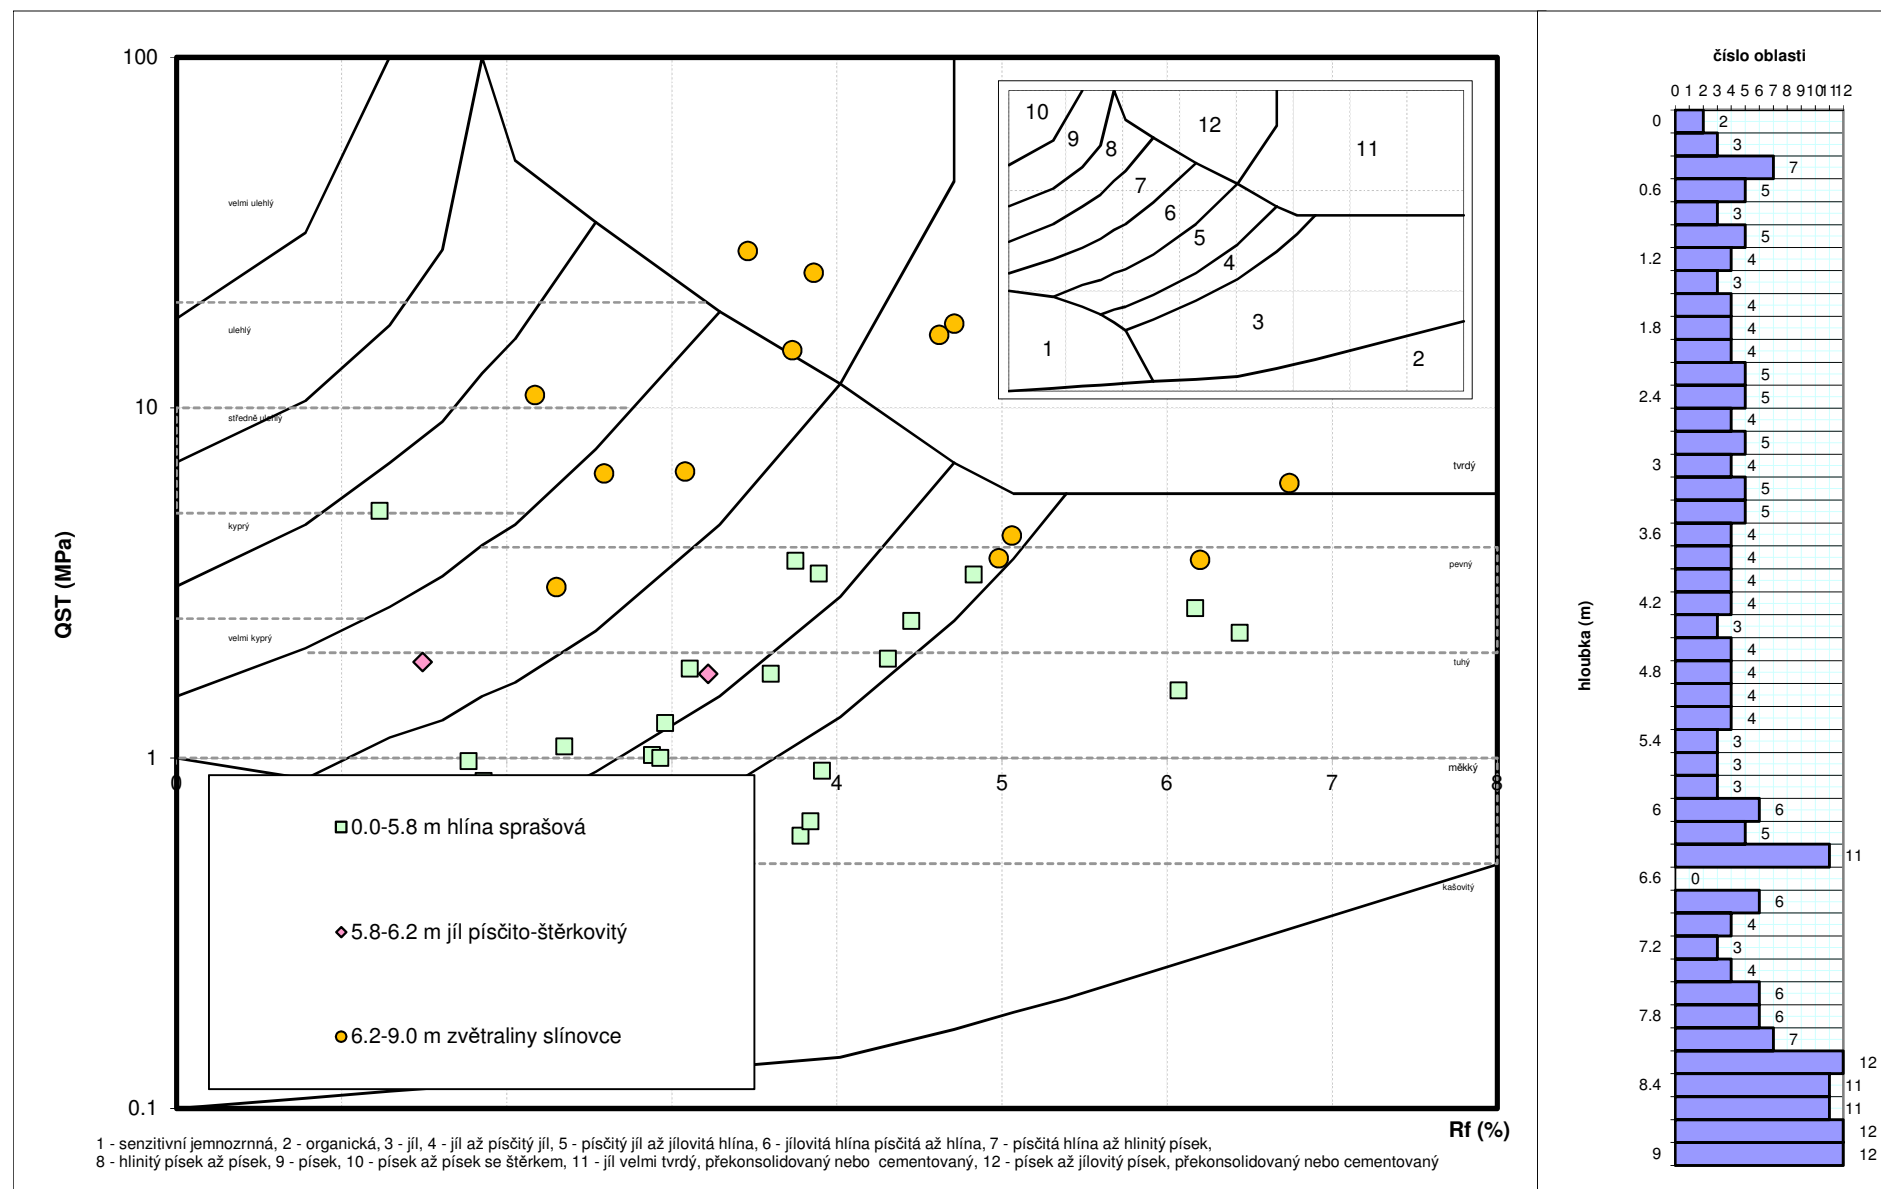






Lokalita	D11 1108 Jaroměř - Trutnov
Zákazník	
Poznámka	použito snížovače
Operátor	
Sonda	SP646
Hloubka pažení	

Datum	9.8.2019
HI vody naražené	
HI vody ustálené	2,5 m
X	
Y	
Z	

hi	QST	QT	0	—	QT	—	200 [kN]
[m]	[Mpa]	[kN]	0	—	qc	—	50 [Mpa]

Rf	FS	0	—	Fs	—	1 [Mpa]
%	[Mpa]	0	—	Rf	—	25 [%]

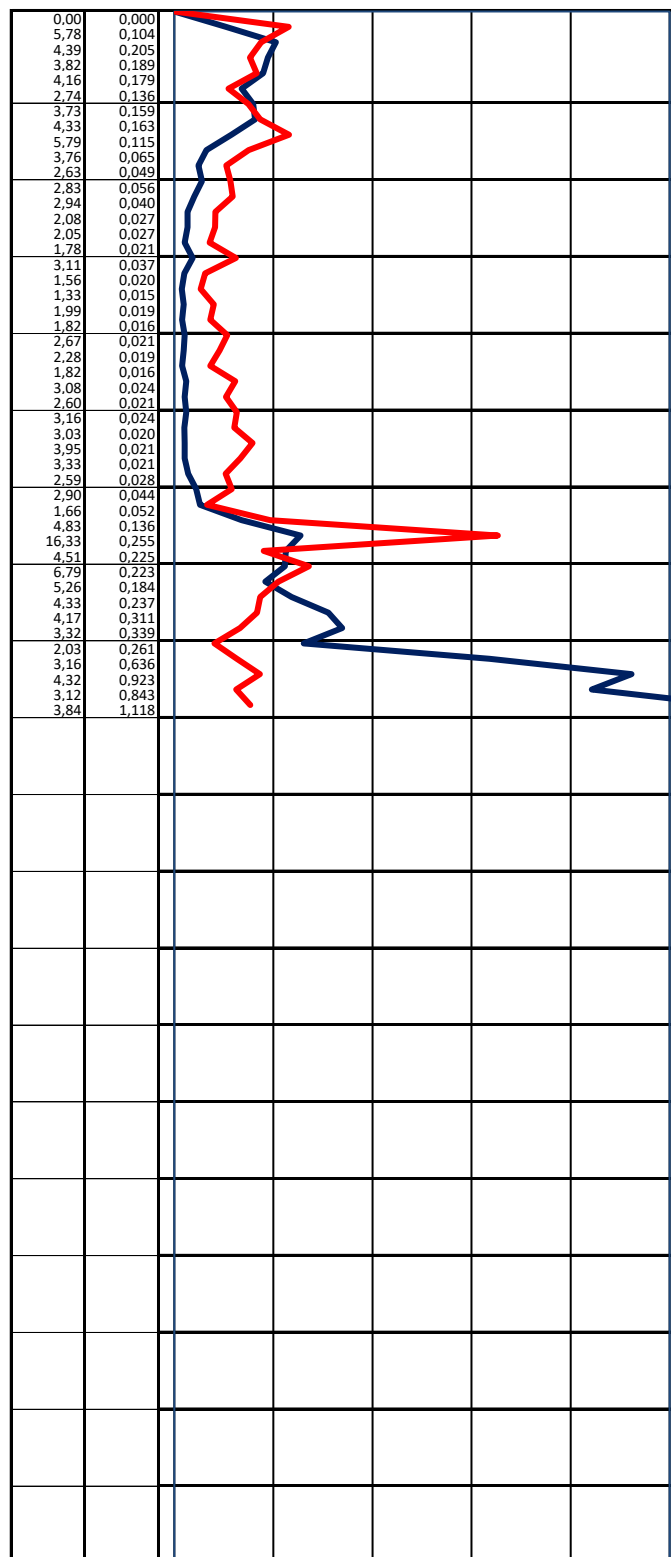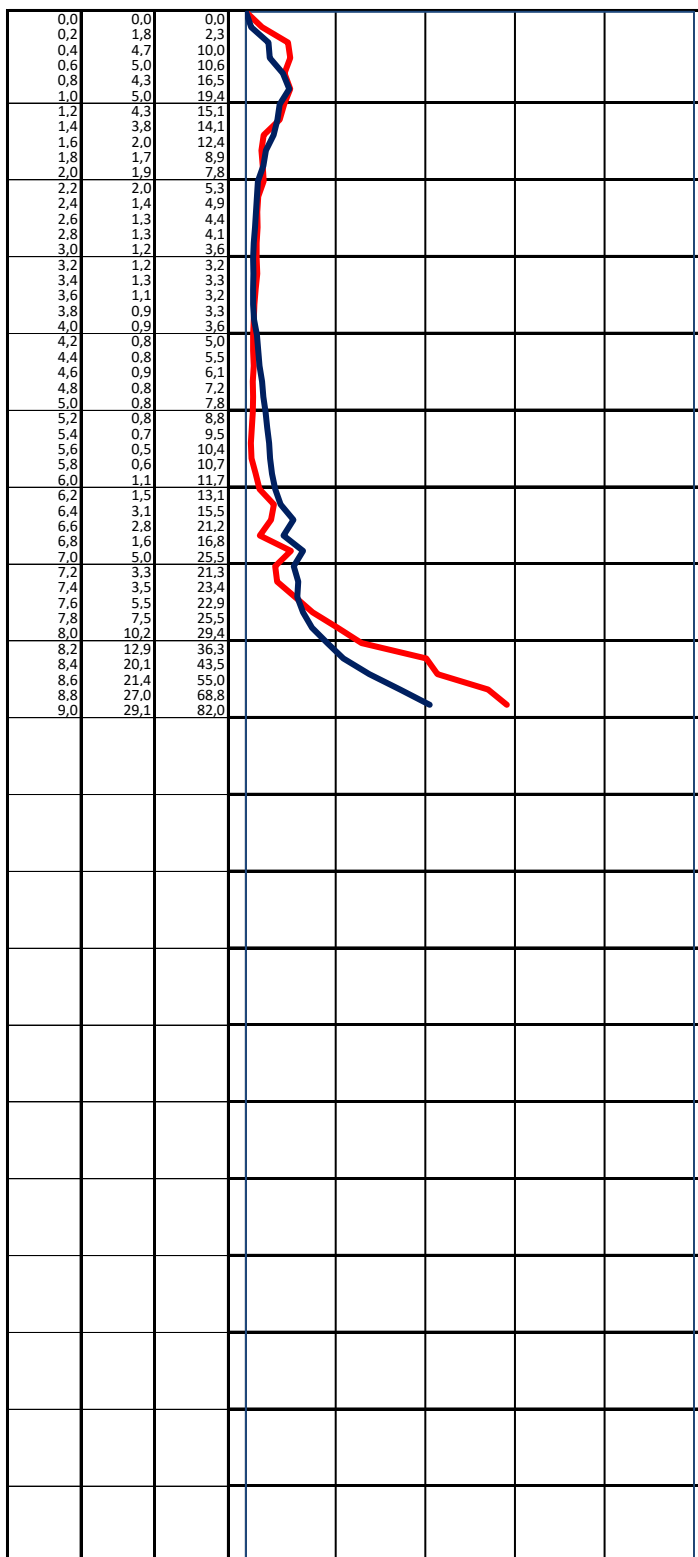

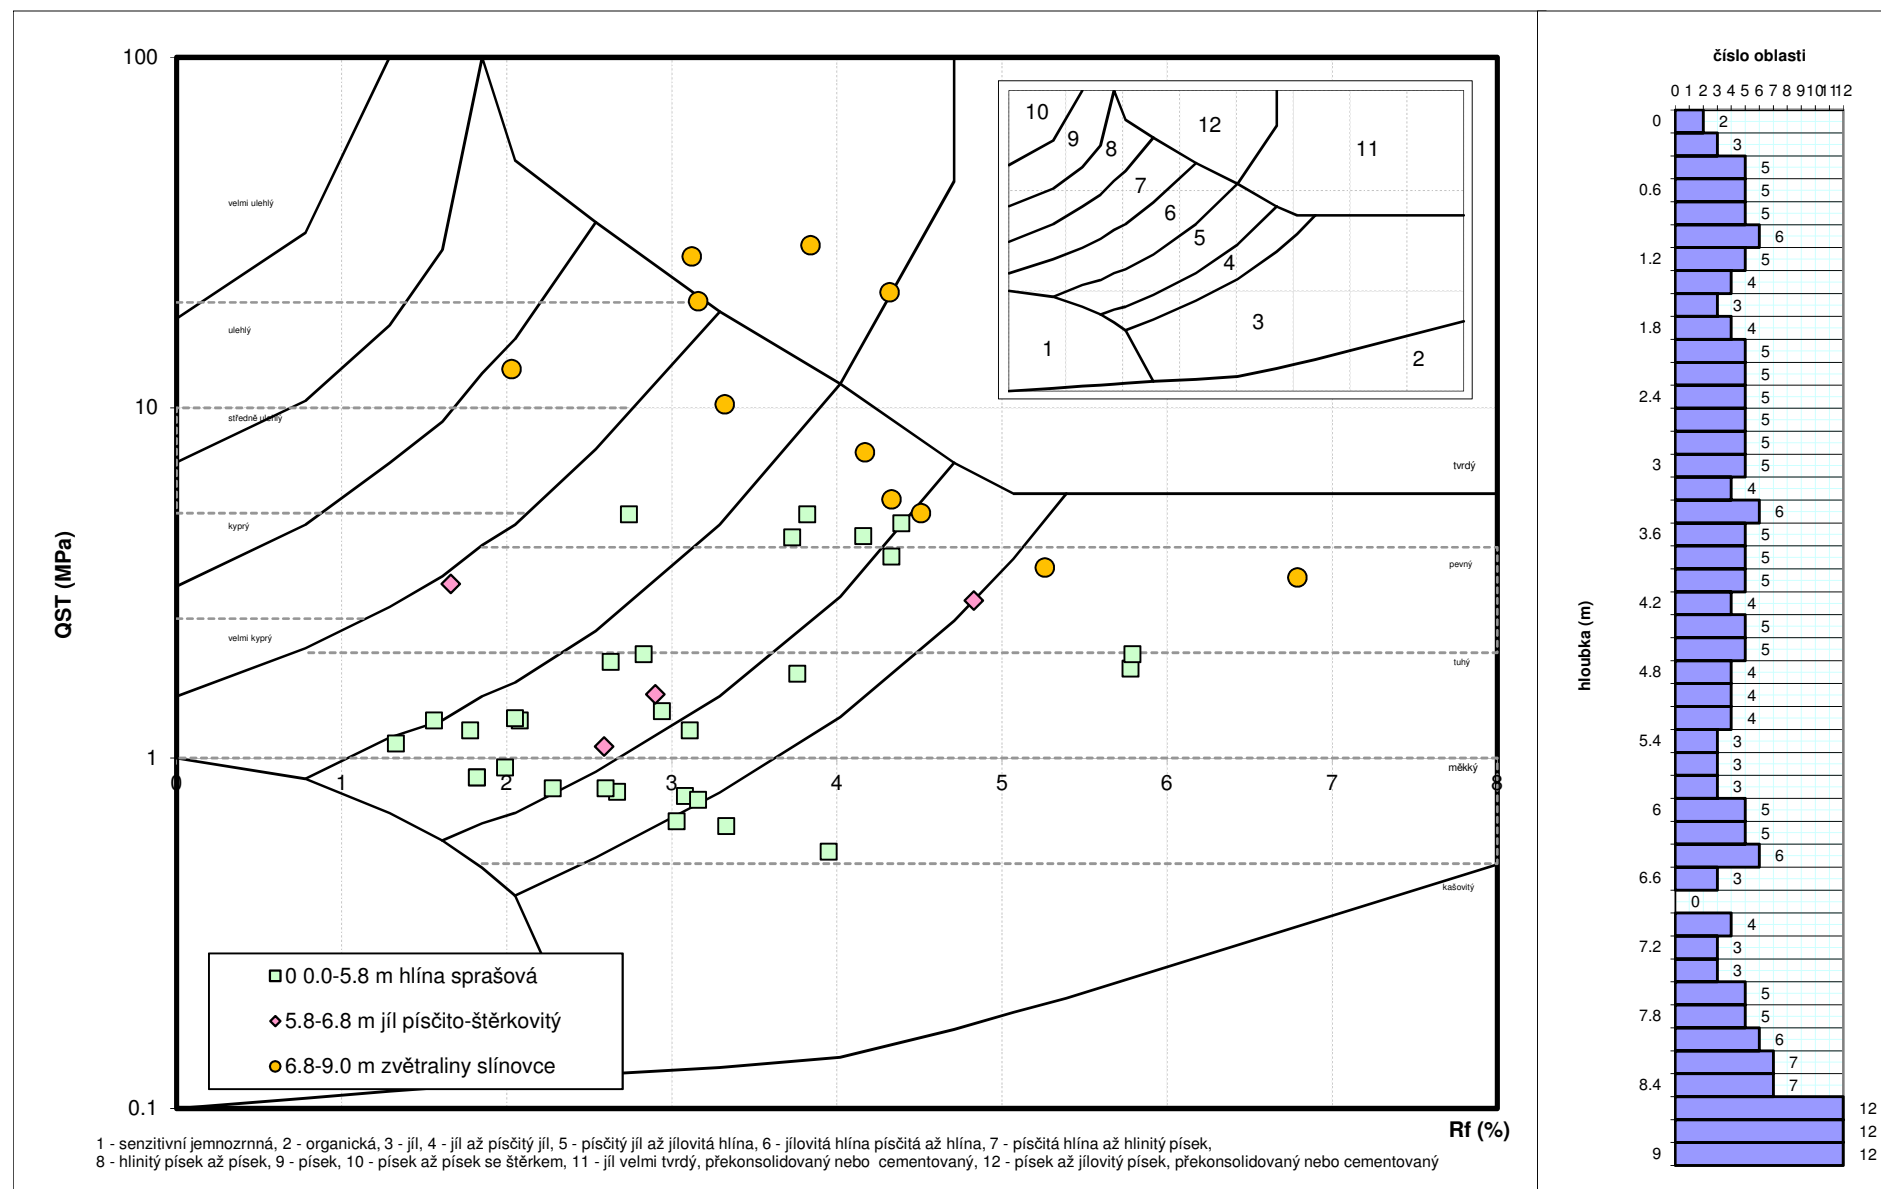






Lokalita	D11a
Zákazník	
Poznámka	použito snižovače
Operátor	
Sonda	SP652
Hloubka pažení	

Datum	9.8.2019
HI vody naražené	
HI vody ustálené	suchá
X	
Y	
Z	

hi	QST	QT	0	—	QT	—	200 [kN]
[m]	[Mpa]	[kN]	0	—	qc	—	50 [Mpa]

Rf	FS	0	—	Fs	—	1 [Mpa]
%	[Mpa]	0	—	Rf	—	25 [%]

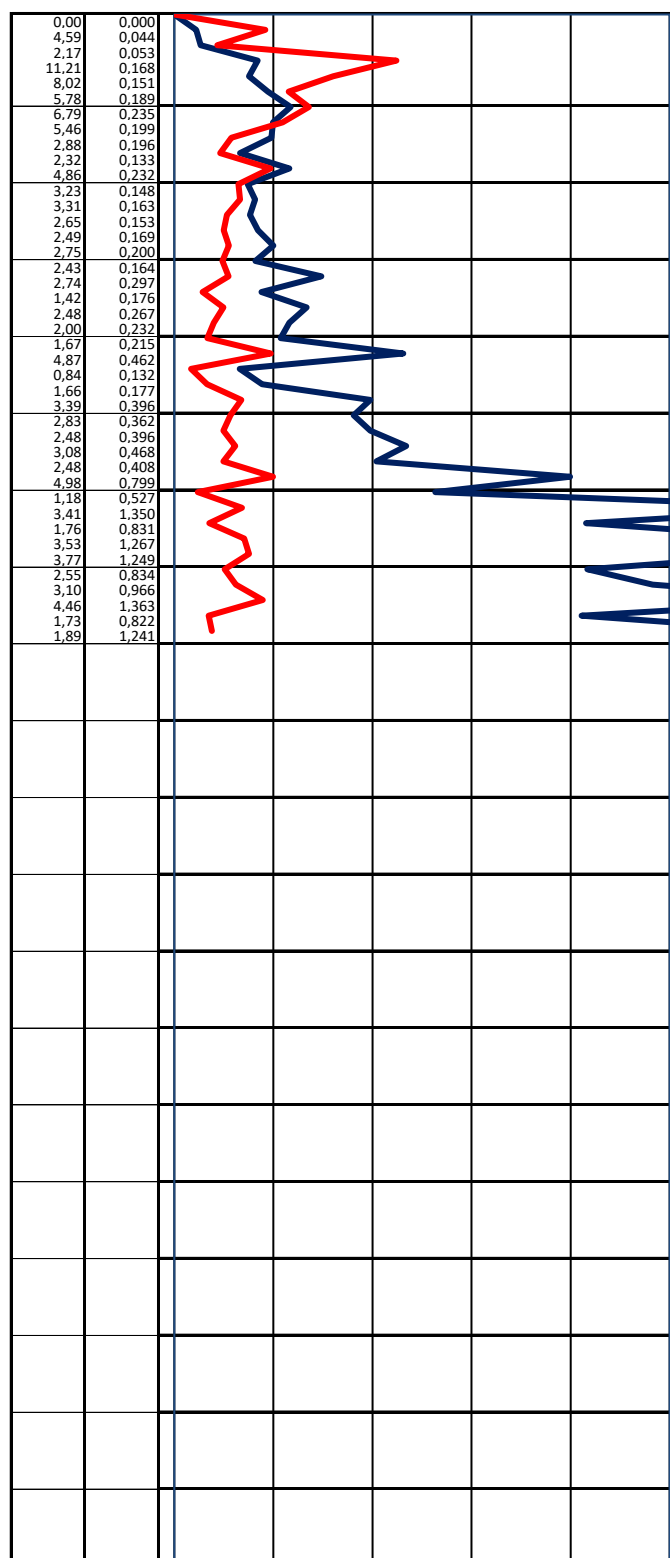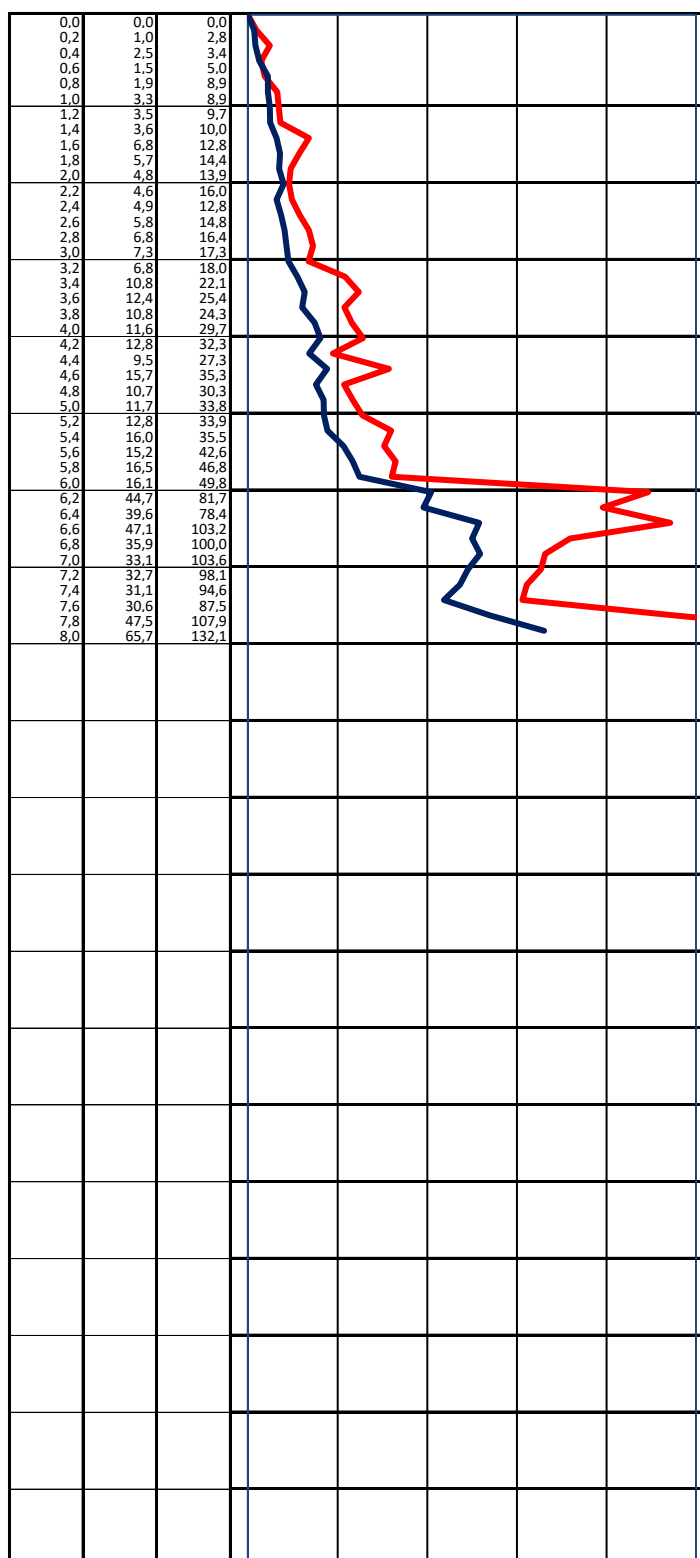

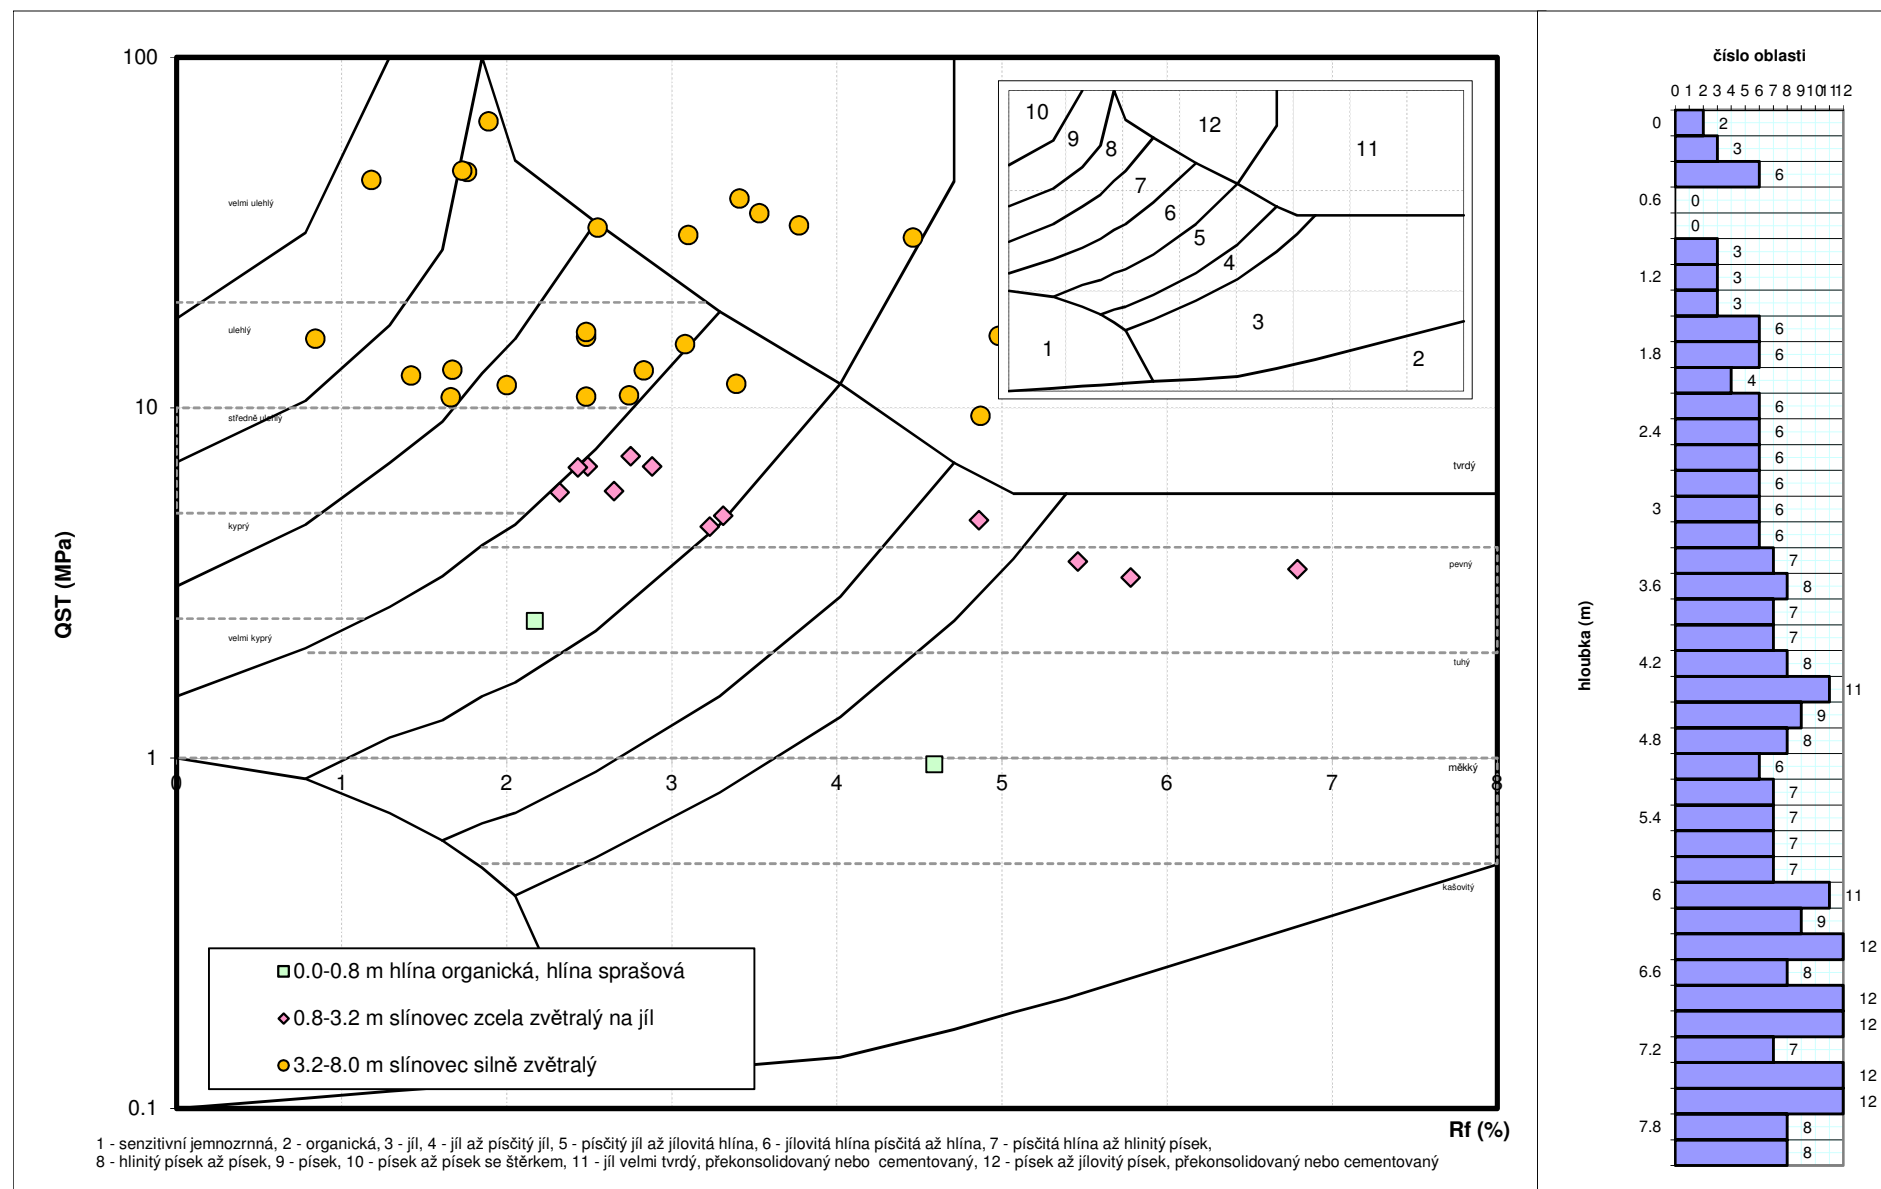






Lokalita	D11 1108 Jaroměř - Trutnov
Zákazník	
Poznámka	použito snižovače
Operátor	
Sonda	SP665
Hloubka pažení	

Datum	24.3.2019
HI vody naražené	
HI vody ustálené	suchá
X	
Y	
Z	

hi	QST	QT	0		QT		200 [kN]
[m]	[Mpa]	[kN]	0		qc		50 [Mpa]

Rf	FS	0		Fs		1 [Mpa]
%	[Mpa]	0		Rf		25 [%]

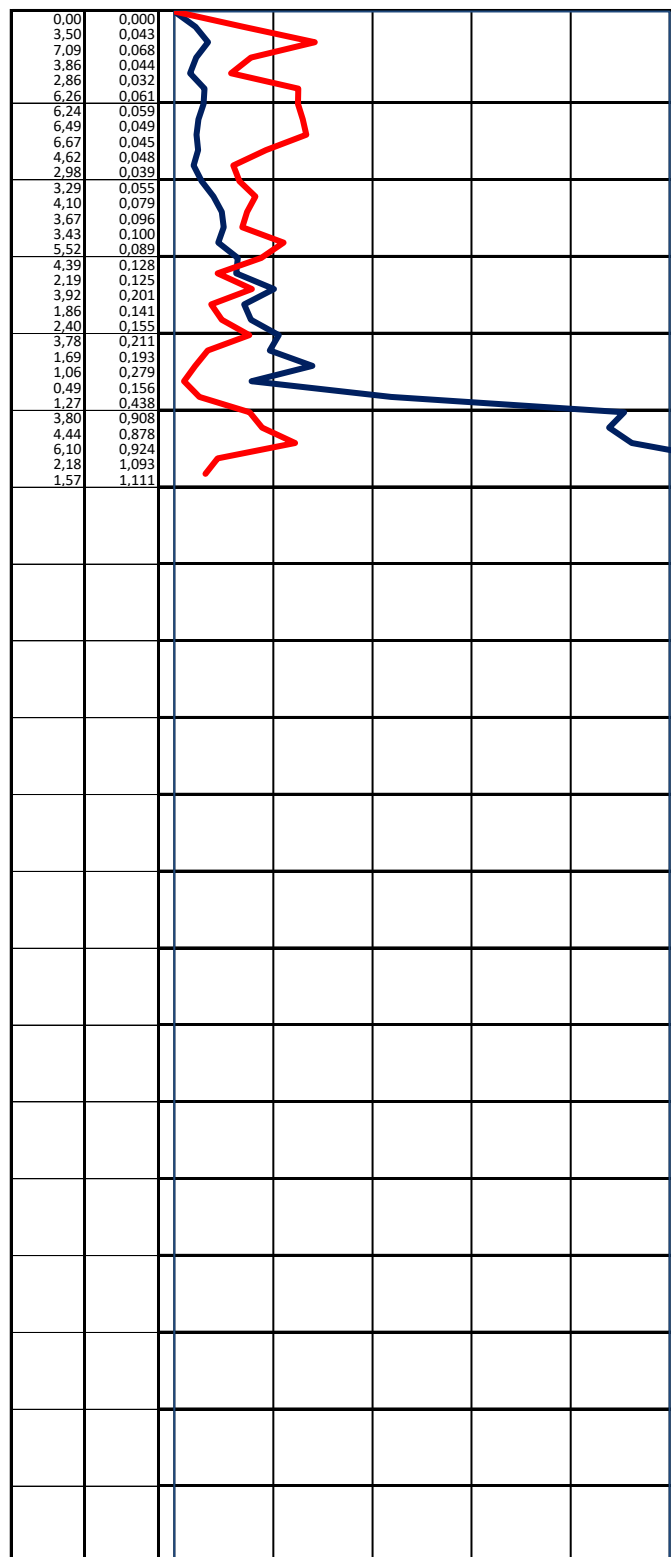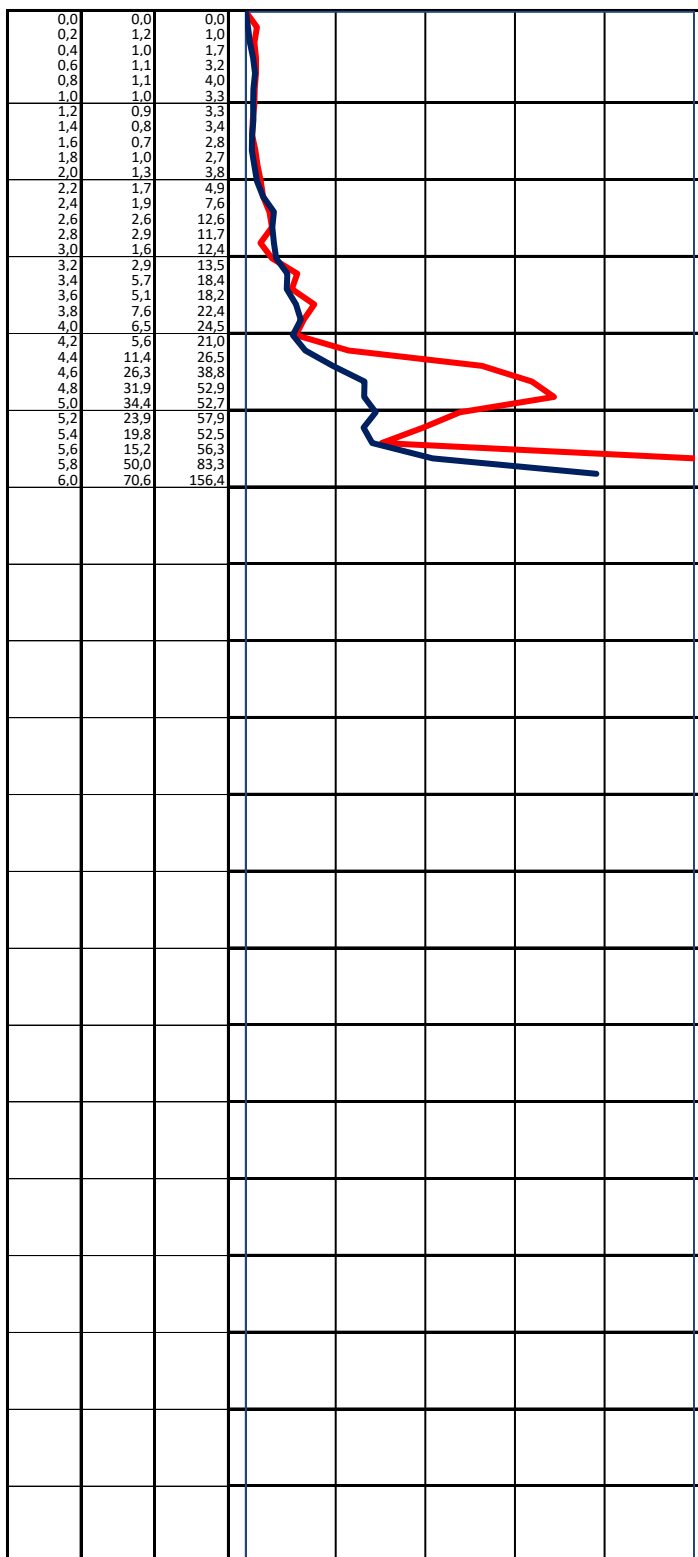

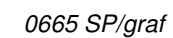






Lokalita	D11 1108 Jaroměř - Trutnov
Zákazník	
Poznámka	použito snižova
Operátor	
Sonda	SP678
Hloubka pažení	

Datum	24.3.2019
Hl vody naražené	
Hl vody ustálené	0,8 m
X	
Y	
Z	

hl	QST	QT	0		QT		200 [kN]
[m]	[Mpa]	[kN]	0		qc		50 [Mpa]

Rf	FS	0		Fs		1 [Mpa]
%	[Mpa]	0		Rf		25 [%]

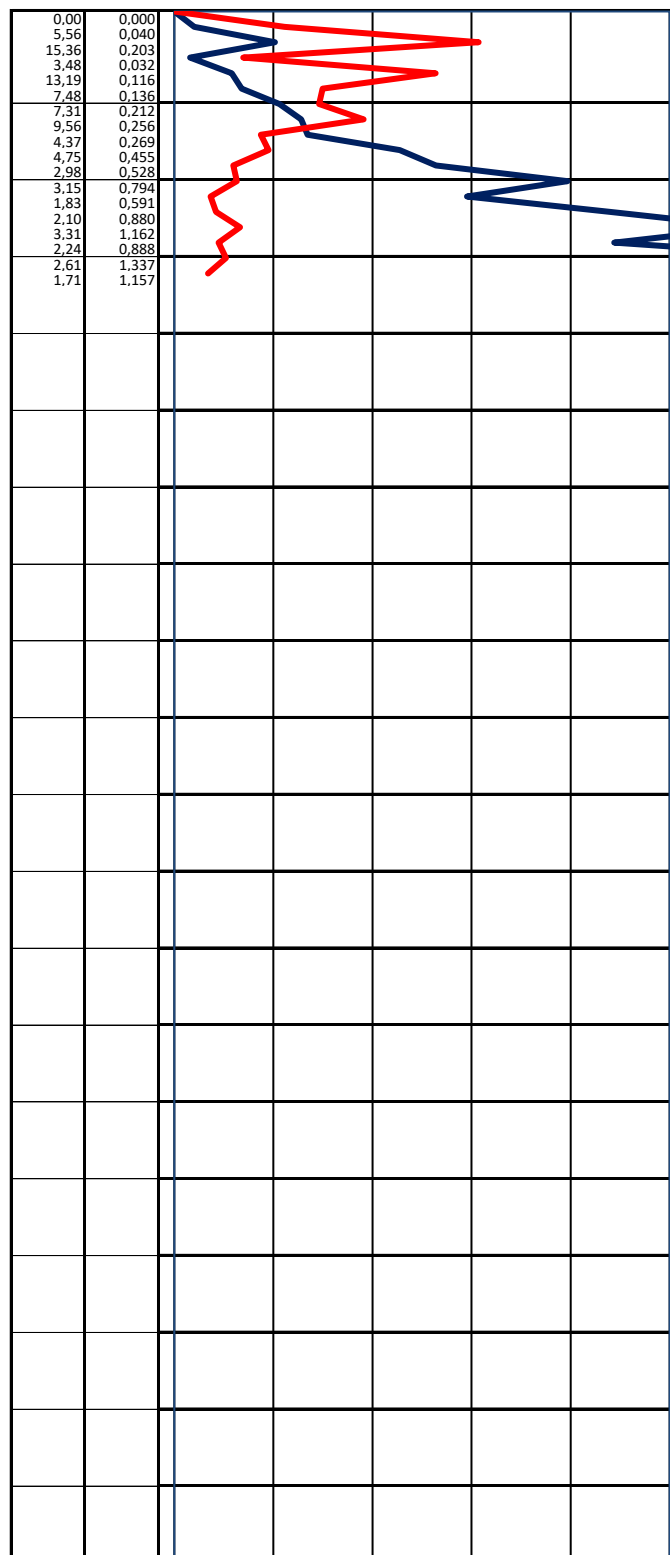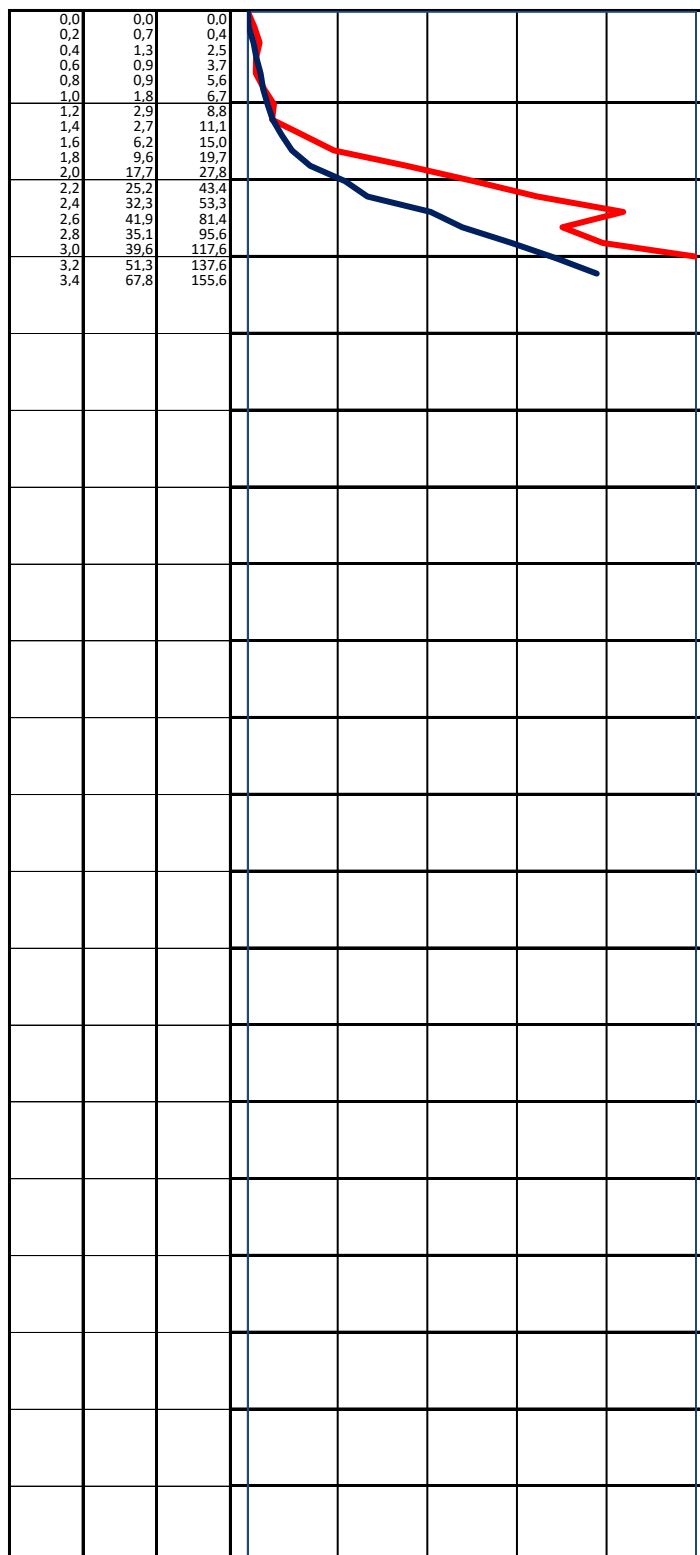

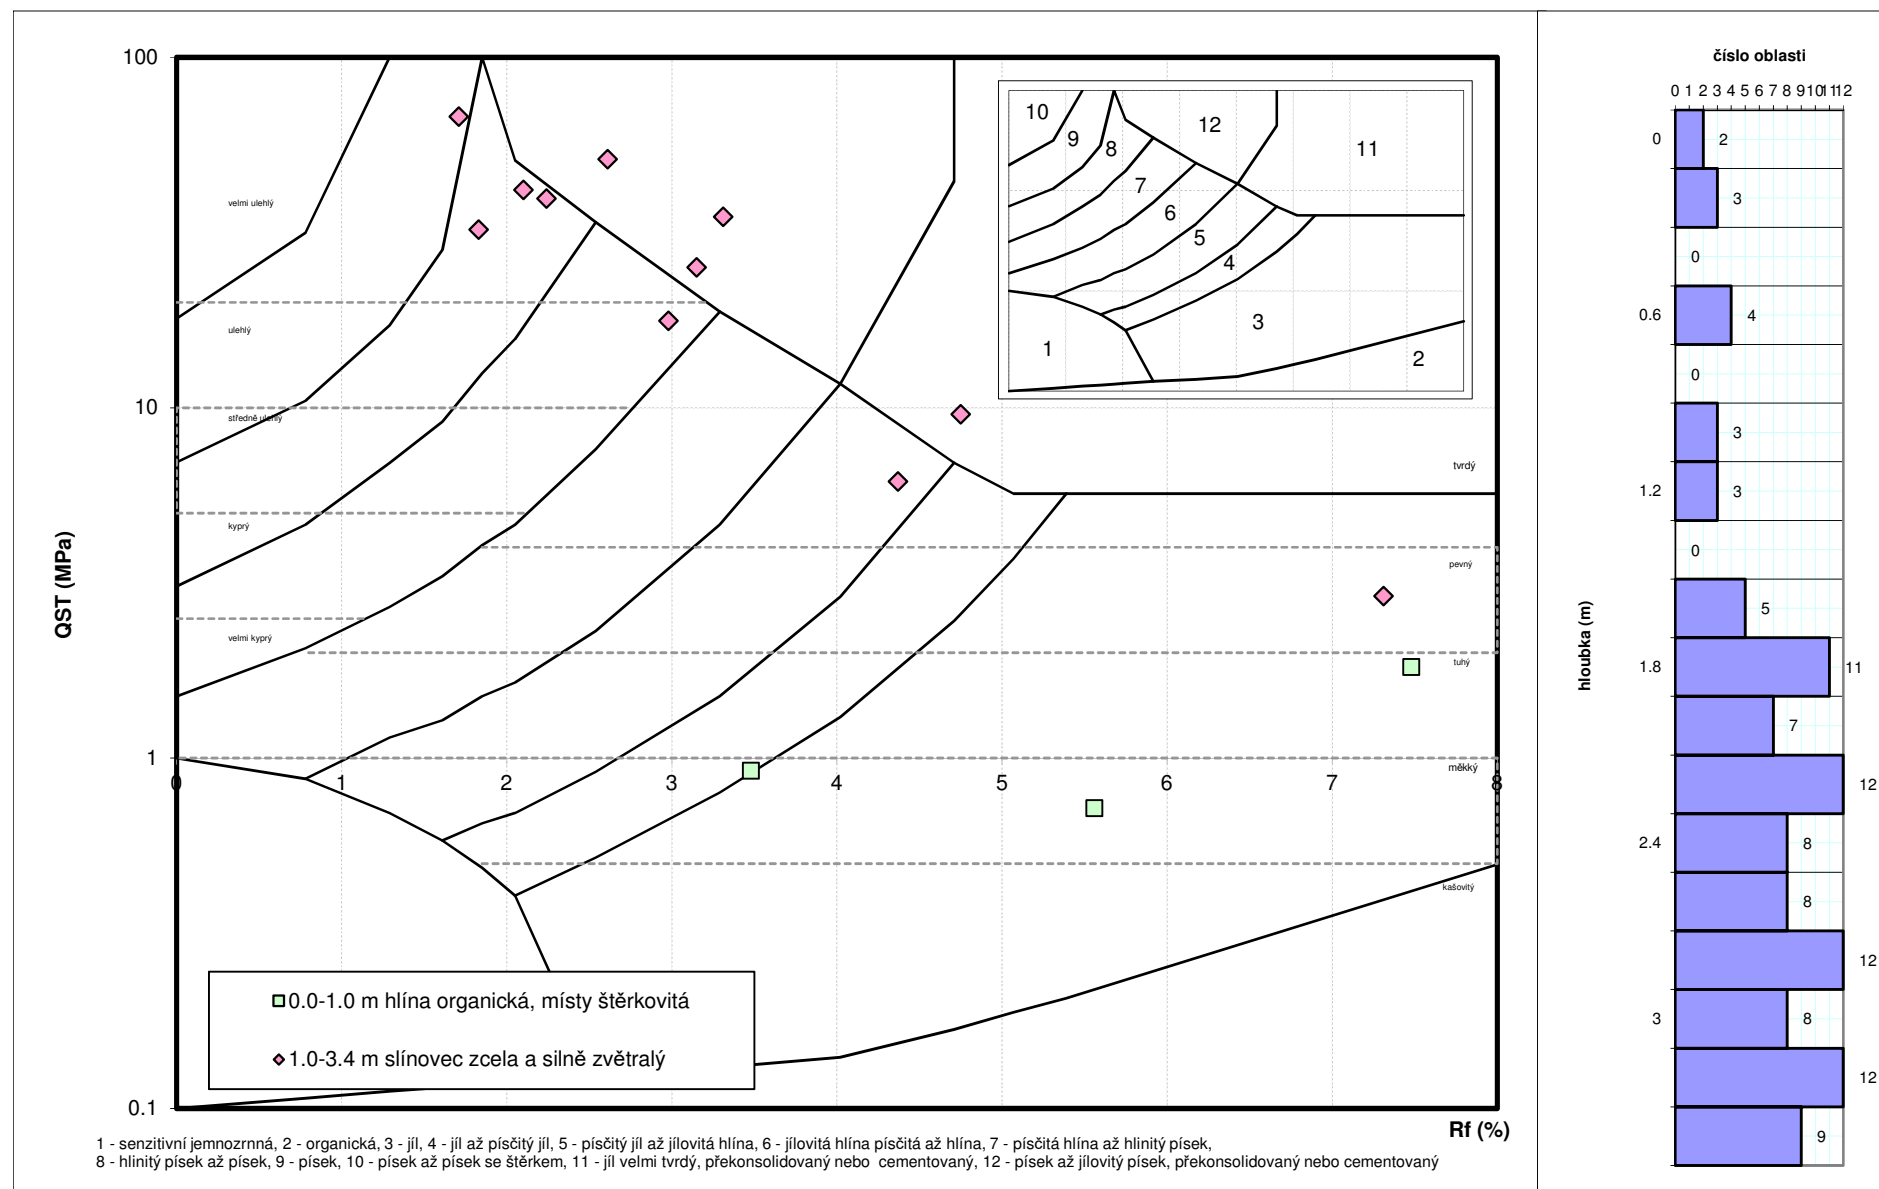






Lokalita	D11 1108 Jaroměř - Trutnov
Zákazník	
Poznámka	použito snížovače
Operátor	
Sonda	SP683
Hloubka pažení	

Datum	9.8.2019
HI vody naražené	
HI vody ustálené	0,5 m zavaleno
X	
Y	
Z	

hi	QST	QT	0		QT		200 [kN]
[m]	[Mpa]	[kN]	0		qc		50 [Mpa]

Rf	FS	0		Fs		1 [Mpa]
%	[Mpa]	0		Rf		25 [%]

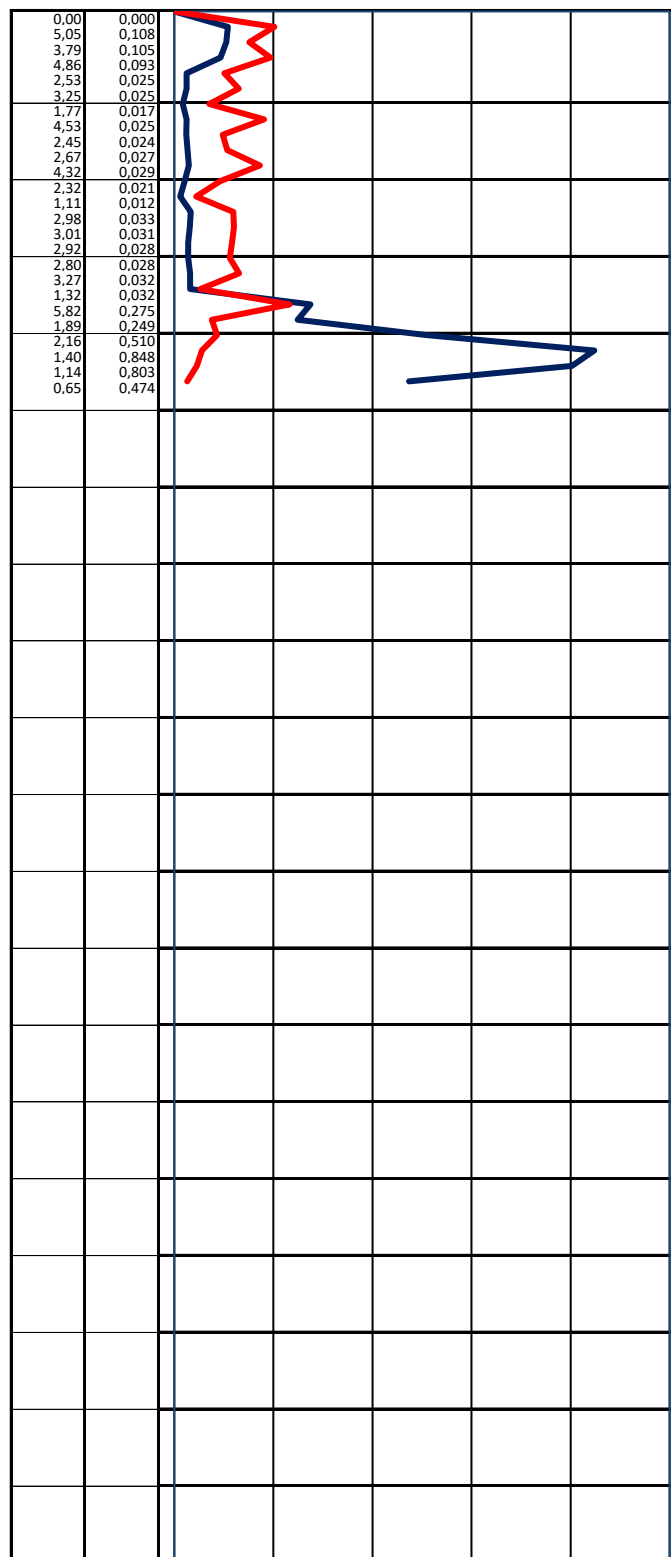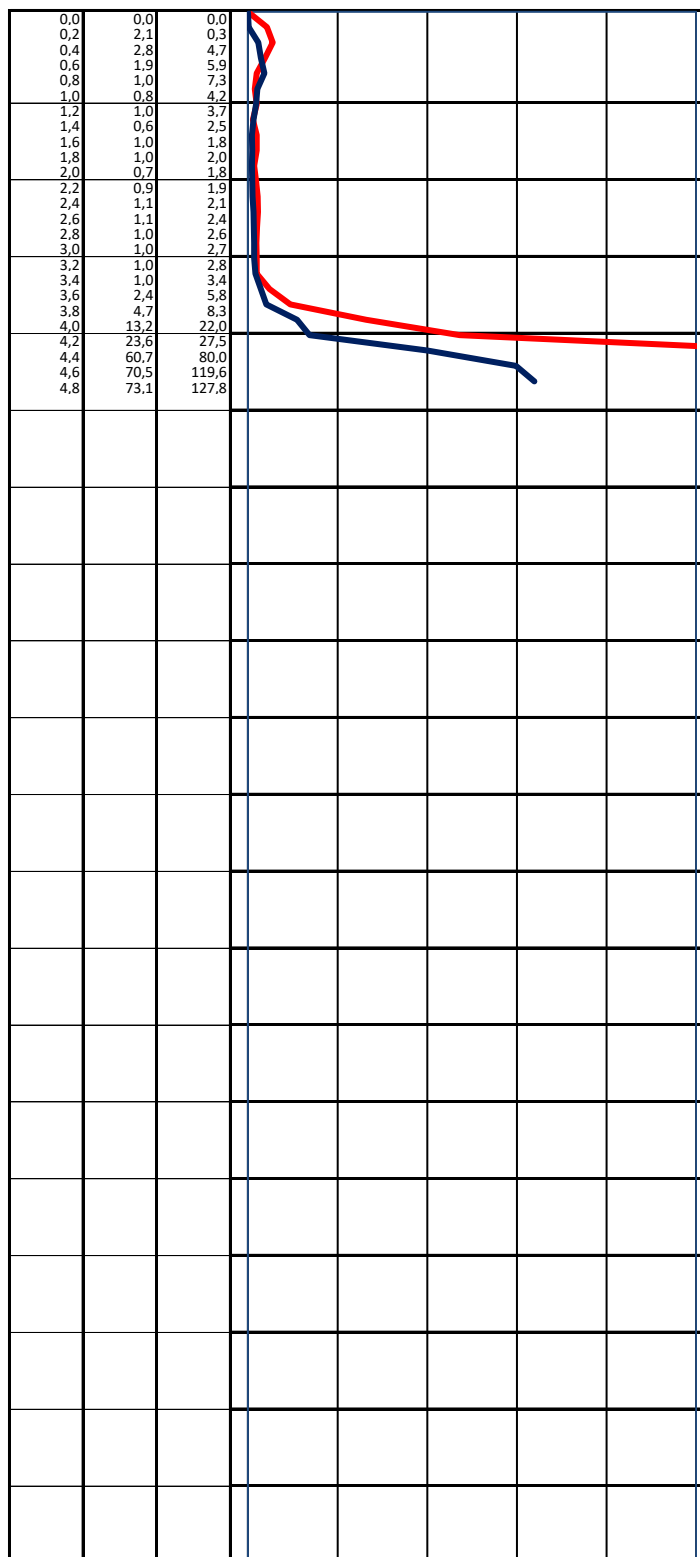

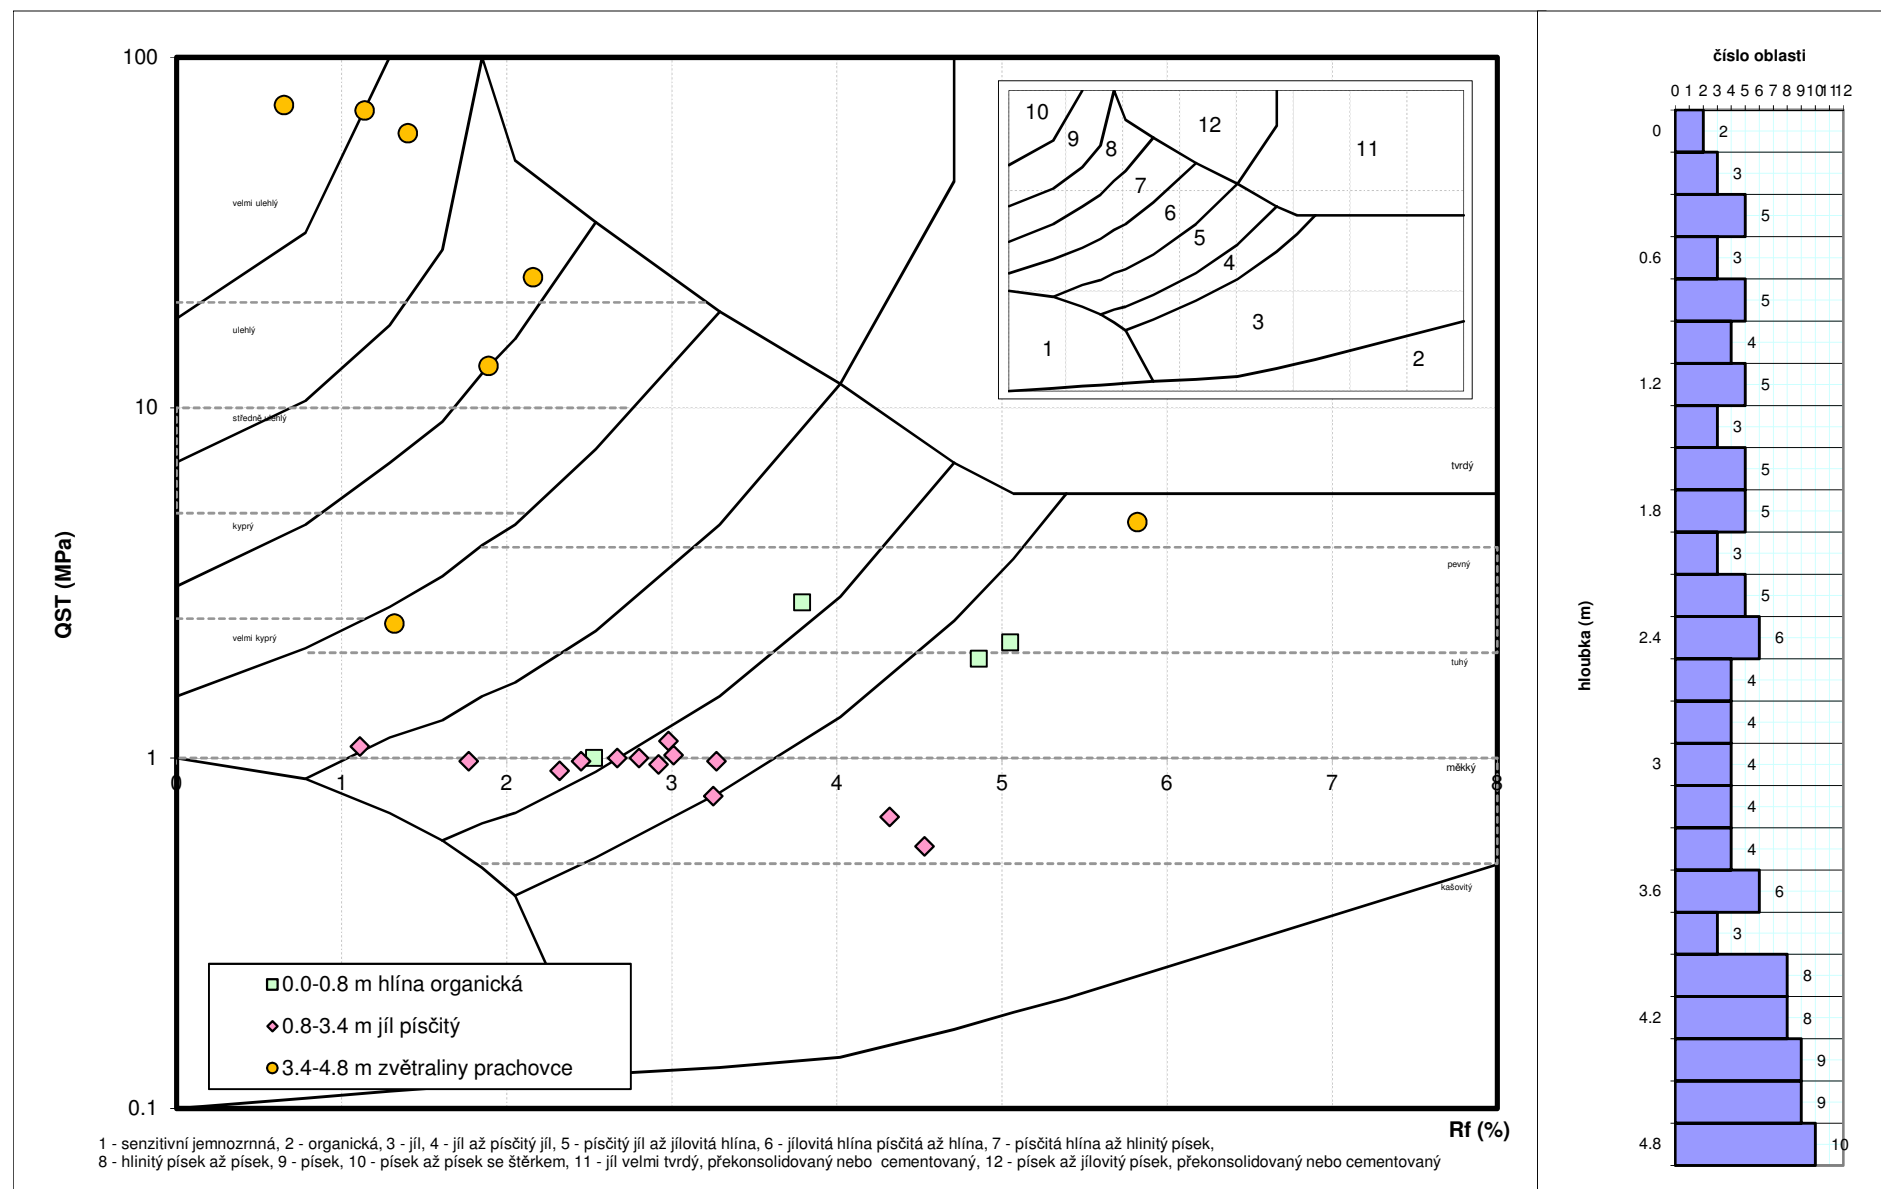



Lokalita	D11 1108 Jaroměř - Trutnov
Zákazník	
Poznámka	použito snížovače
Operátor	
Sonda	SP910
Hloubka pažení	

Datum	9.8.2019
HI vody naražené	
HI vody ustálené	suchá
X	
Y	
Z	

hi	QST	QT	0		QT		200 [kN]
[m]	[Mpa]	[kN]	0		qc		50 [Mpa]

Rf	FS	0		Fs		1 [Mpa]
%	[Mpa]	0		Rf		25 [%]

