
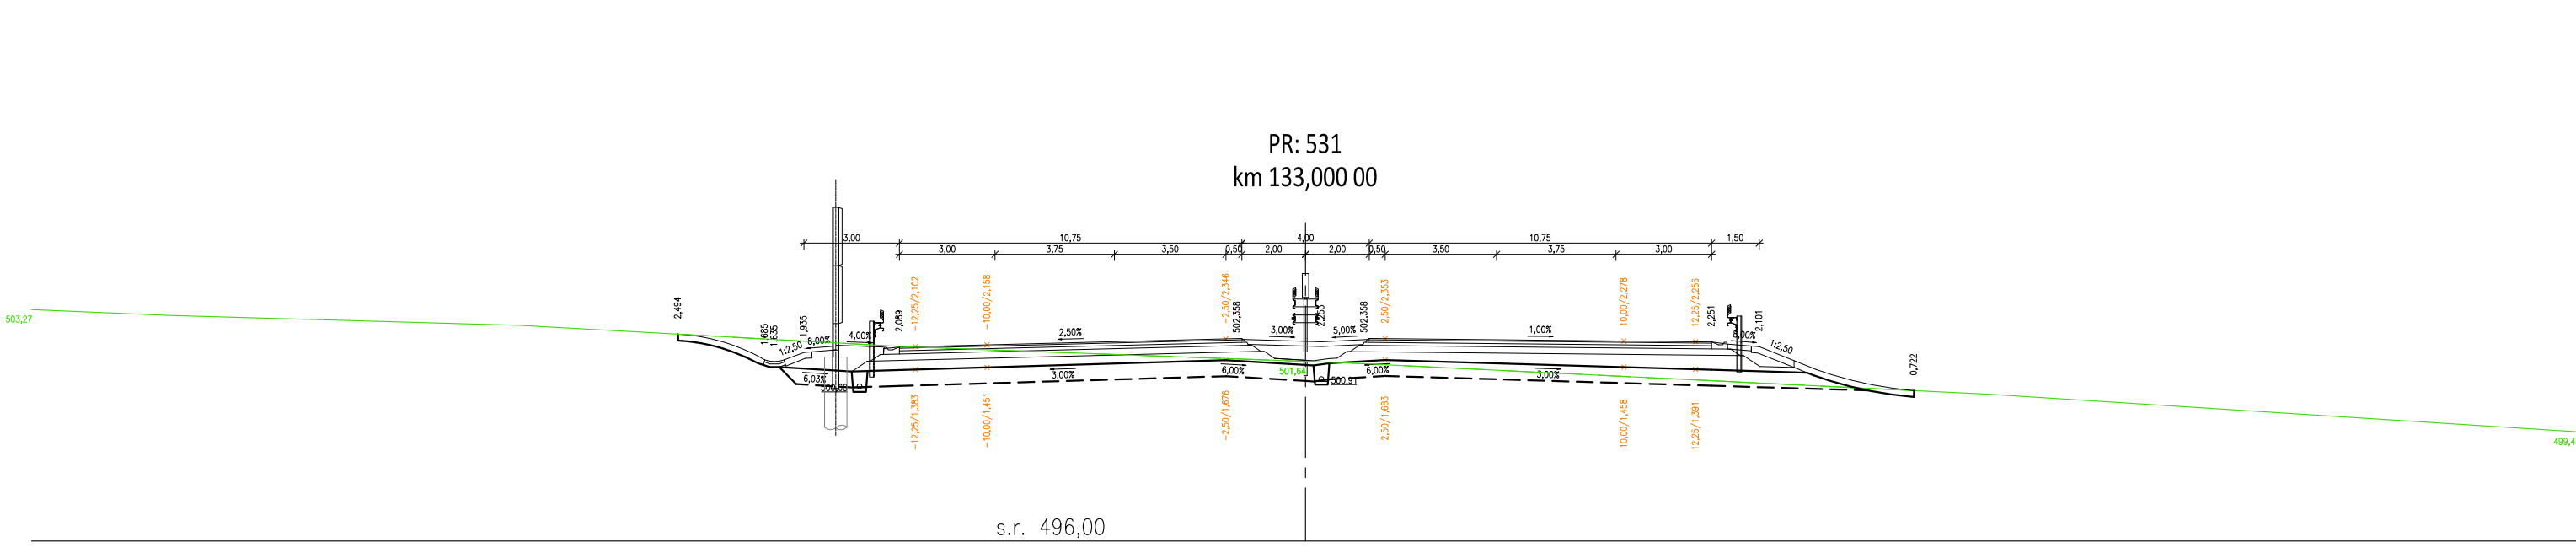
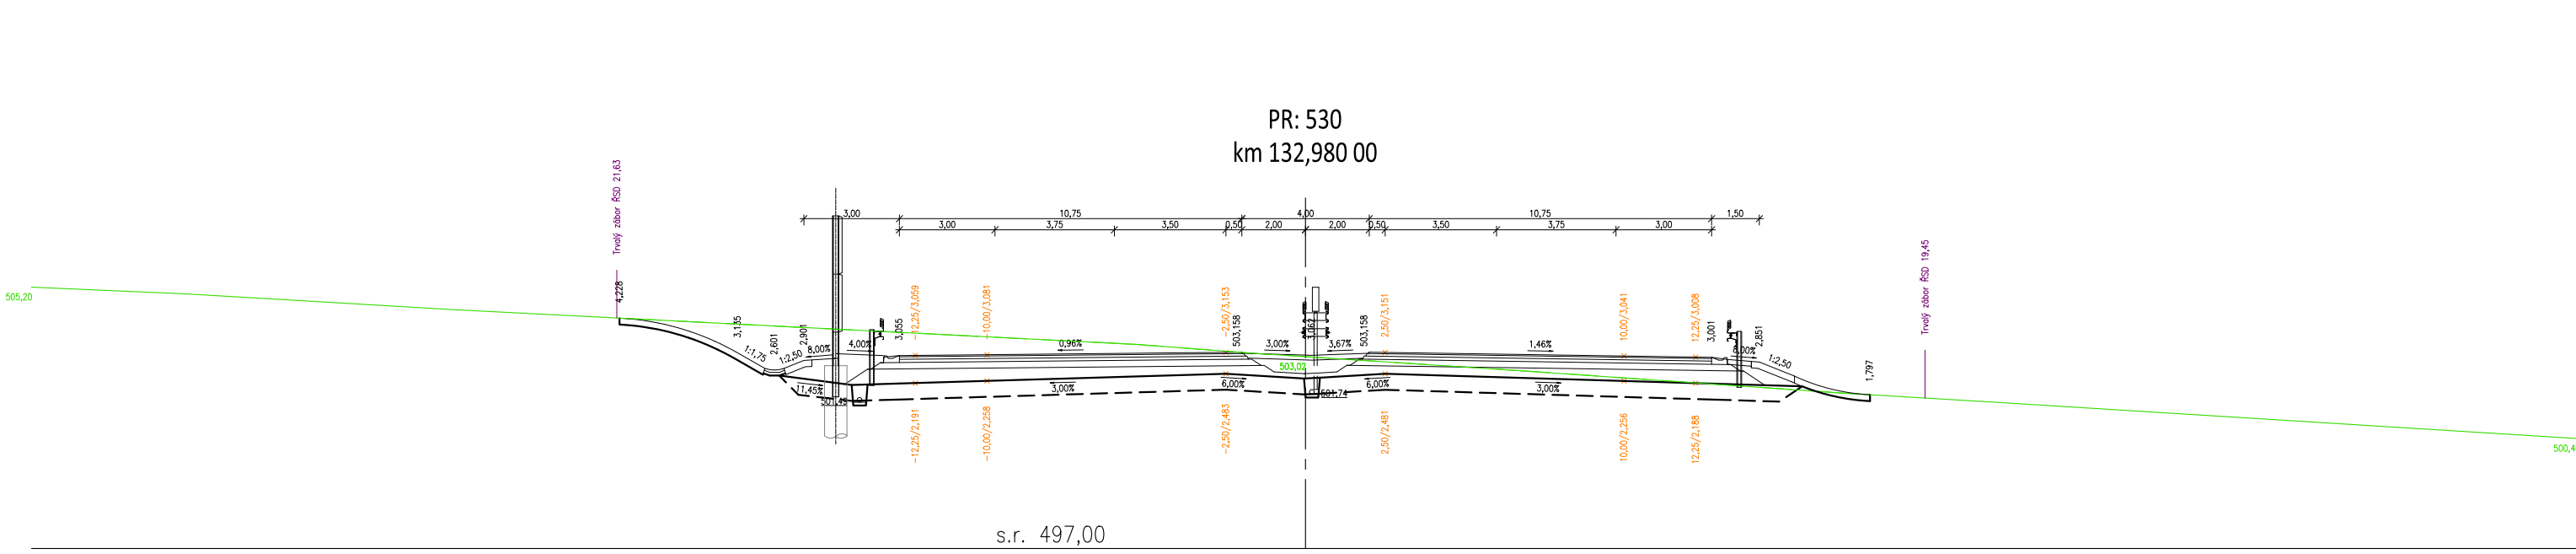
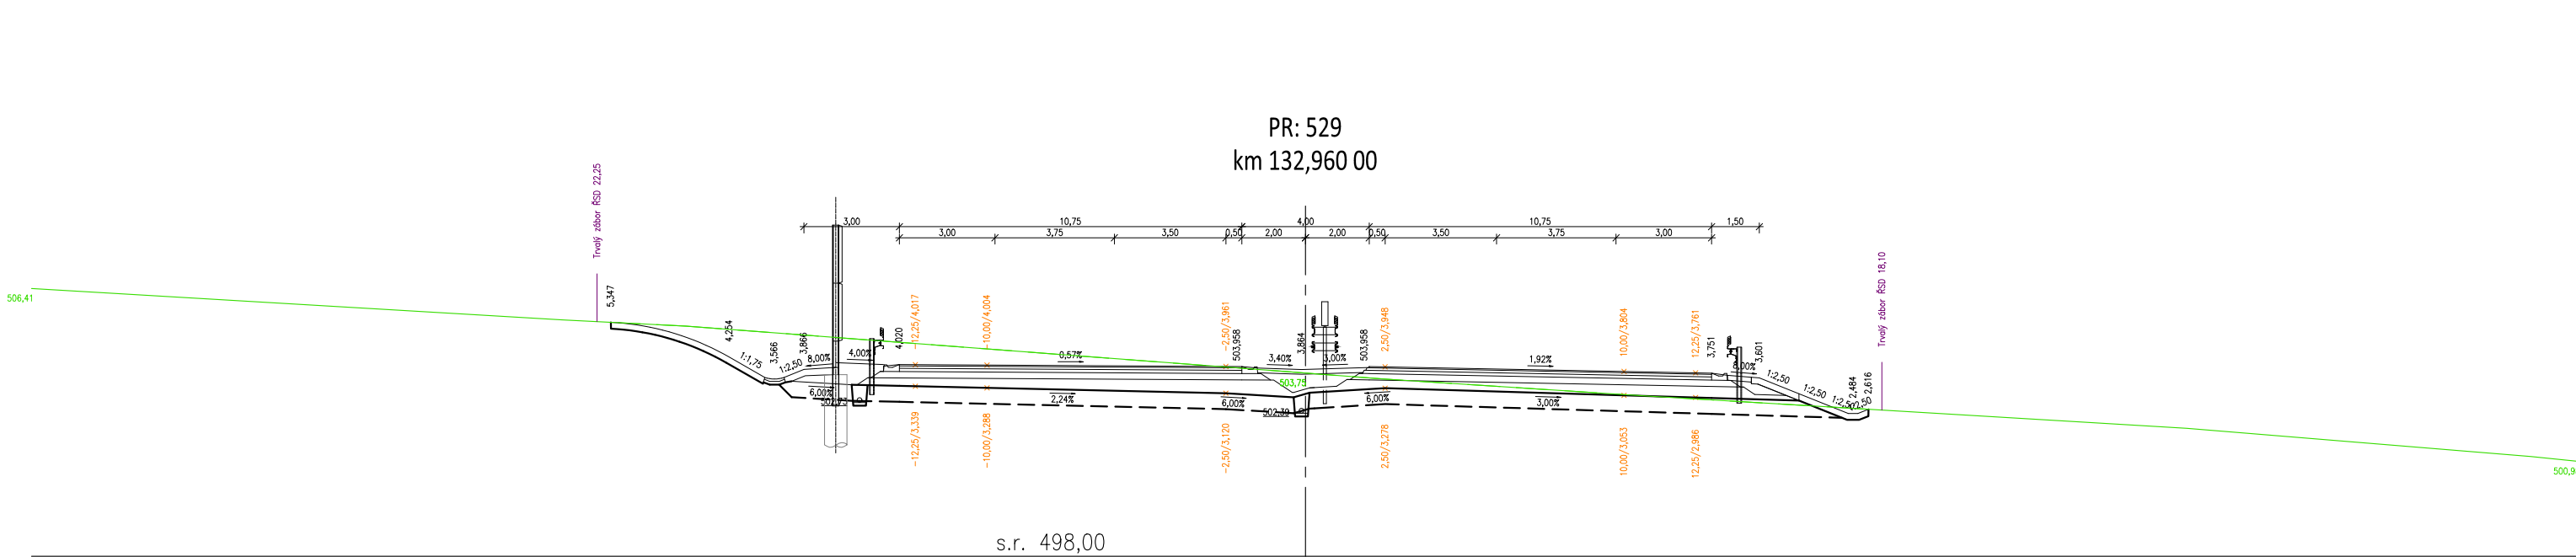
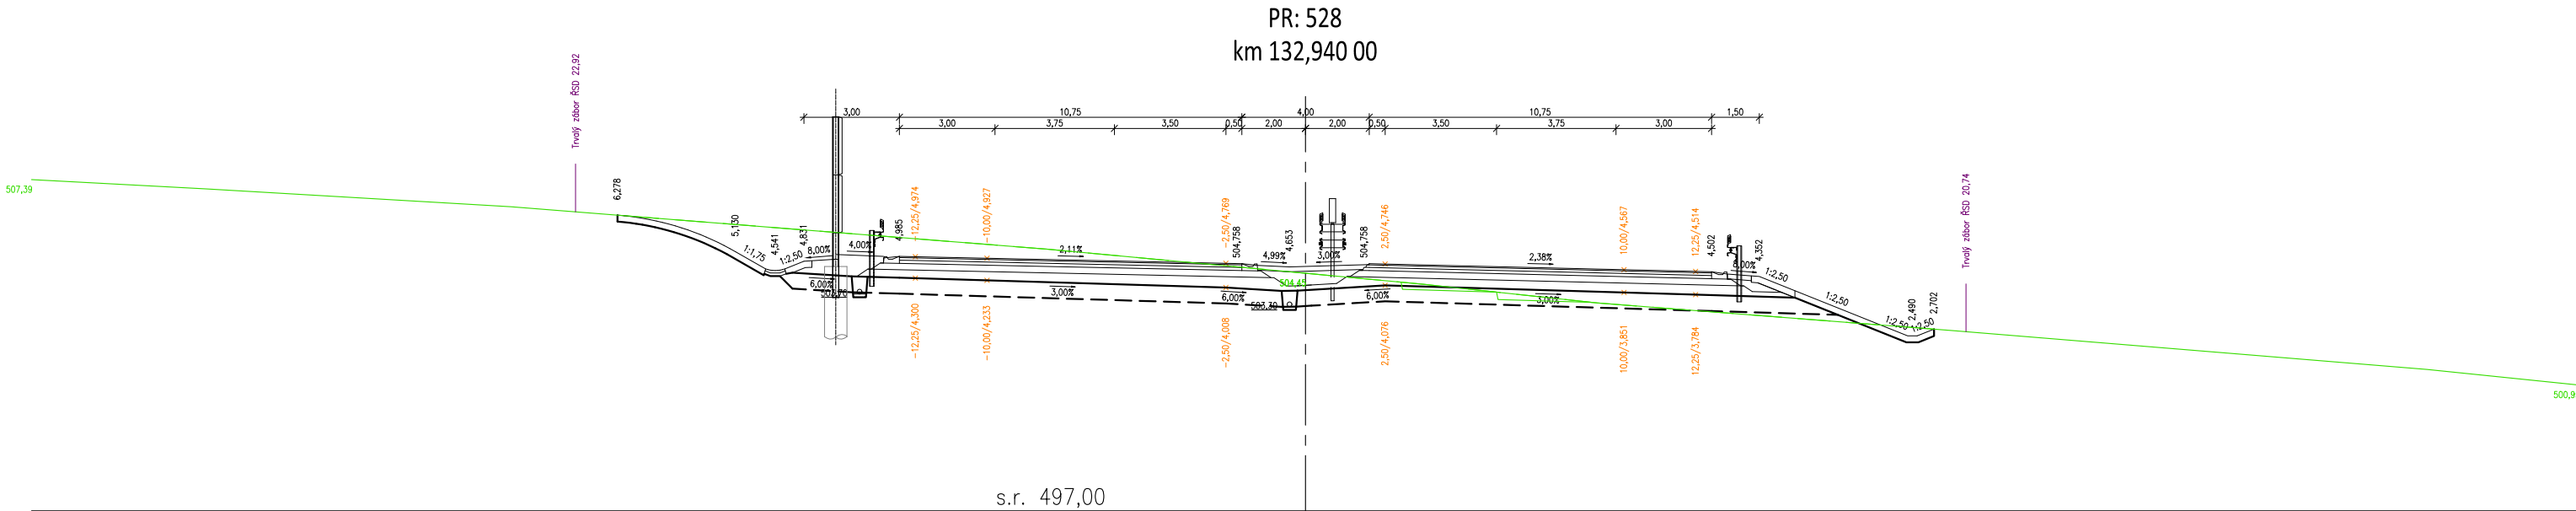
 
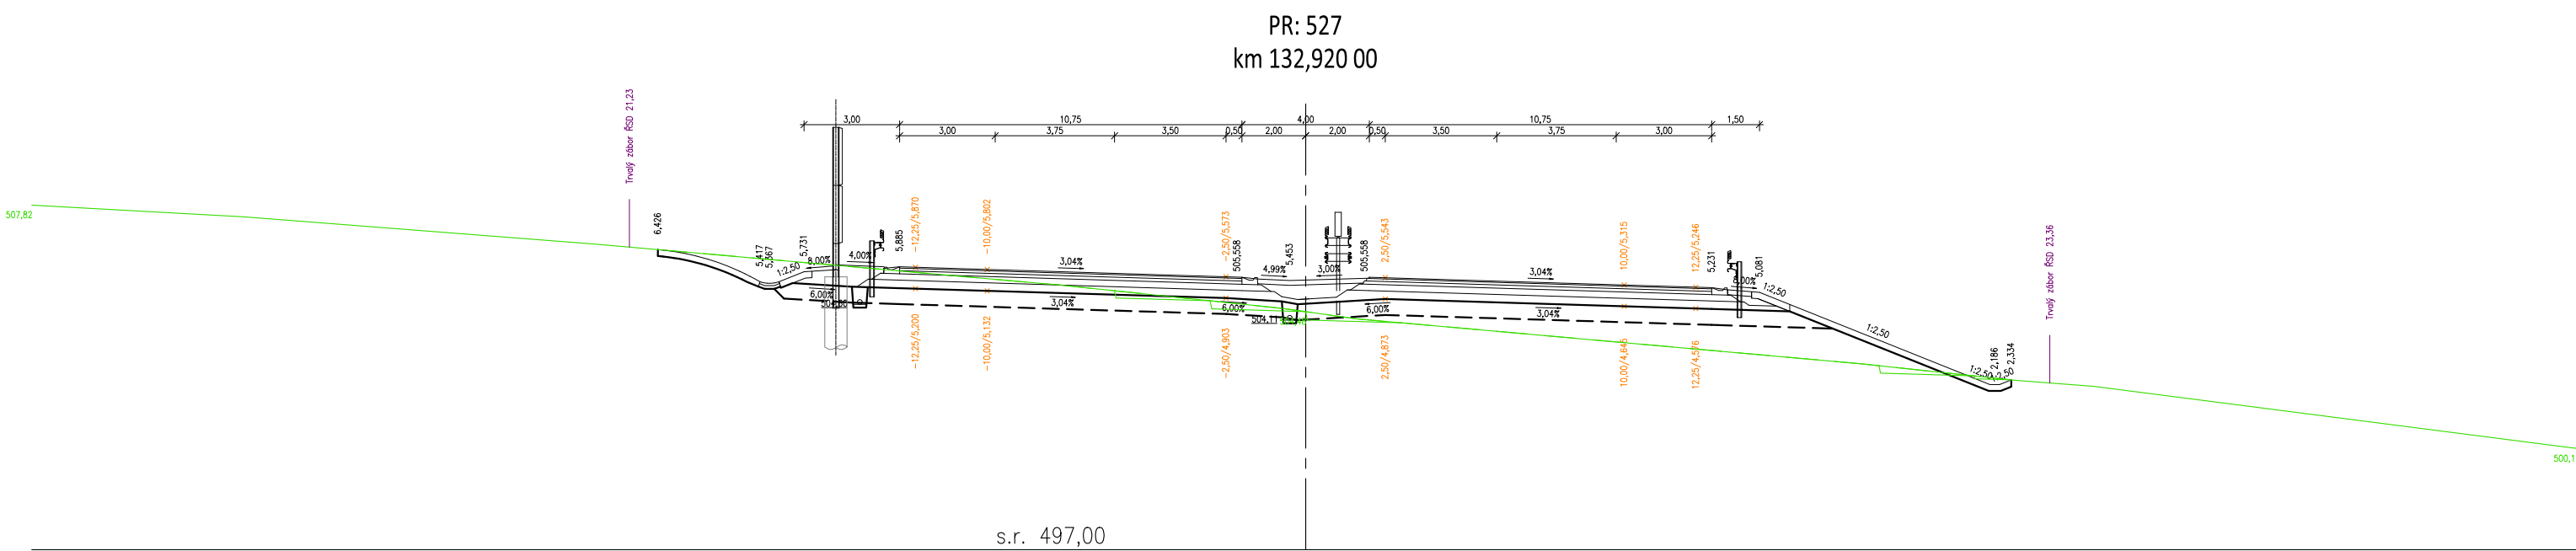
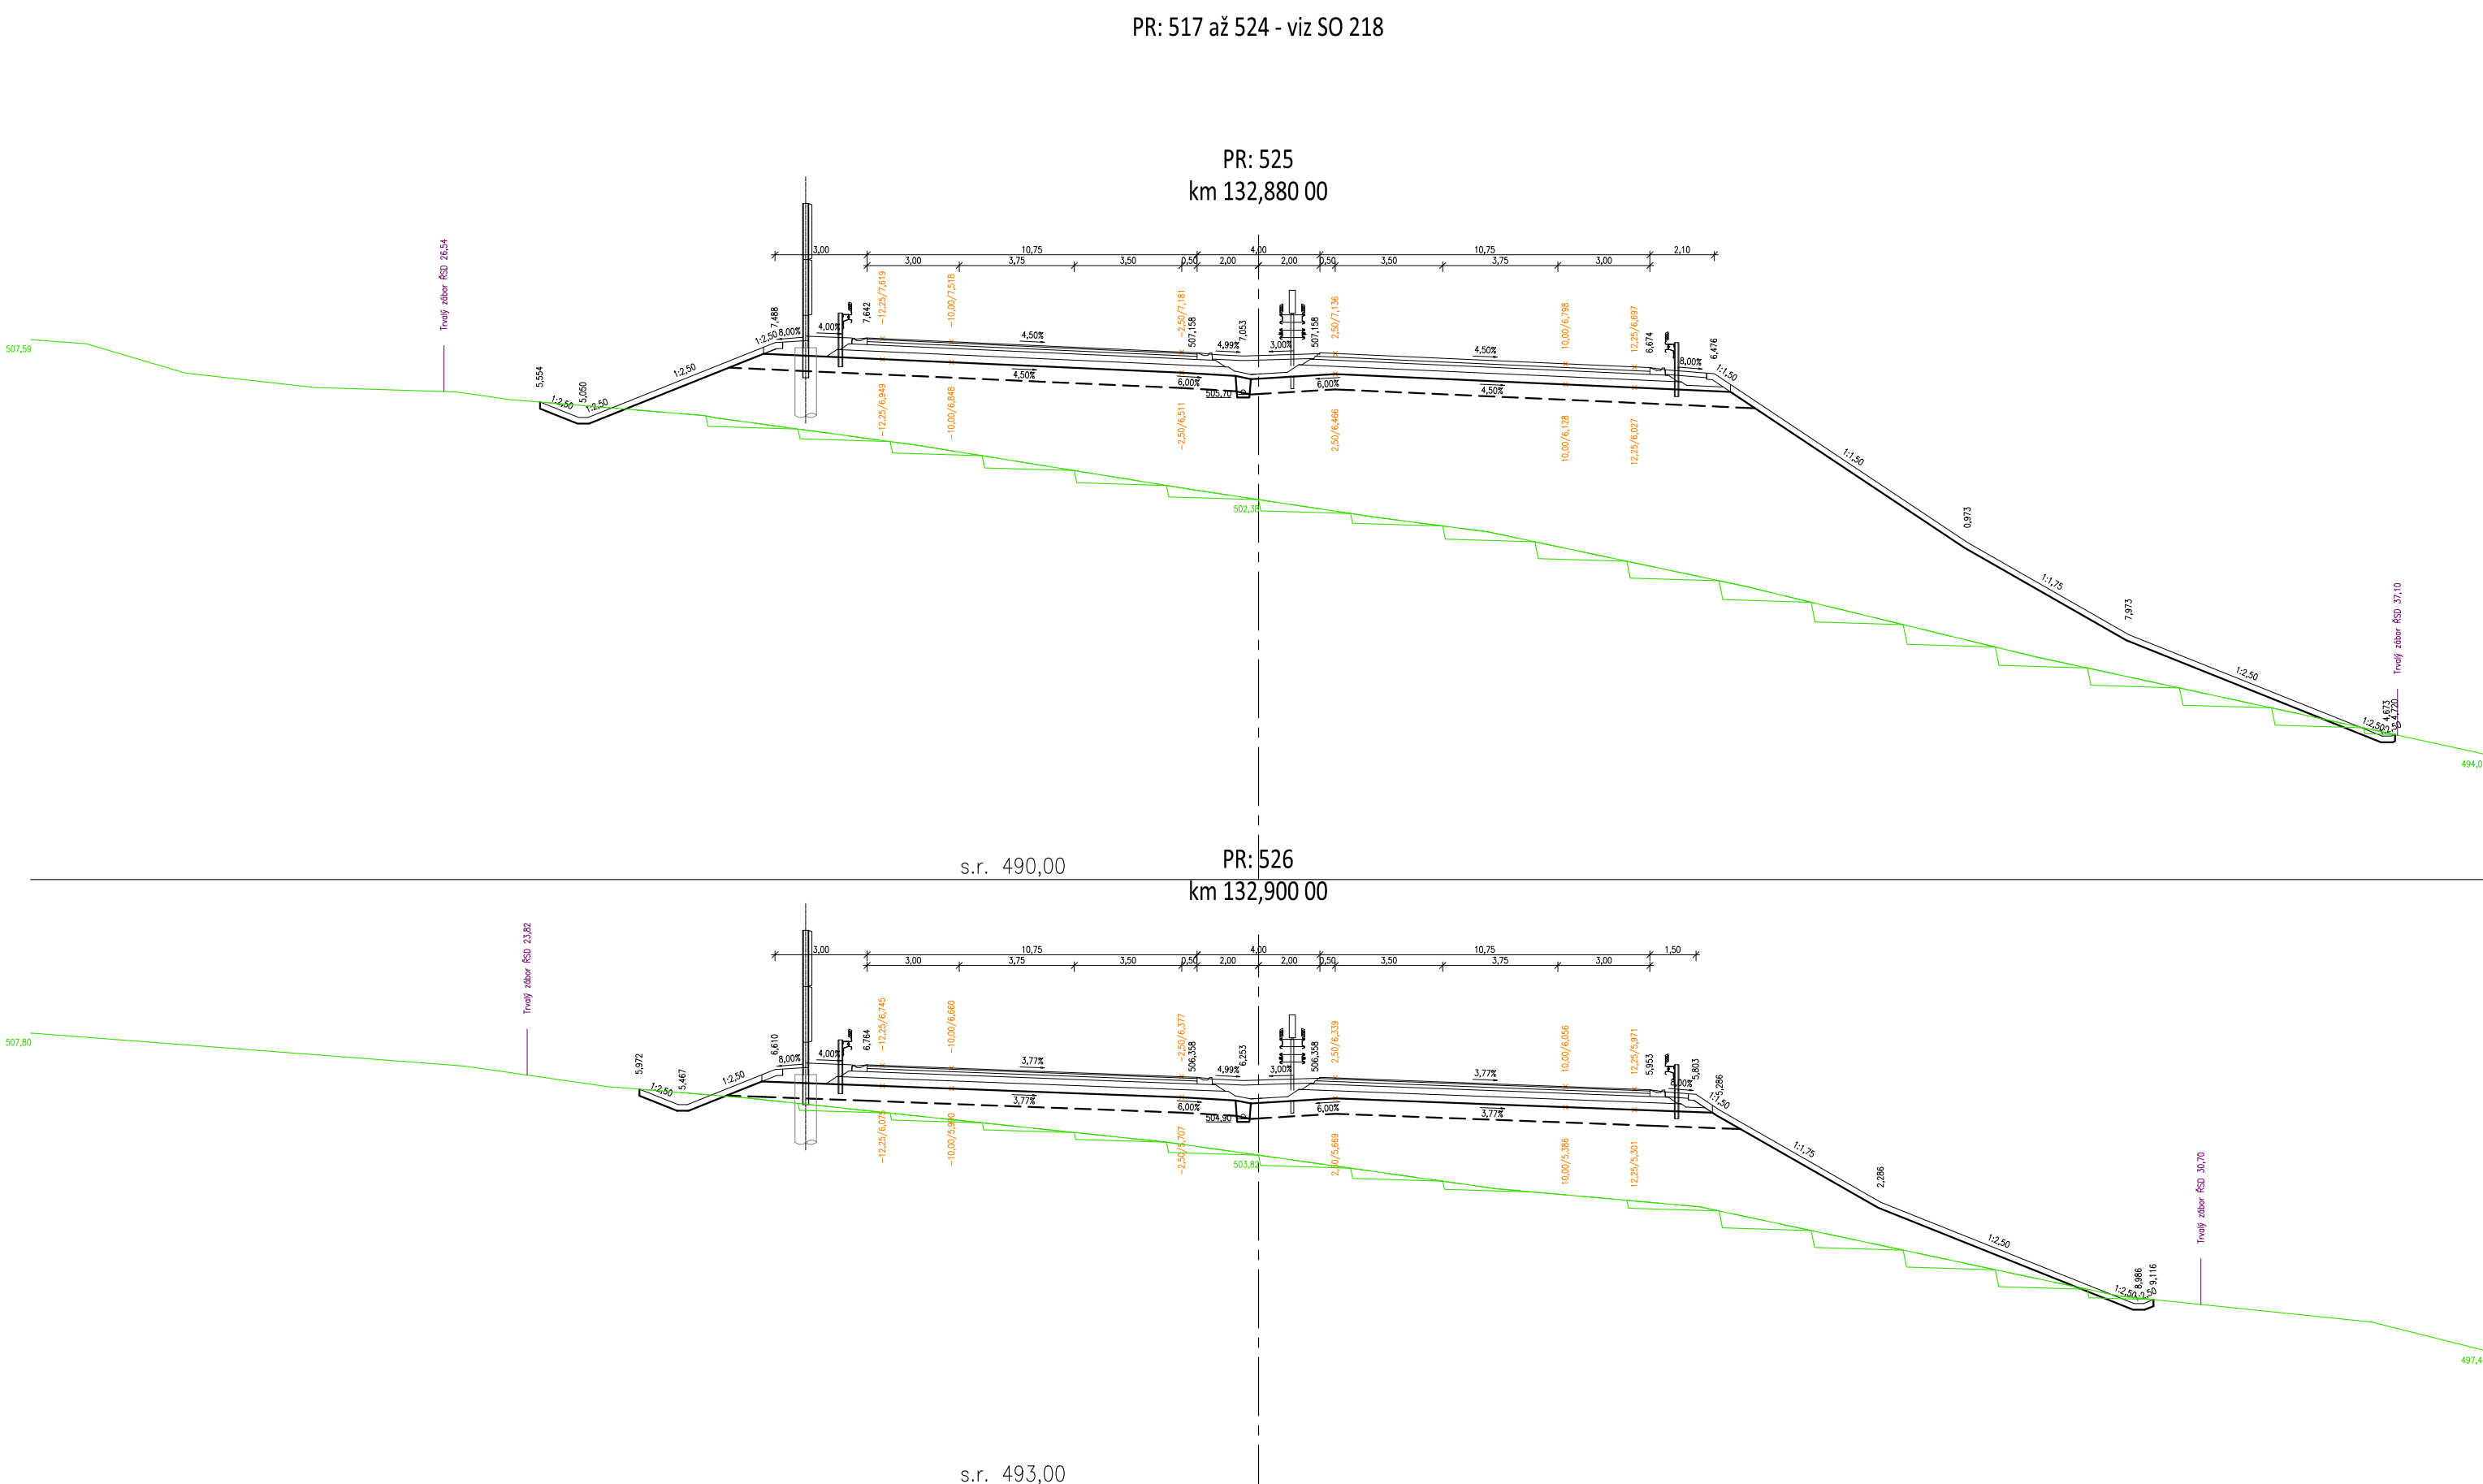
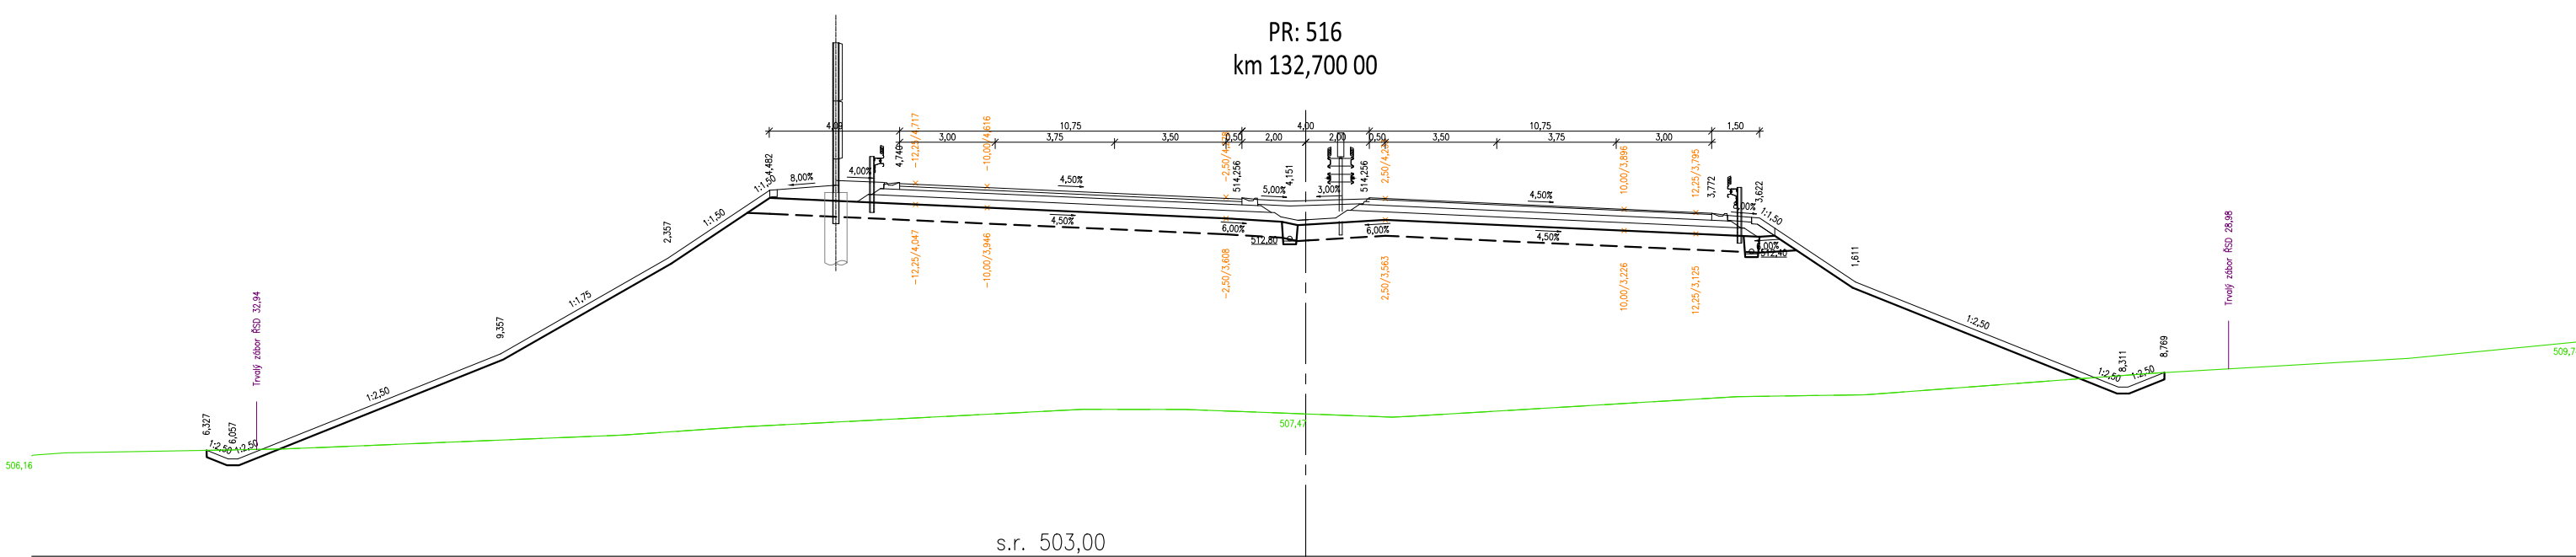


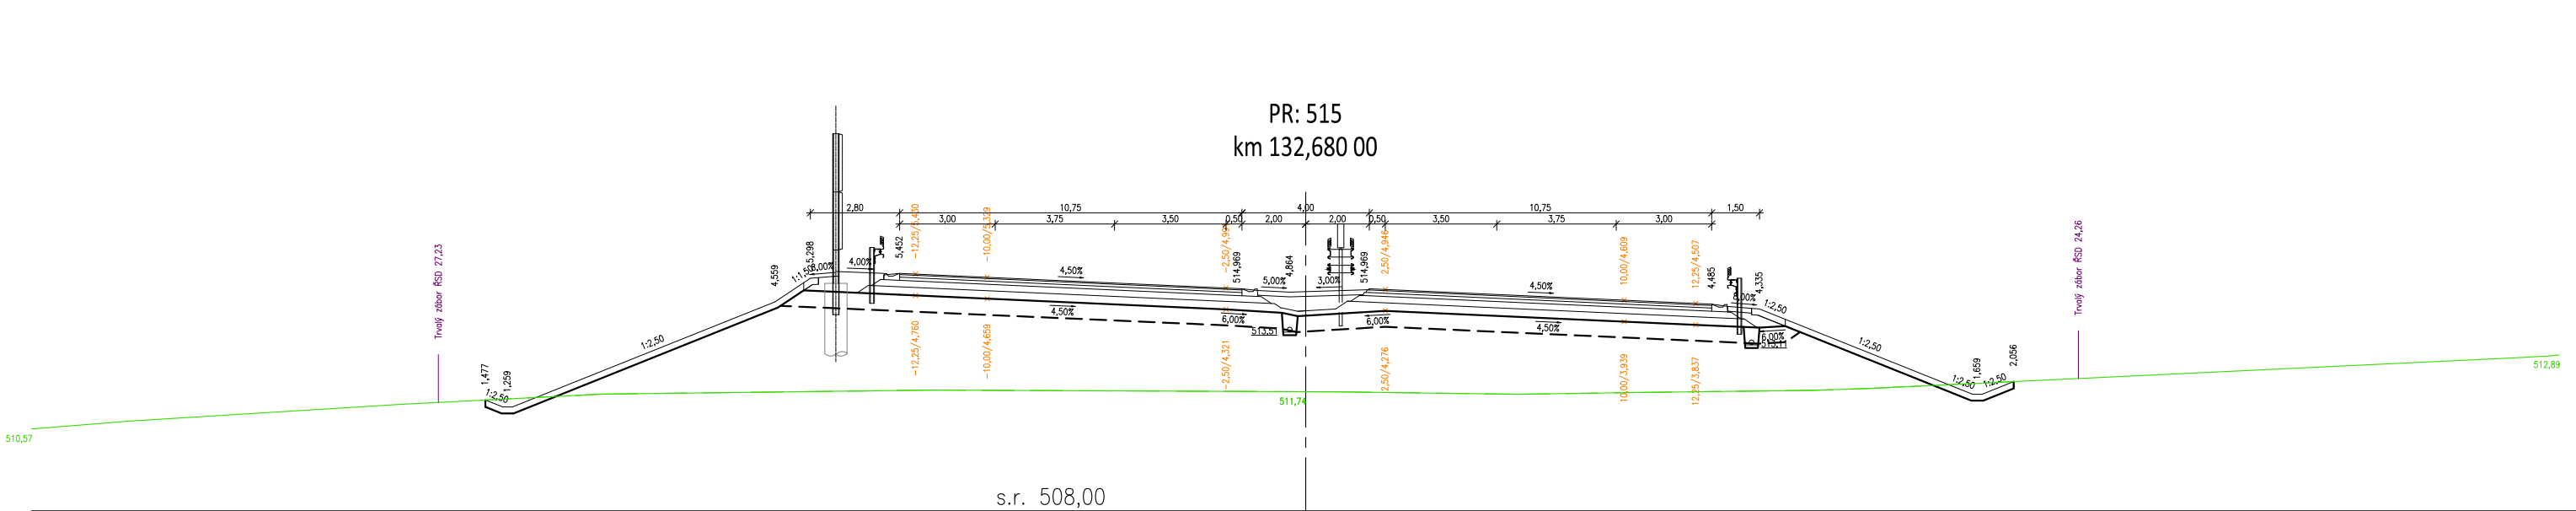

SO 101

D.1.1

VÝŠKOVÝ SYSTÉM Bpv SOUŘADNICOVÝ SYSTÉM S-JTSC

Číslo změny:	Obsah změny:	Datum změny:
01	-	-
02	-	-
03	-	-

**BENTELSTVÍ
SILNIC
A DÁLNIC**

Ředitelství silnic a dálnic s. p.
Na Pankraci 546/56, 140 00 Praha 4
Stavbu zajišťuje Závod Praha
Na Pankraci 546/56, 140 00 Praha 4

Zhotovitel: Společnost ve sdružení

SG_Velké projekty, BIM 2020
zastoupené

SUDOP PRAHA a.s.
Hlavní inženýr projektu: Ing. Roman Petřík

Ošlanská 1a, 130 80 Praha 3
telefon: +420 267 094 111

Správce:

SUDOP PRAHA a.s.
Ošlanská 1a, 130 80 Praha 3
tel.: +420 267 094 111
e-mail: praha@sudop.cz

Vedoucí týmu:

ING. ROMAN PETŘÍK

Asistent vedoucího týmu:

ING. PAVEL MICHL
Specialista profese:
-

Zpracovatel:

PUDIS

projektová, průzkumná a konzultační společnost

PUDIS a.s., Podbabská 1014/20, 160 00 Praha 6
tel.: +420 267 004 111, info@pudis.cz

Vedoucí střediska:	Odpovědný projektant SO, IO, PS:	Výpracoval:	Kontroloval:
ING. ZDĚŇKA BOLEHOVSKÁ	ING. MICHAL TUREK	PETR KOTLABA	ING. MICHAL TUREK

Název akce:	Číslo směrovky:
D11 1108 Jaroměř - Trutnov VD-ZDS + TP + AD	22-014.250
Část:	Projektový stupeň:
D.1.1 OBJEKTY POZEMNÍCH KOMUNIKACÍ VČETNĚ PROPUSTKŮ SO 101 HLAVNÍ TRASA D11 1108	VD-ZDS
Název přílohy:	Datum:
PŘÍČNÉ ŘEZY - 34.část	11/2024
	Číslo části:
	D.1.1
	Mřížko:
	1:200
	Počet formátů:
	10xA4
	Číslo přílohy:
	5.34