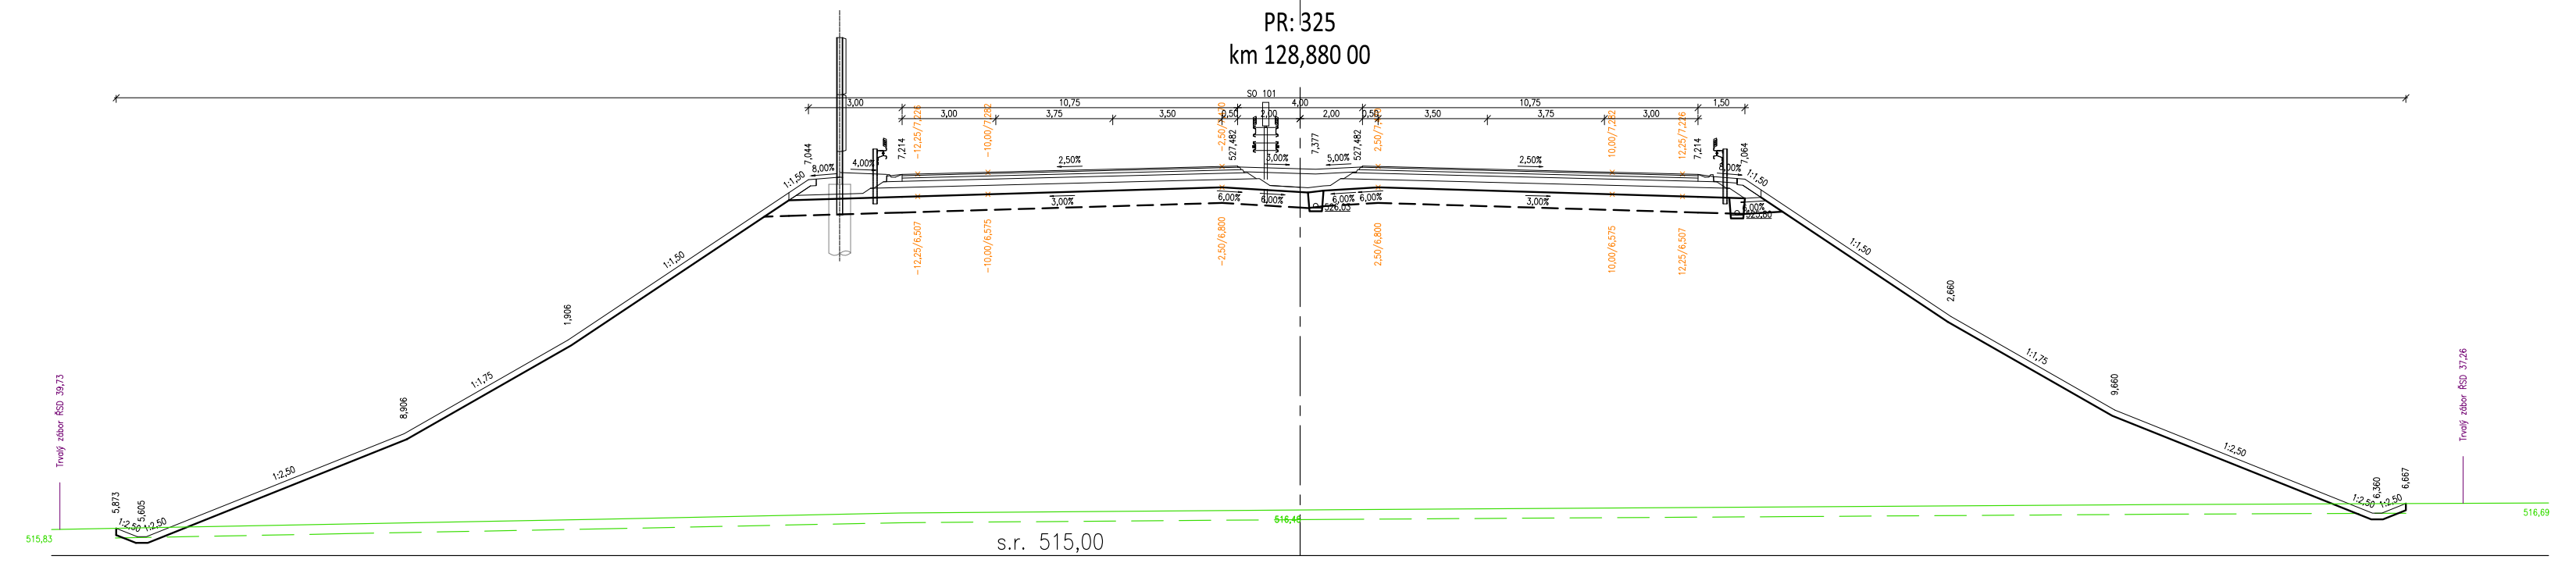
PR: 325
km 128,880 00

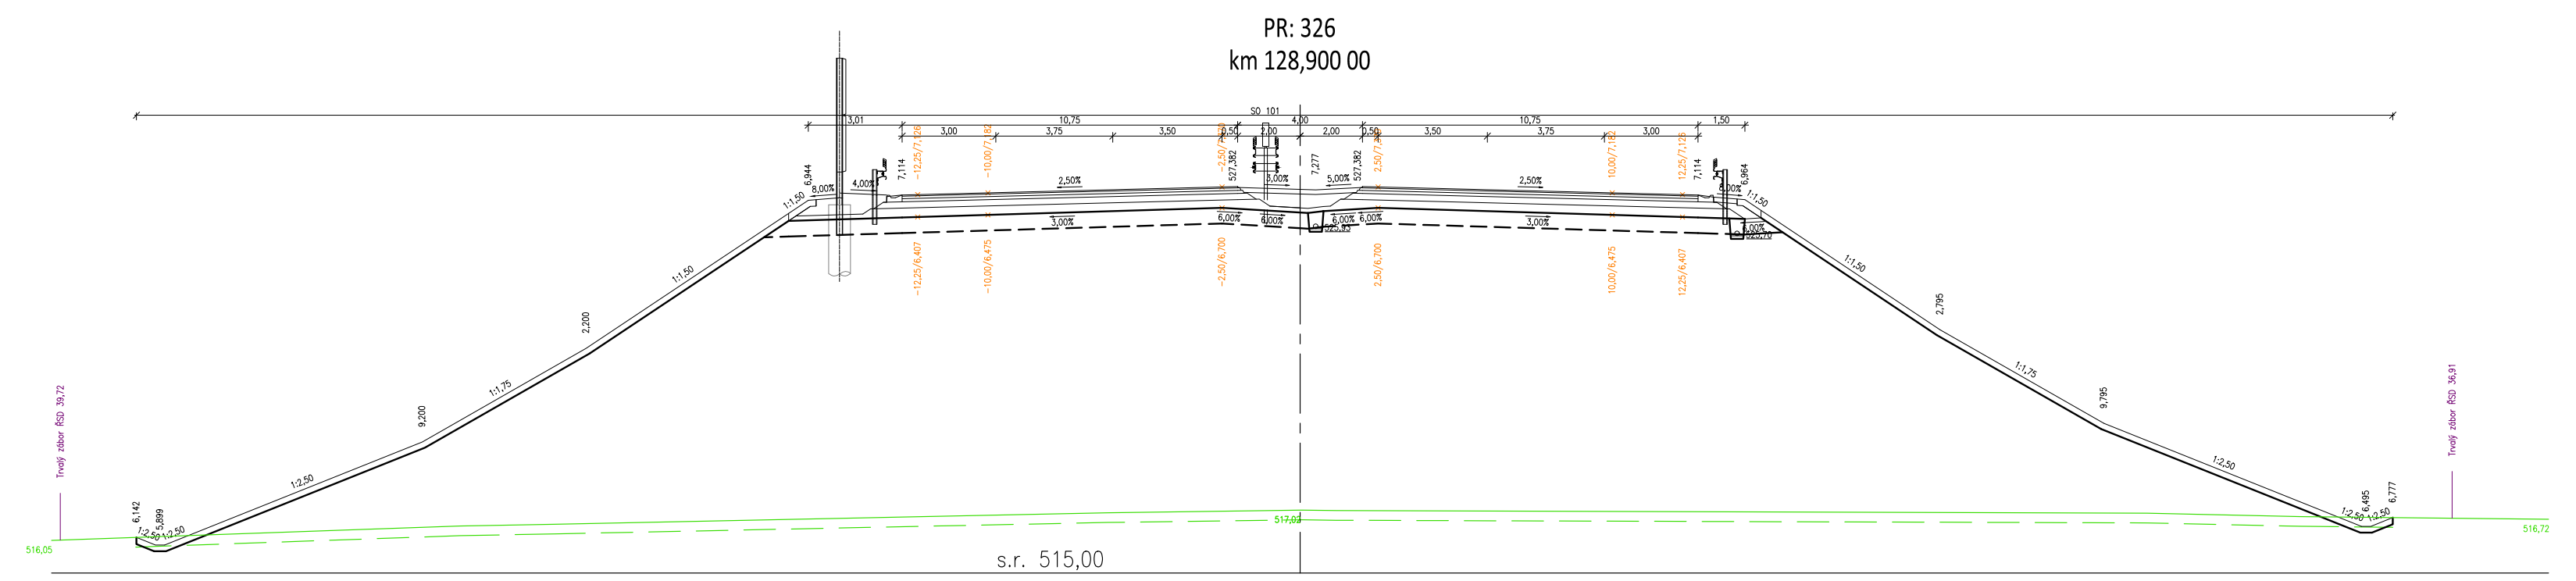
PR: 326
km 128,900 00

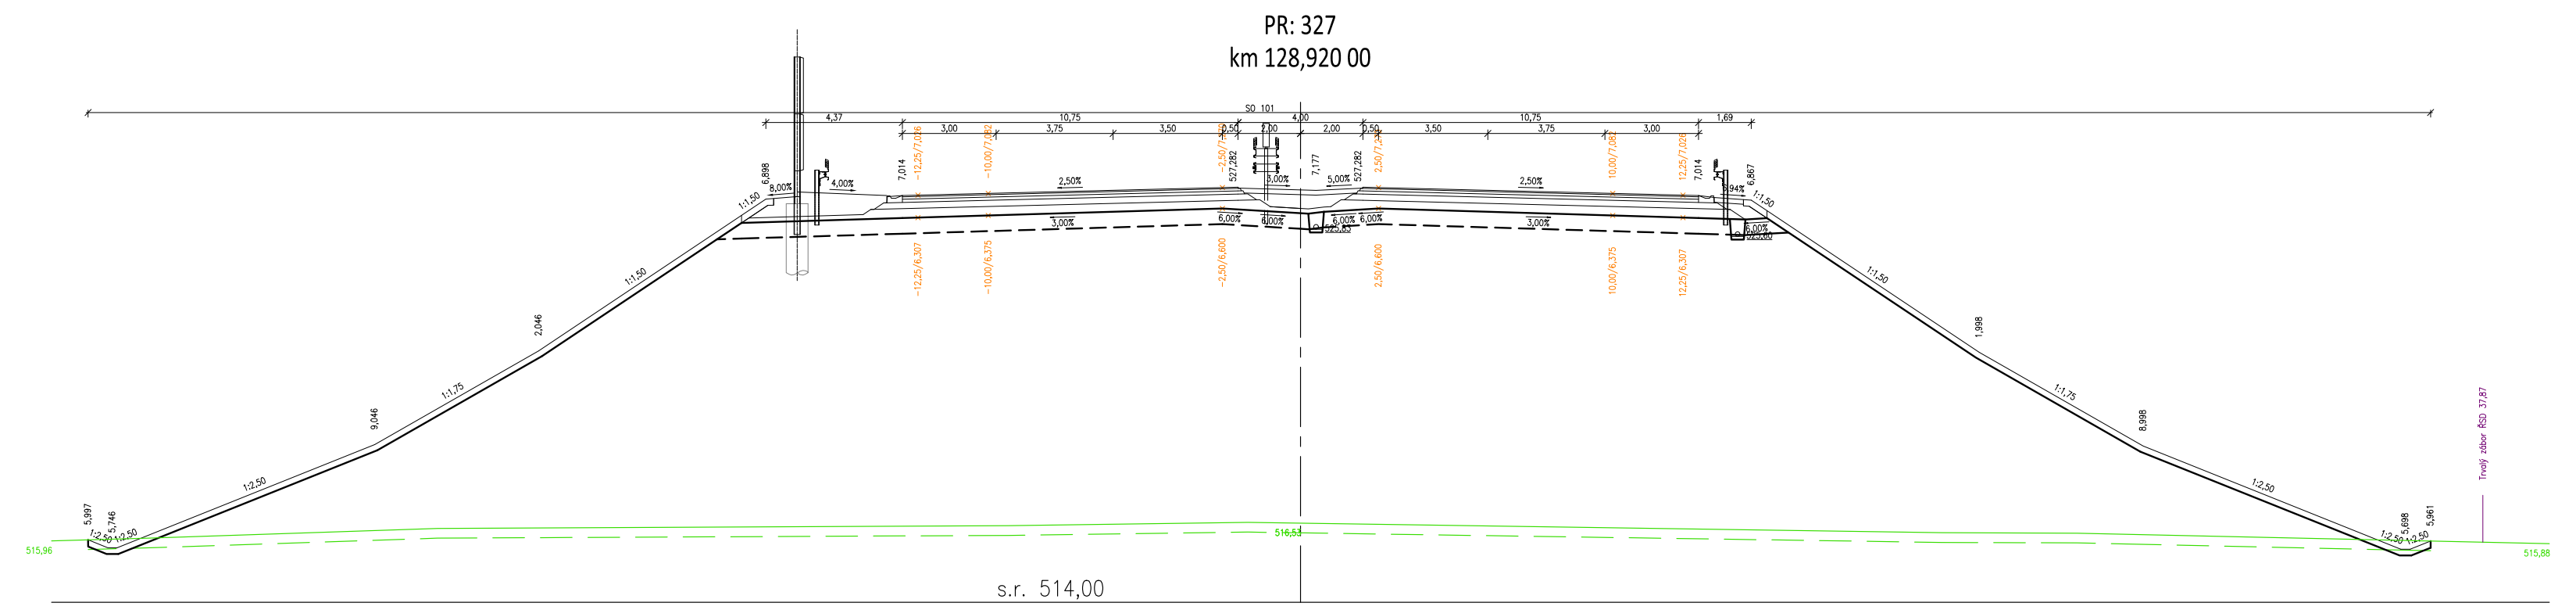
PR: 327
km 128,920 00

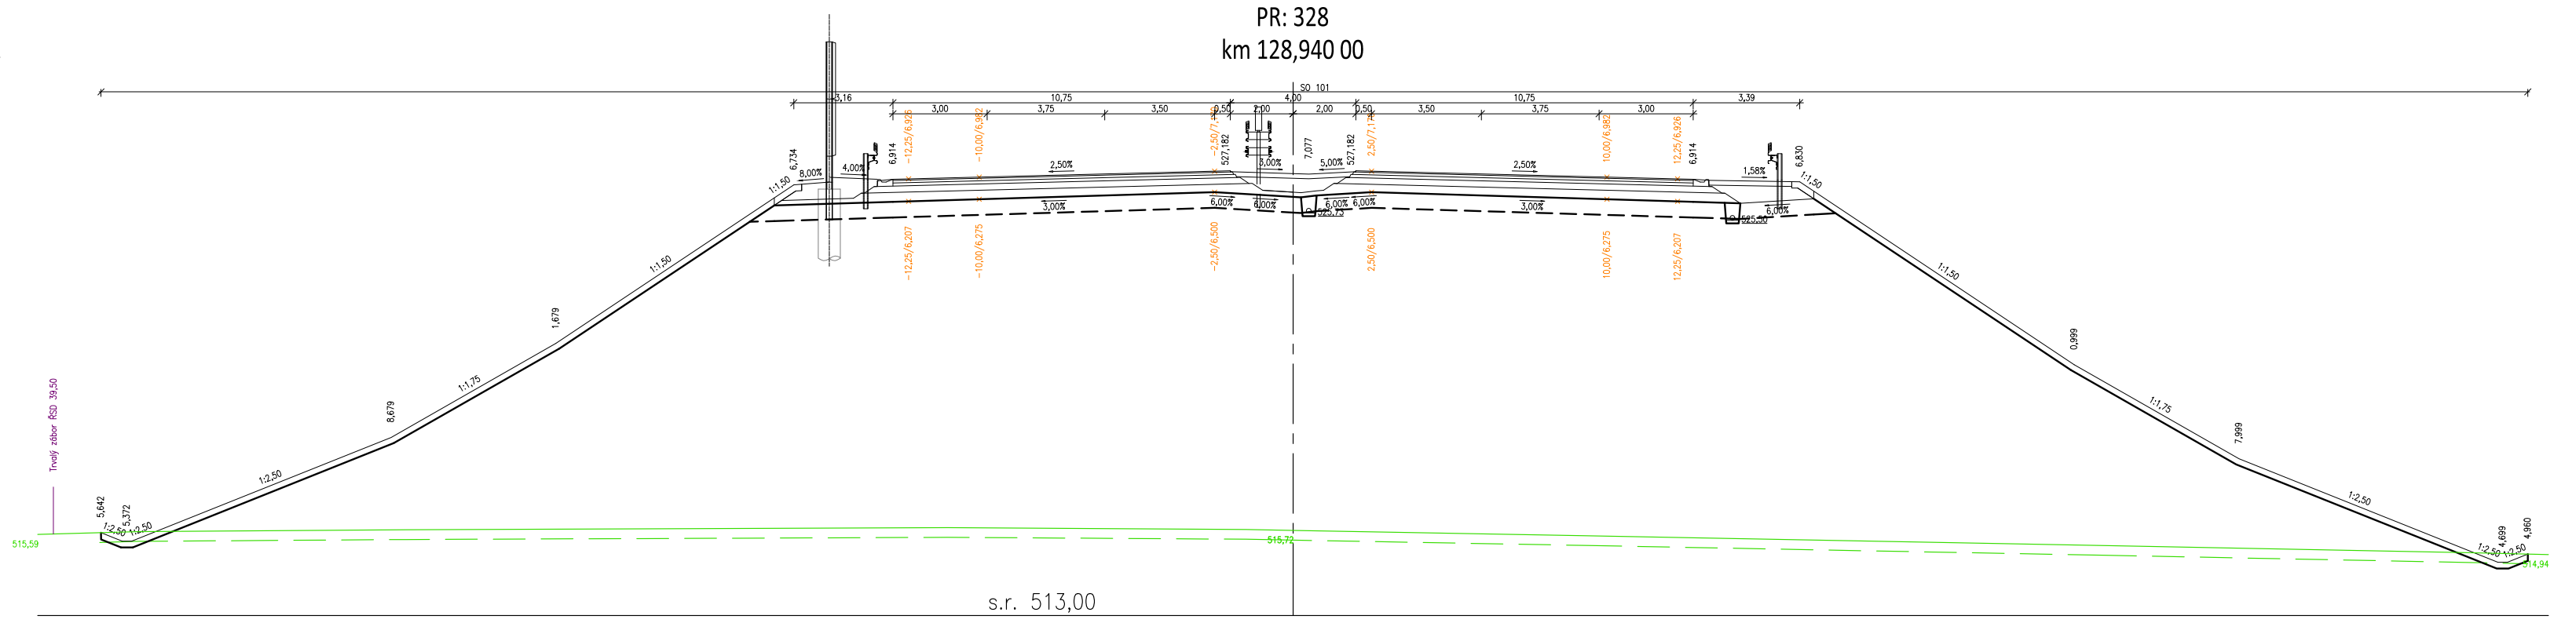
PR: 328
km 128,940 00

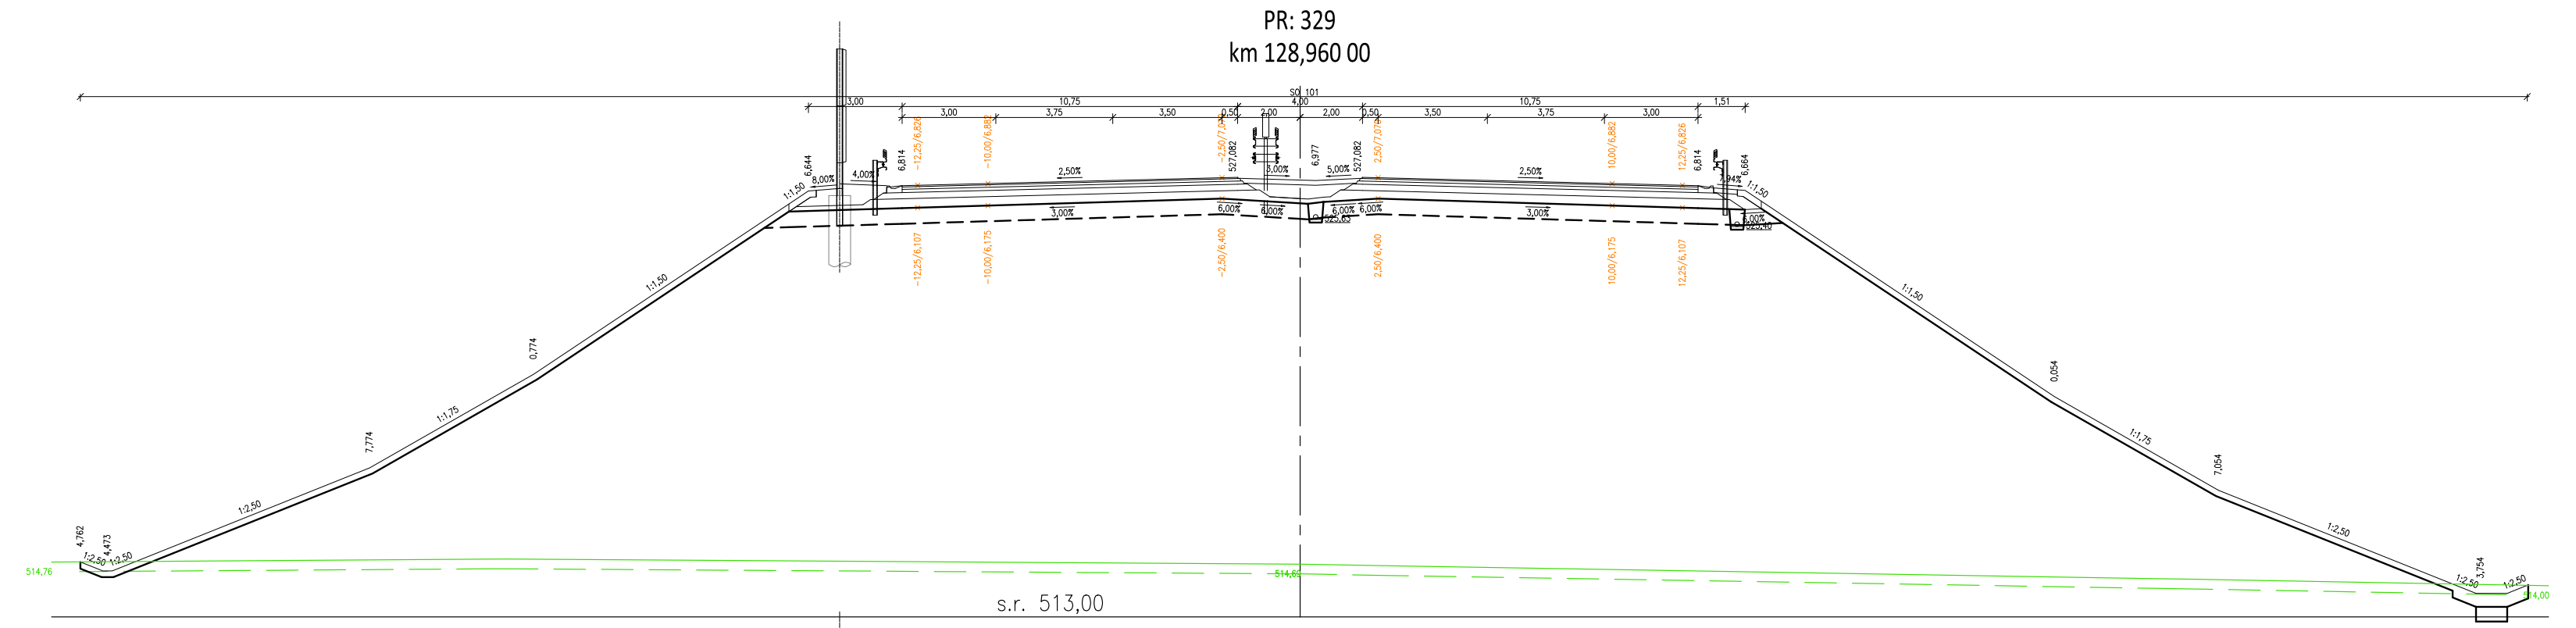
PR: 329
km 128,960 00

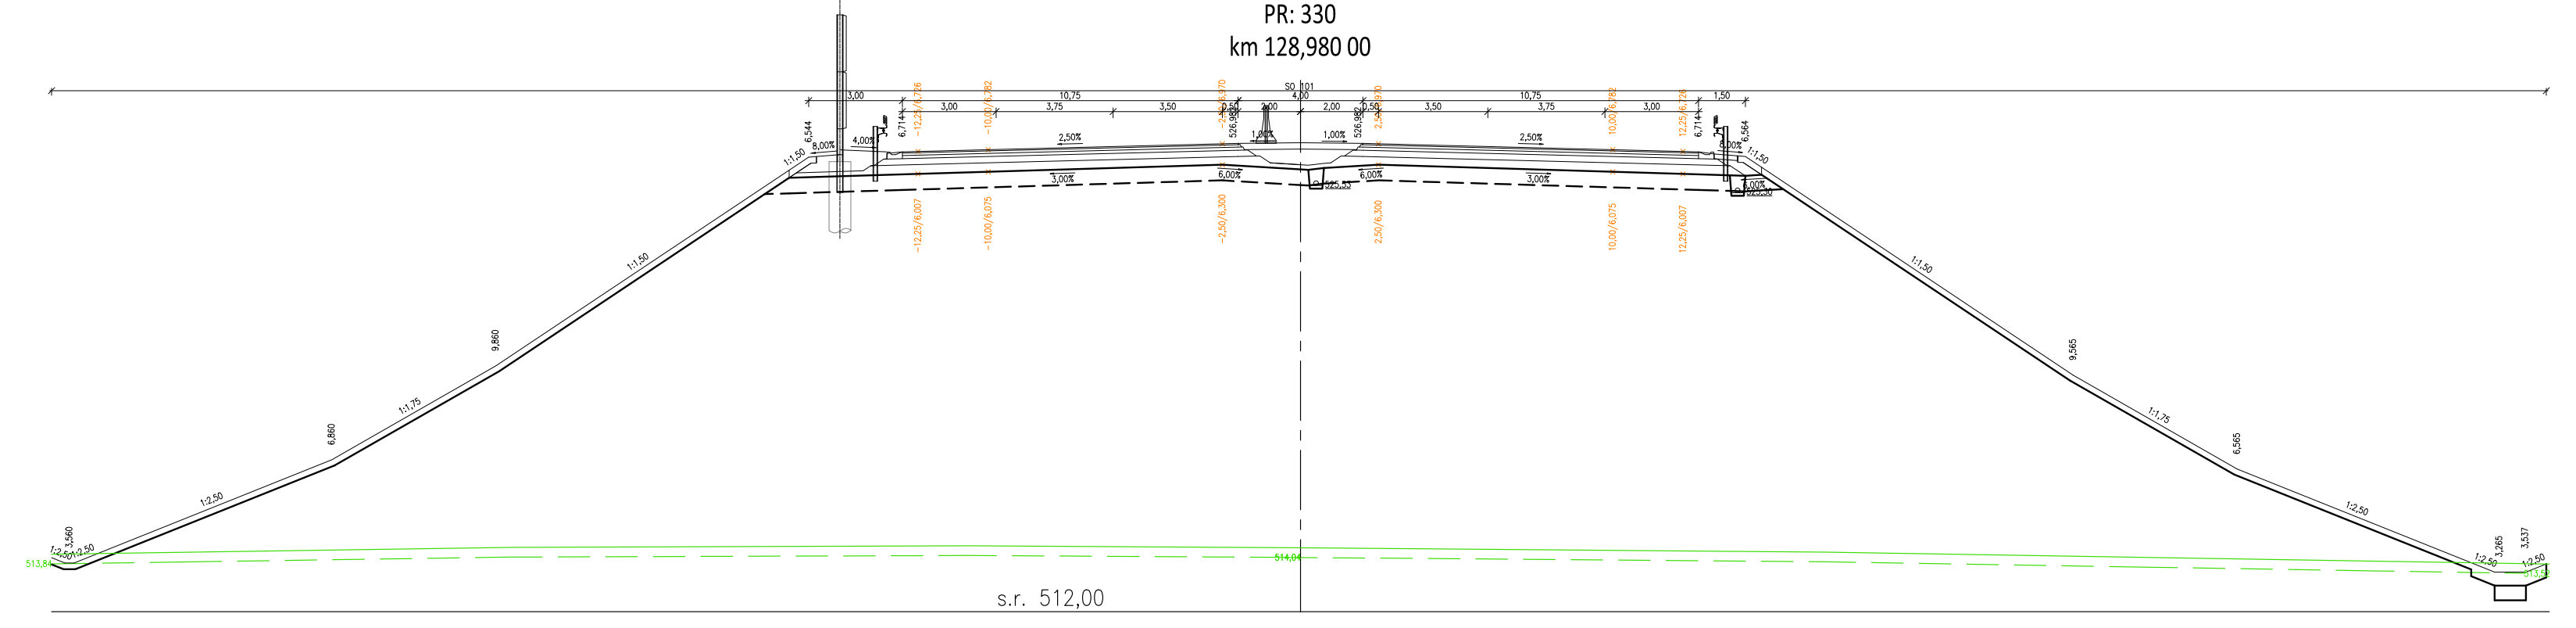
PR: 330
km 128,980 00

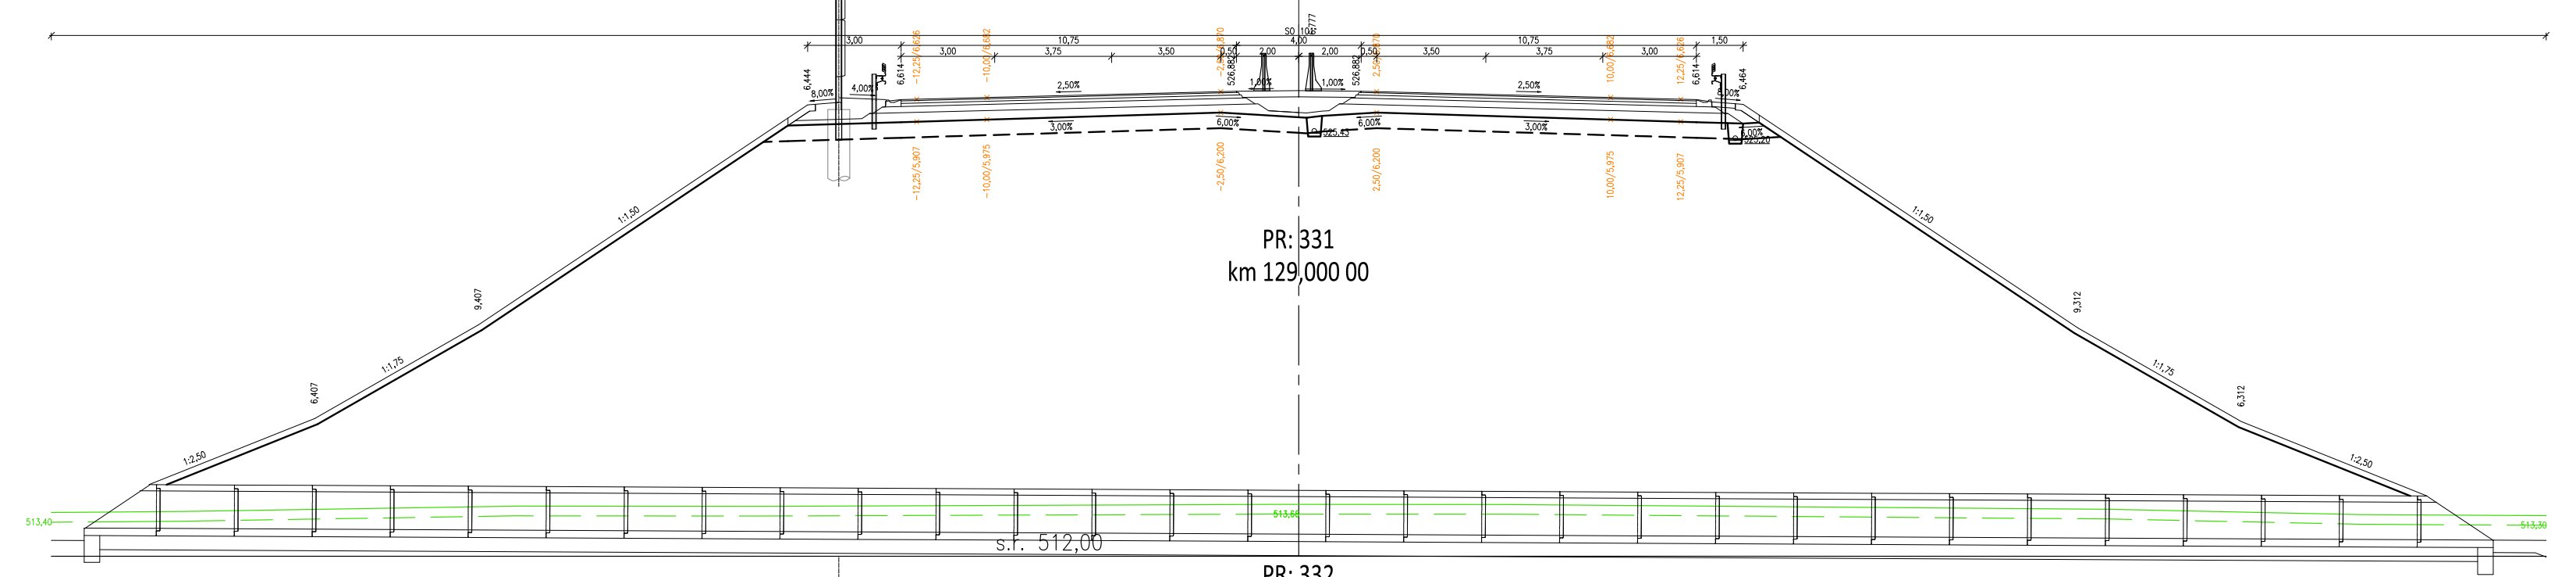
PR: 331
km 129,000 00

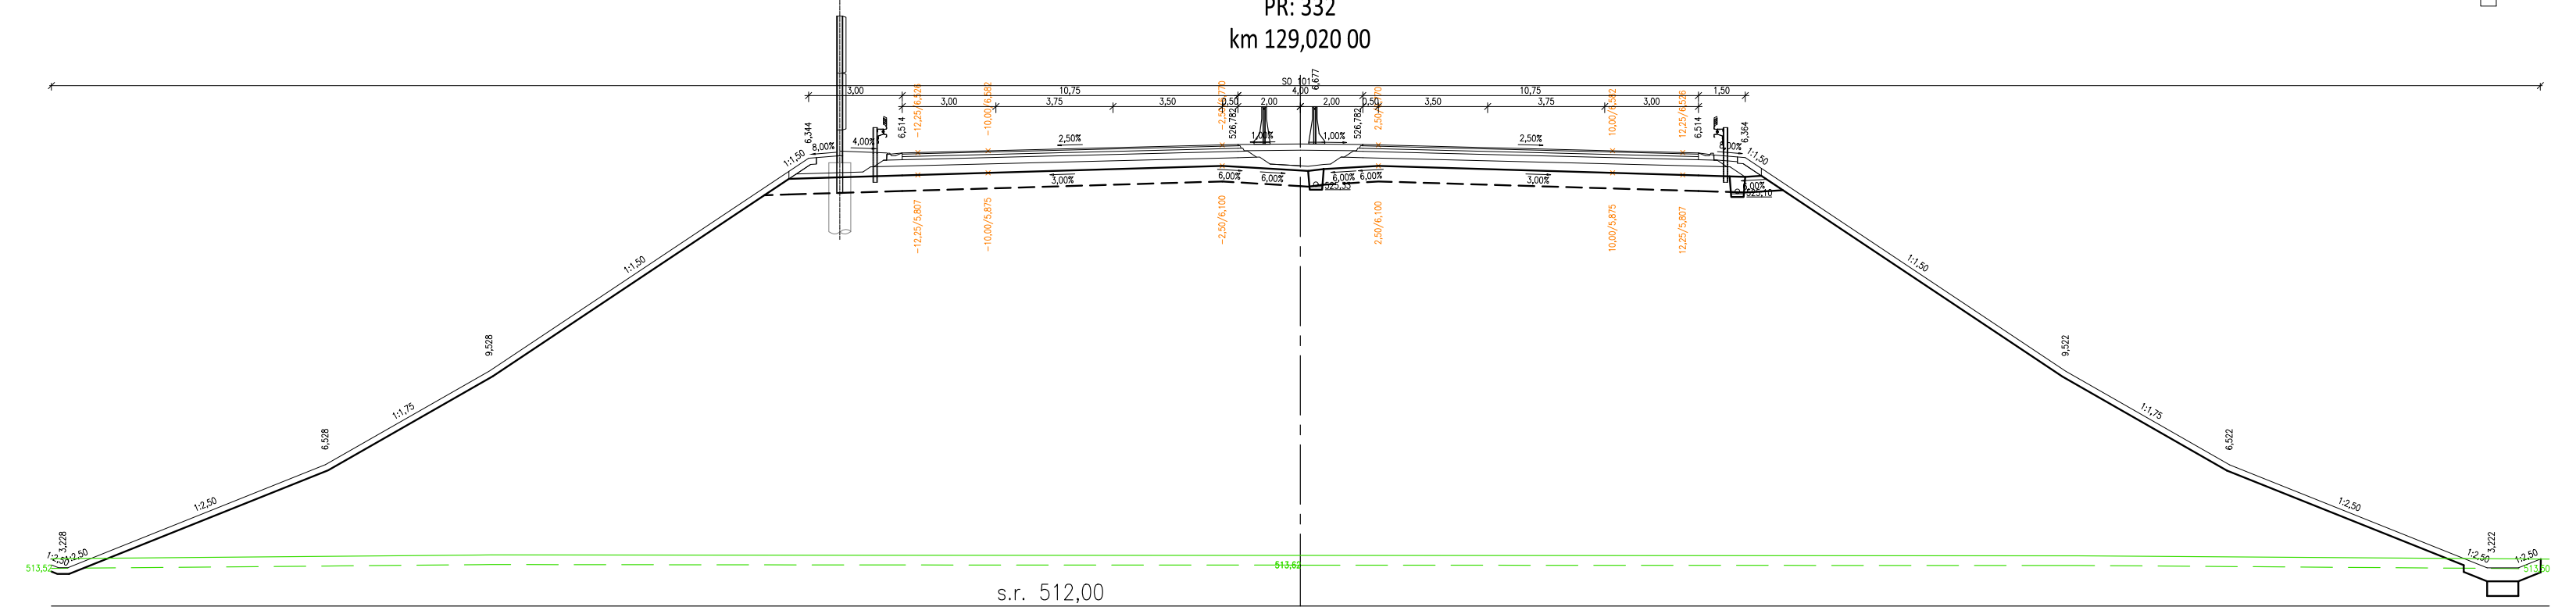
PR: 332
km 129,020 00

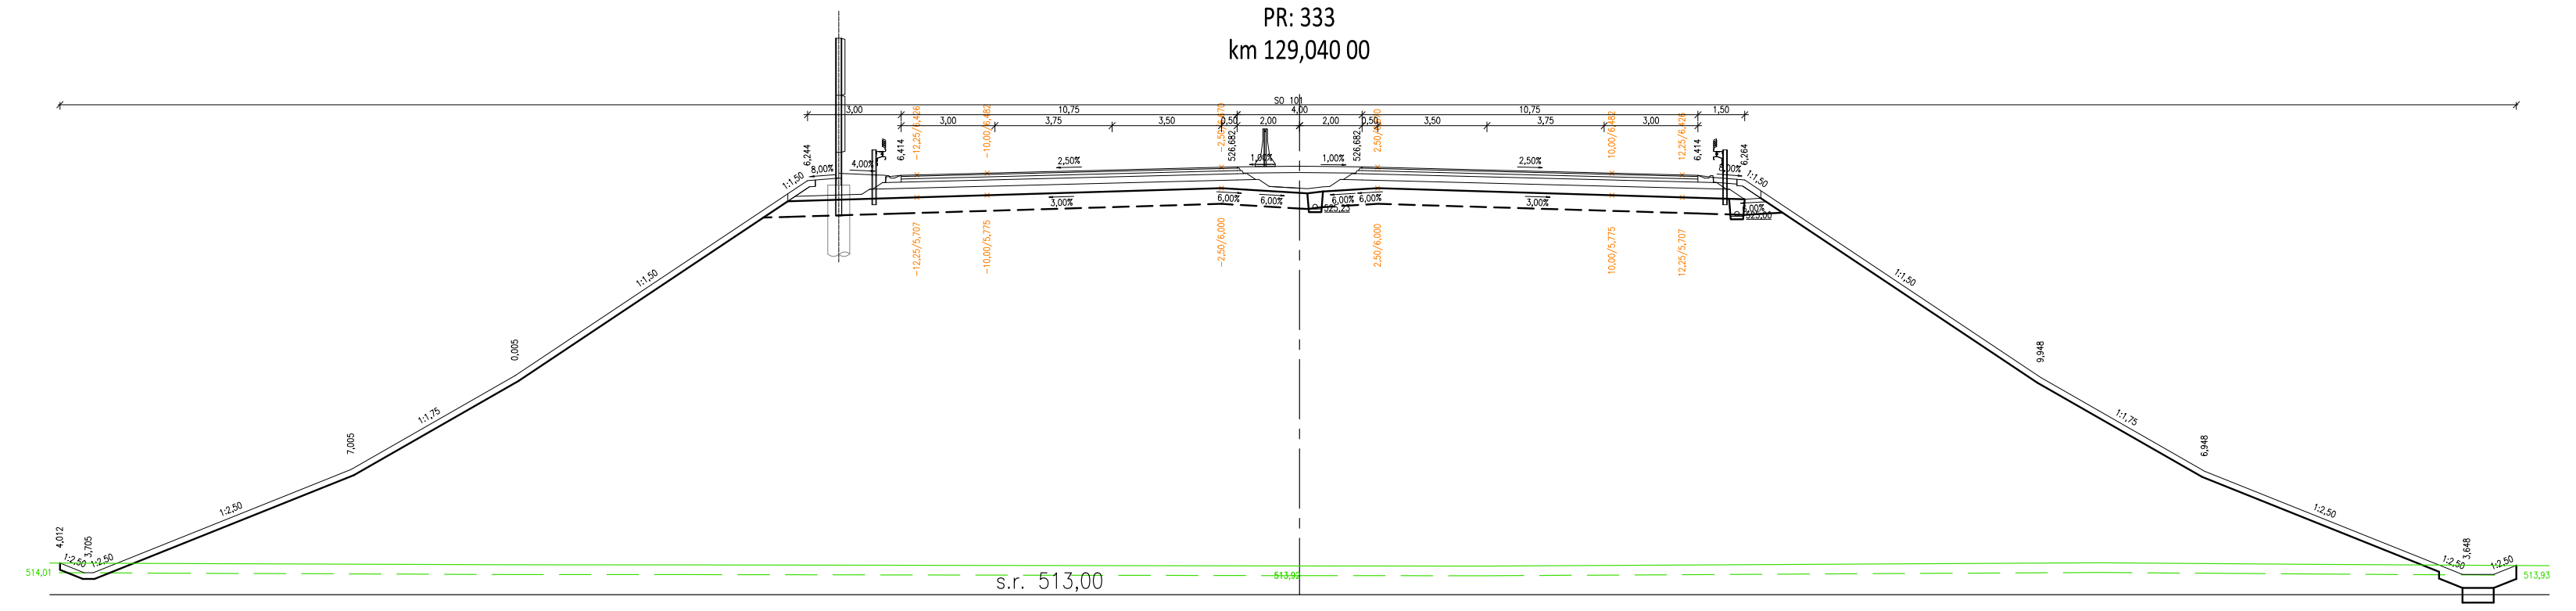
PR: 333
km 129,040 00

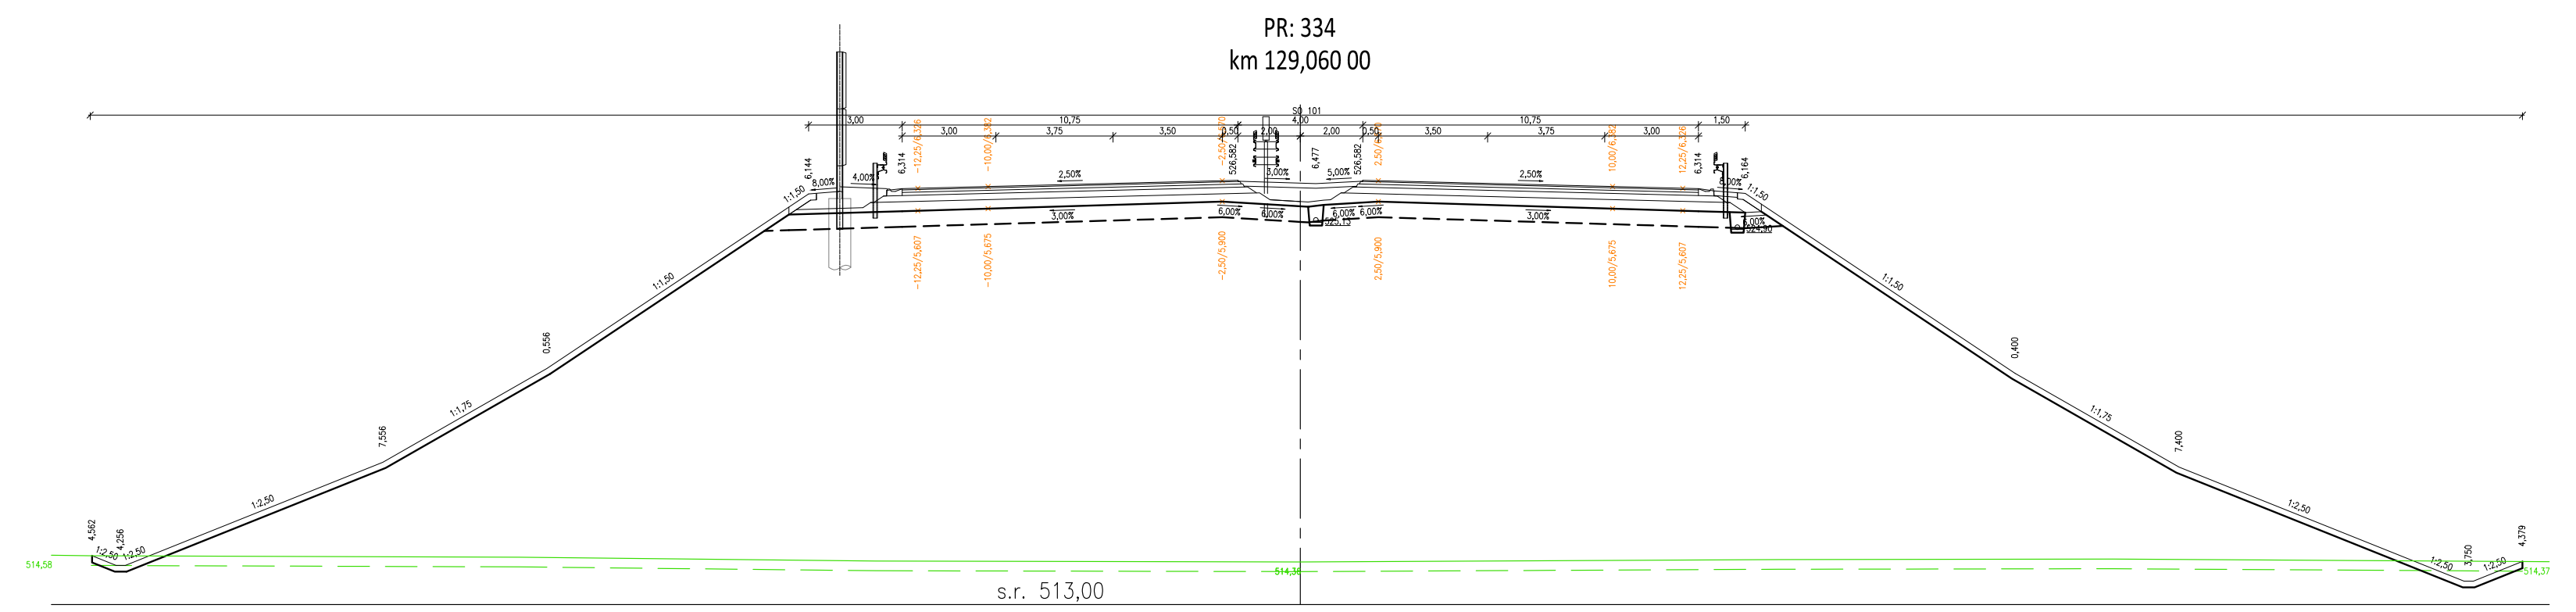
PR: 334
km 129,060 00

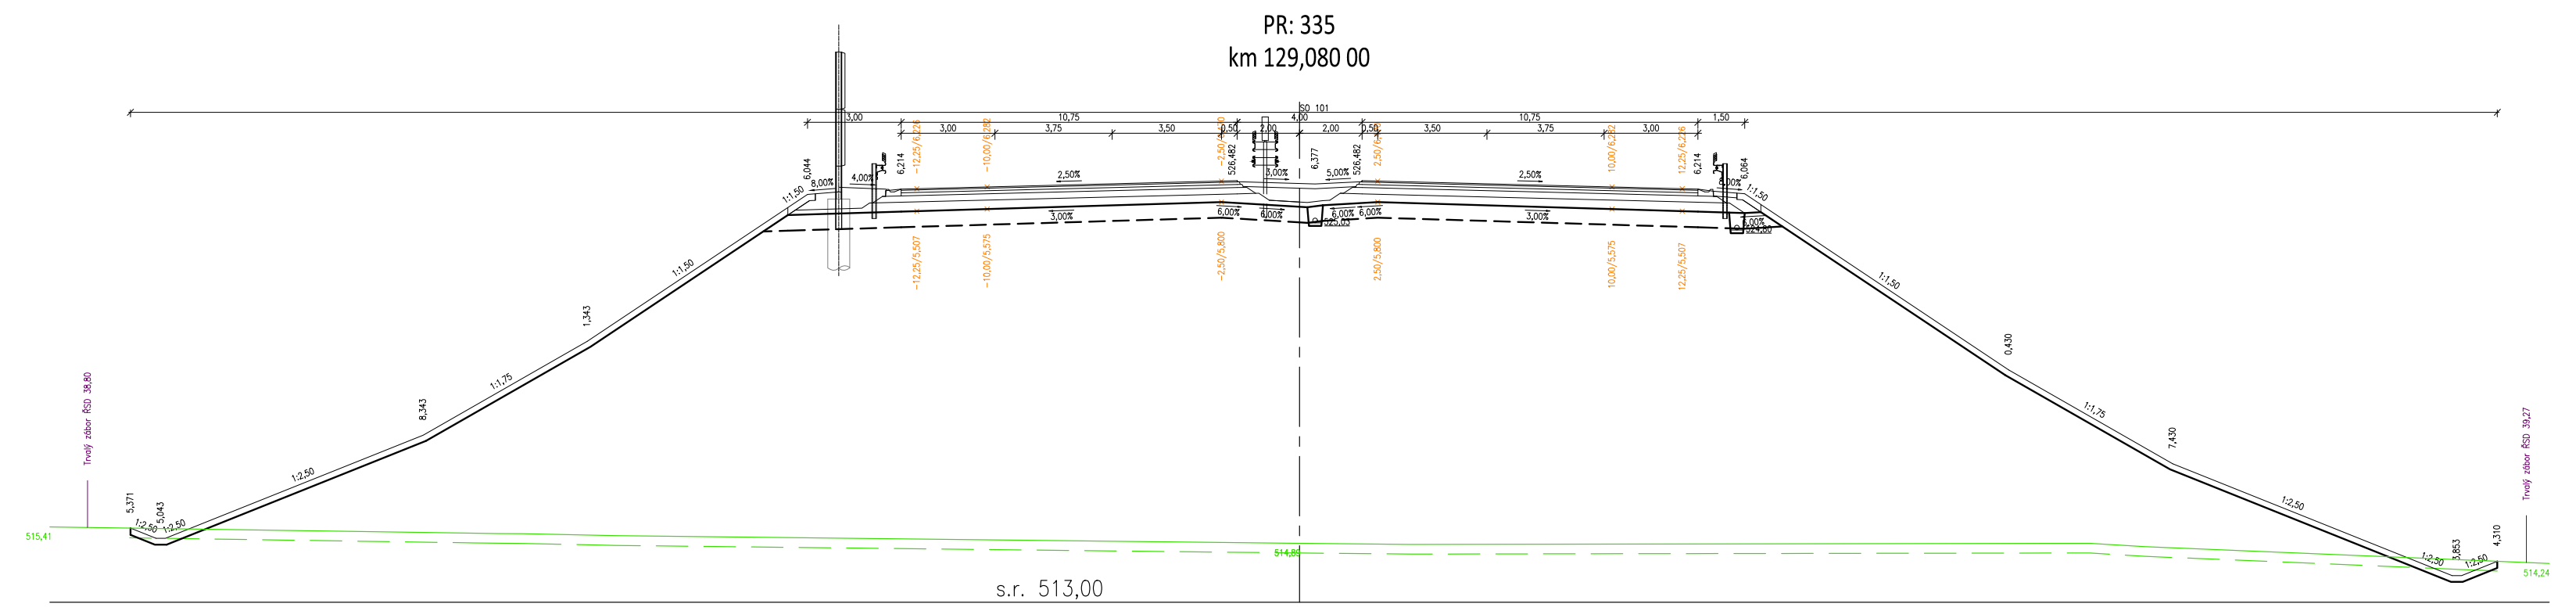
PR: 335
km 129,080 00

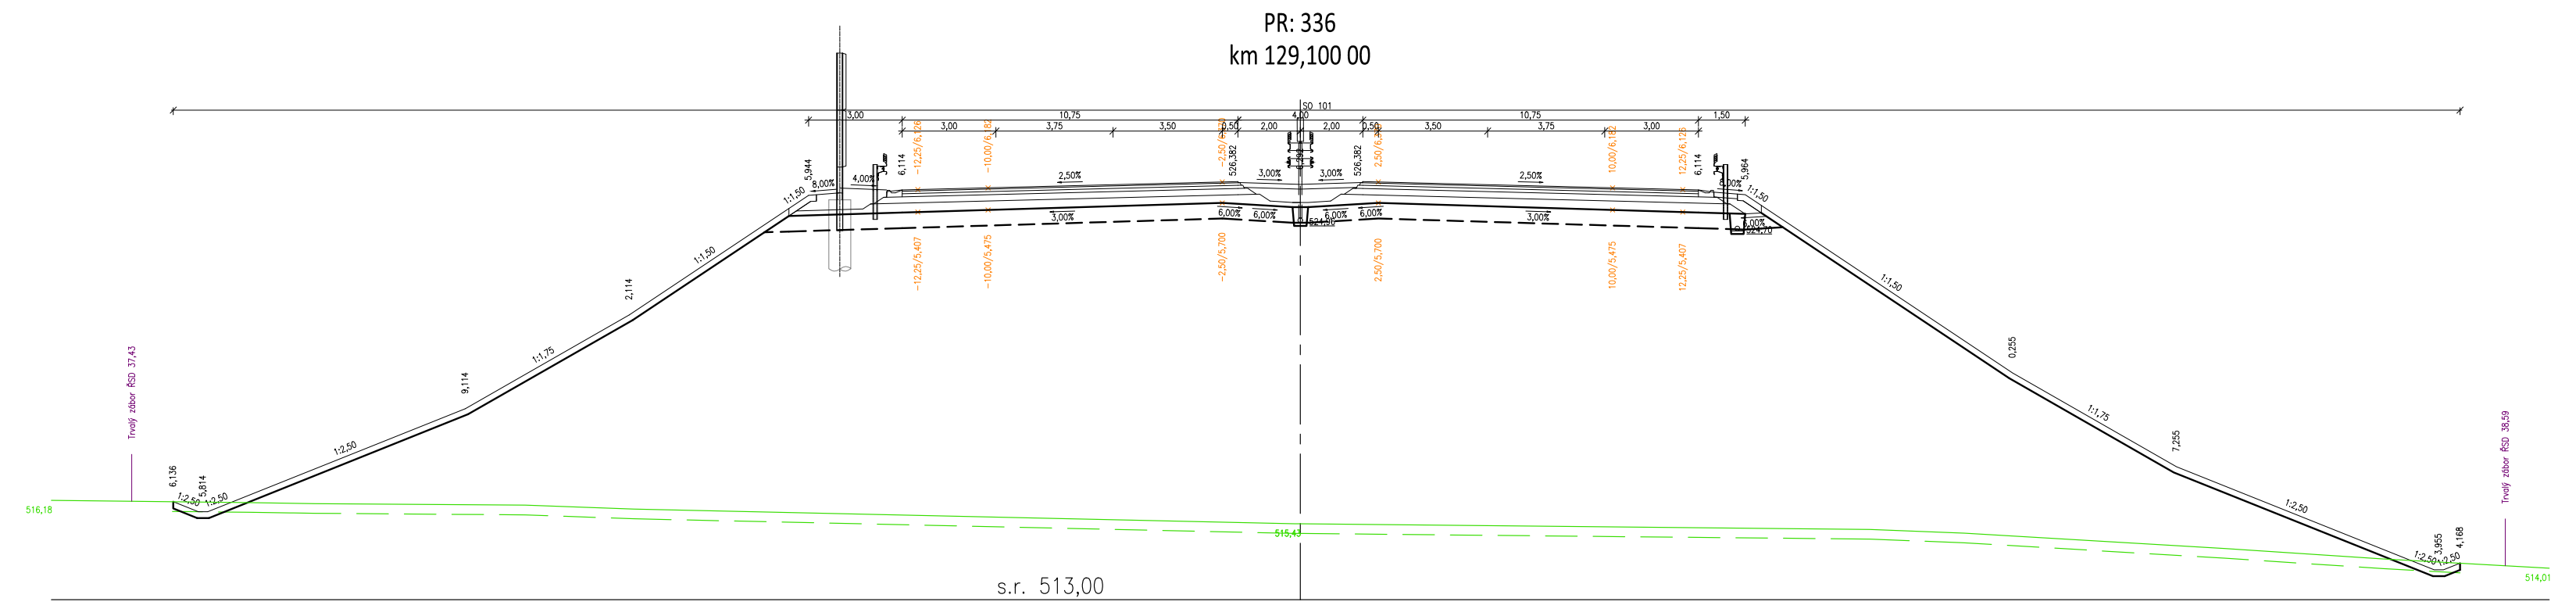
PR: 336
km 129,100 00

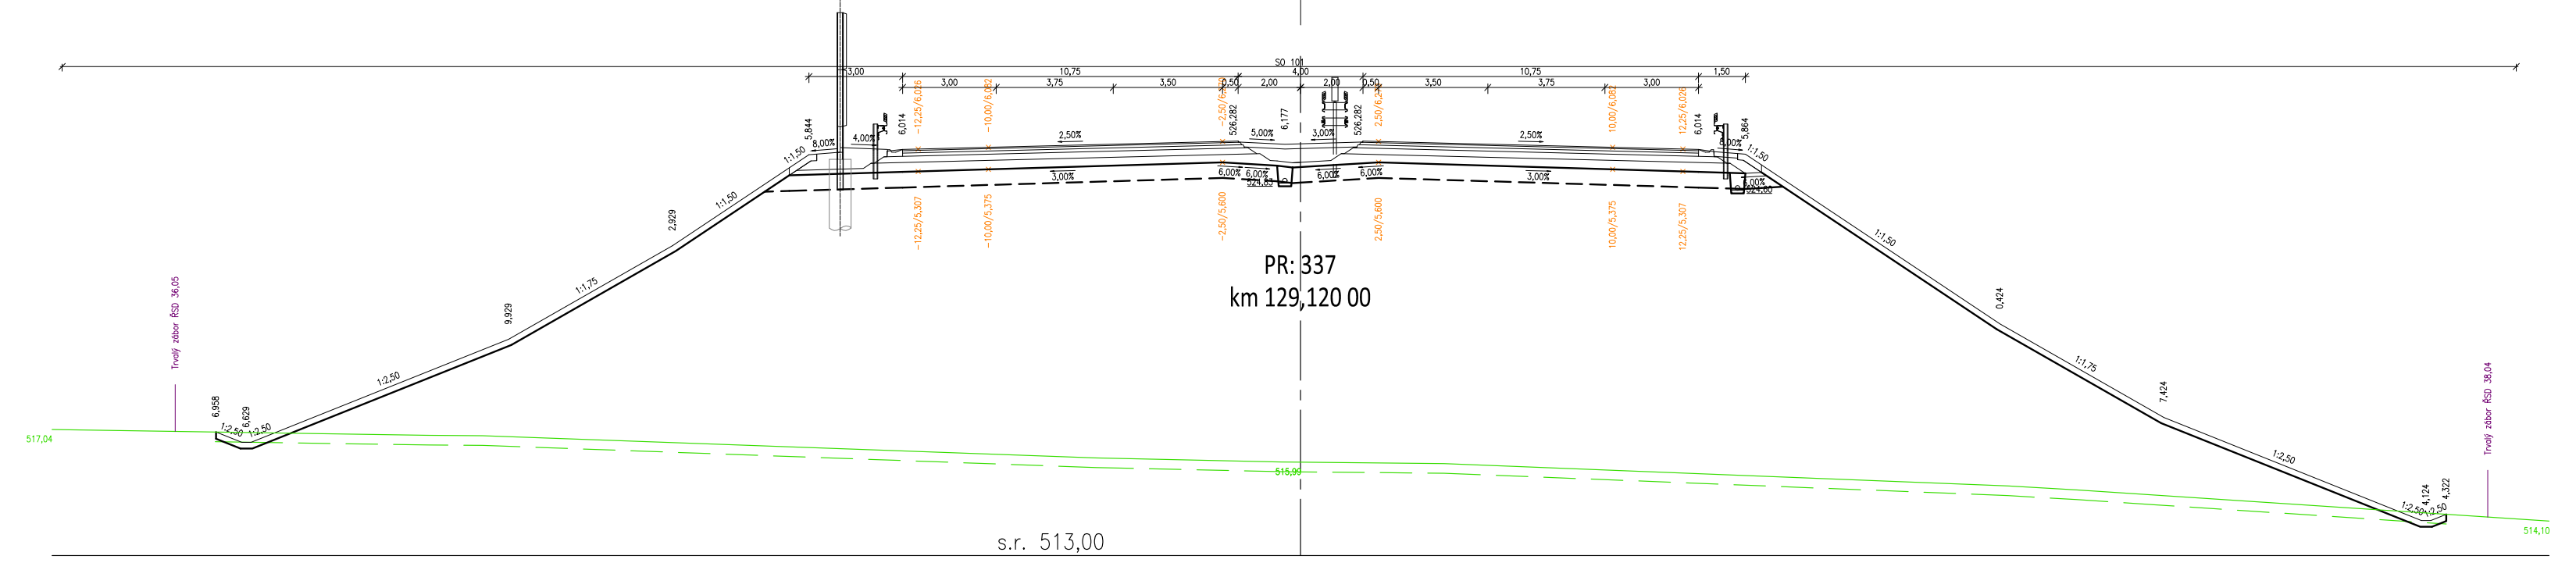
PR: 337
km 129,120 00

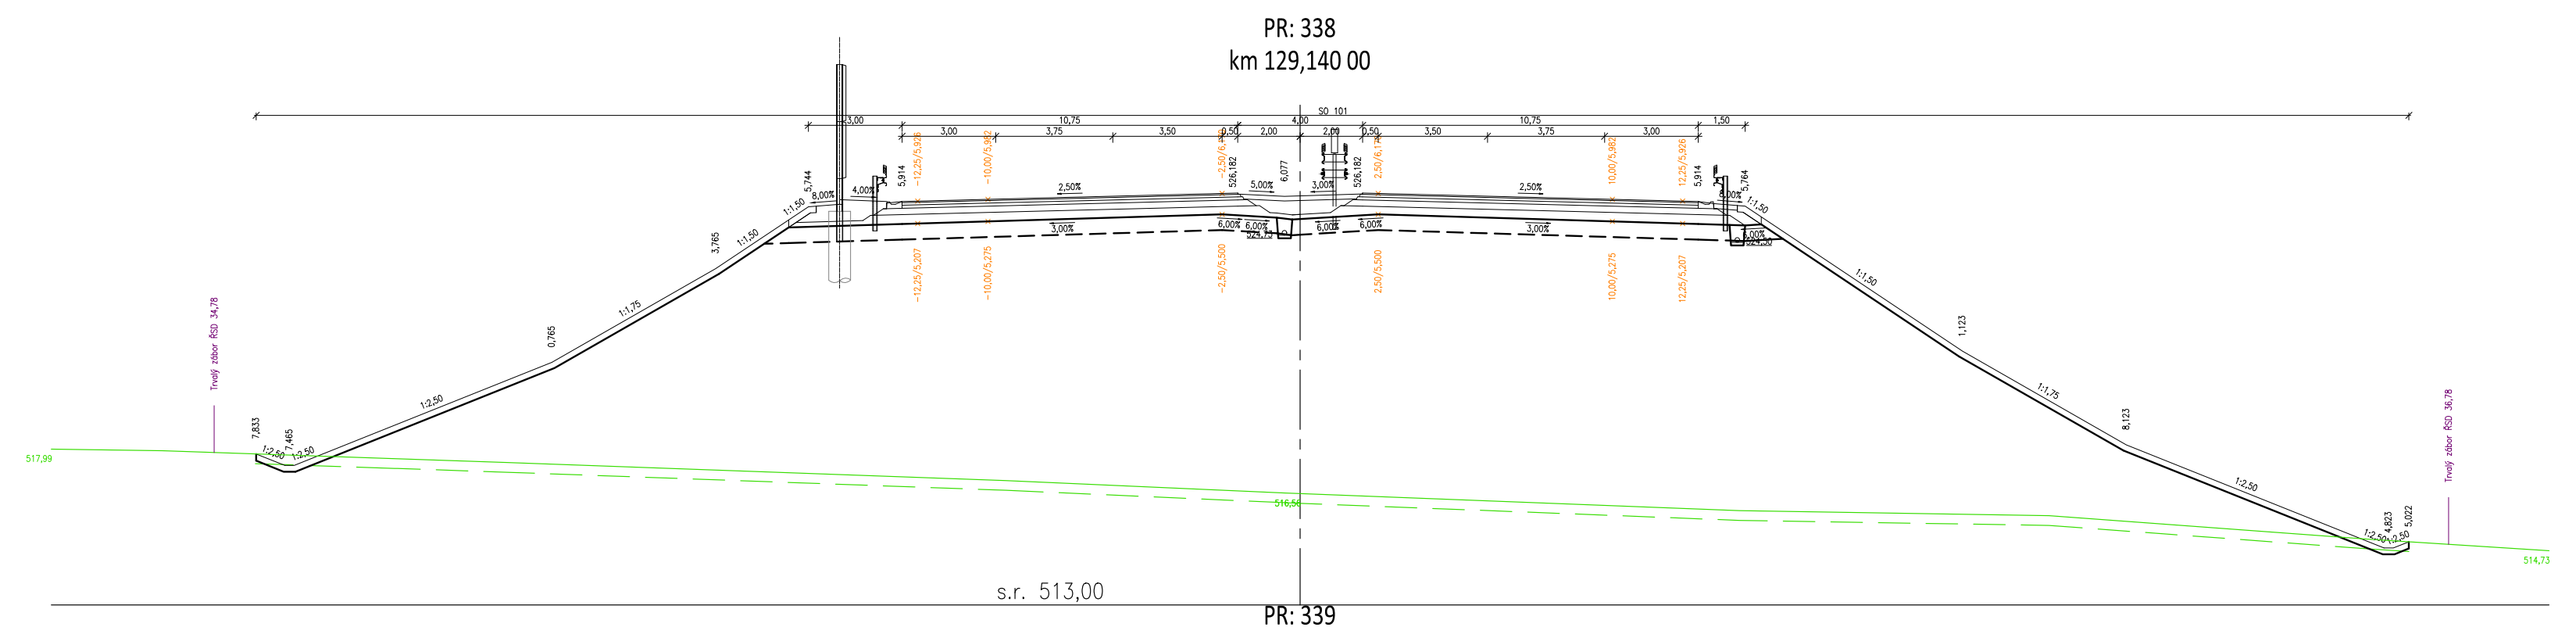
PR: 338
km 129,140 00

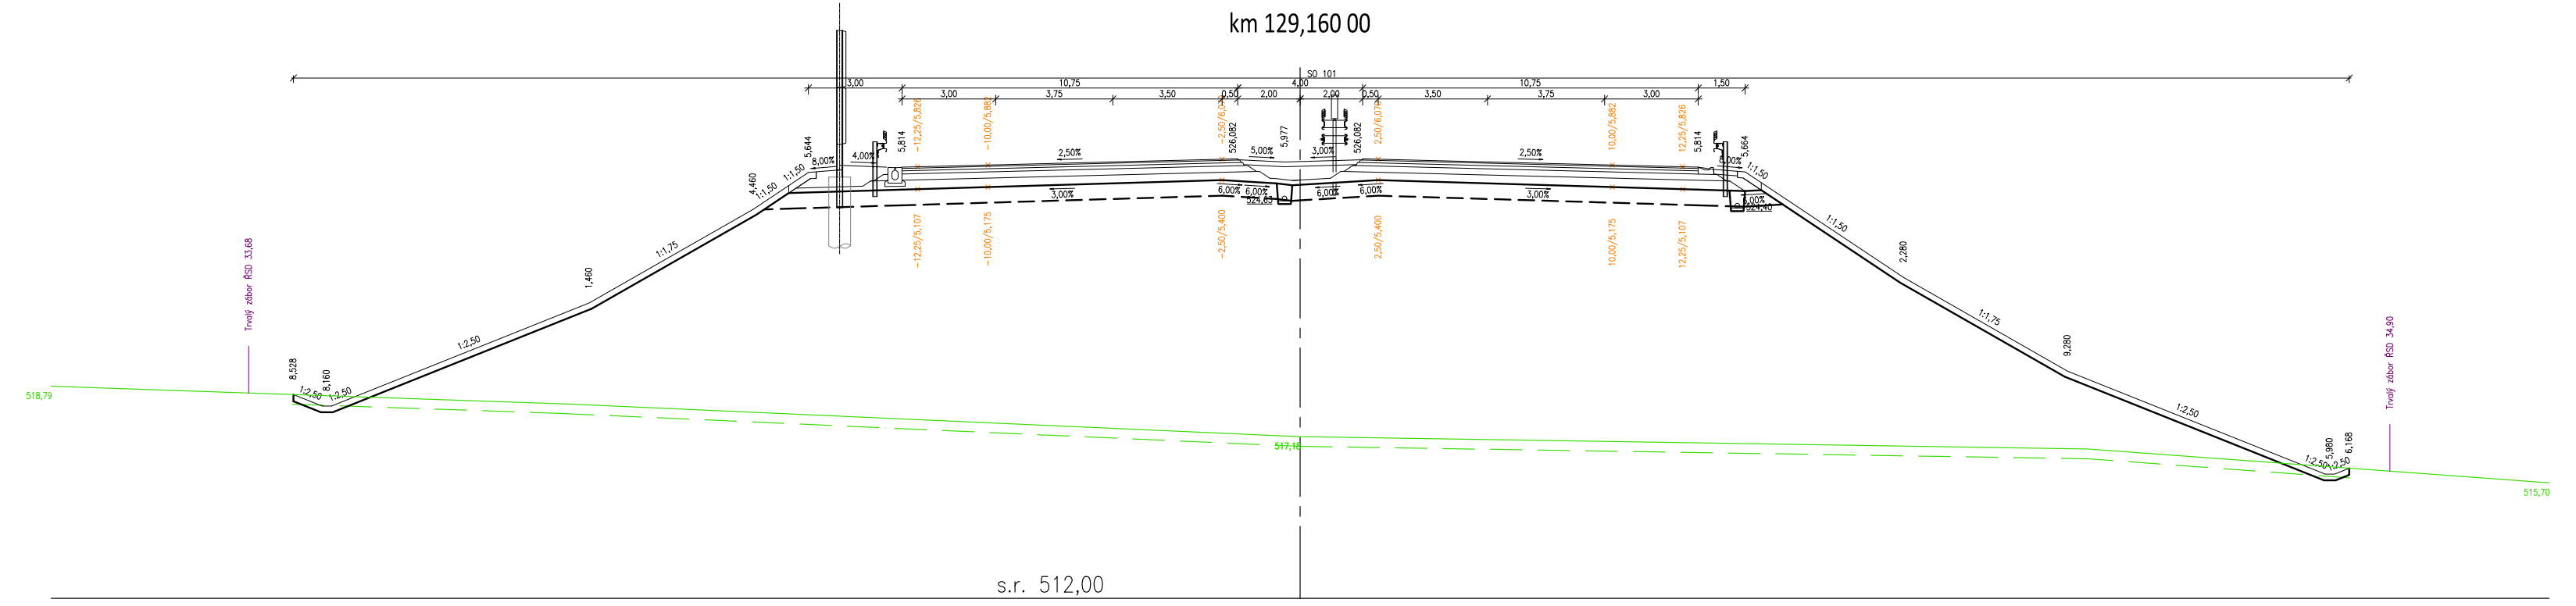
PR: 339
km 129,160 00

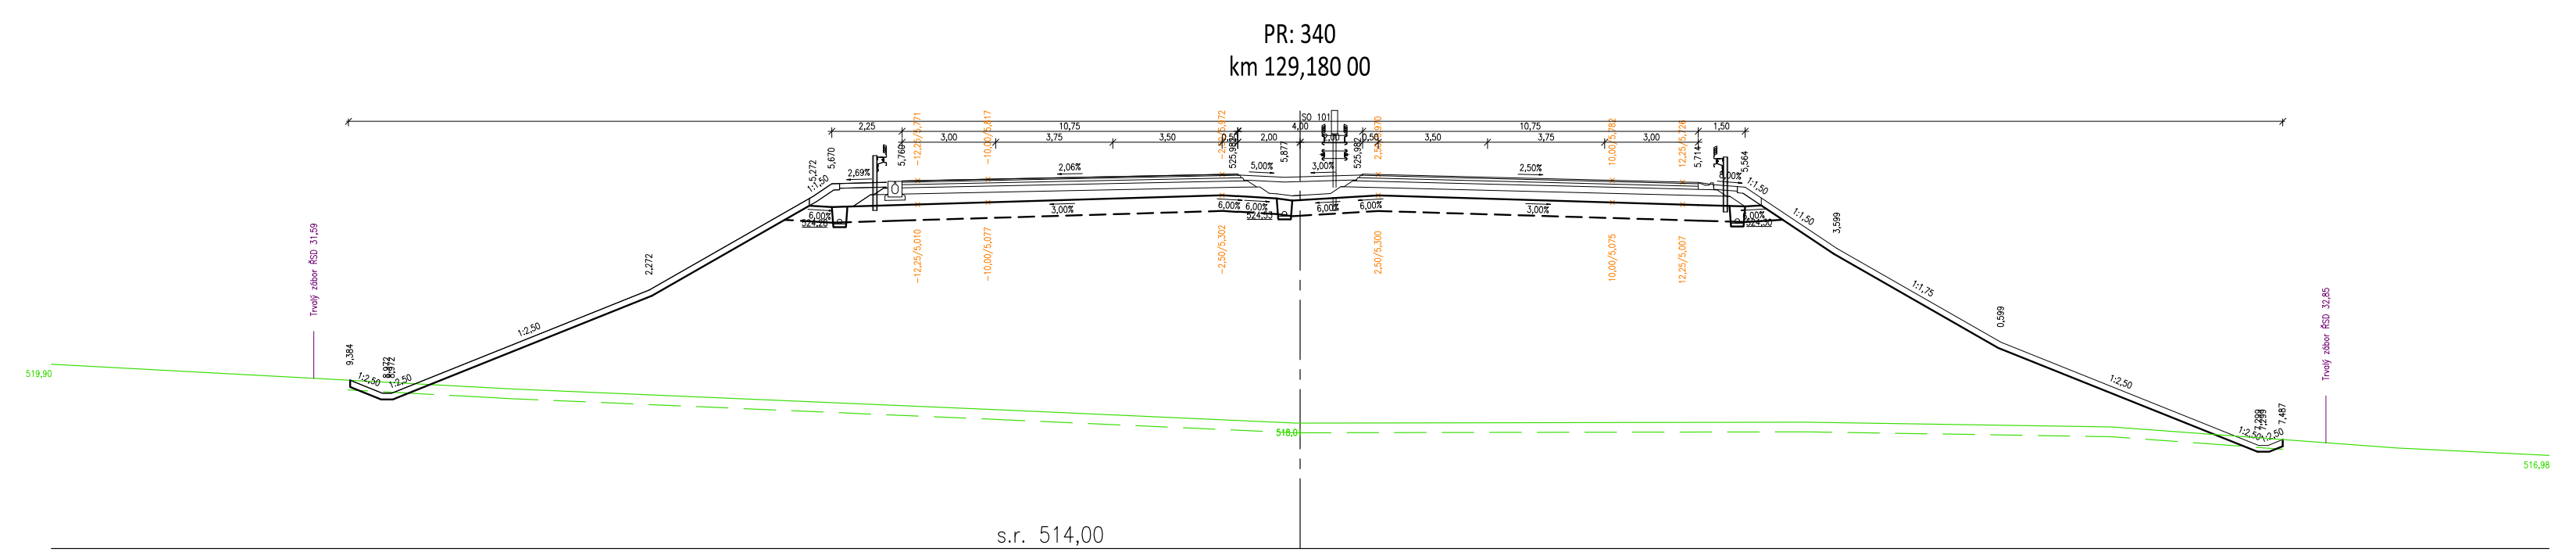
PR: 340
km 129,180 00

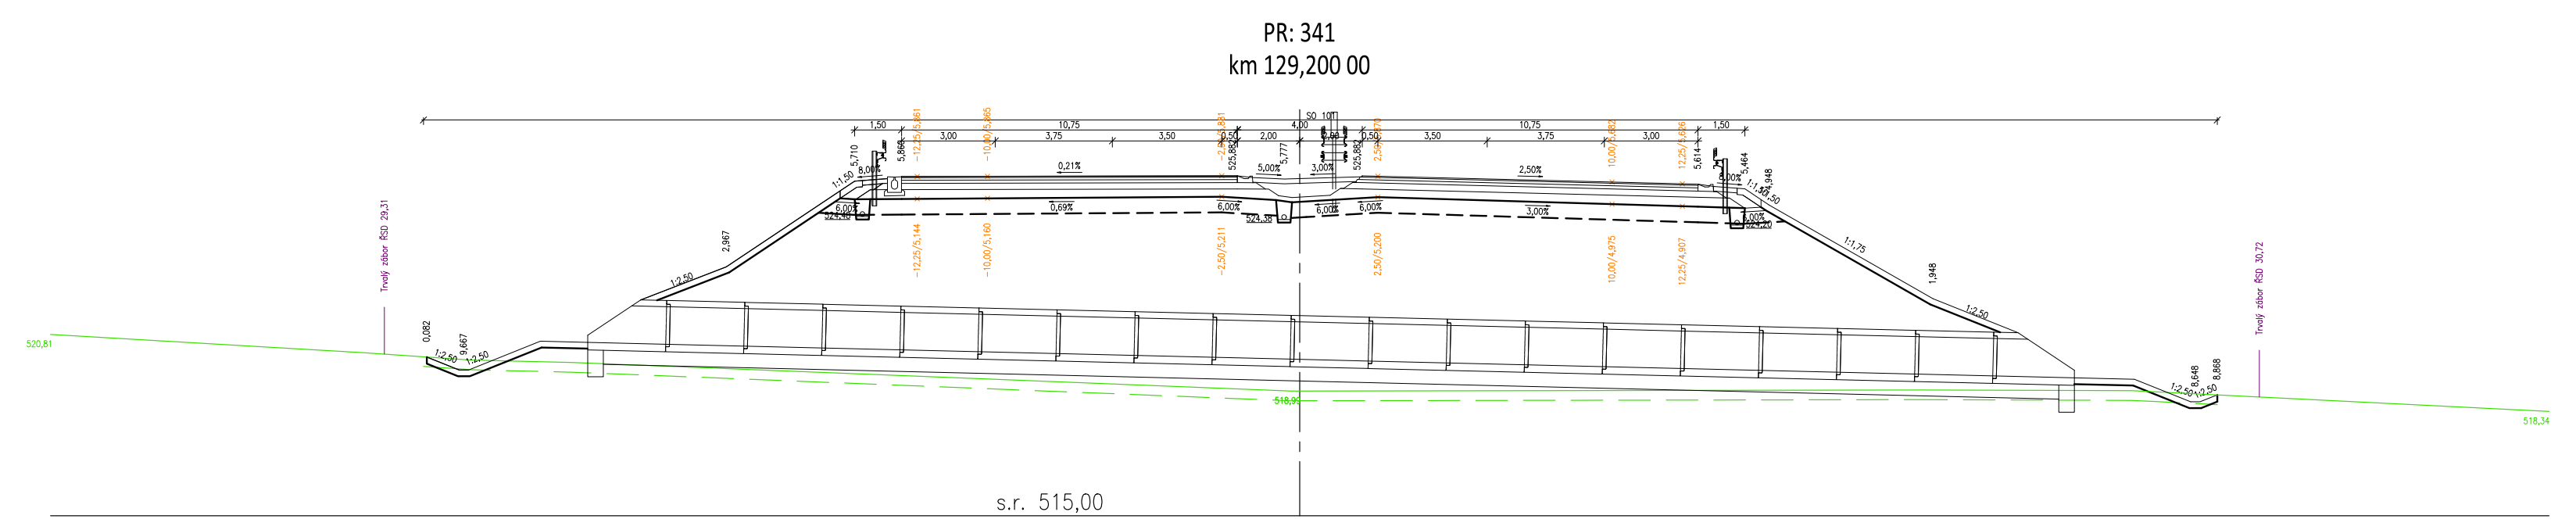
PR: 341
km 129,200 00

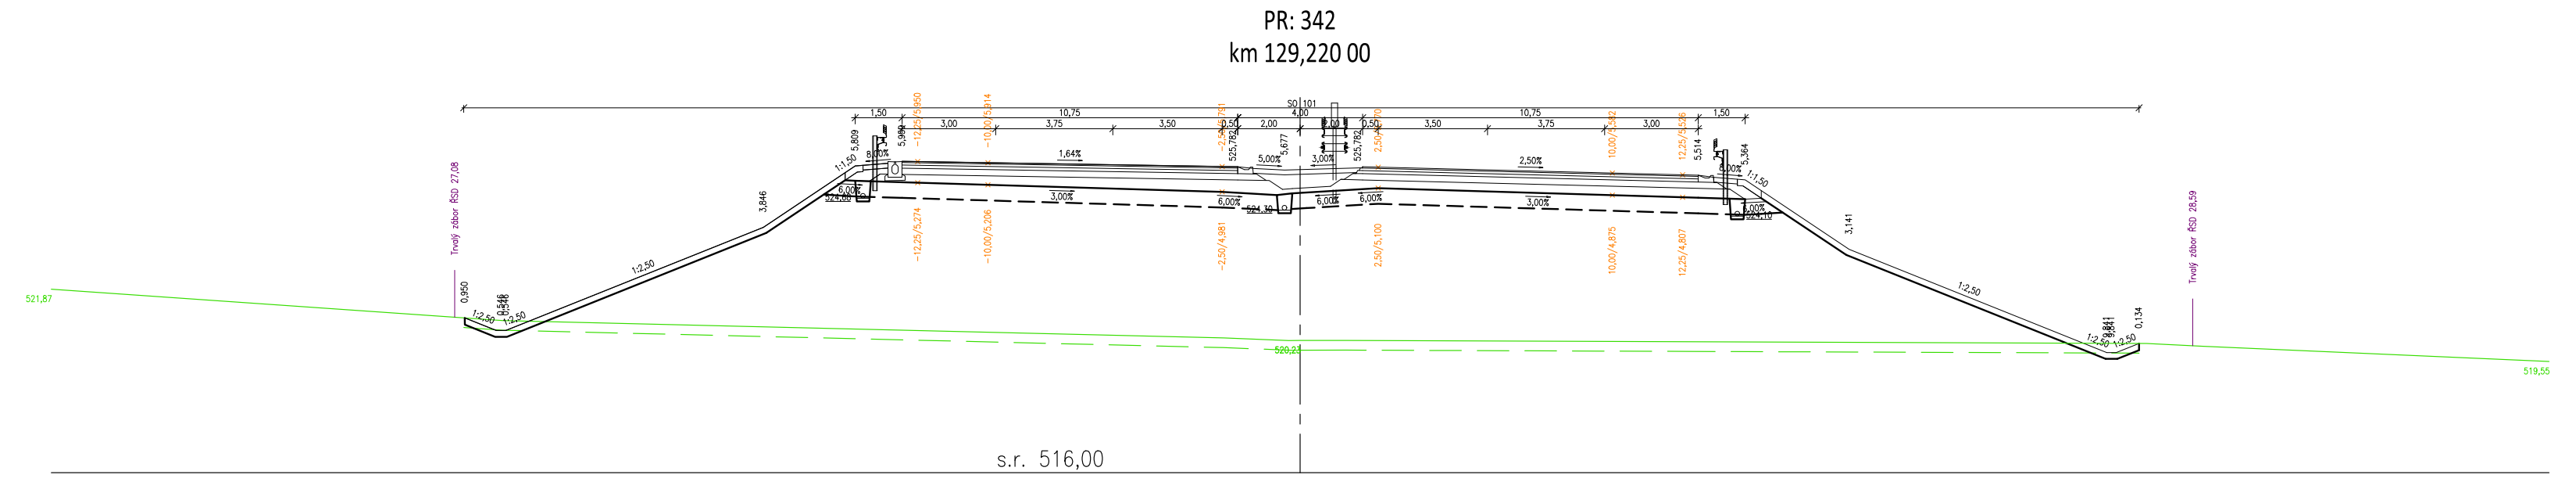
PR: 342
km 129,220 00

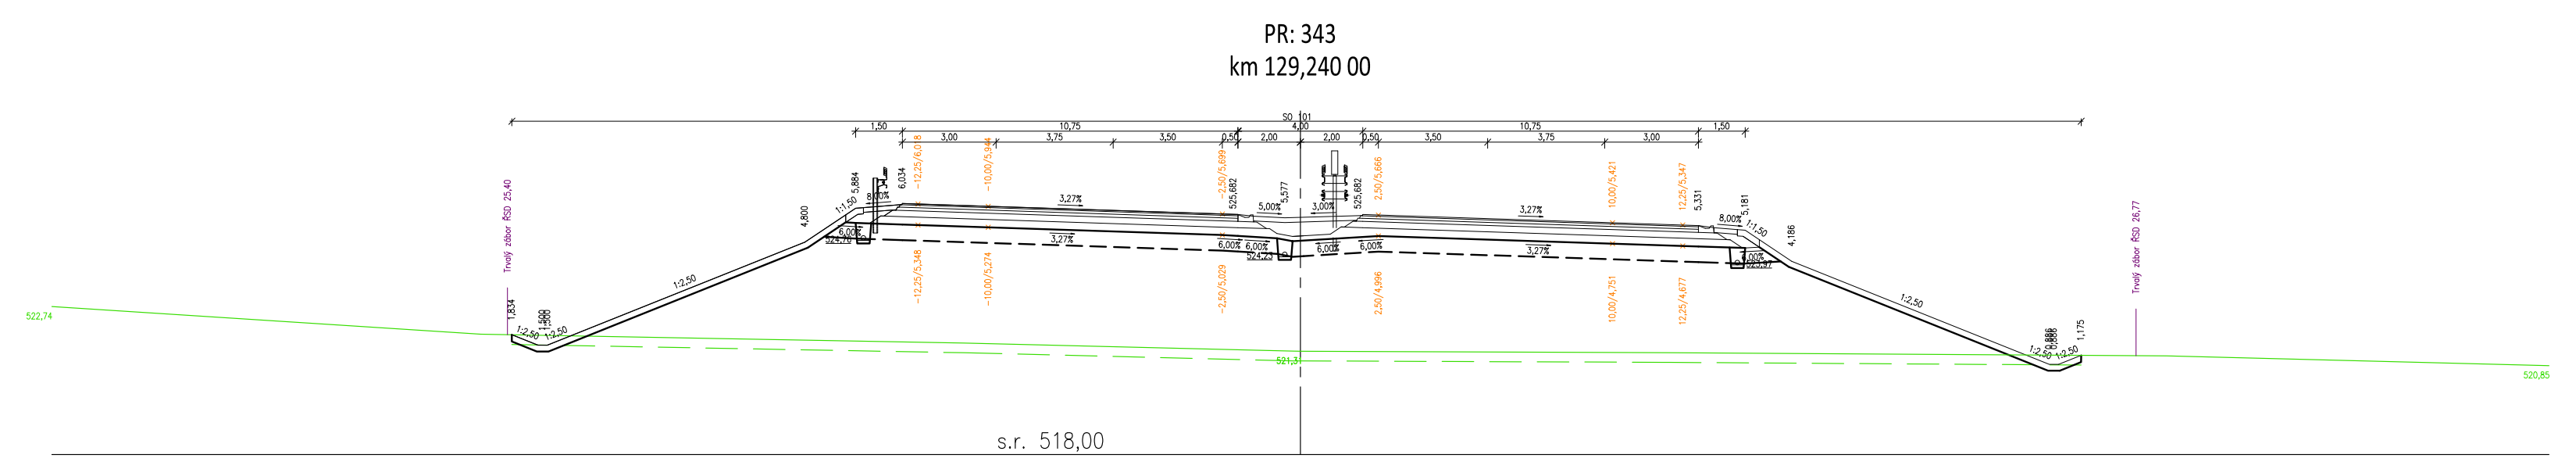
PR: 343
km 129,240 00

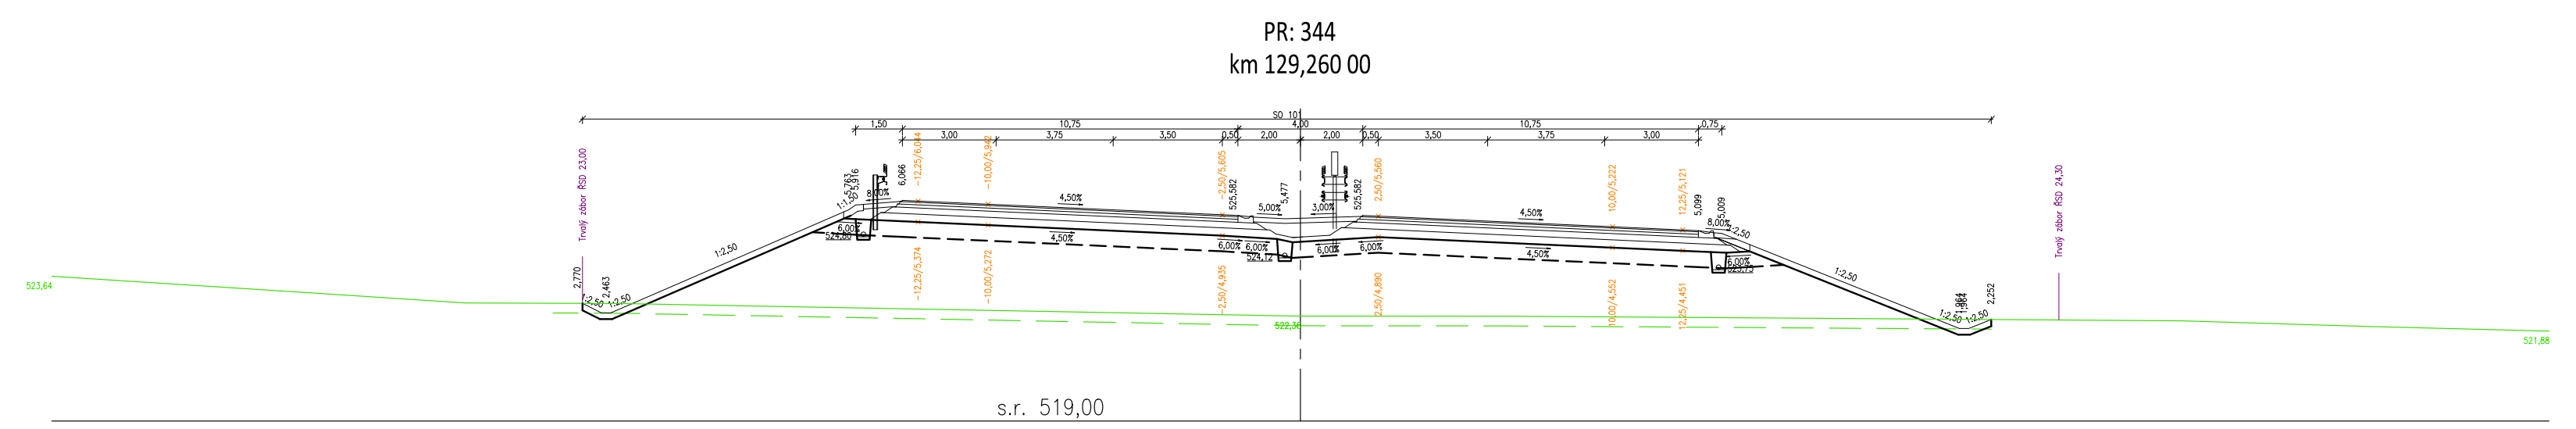
PR: 344
km 129,260 00

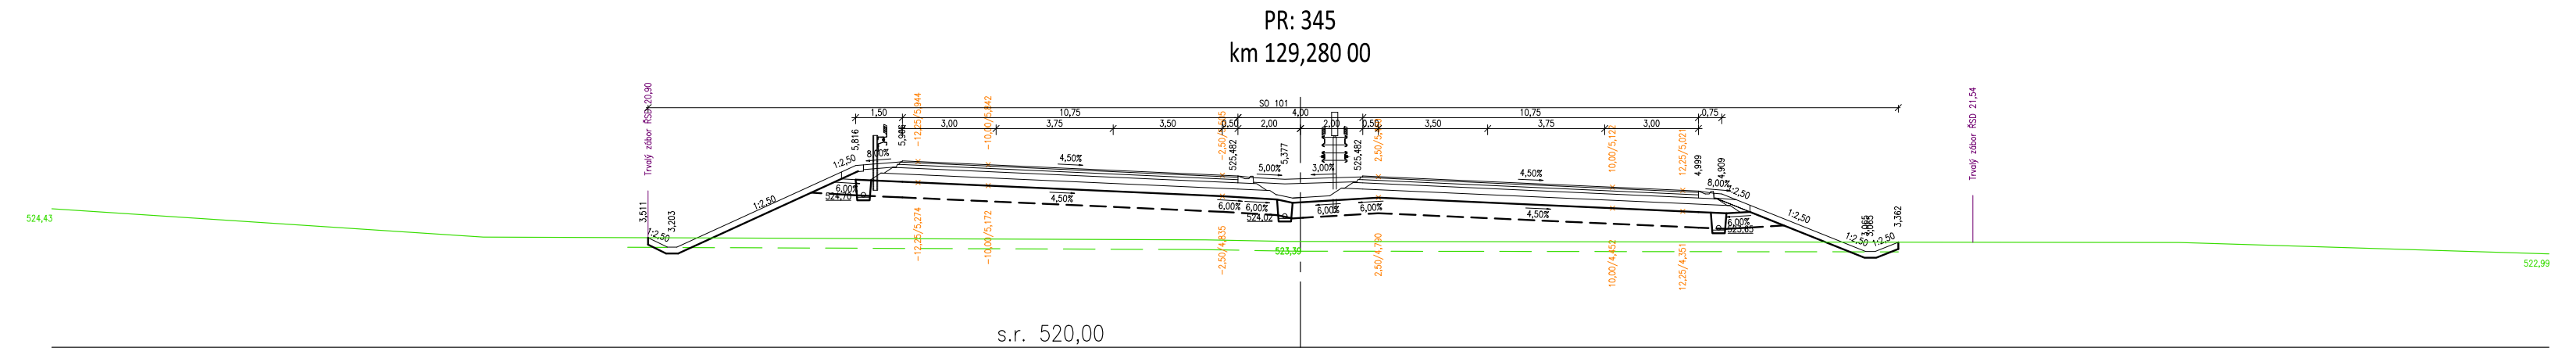
PR: 345
km 129,280 00

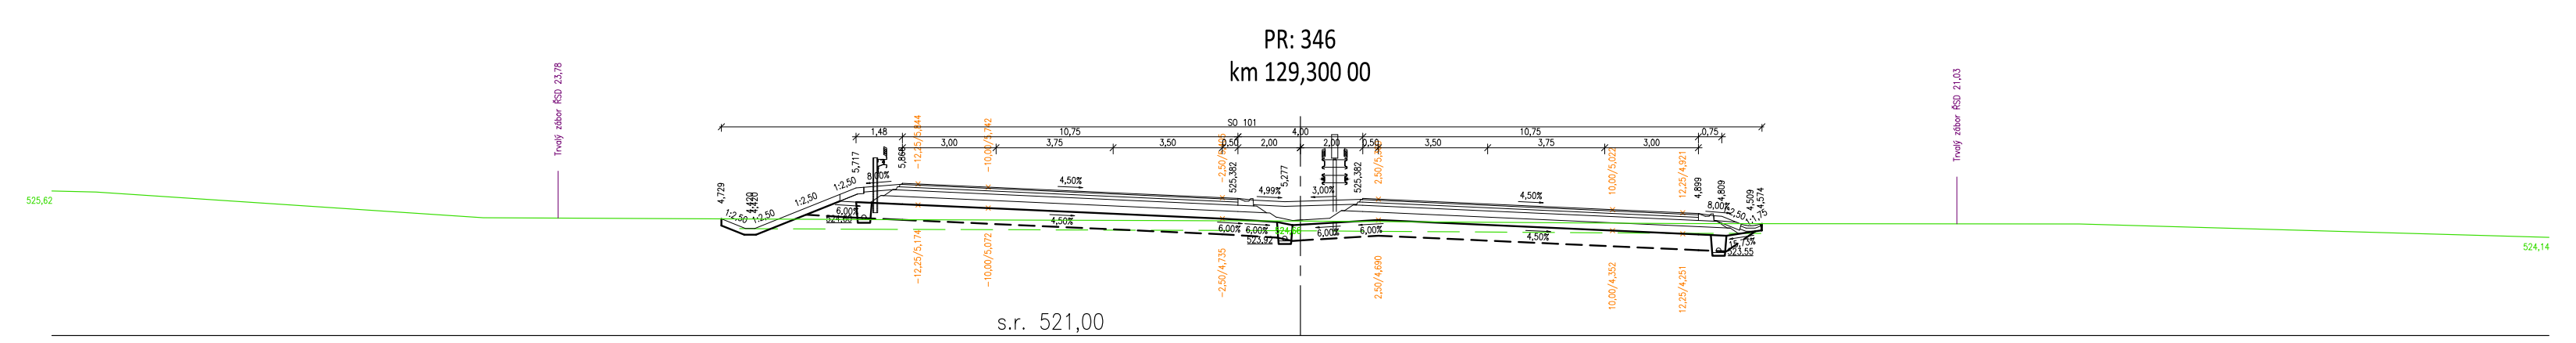
PR: 346
km 129,300 00

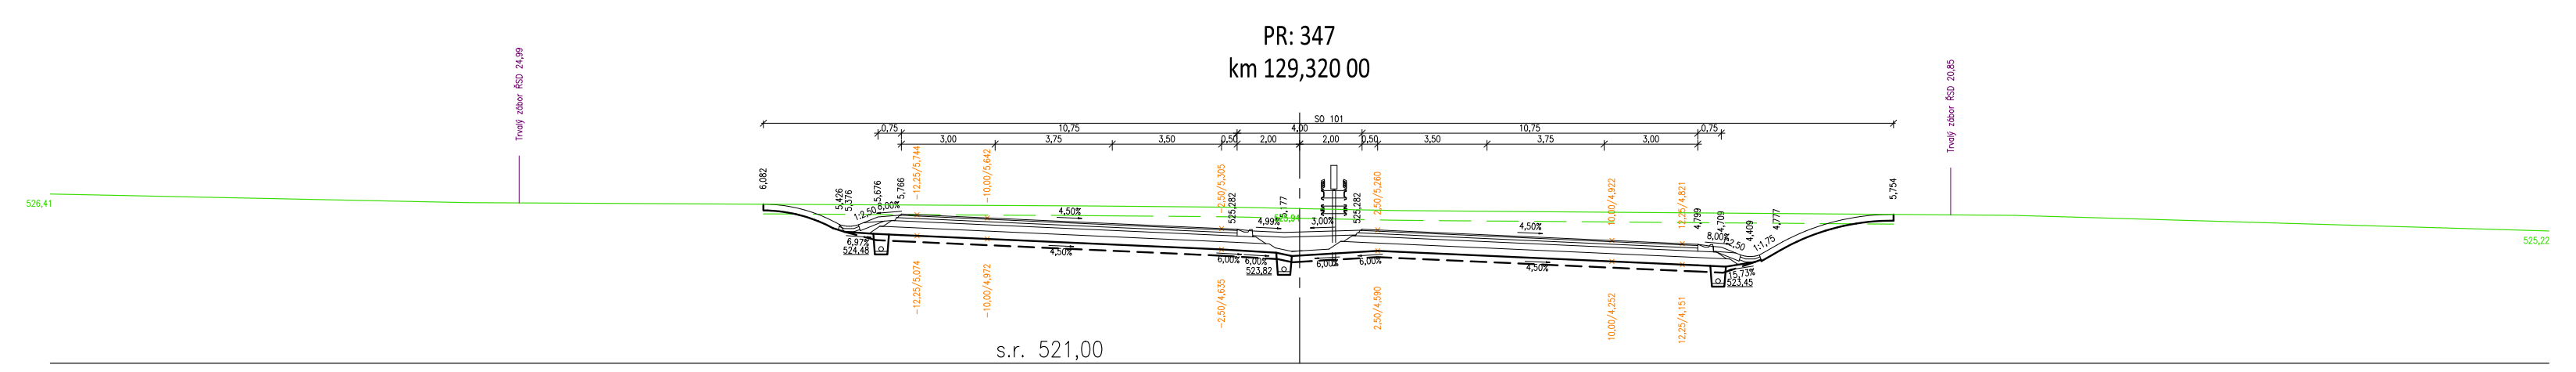
PR: 347
km 129,320 00

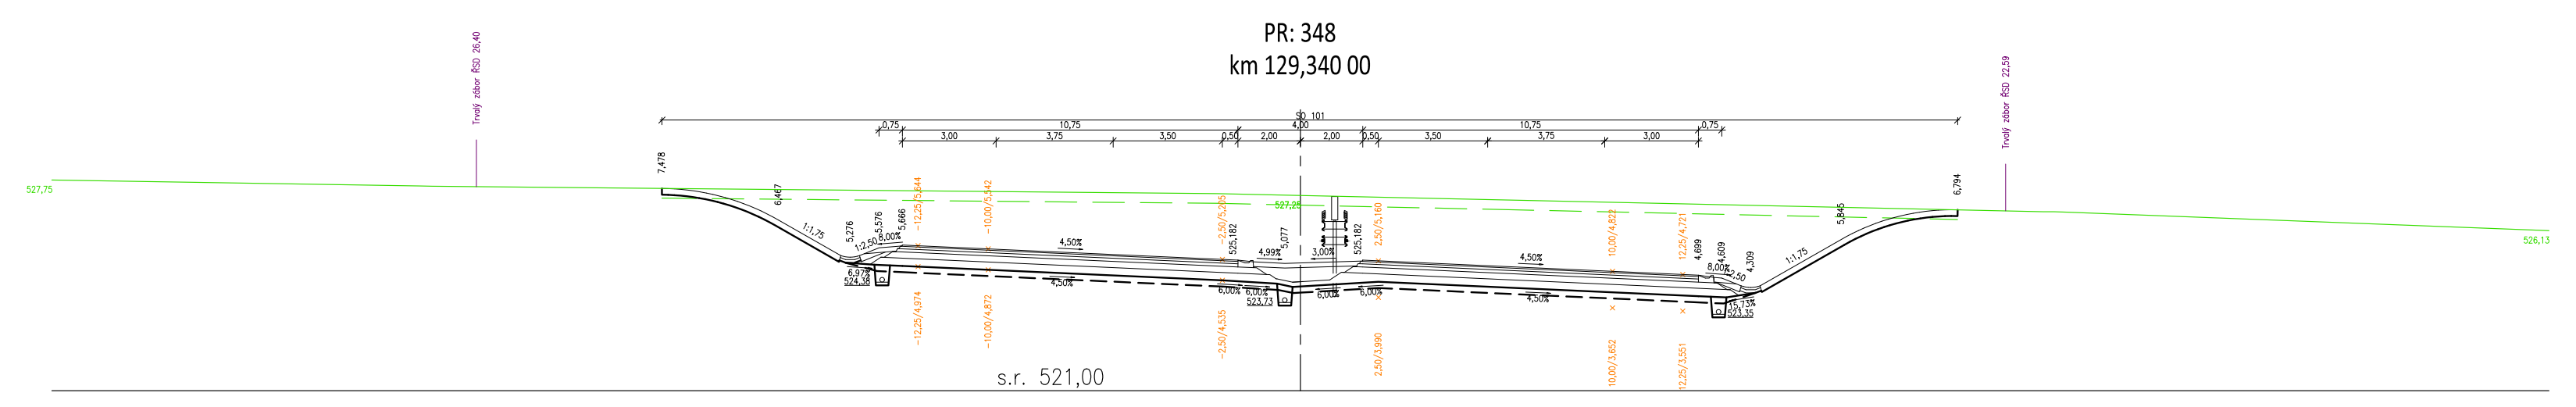
PR: 348
km 129,340 00

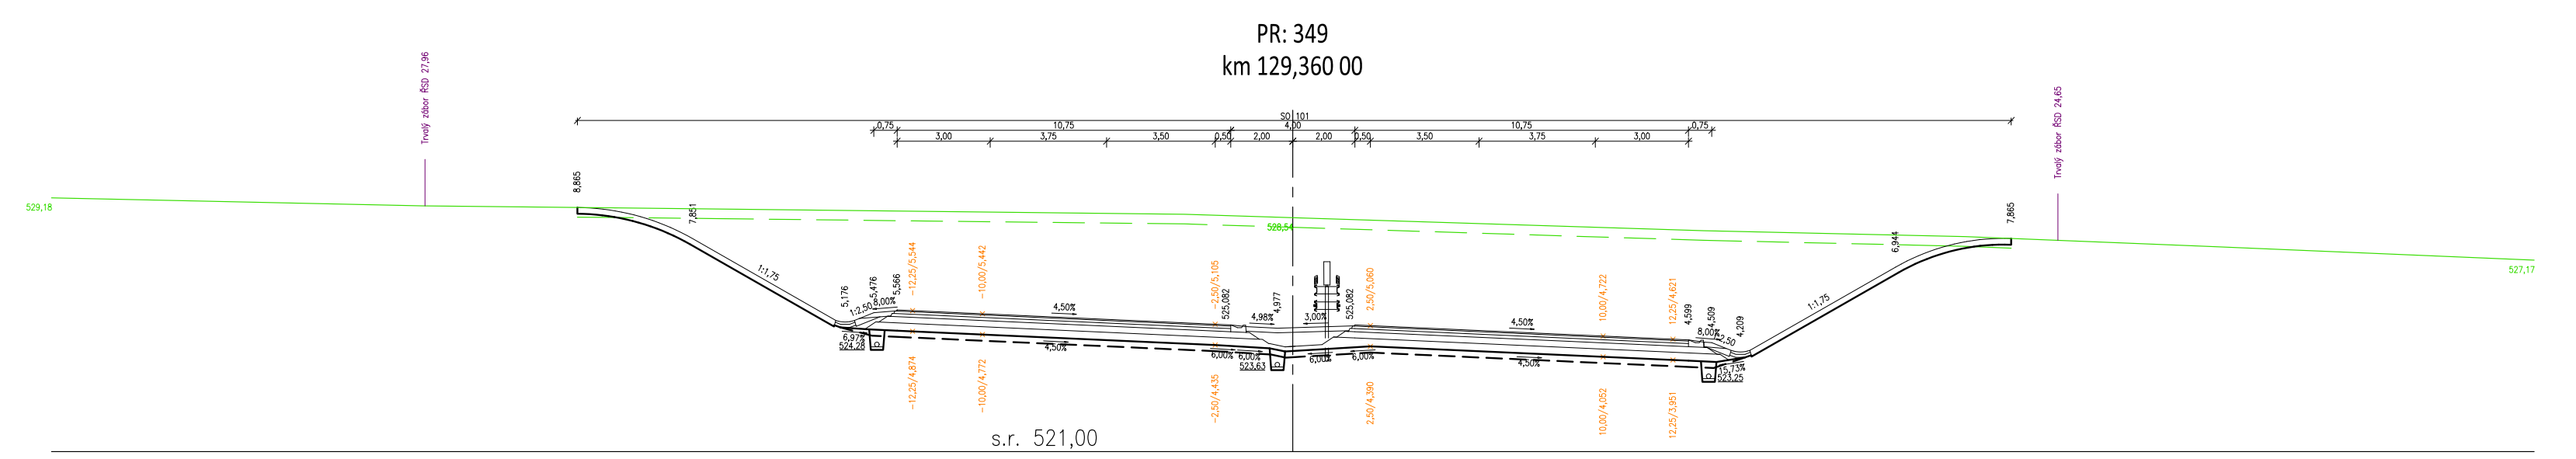
PR: 349
km 129,360 00

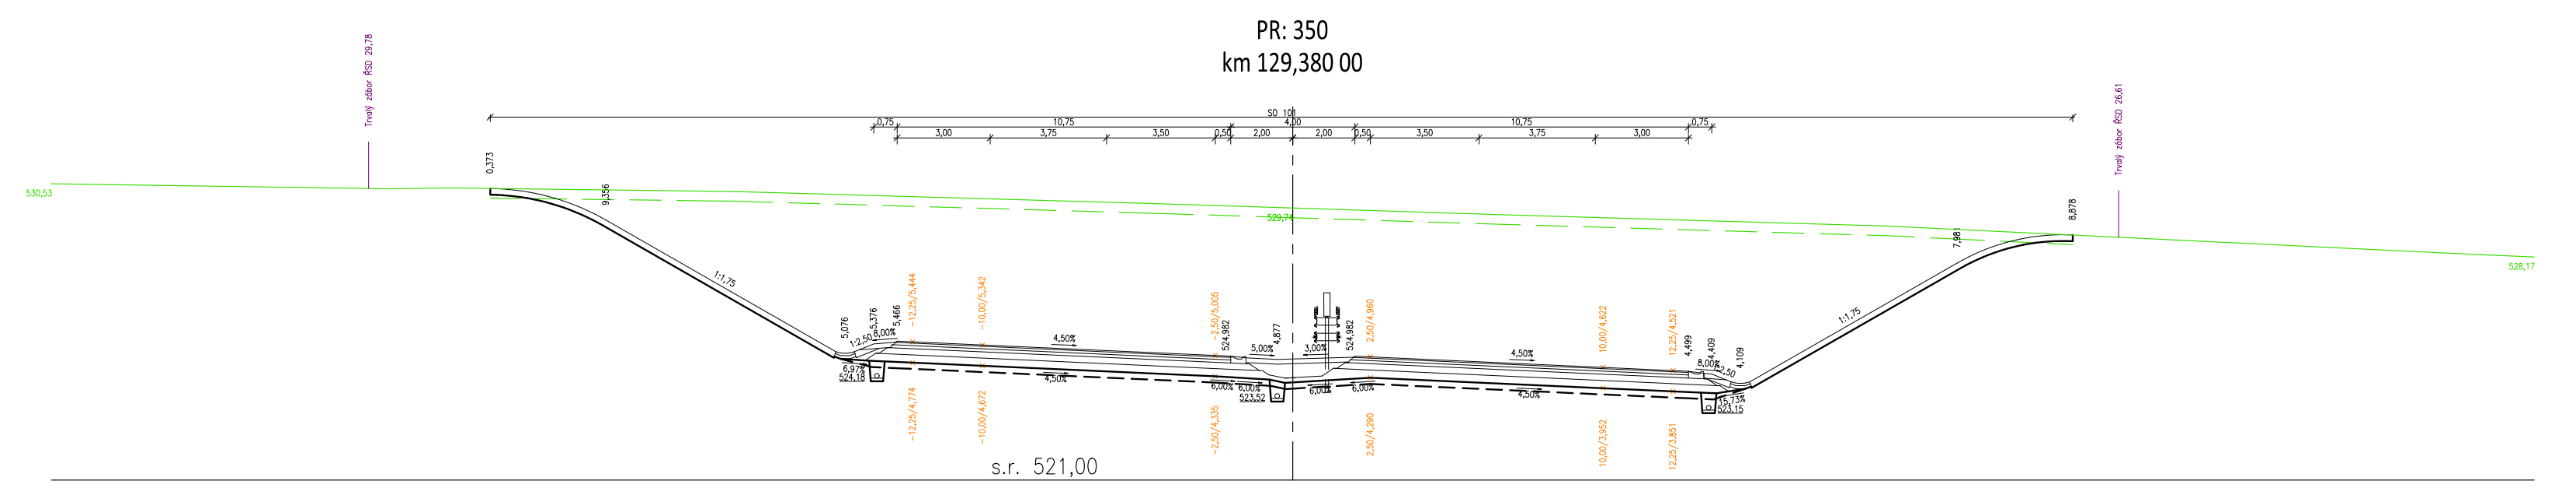
PR: 350
km 129,380 00

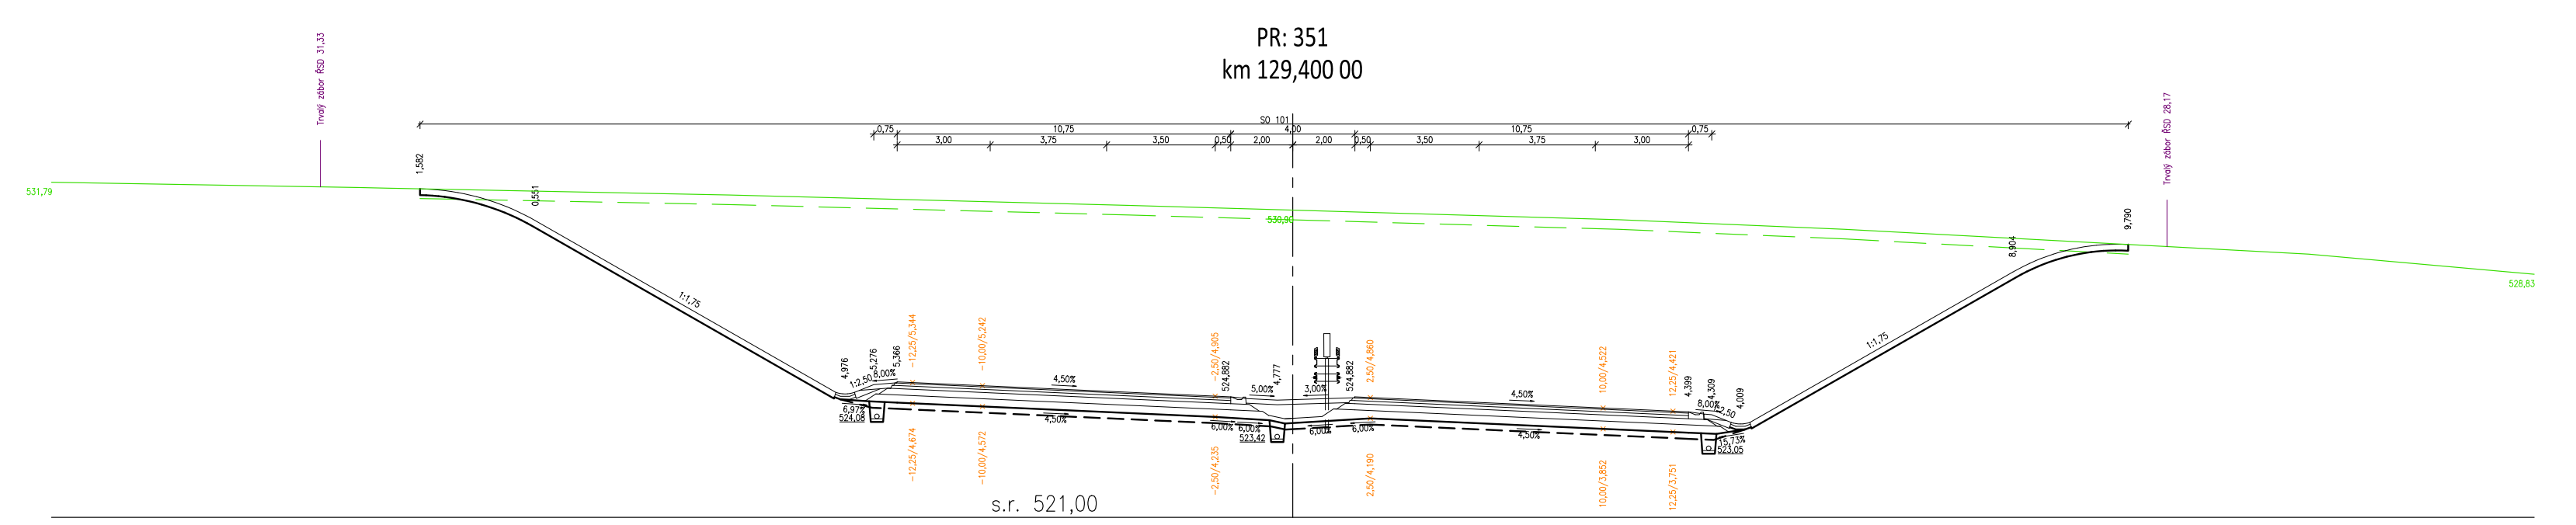
PR: 351
km 129,400 00

SO 101
D.1.1

VÝŠKOVÝ SYSTÉM Bpv

SOUŘADNICOVÝ SYSTÉM S-JTSK

Číslo změny:	Obsah změny:	Datum změny:
01	-	-
02	-	-
03	-	-

Objednatel:
Ředitelství silnic a dálnic s. p.
Na Pankráci 546/56, 140 00 Praha 4

Stavbu zajišťuje Závod Praha
Na Pankráci 546/56, 140 00 Praha 4

Zhotovitel: Společníci ve sdružení
SG_Velké projekty_BIM 2020
zastoupené
SUDOP PRAHA a.s.
Hlavní inženýr projektu: Ing. Roman Petřík
Olšanská 1a, 130 80 Praha 3
telefon: +420 267 094 111

DOPRAVOPROJEKT BRNO

DOPRAVOPROJEKT

Správce:
SUDOP PRAHA a.s.
Olšanská 1a, 130 80 Praha 3
tel.: +420 267 094 111
e-mail: praha@sudop.cz

Vedoucí týmu: ING. ROMAN PETŘÍK

Asistent vedoucího týmu: ING. PAVEL MICHL

Specialista profese: -

Zpracovatel části:
projektová, průzkumná a konzultační společnost
PUDIS a.s., Podbabská 1014/20, 160 00 Praha 6
tel.: +420 267 004 111, www.pudis.cz, info@pudis.cz

Vedoucí střediska:	Odpovědný projektant SO, IO, PS:	Vypracoval:	Kontroloval:
ING. ZDEŇKA BOLEHOVSKÁ	ING. MICHAL TUREK	PETR KOTLABA	ING. MICHAL TUREK

Název akce:
D11 1108 Jaroměř - Trutnov VD-ZDS + TP + AD

Číslo smlouvy: 22-014.250

Projektový stupeň: VD-ZDS

Část:
D.1.1 OBJEKTY POZEMNÍCH KOMUNIKACÍ VČETNĚ PROPUSTKŮ
SO 101 HLAVNÍ TRASA D11 1108

Datum: 11/2024

Číslo části: D.1.1

Název přílohy:
PŘÍČNÉ ŘEZY - 27.část

Měřítko: 1:200

Počet formátů: 20xA4

Číslo přílohy: **5.27**

DOKUMENT LZE UŽÍVAT POUZE VE SMYSLU PŘÍSLUŠNÉ SMLOUVY O DÍLO. ŽÁDNÁ JEHO ČÁST NEMŮŽE BÝT DLE ZÁKONA č.121/2000 Sb. KOPÍROVÁNA NEBO JINÝM ZPŮSOBEM ROZŠIŘOVÁNA BEZ SOUHLASU SUDOP PRAHA a.s.