

PODROBNÝ PODÉLNÝ PROFIL: SO 124.1
M 1:1000/100, ROZSAH: KM 0,34018 – KM 0,62680

DRUH POVRCHU ÚZEMÍ:
KATASTRÁLNÍ ÚZEMÍ:
OKRES:
KRAJ:

	OSTATNÍ PLOCHA
	STŘÍTEŽ U TRUTNOVA
	TRUTNOV
	KRALOVEHRADECKÝ

SKLONOVÉ POMĚRY:

PRAVOSTRANNÝ PŘÍKOP
LEVOSTRANNÝ PŘÍKOP - - - -

ZPEVNĚNÝ PŘÍKOP VLEVO

ZPEVNĚNÝ PŘÍKOP VPRAVO

SROVNÁVACÍ ROVINA:


ZMĚNA PŘÍČ. SKLONU:

KÓTY NIVELETY:

KÓTY TERÉNU:

STANIČENÍ:

SMĚROVÉ POMĚRY:

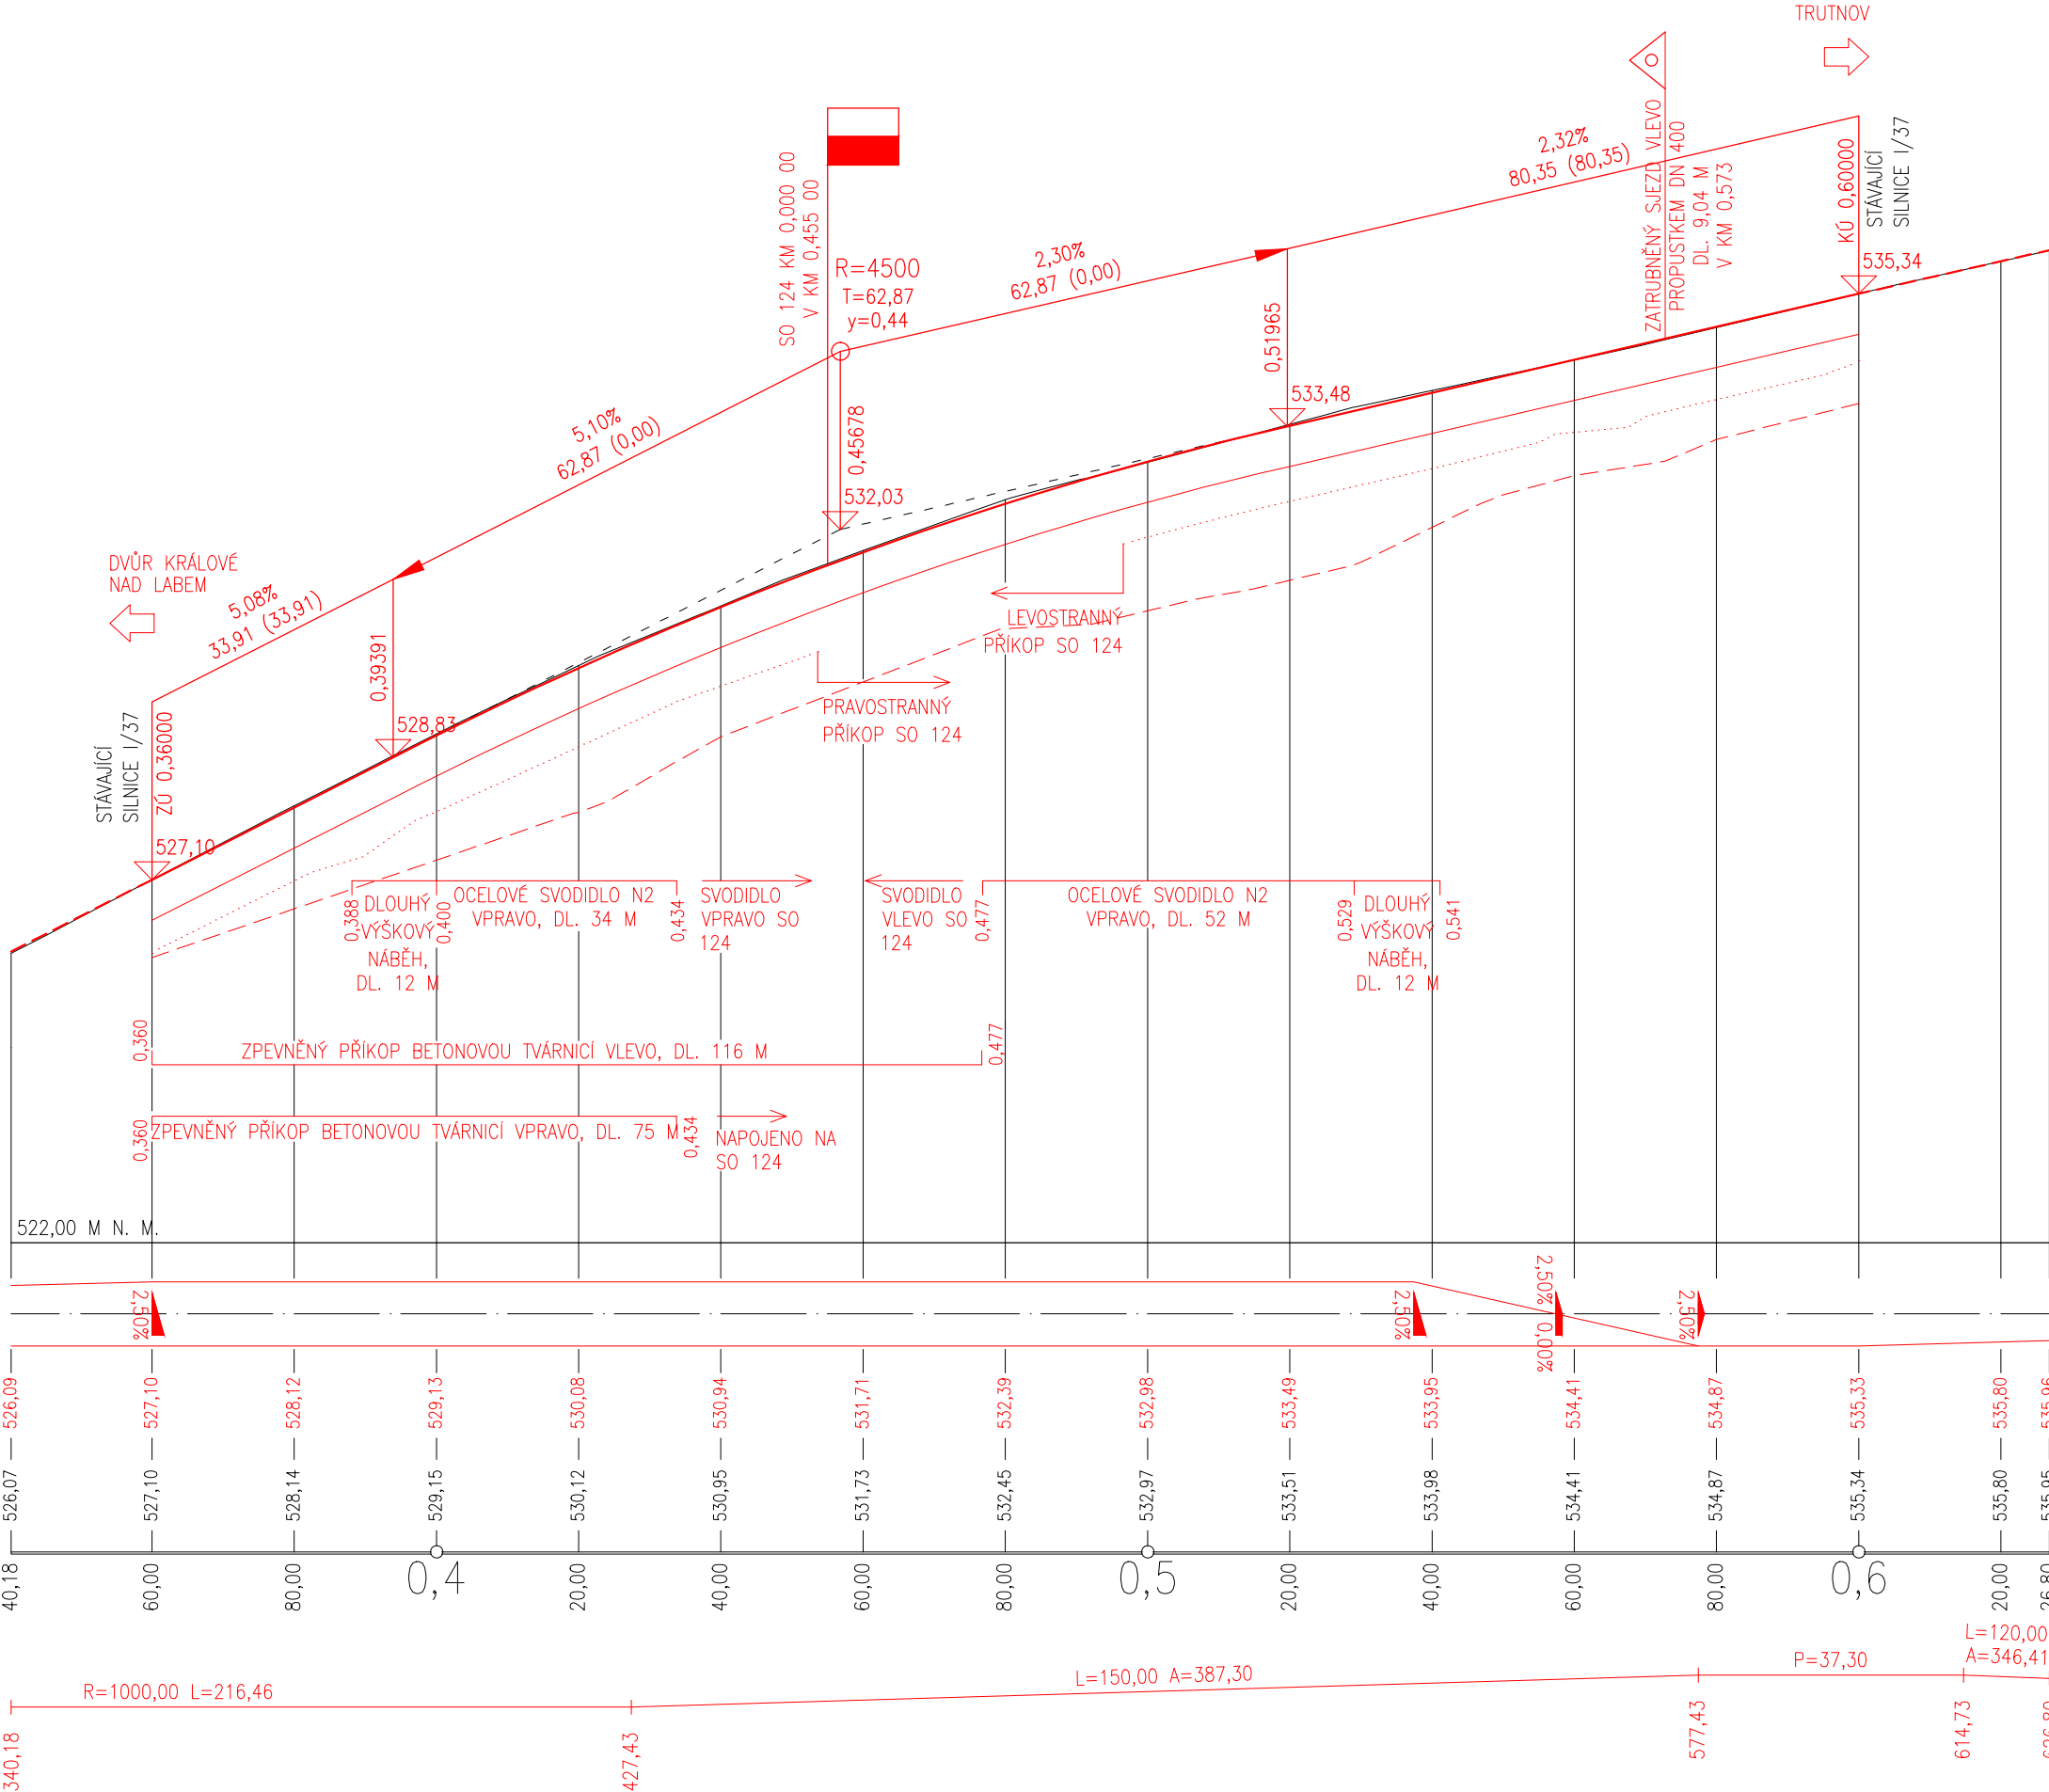

SO 124.1

D.1.1

VÝŠKOVÝ SYSTÉM Bpv

SOUŘADNICOVÝ SYSTÉM S-JTSK

Číslo změny:	Obsah změny:	Datum změny:
01	-	-
02	-	-
03	-	-

Objednatel:	Ředitelství silnic a dálnic s. p. Na Pankráci 546/56, 140 00 Praha 4
	Stavbu zajišťuje Závod Praha Na Pankráci 546/56, 140 00 Praha 4

Zhotovitel: Společníci ve sdružení	SG_Velké projekty_BIM 2020 zastoupené
SUDOP PRAHA a.s. Hlavní inženýr projektu: Ing. Roman Petřík	Olšanská 1a, 130 80 Praha 3 telefon: +420 267 094 111

Správce:	SUDOP PRAHA a.s. Olšanská 1a, 130 80 Praha 3 tel.: +420 267 094 111 e-mail: praha@sudop.cz	Vedoucí týmu:	Asistent vedoucího týmu:
		ING. ROMAN PETŘÍK	ING. PAVEL MICHL
			Specialista profese:
			-

Zpracovatel částí:



PUDIS

projektová, průzkumná a konzultační společnost

PUDIS a.s., Podbabská 1014/20, 160 00 Praha 6
tel.: +420 267 004 111, www.pudis.cz, info@pudis.cz

Vedoucí střediska:	Odpovědný projektant SO, IO, PS:	Vypracoval:	Kontroloval:
ING. ZDEŇKA BOLEHOVSKÁ	ING. MICHAL TUREK	ING. TOMÁŠ VÁŇA	ING. MICHAL TUREK

Název akce:		Číslo smlouvy:	
D11 1108 Jaroměř - Trutnov VD-ZDS + TP + AD		22-014.250	
		Projektový stupeň:	
		VD-ZDS	
Část:		Datum:	
D.1.1 OBJEKTY POZEMNÍCH KOMUNIKACÍ VČETNĚ PROPUSTKŮ SO 124.1 PŘELOŽKA SILNICE III/30015 (KM 132,22), PŘÍDATNÉ PRUHY NA SIL. I/37		11/2024	
Název přílohy:		Číslo částí:	
		D.1.1	
		Měřítko:	Počet formátů:
PODÉLNÝ PROFIL		1:1000/100	3xA4
		Číslo přílohy:	
		3	