

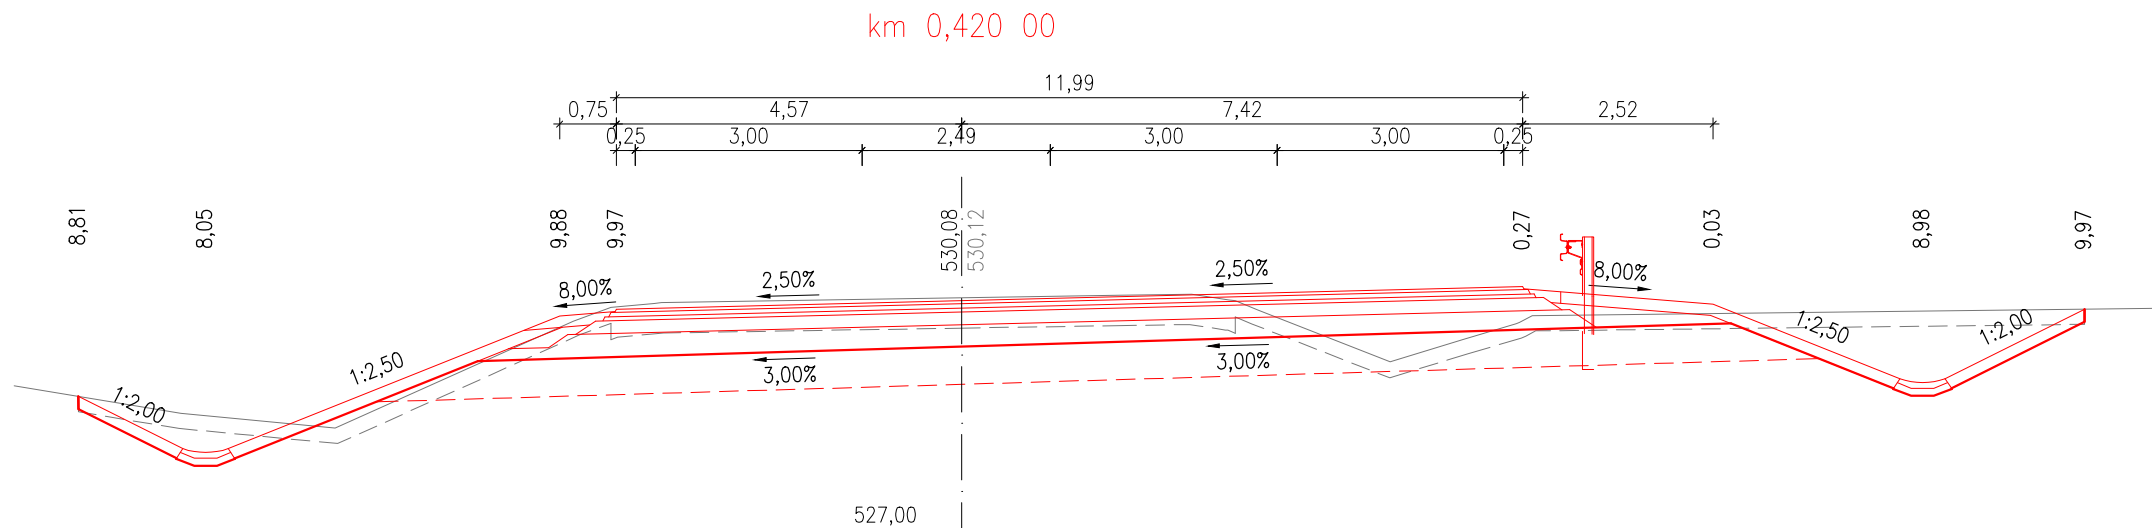
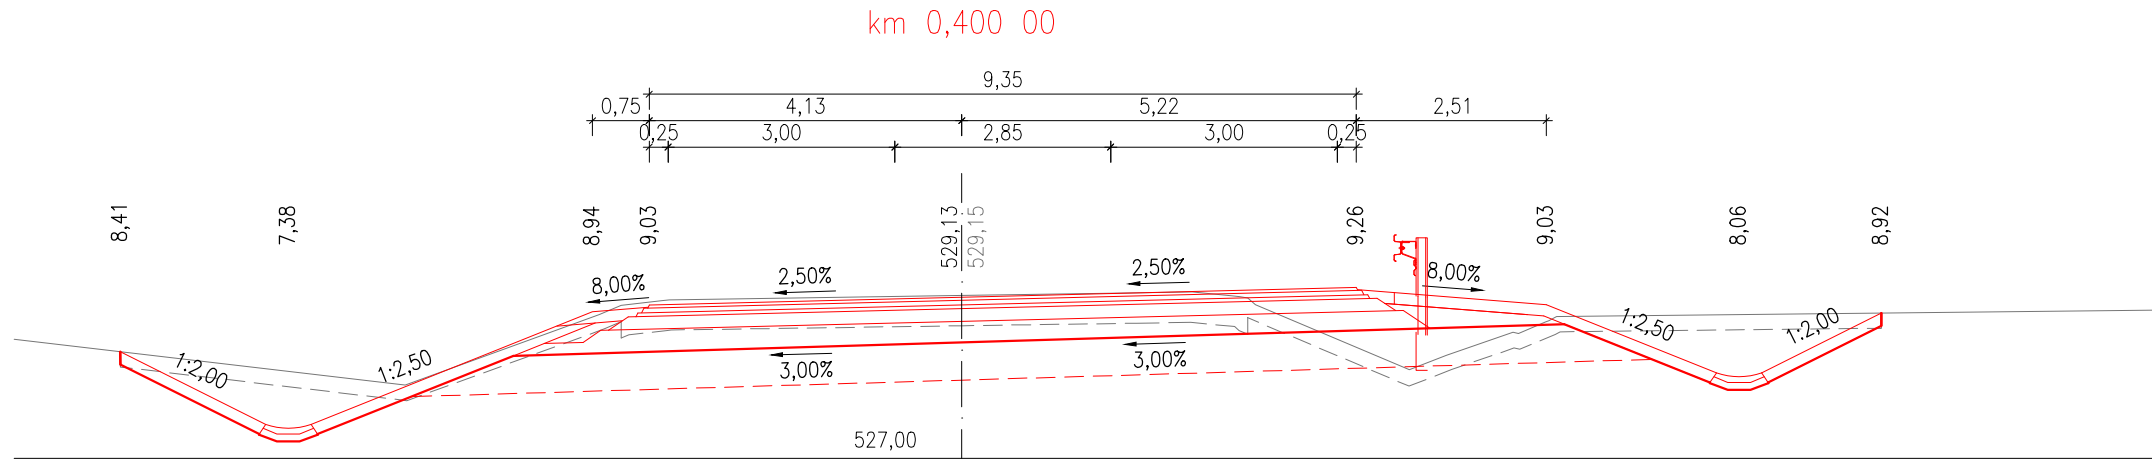
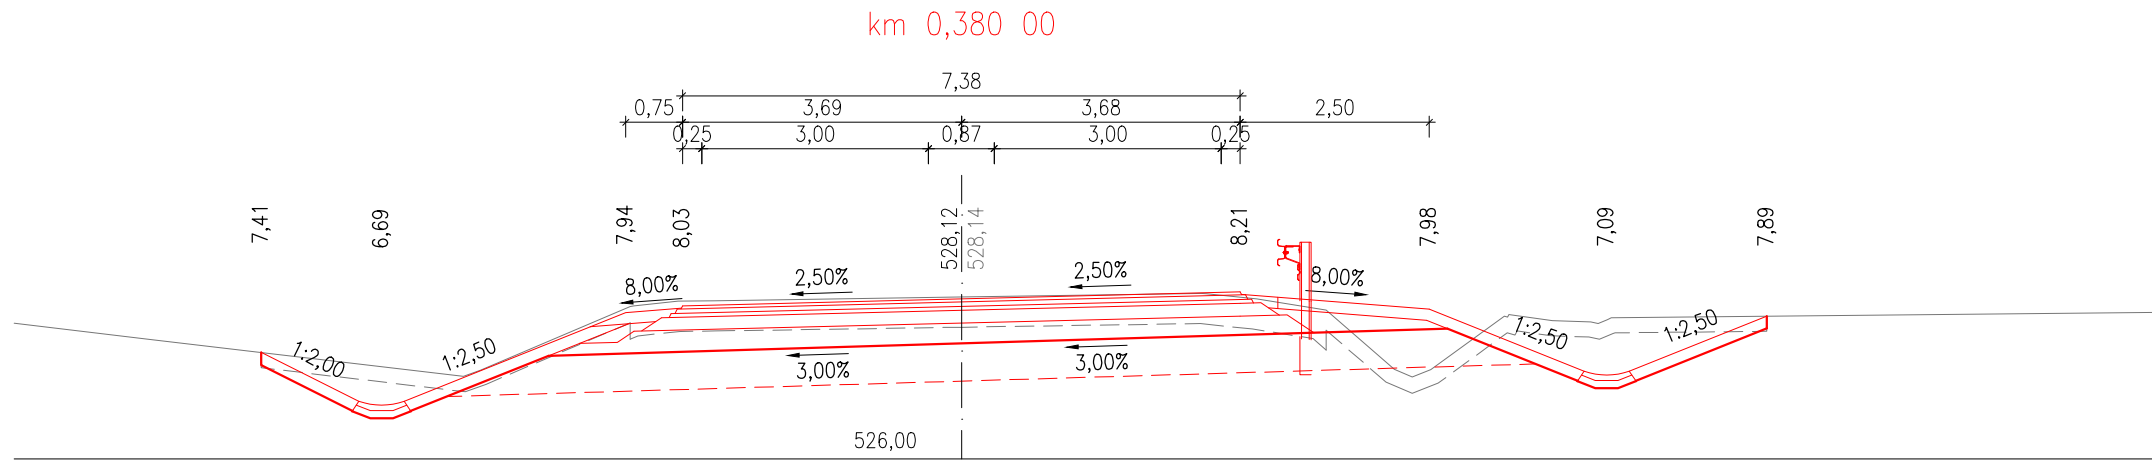
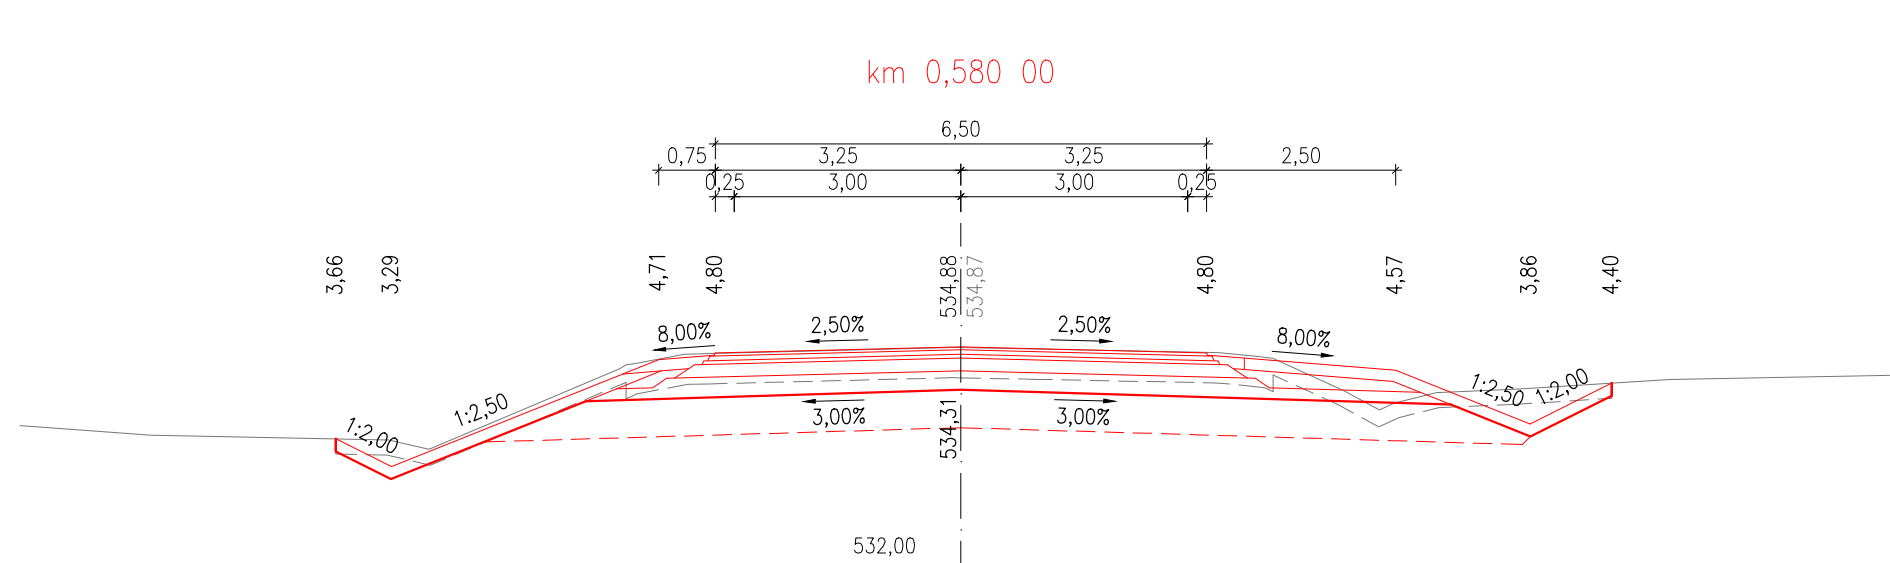
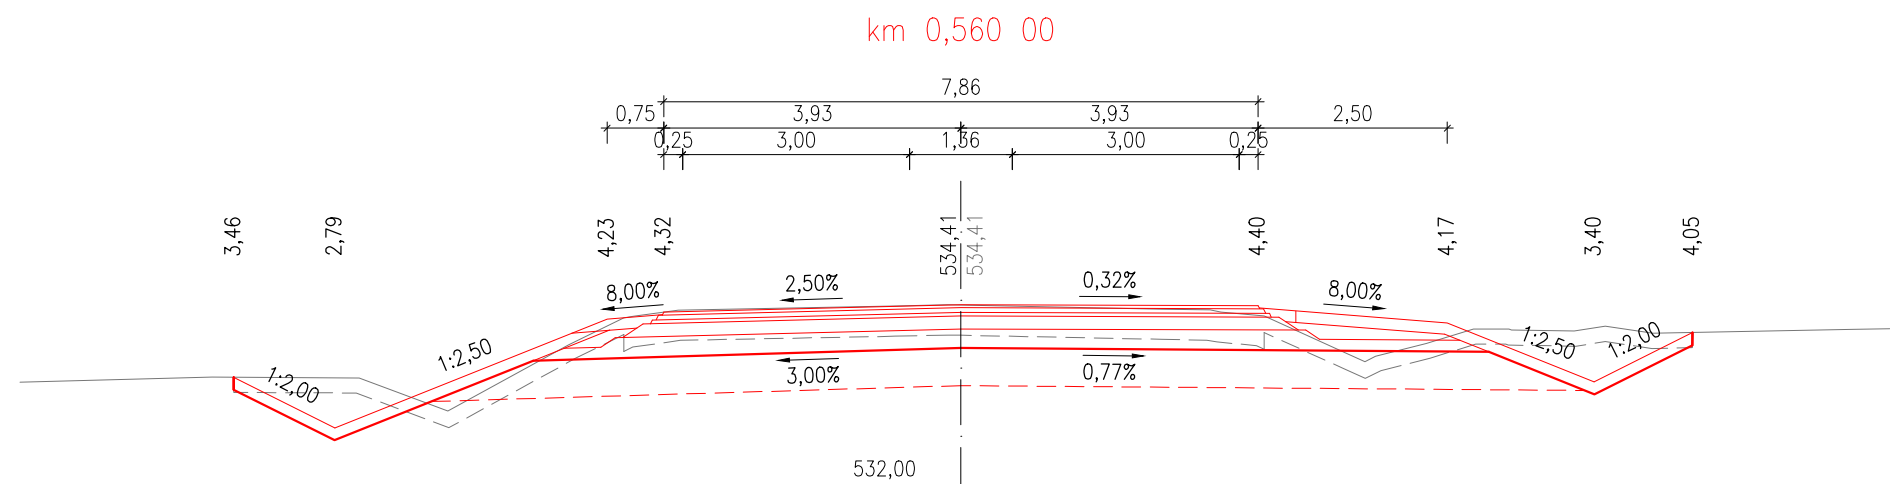
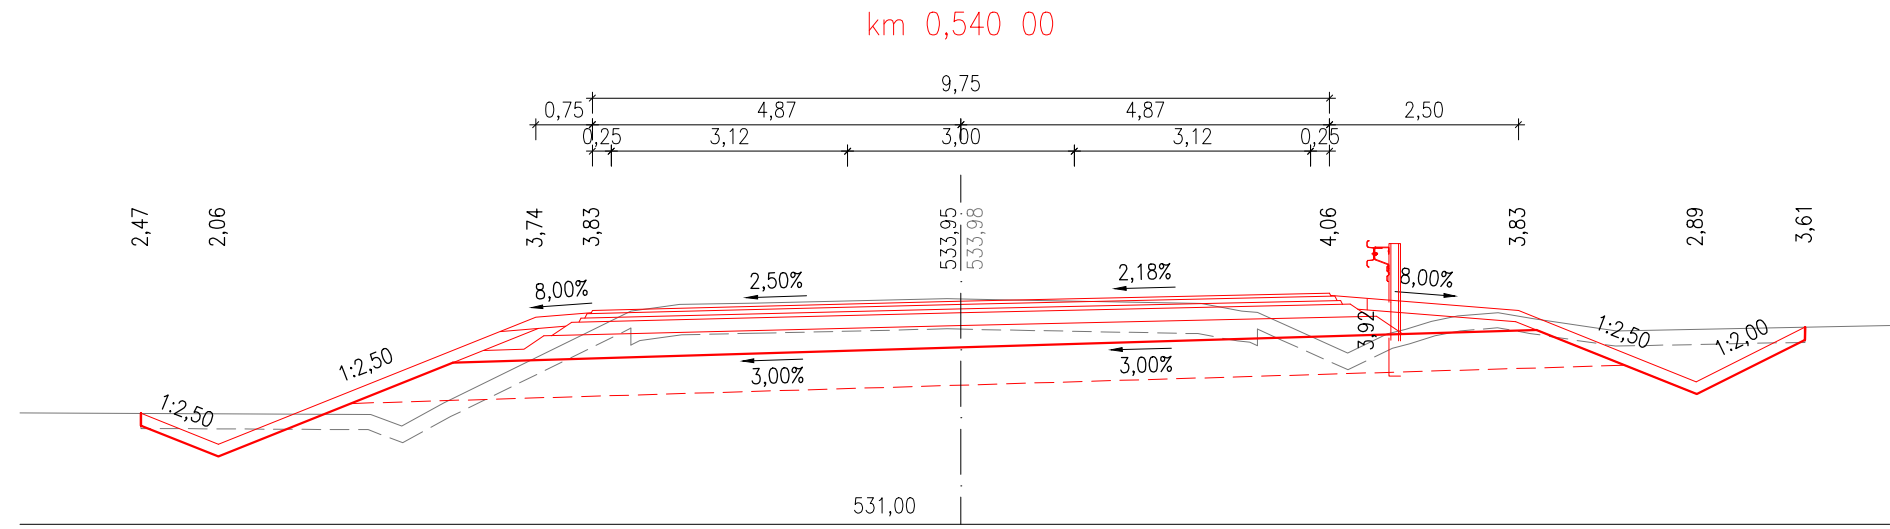
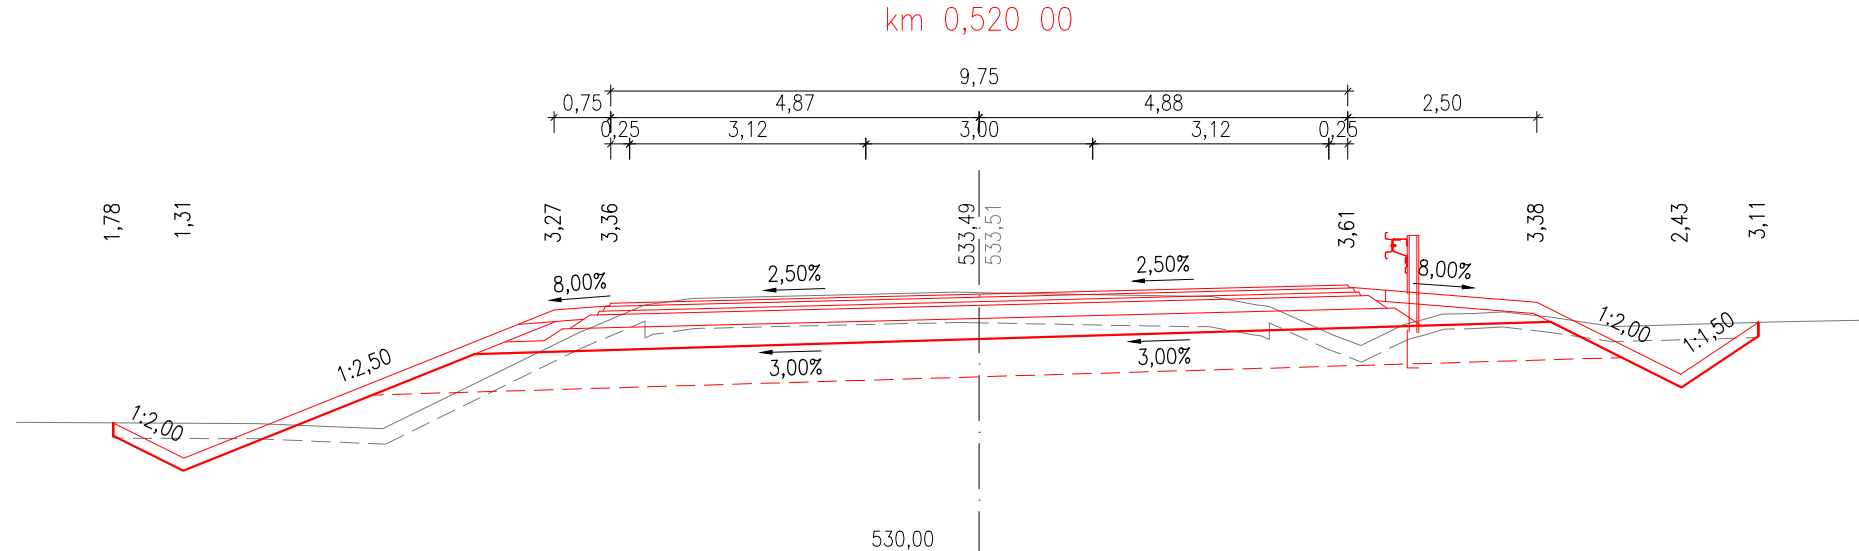


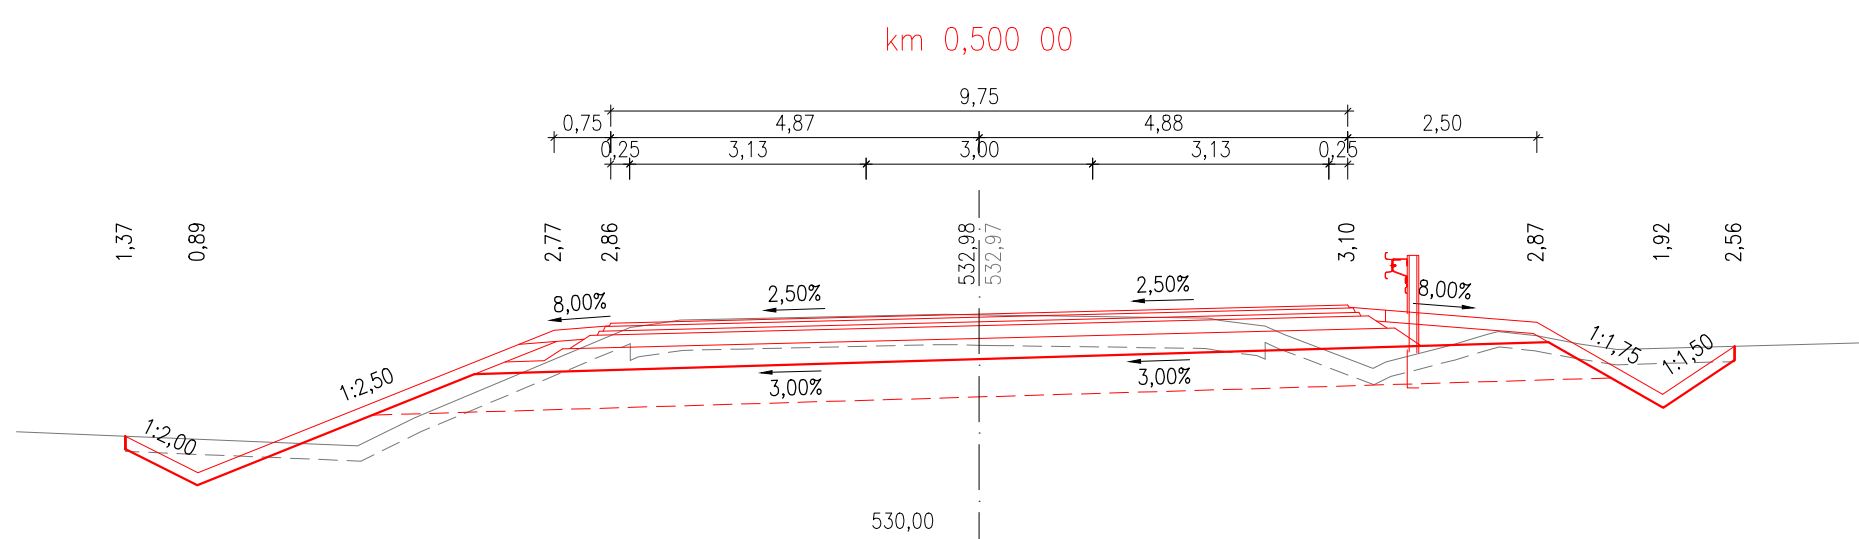

km 0,440 00
ŘEZ KŘIŽOVATKOU

km 0,460 00
ŘEZ KŘIŽOVATKOU

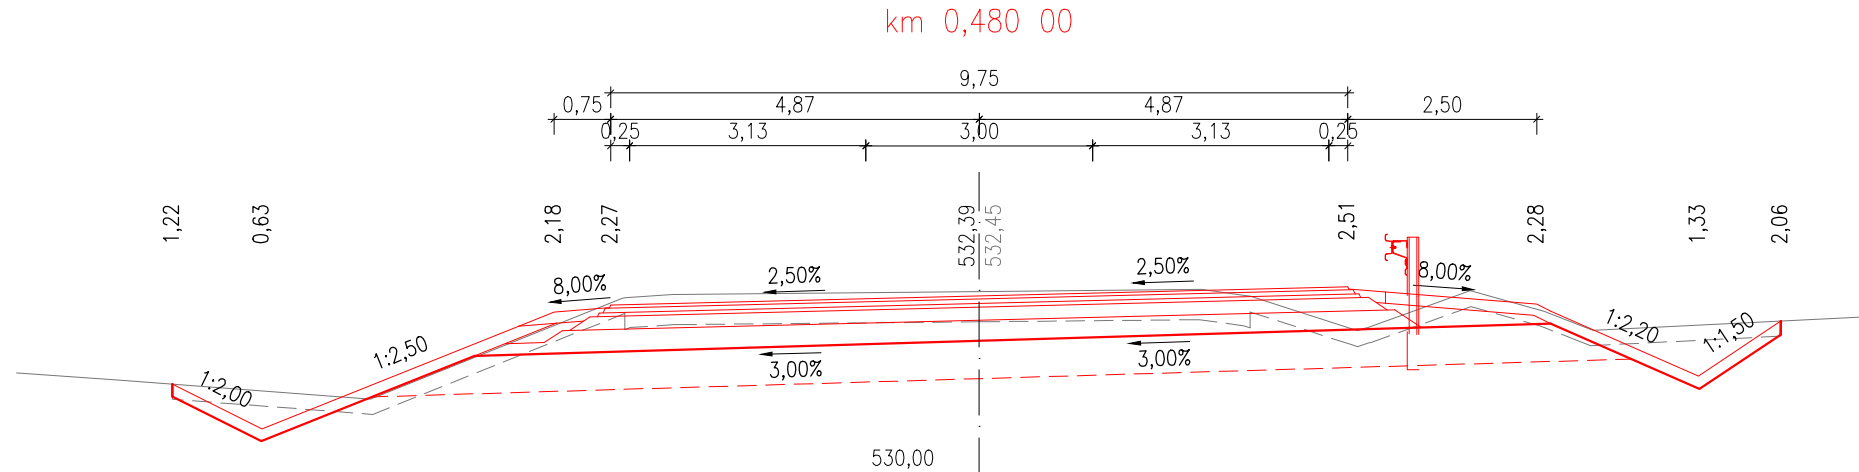

SO 124.1 D.1.1

VÝŠKOVÝ SYSTÉM Bpv SOUŘADNICOVÝ SYSTÉM S-JTSK

Číslo změny:	Obsah změny:	Datum změny:
01	-	-
02	-	-
03	-	-

Objednatel:	Ředitelství silnic a dálnic s. p. Na Pankráci 546/56, 140 00 Praha 4
	Stavbu zajišťuje Závod Praha Na Pankráci 546/56, 140 00 Praha 4

Zhotovitel: Společníci ve sdružení	SG_Velké projekty_BIM 2020 zastoupené
SUDOP PRAHA a.s. Hlavní inženýr projektu: Ing. Roman Petřík	Olišanská 1a, 130 80 Praha 3 telefon: +420 267 094 111

--	--	--	--	--

Správce:	SUDOP PRAHA a.s. Olišanská 1a, 130 80 Praha 3 tel.: +420 267 094 111 e-mail: praha@sudop.cz	Vedoucí týmu:	ING. ROMAN PETŘÍK	Asistent vedoucího týmu:	ING. PAVEL MICHL	Specialista profese:	-
----------	--	---------------	-------------------	--------------------------	------------------	----------------------	---

Zpracovatel část:	projektová, průzkumná a konzultační společnost PUDIS a.s., Podbabská 1014/20, 160 00 Praha 6 tel.: +420 267 004 111, www.pudis.cz, info@pudis.cz
-------------------	--

Vedoucí střediska:	Odpovědný projektant SO, IO, PS:	Vypracoval:	Kontroloval:
ING. ZDENKA BOLEHOVSKÁ	ING. MICHAL TUREK	ING. TOMÁŠ VÁŇA	ING. MICHAL TUREK

Název akce:	Číslo smlouvy:
D11 1108 Jaroměř - Trutnov VD-ZDS + TP + AD	22-014.250
Část:	Projektový stupeň:
D.1.1 OBJEKTY POZEMNÍCH KOMUNIKACÍ VČETNĚ PROPUSTKŮ SO 124.1 PŘELOŽKA SILNICE III/30015 (KM 132,22), PŘÍDATNÉ PRUHY NA SIL. I/37	VD-ZDS
Název přílohy:	Datum:
PŘÍČNÉ ŘEZY	11/2024
	Číslo část:
	D.1.1
	Měřítko:
	1:100
	Počet formátů:
	5xA4
	Číslo přílohy:
	5