

km 0,573
DN 400
PŮDORYS PROPUSTKU
(M 1:50)



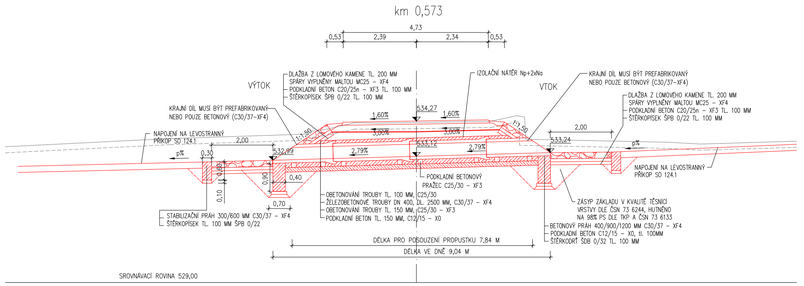

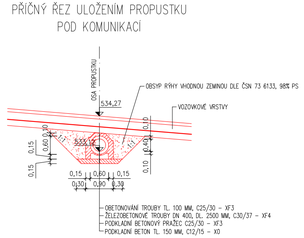

SO 124.1
D.1.1

VÝŠKOVÝ SYSTÉM Bpv — SOUŘADNICOVÝ SYSTÉM S-JTSK

Číslo změny:	Obsah změny:	Datum změny:
01	-	-
02	-	-
03	-	-

Objednatel:
ŘEDITELSTVÍ SILNIC A DÁLNIC
Ředitelství silnic a dálnic s. p.
Na Pankráci 546/56, 140 00 Praha 4
Stavbu zajišťuje Závod Praha
Na Pankráci 546/56, 140 00 Praha 4

Zhotovitel: Společníci ve sdružení
SG_Velké projekty_BIM 2020
zastoupené
SUDOP PRAHA a.s.
Hlavní inženýr projektu: Ing. Roman Petřík
Olšanská 1a, 130 80 Praha 3
telefon: +420 267 094 111

Správce:
SUDOP PRAHA a.s.
Olšanská 1a, 130 80 Praha 3
tel.: +420 267 094 111
e-mail: praha@sudop.cz

Vedoucí týmu:
ING. ROMAN PETŘÍK

Asistent vedoucího týmu:
ING. PAVEL MICHL

Specialista profese:
-

Zpracovatel části:
PUDIS
projektová, průzkumná a konzultační společnost
PUDIS a.s., Podbabská 1014/20, 160 00 Praha 6
tel.: +420 267 004 111, www.pudis.cz, info@pudis.cz

Vedoucí střediska:	Odpovědný projektant SO, IO, PS:	Vypracoval:	Kontroloval:
ING. ZDEŇKA BOLEHOVSKÁ	ING. MICHAL TUREK	ING. TOMÁŠ VÁŇA	ING. MICHAL TUREK

Název akce:
D11 1108 Jaroměř - Trutnov VD-ZDS + TP + AD

Číslo smlouvy: 22-014.250
Projektový stupeň: VD-ZDS

Část:
D.1.1 OBJEKTY POZEMNÍCH KOMUNIKACÍ VČETNĚ PROPUSTKŮ
SO 124.1 PŘELOŽKA SILNICE III/30015 (KM 132,22), PŘÍDATNÉ PRUHY NA SIL. I/37

Datum: 11/2024
Číslo části: D.1.1

Název přílohy:
PROPUSTEK DN 400 V KM 0,573

Měřítko: 1:100
Počet formátů: 4xA4
Číslo přílohy: **6**

DOKUMENT LZE UŽÍVAT POUZE VE SMYSLU PŘÍSLUŠNÉ SMLOUVY O DÍLO. ZÁDNÁ JEHO ČÁST NEMŮŽE BÝT DLE ZÁKONA č.121/2000 Sb. KOPÍROVÁNA NEBO JINÝM ZPŮSOBEM ROZŠIŘOVÁNA BEZ SOUHLASU SUDOP PRAHA a.s.