
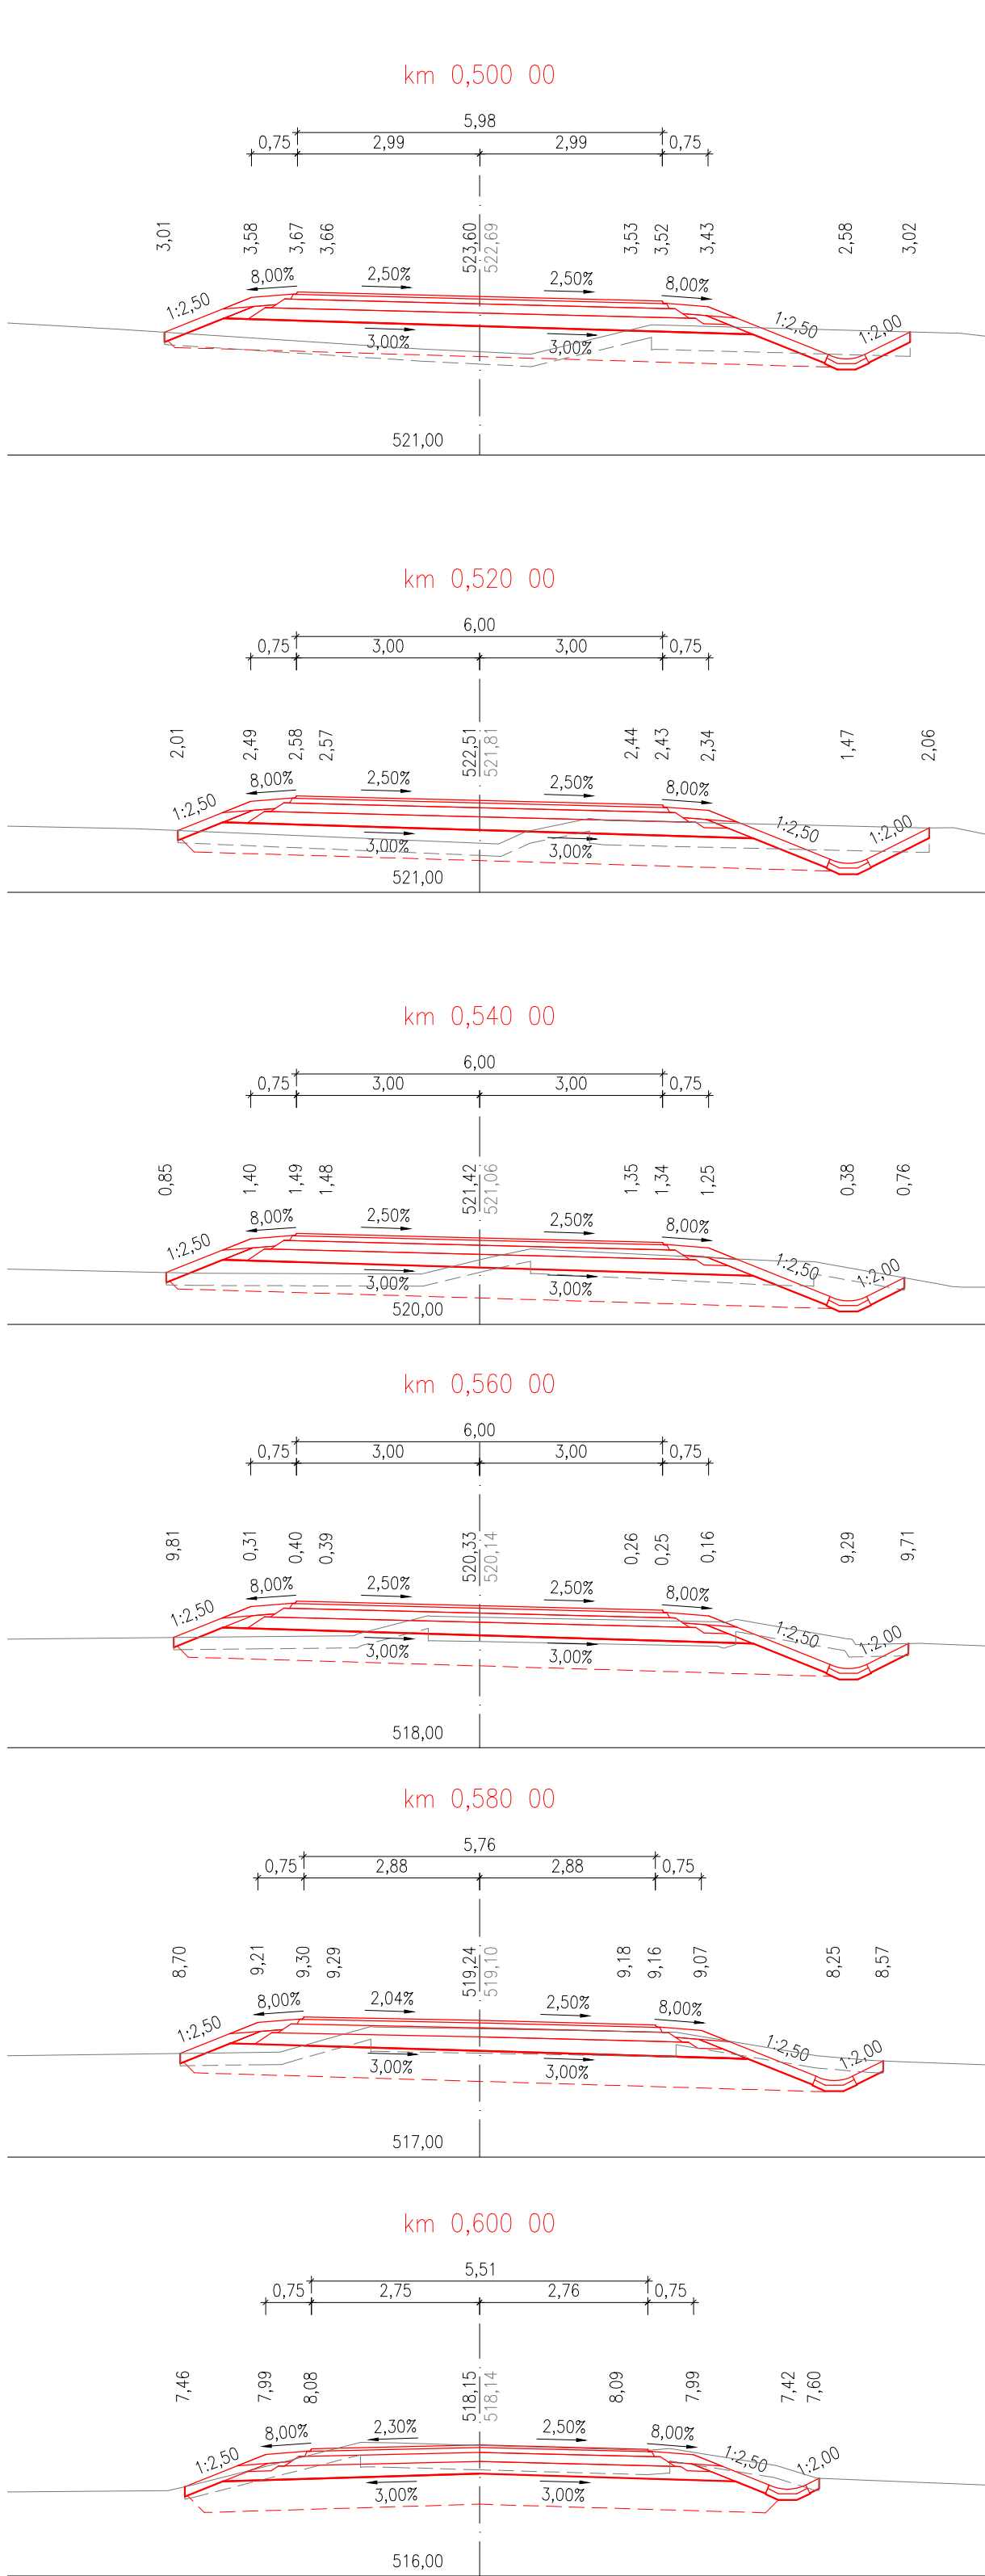
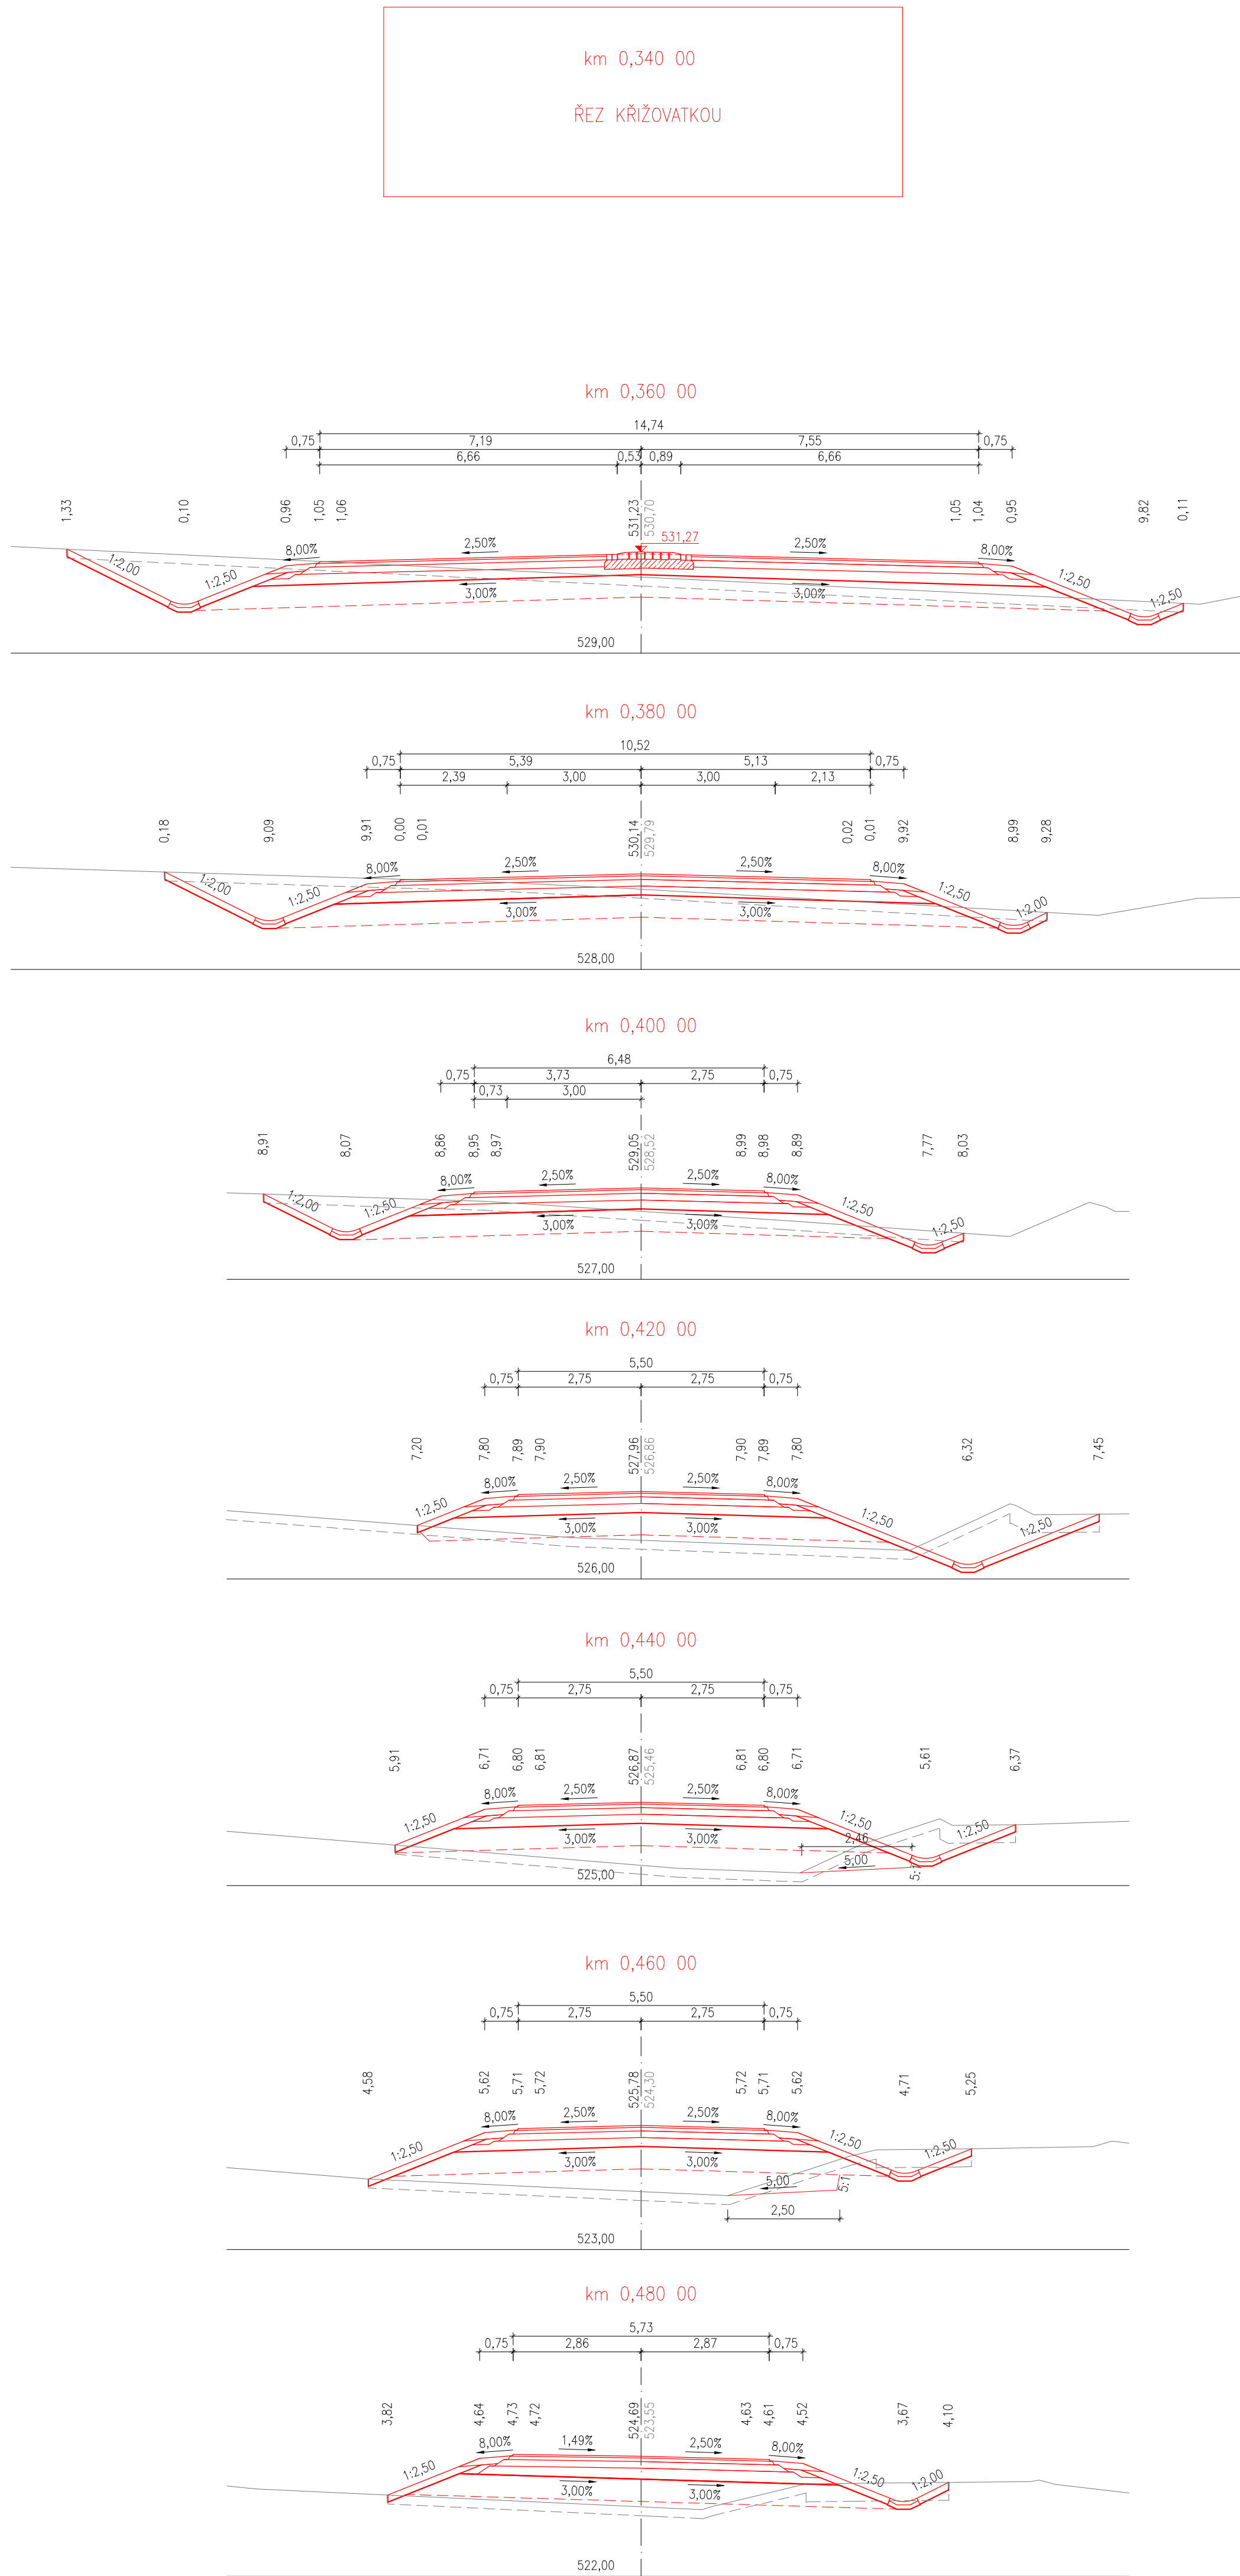
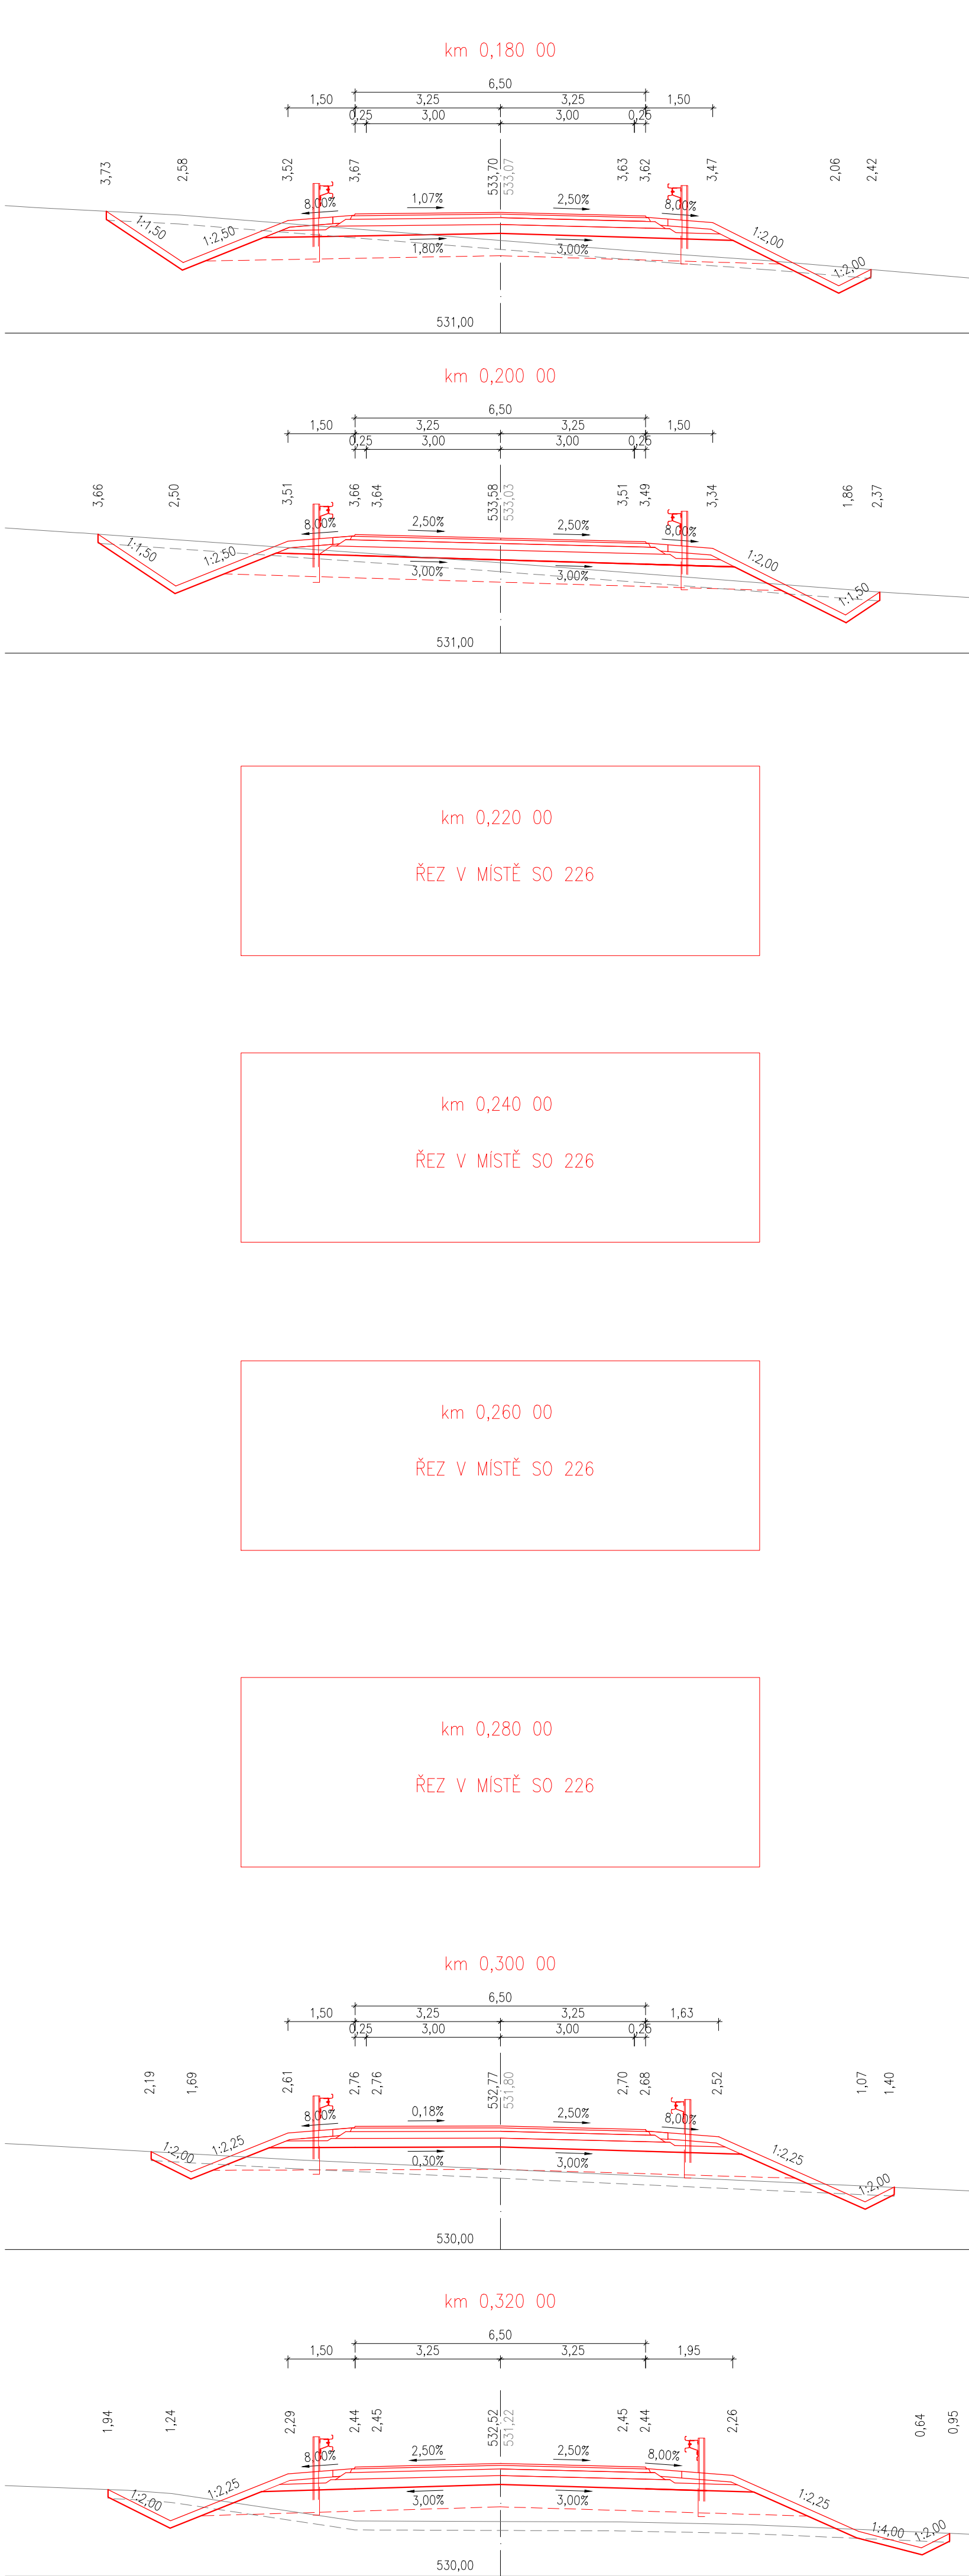


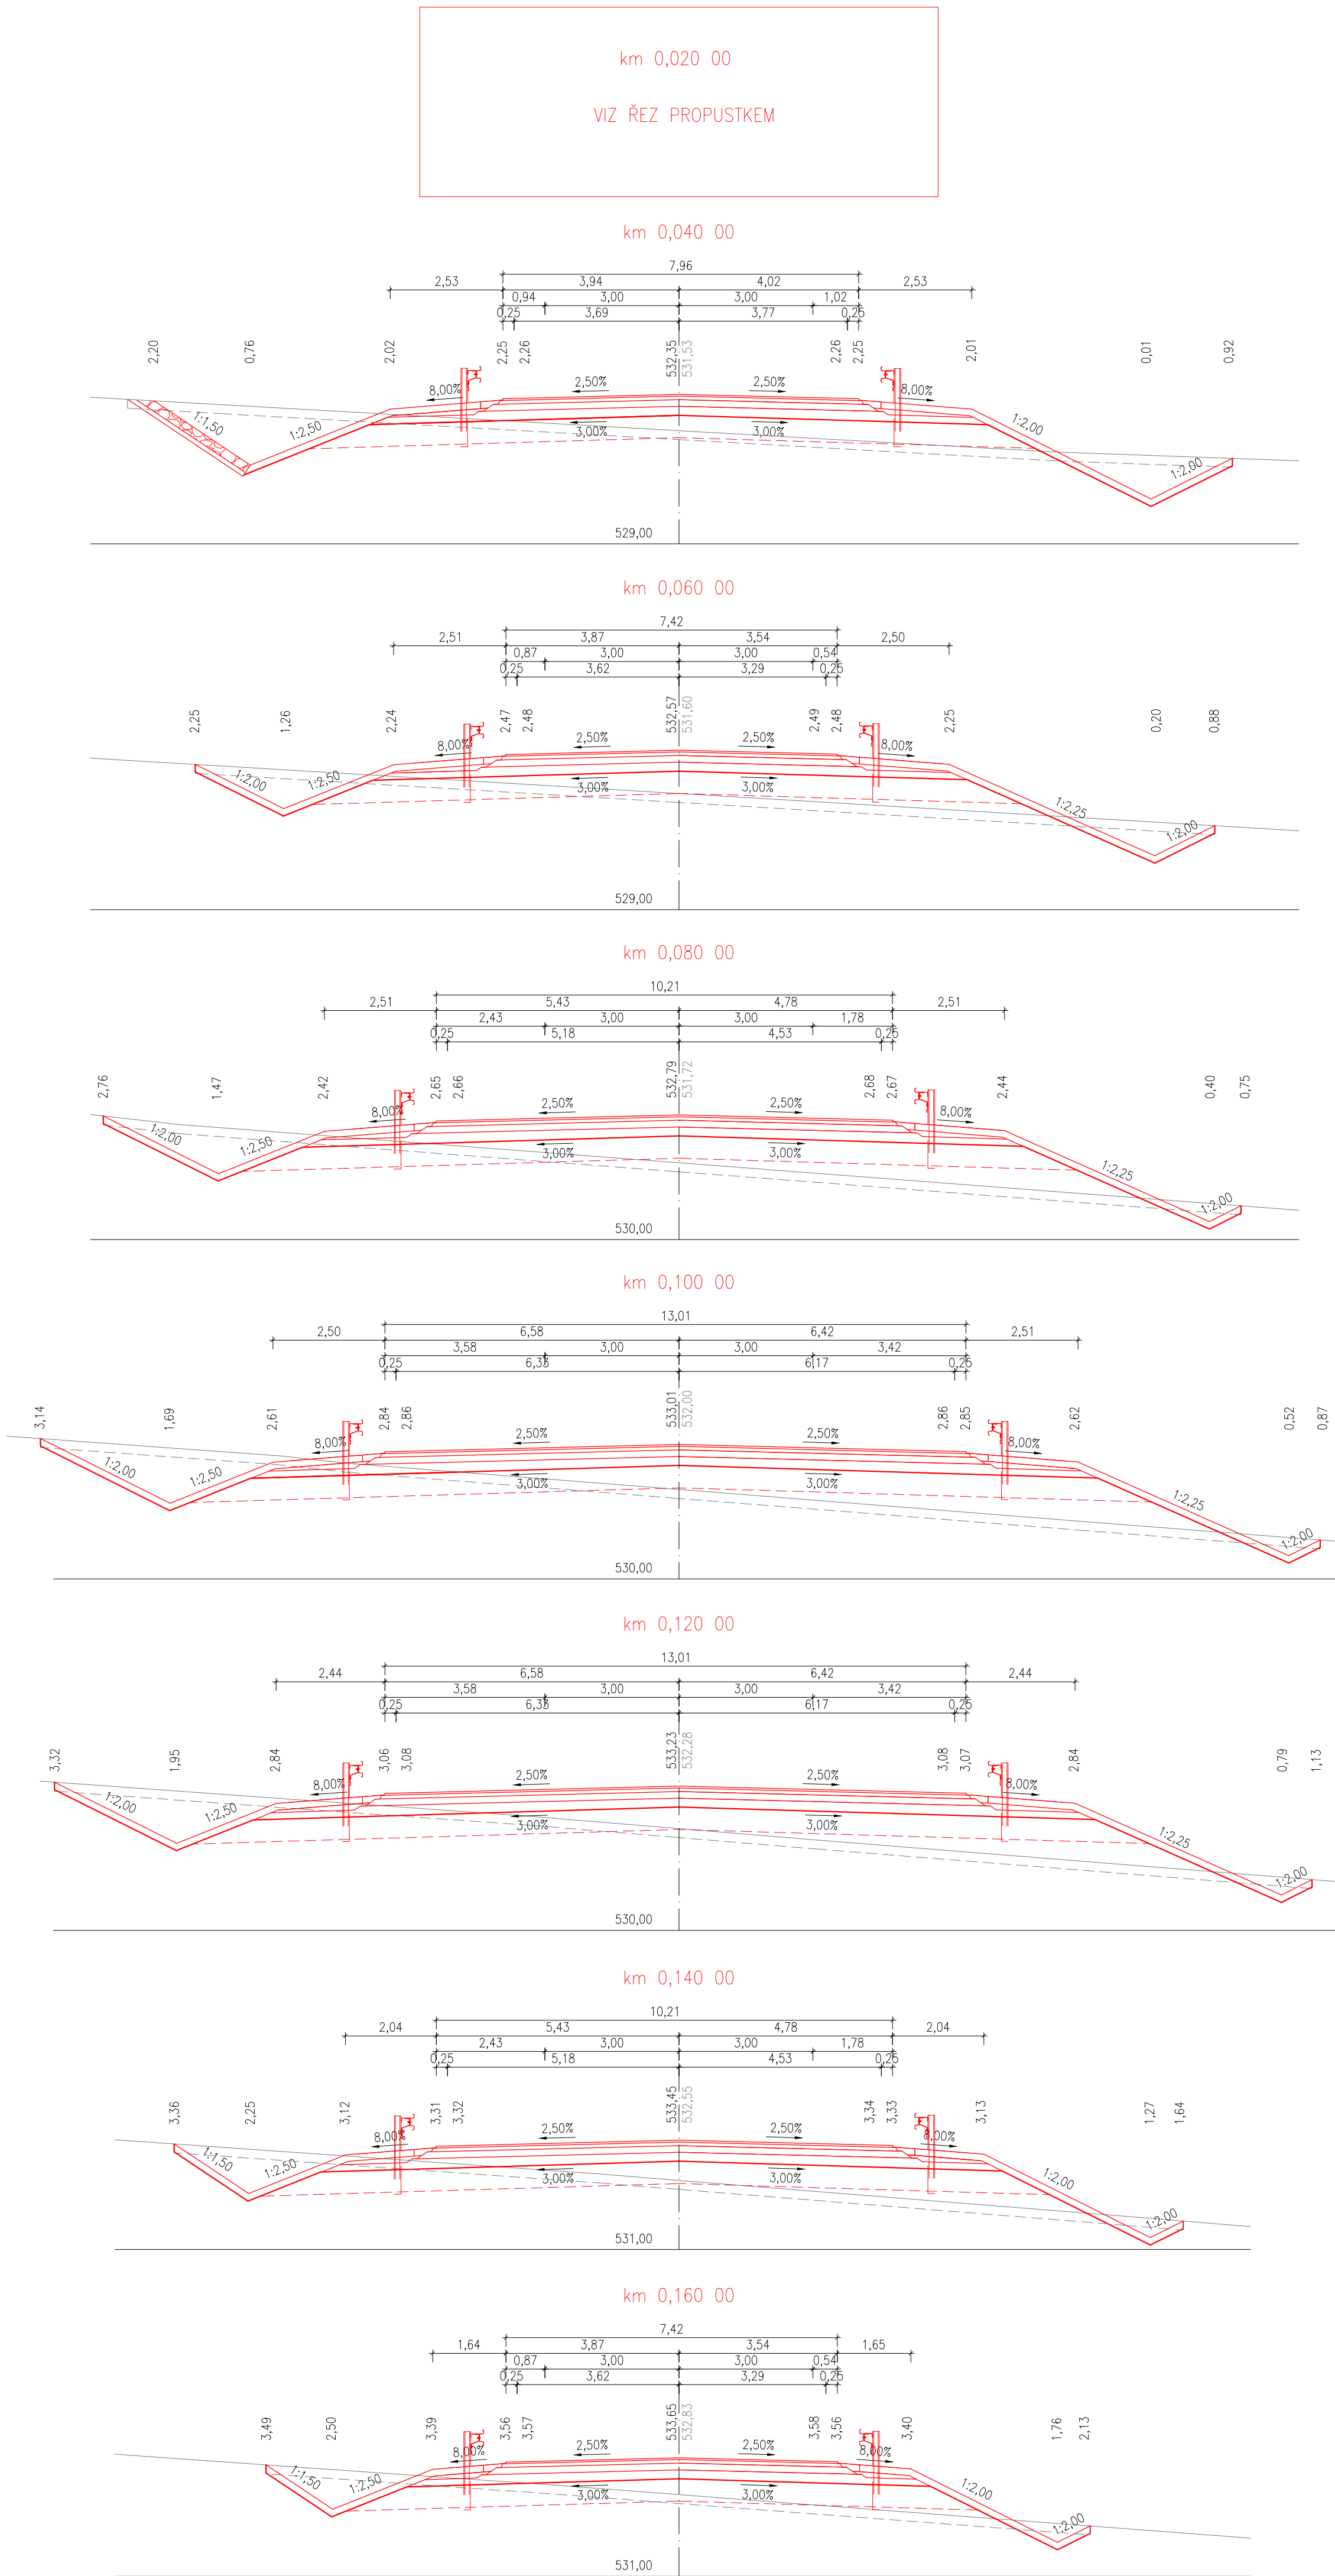

SO 124

D.1.1

VÝŠKOVÝ SYSTÉM BpV		SOUŘADNICOVÝ SYSTÉM S-JTSK	
Číslo změny:	Obsah změny:	Datum změny:	
01	-	-	
02	-	-	
03	-	-	
Objednatel:		Ředitelství silnic a dálnic s. p. Na Pankraci 540/56, 140 00 Praha 4 Stavbu zajišťuje Závod Praha Na Pankraci 540/56, 140 00 Praha 4	
			
Zhotovitel: Společnosti ve sdružení		SG_Velké projekty BIM 2020 zastoupené	
SUDOP PRAHA a.s. Hlavní inženýr projektu: Ing. Roman Petřík		Ošarská 1a, 130 80 Praha 3 telefon: +420 267 094 111	
			
Správce:		Vedoucí týmu:	Asistent vedoucího týmu:
		SUDOP PRAHA a.s. Ošarská 1a, 130 80 Praha 3 tel.: +420 267 094 111 e-mail: praha@sudop.cz	ING. PAVEL MICHL Specialista profese: -
Zpracovatel:		ING. ROMAN PETŘÍK	
		projektová, průzkumná a konzultační společnost PUDIS a.s., Podbabská 1014/20, 160 00 Praha 6 tel.: +420 267 004 111, www.pudis.cz, info@pudis.cz	
Vedoucí střediska:		Výpracoval:	Kontroloval:
ING. ZDĚNKA BOLEHOVSKÁ		ING. MICHAL TUREK	ING. MICHAL TUREK
Název akce:		Číslo směry:	
D11 1108 Jaroměř - Trutnov VD-ZDS + TP + AD		22-014.250	
Část:		Datum:	
		VD-ZDS	
D.1.1 OBJEKTY POZEMNÍCH KOMUNIKACÍ VČETNĚ PROPUSTKŮ SO 124 PŘELOŽKA SILNICE III/30015 (KM 132,22)		Číslo části:	
Název přílohy:		D.1.1	
		Měřítko:	Počet fólií:
		1:100	12xA4
PŘÍČNÉ ŘEZY		Číslo přílohy:	5