
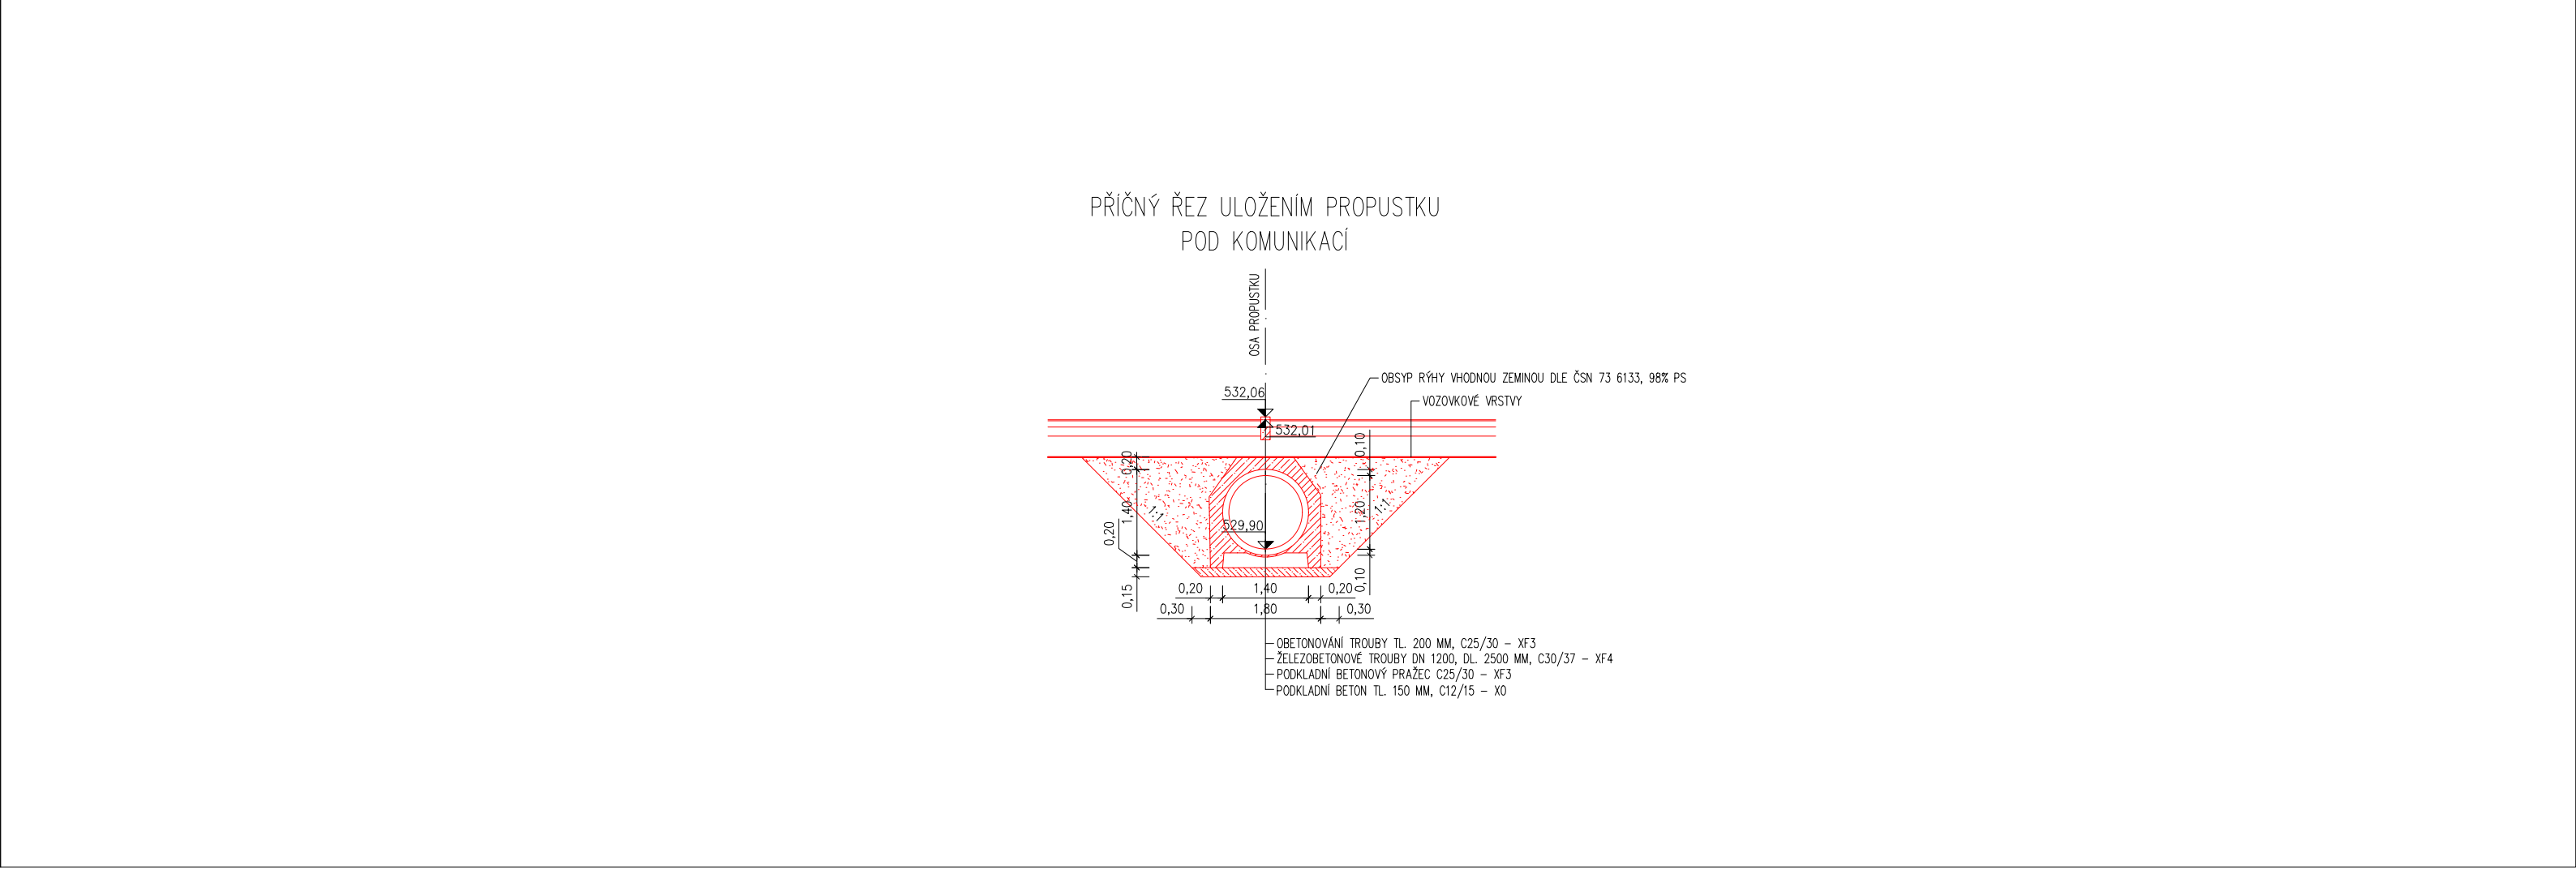
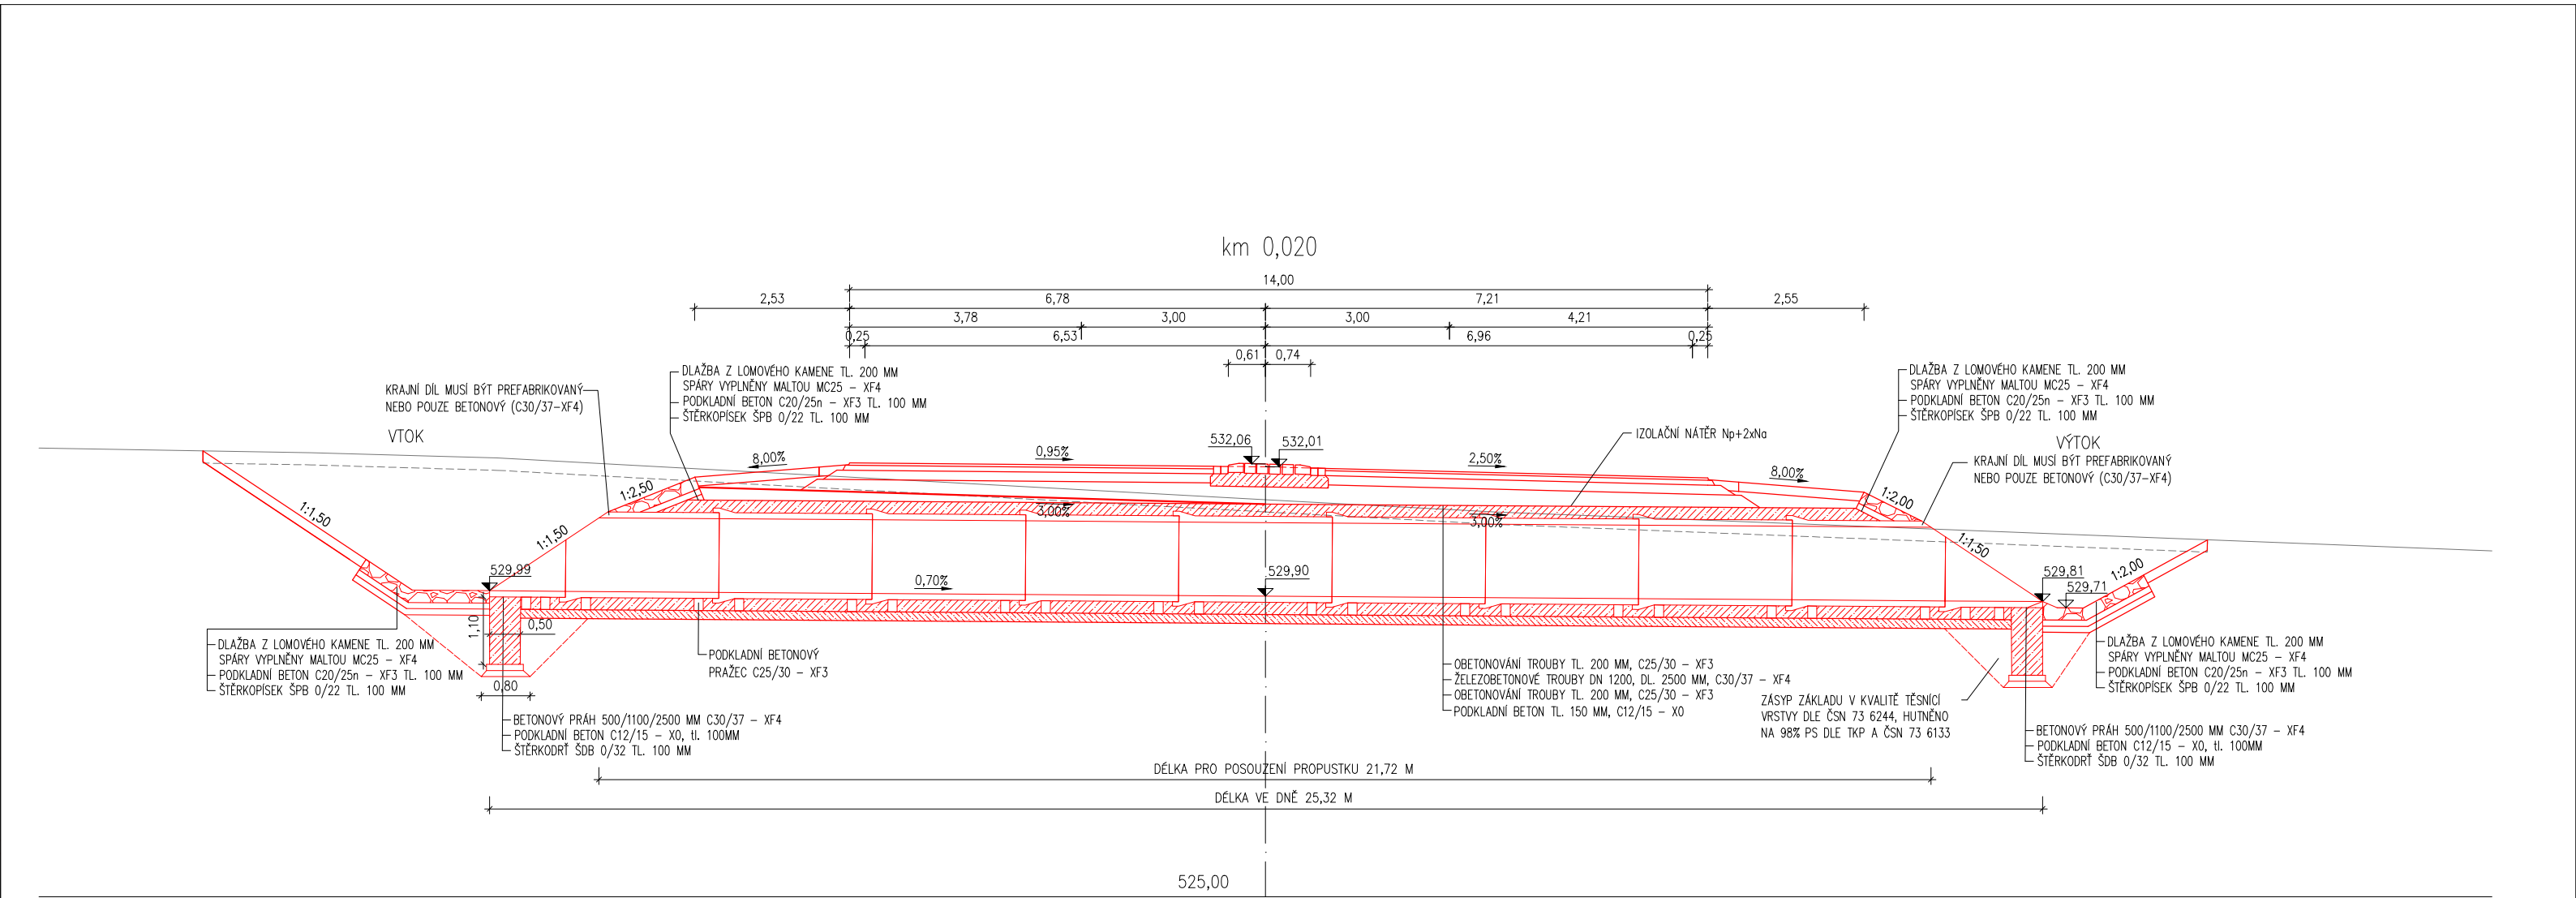


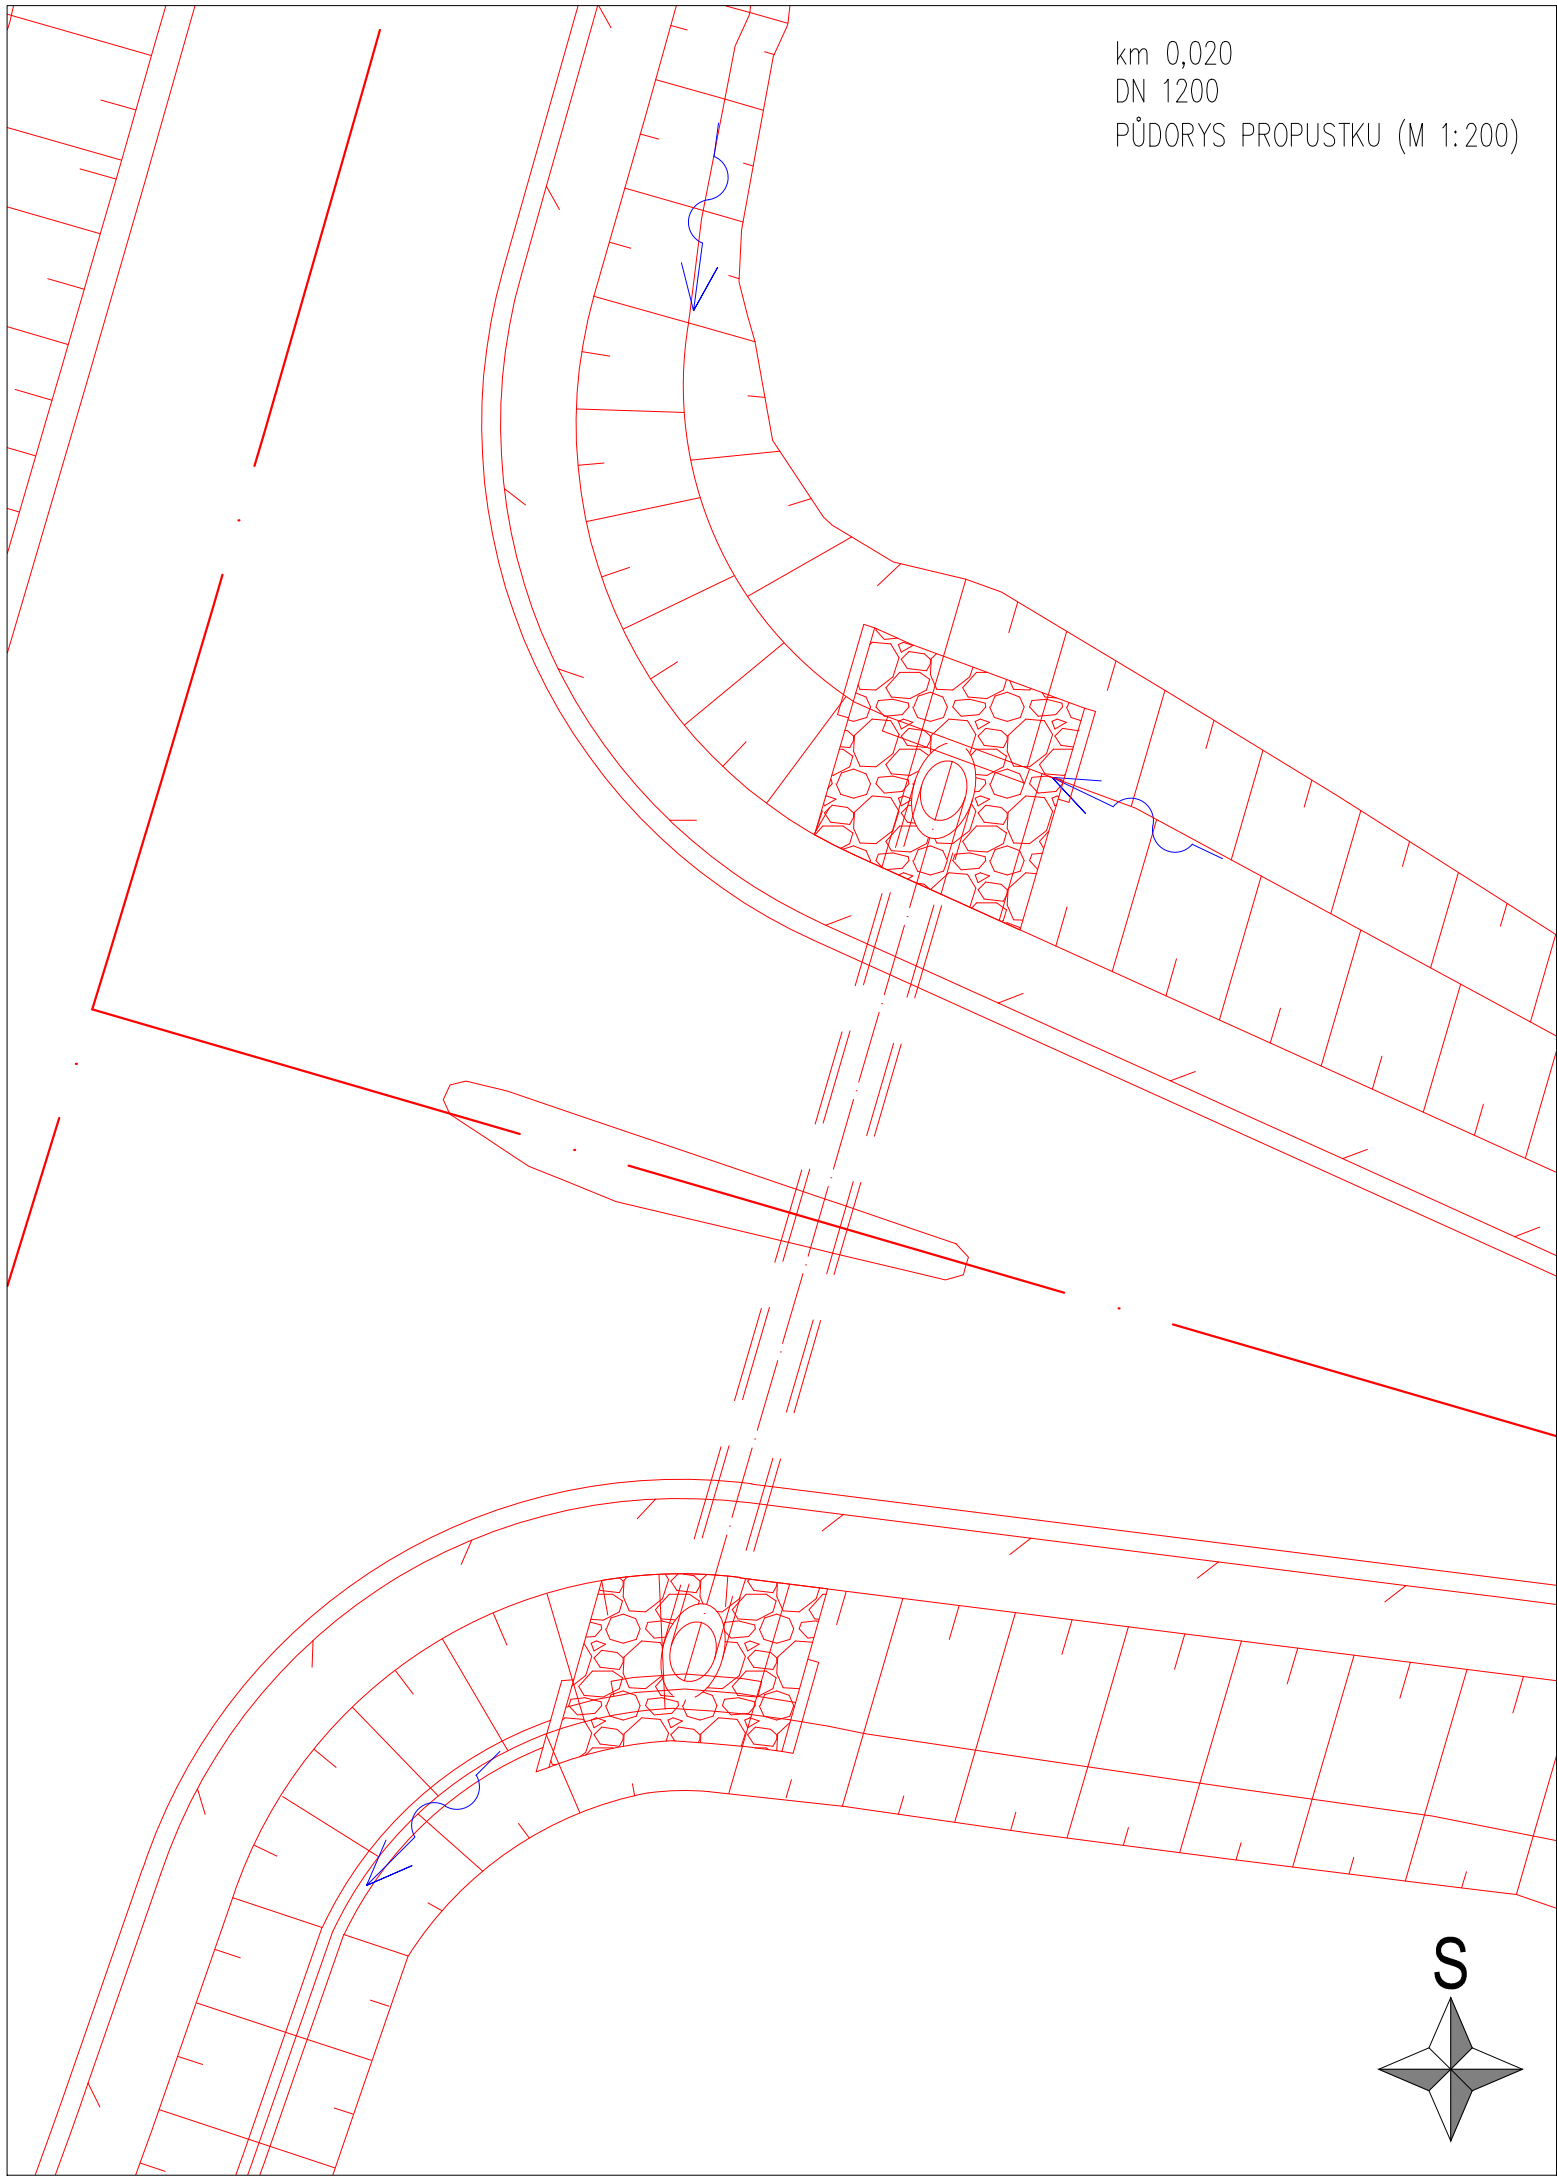

SO 124

D.1.1

VÝŠKOVÝ SYSTÉM Bpv

SOUŘADNICOVÝ SYSTÉM S-JTSK

Číslo změny:	Obsah změny:	Datum změny:
01	-	-
02	-	-
03	-	-

Objednatel:	Ředitelství silnic a dálnic
Ředitelství silnic a dálnic	Na Pankraci 546/56, 140 00 Praha 4
Stavbu zajišťuje	Závod Praha
Na Pankraci 546/56, 140 00 Praha 4	

Zhotovitel: Společníci ve sdružení	SG_Velké projekty BIM 2020
zastoupené	
SUDOP PRAHA a.s.	Olšanská 1a, 130 80 Praha 3
Hlavní inženýr projektu: Ing. Roman Petřík	telefon: +420 267 094 111

SUDOP PRAHA	PUDIS	SUDOP	DOPRAVOPROJEKT BRNO	DOPRAVOPROJEKT
Správce:	SUDOP PRAHA a.s.	Vedoucí týmu:	Asistent vedoucího týmu:	
	Olšanská 1a, 130 80 Praha 3		ING. PAVEL MICHL	
	tel.: +420 267 094 111		Specialista profese:	
	e-mail: praha@sudop.cz	ING. ROMAN PETŘÍK	-	

Zpracovatel částí:	projektová, průzkumná a konzultační společnost
PUDIS	PUDIS a.s., Podbabská 1014/20, 160 00 Praha 6
	tel.: +420 267 004 111, www.pudis.cz, info@pudis.cz

Vedoucí střediska:	Odpovědný projektant SO, IO, PS:	Vypracoval:	Kontroloval:
ING. ZDEŇKA BOLEHOVSKÁ	ING. MICHAL TUREK	ING. TOMÁŠ VÁŇA	ING. MICHAL TUREK

Název akce:	Číslo smlouvy:	
	22-014.250	
D11 1108 Jaroměř - Trutnov VD-ZDS + TP + AD	Projektový stupeň:	
	VD-ZDS	
Část:	Datum:	
	11/2024	
D.1.1 OBJEKTY POZEMNÍCH KOMUNIKACÍ VČETNĚ PROPUSTKŮ SO 124 PŘELOŽKA SILNICE III/30015 (KM 132,22)	Číslo částí:	
	D.1.1	
Název přílohy:	Měřítko:	Počet formátů:
	1:100	4xA4
PROPUSTEK DN 1200 V KM 0,020	Číslo přílohy:	
	6	

DOKUMENT LZE UŽÍVAT POUZE VE SMYSLU PŘÍSLUŠNÉ SMLOUVY O DILO. ŽÁDNÁ JEHO ČÁST NEMŮŽE BYT DLE ZÁKONA č. 121/2000 Sb. KOPÍROVÁNA NEBO JINÝM ZPŮSOBEM ROZŠÍŘOVÁNA. BEZ SOUHLASU SUDOP PRAHA a.s.