
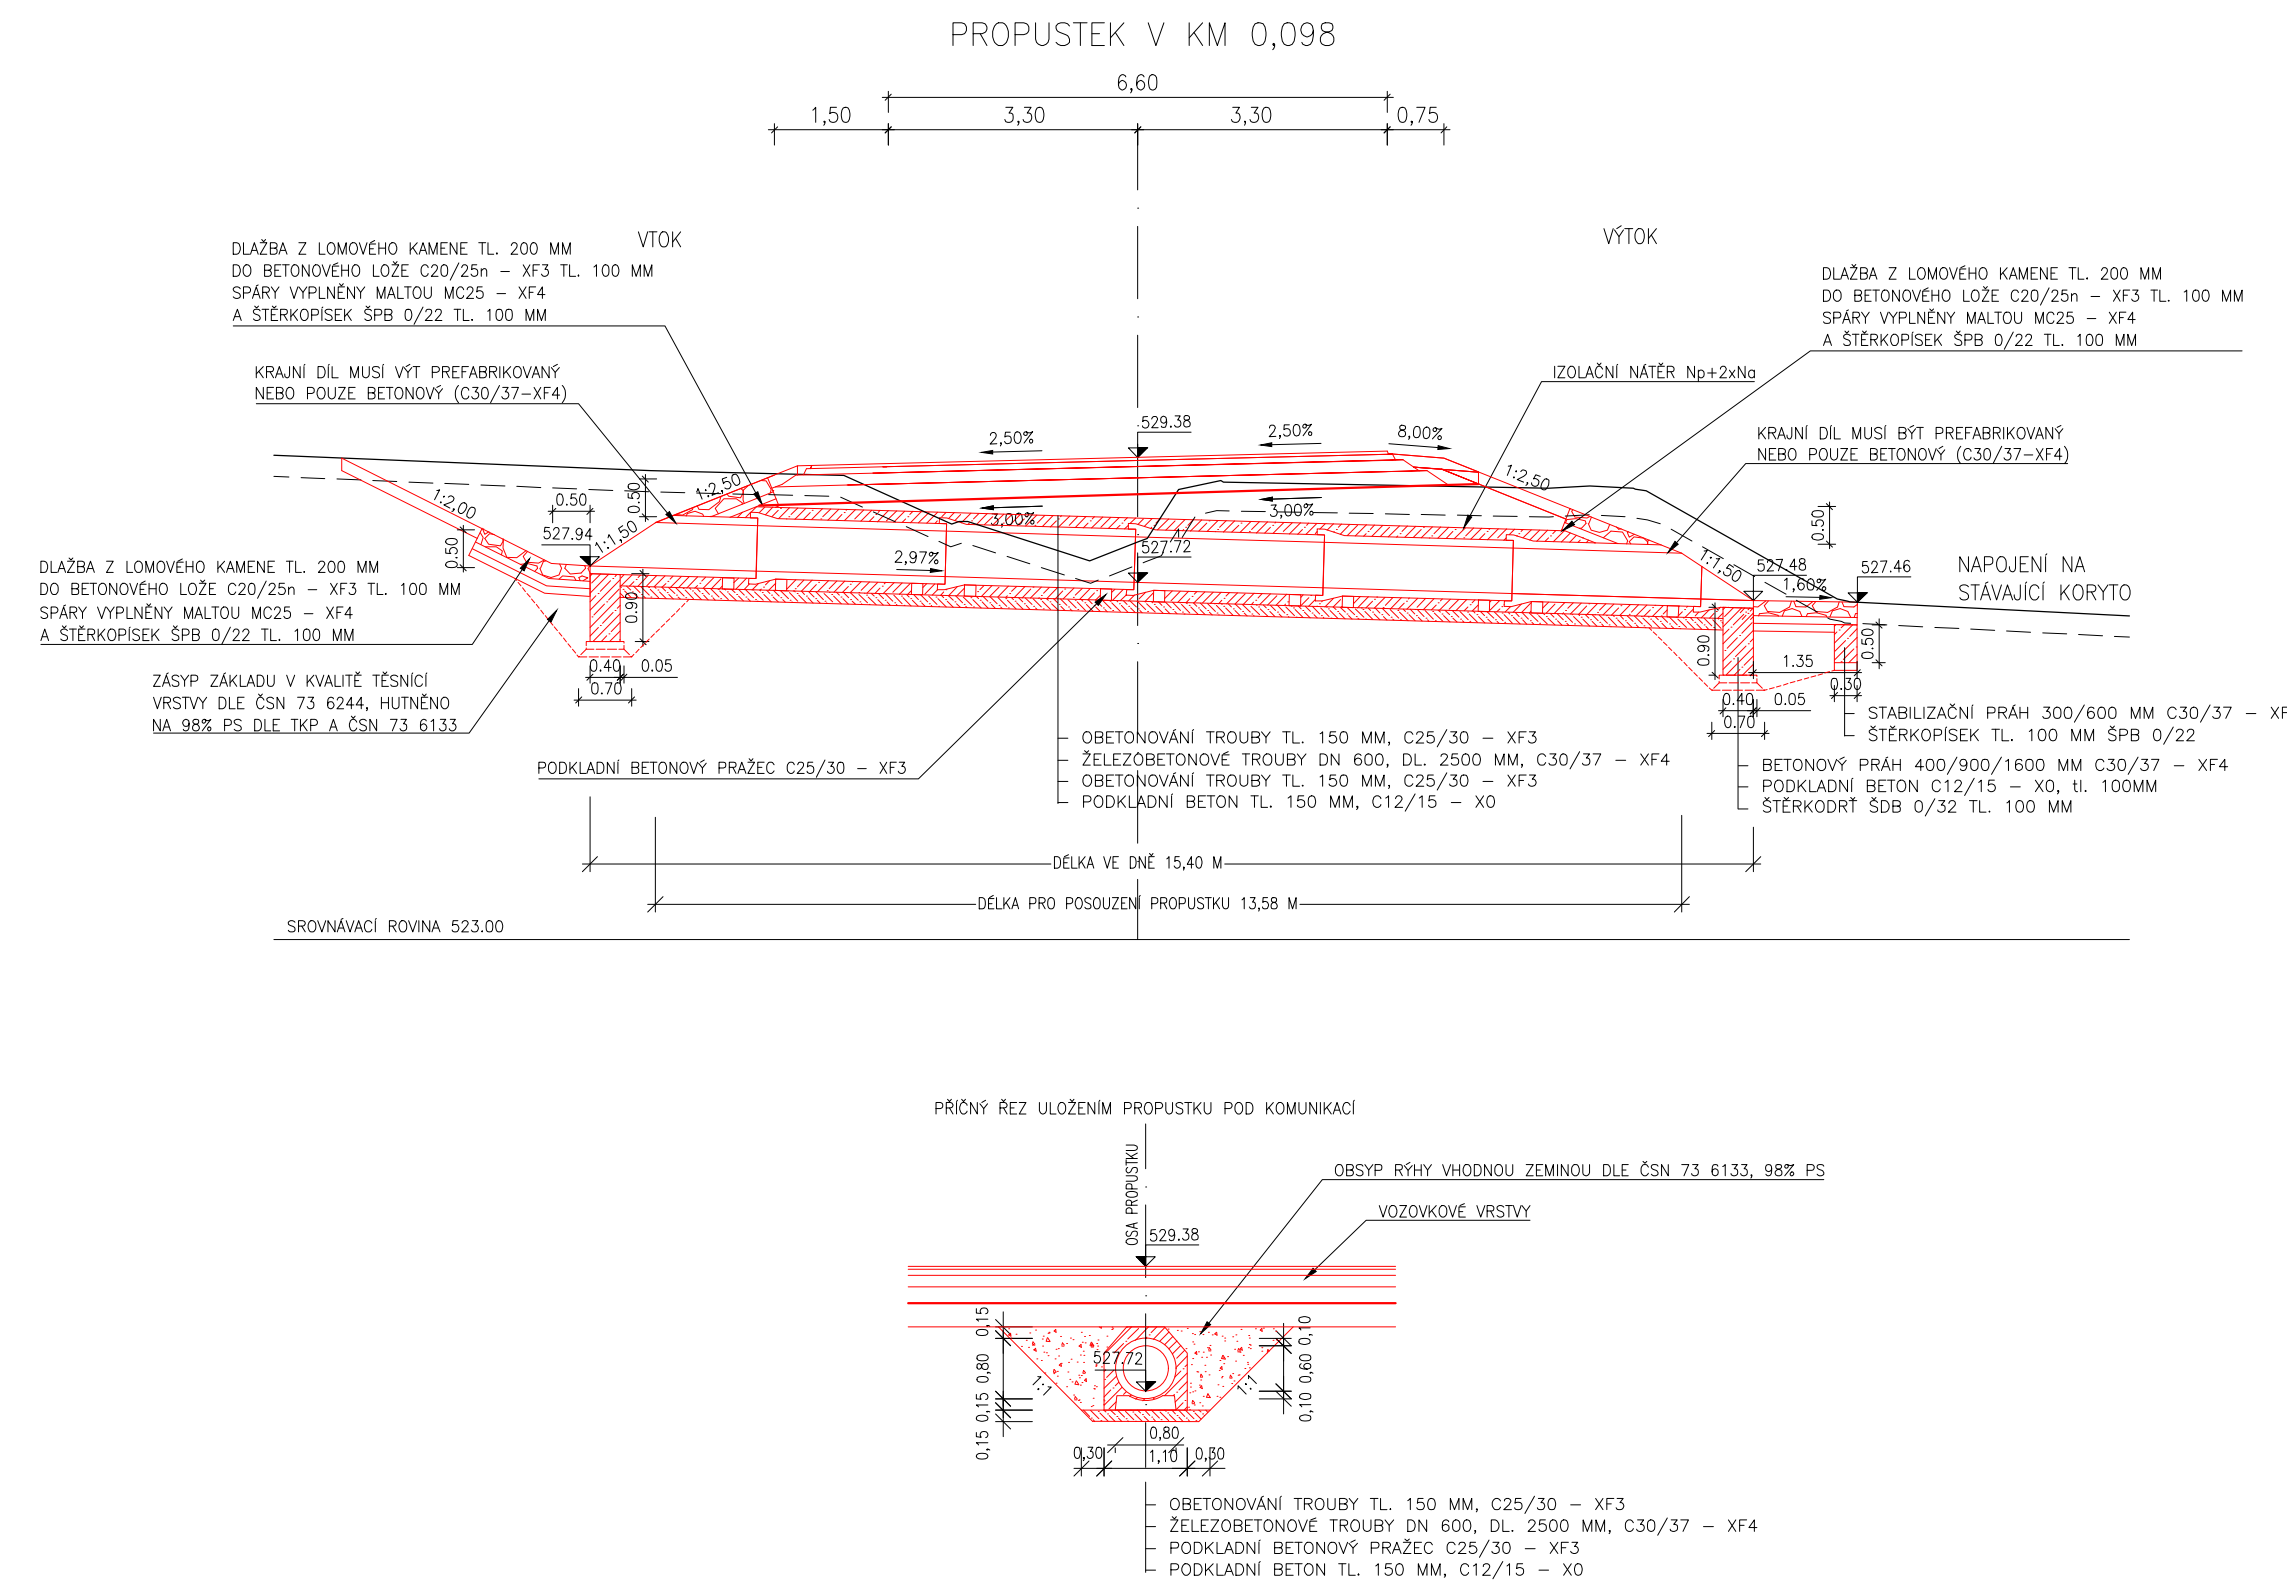


km 0,098
DN 600
PŮDORYS PROPUSTKU (M 1:100)

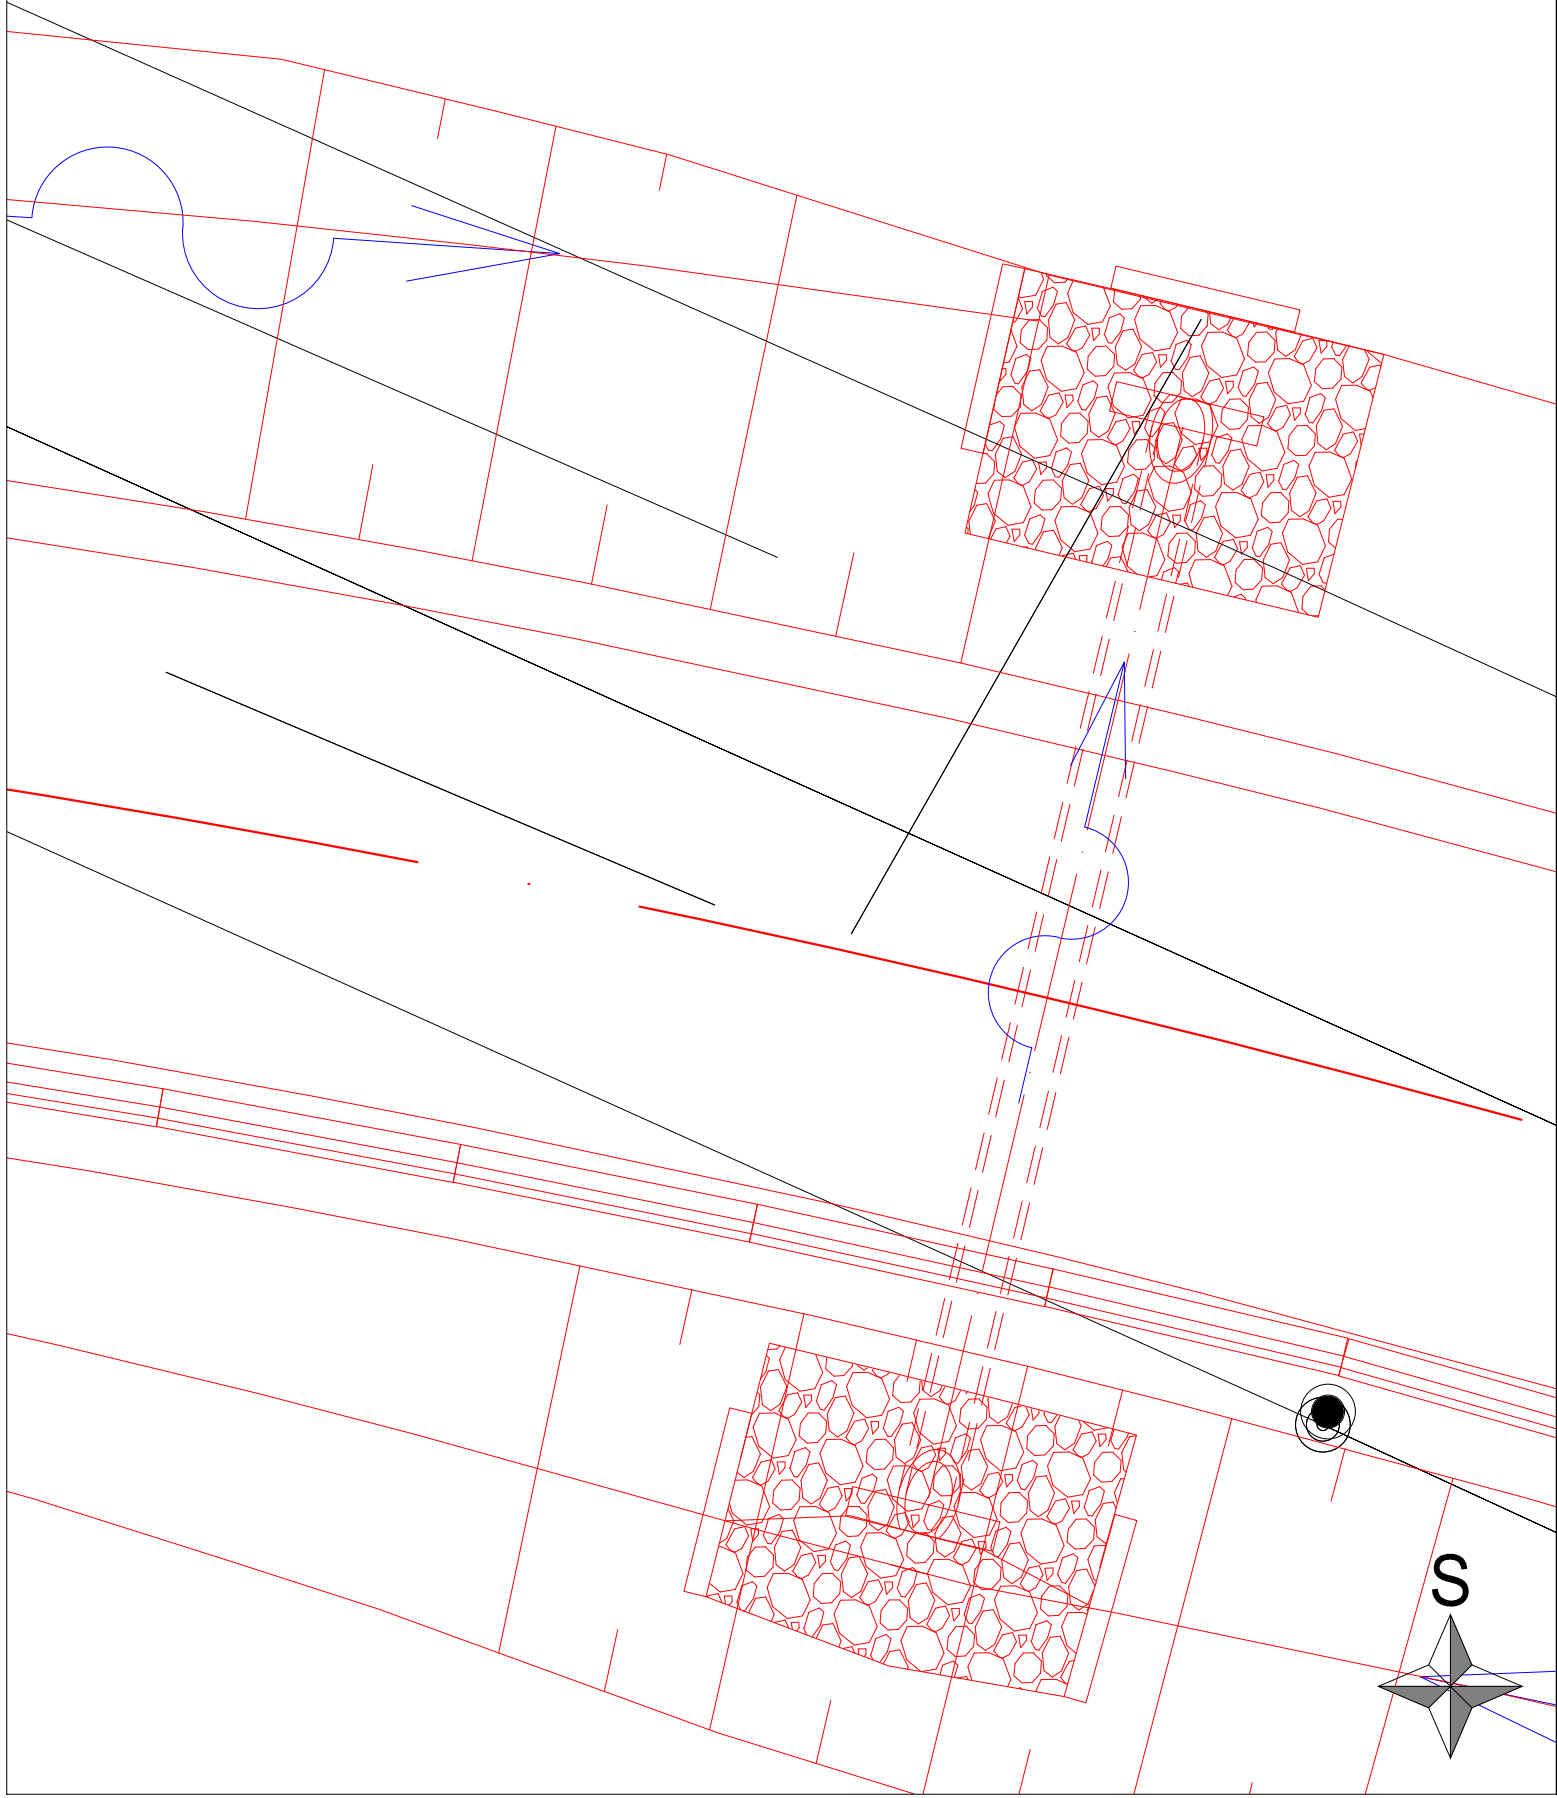

SO 125
D.1.1

VÝŠKOVÝ SYSTÉM B_pv

SOUŘADNICOVÝ SYSTÉM S-JTSK

Číslo změny:	Obsah změny:	Datum změny:
01	-	-
02	-	-
03	-	-

Objednatel:  ŘEDITELSTVÍ SILNIC A DÁLNIC	Ředitelství silnic a dálnic s. p. Na Pankráci 546/56, 140 00 Praha 4 Stavbu zajišťuje Závod Praha Na Pankráci 546/56, 140 00 Praha 4
--	--

<i>Zhotovitel: Společníci ve sdružení</i>		SG_Velké projekty_BIM 2020 zastoupené	
SUDOP PRAHA a.s. Hlavní inženýr projektu: Ing. Roman Petřík		Olšanská 1a, 130 80 Praha 3 telefon: +420 267 094 111	
			
			

<i>Spřávce:</i>  SUDOP PRAHA	SUDOP PRAHA a.s. Olšanská 1a, 130 80 Praha 3 tel.: +420 267 094 111 e-mail: praha@sudop.cz	<i>Vedoucí týmu:</i> ING. ROMAN PETŘÍK	<i>Asistent vedoucího týmu:</i> ING. PAVEL MICHL <i>Specialista profese:</i> -
--	---	--	--


projektová, průzkumná a konzultační společnost
 PUDIS a.s., Podbabská 1014/20, 160 00 Praha 6
 tel.: +420 267 004 111, www.pudis.cz, info@pudis.cz

Vedoucí střediska:	Odpovědný projektant SO, IO, PS:	Vypracoval:	Kontroloval:
ING. ZDĚŇKA BOLEHOVSKÁ	ING. MICHAL TUREK	BC. ZARRINA UTEULINA	ING. MICHAL TUREK

Název akce:	Číslo smlouvy:	
	22-014.250	
D11 1108 Jaroměř - Trutnov VD-ZDS + TP + AD	Projektový stupeň:	
	VD-ZDS	
Část:	Datum:	
D.1.1 OBJEKTY POZEMNÍCH KOMUNIKACÍ VČETNĚ PROPUSTKŮ SO 125 PŘELOŽKA III/30016 (KM 132,15)	11/2024	
	Číslo části:	
Název přílohy:	D.1.1	
	Měřítko:	Počet formátů:
	1:100	4xA4
PROPUSTEK DN 600 V KM 0,098	Číslo přílohy:	
	6.1	