
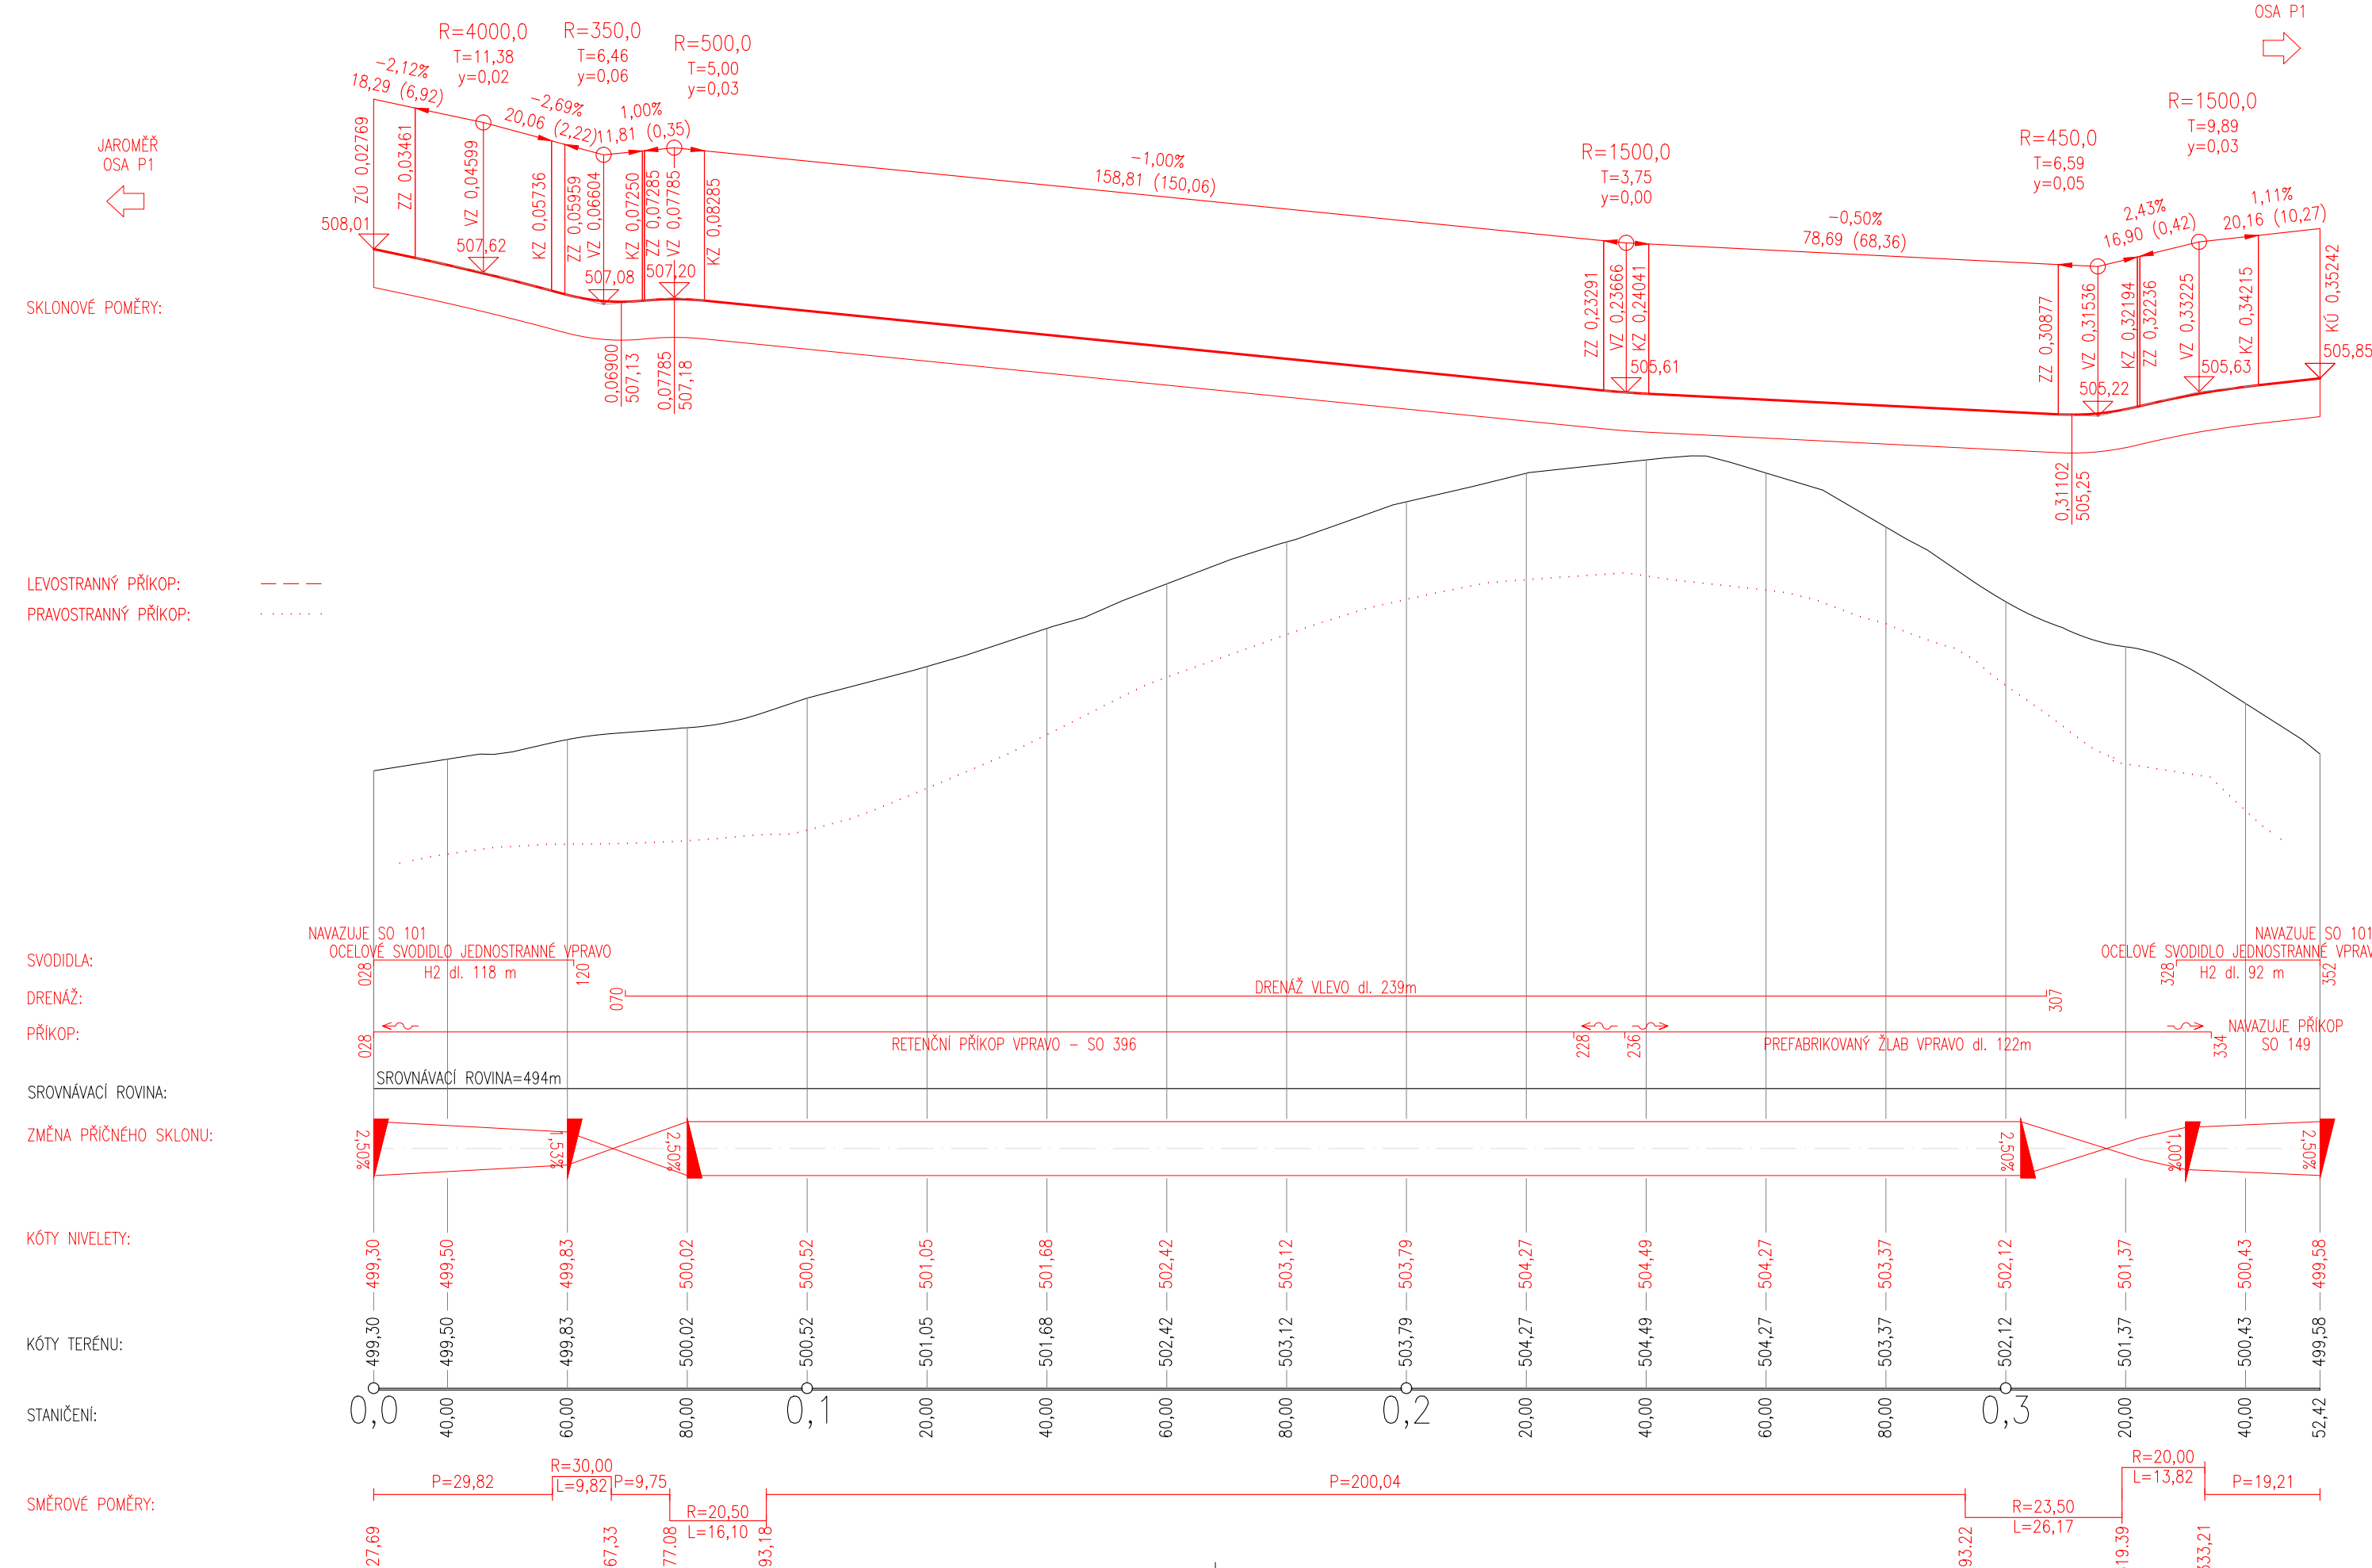
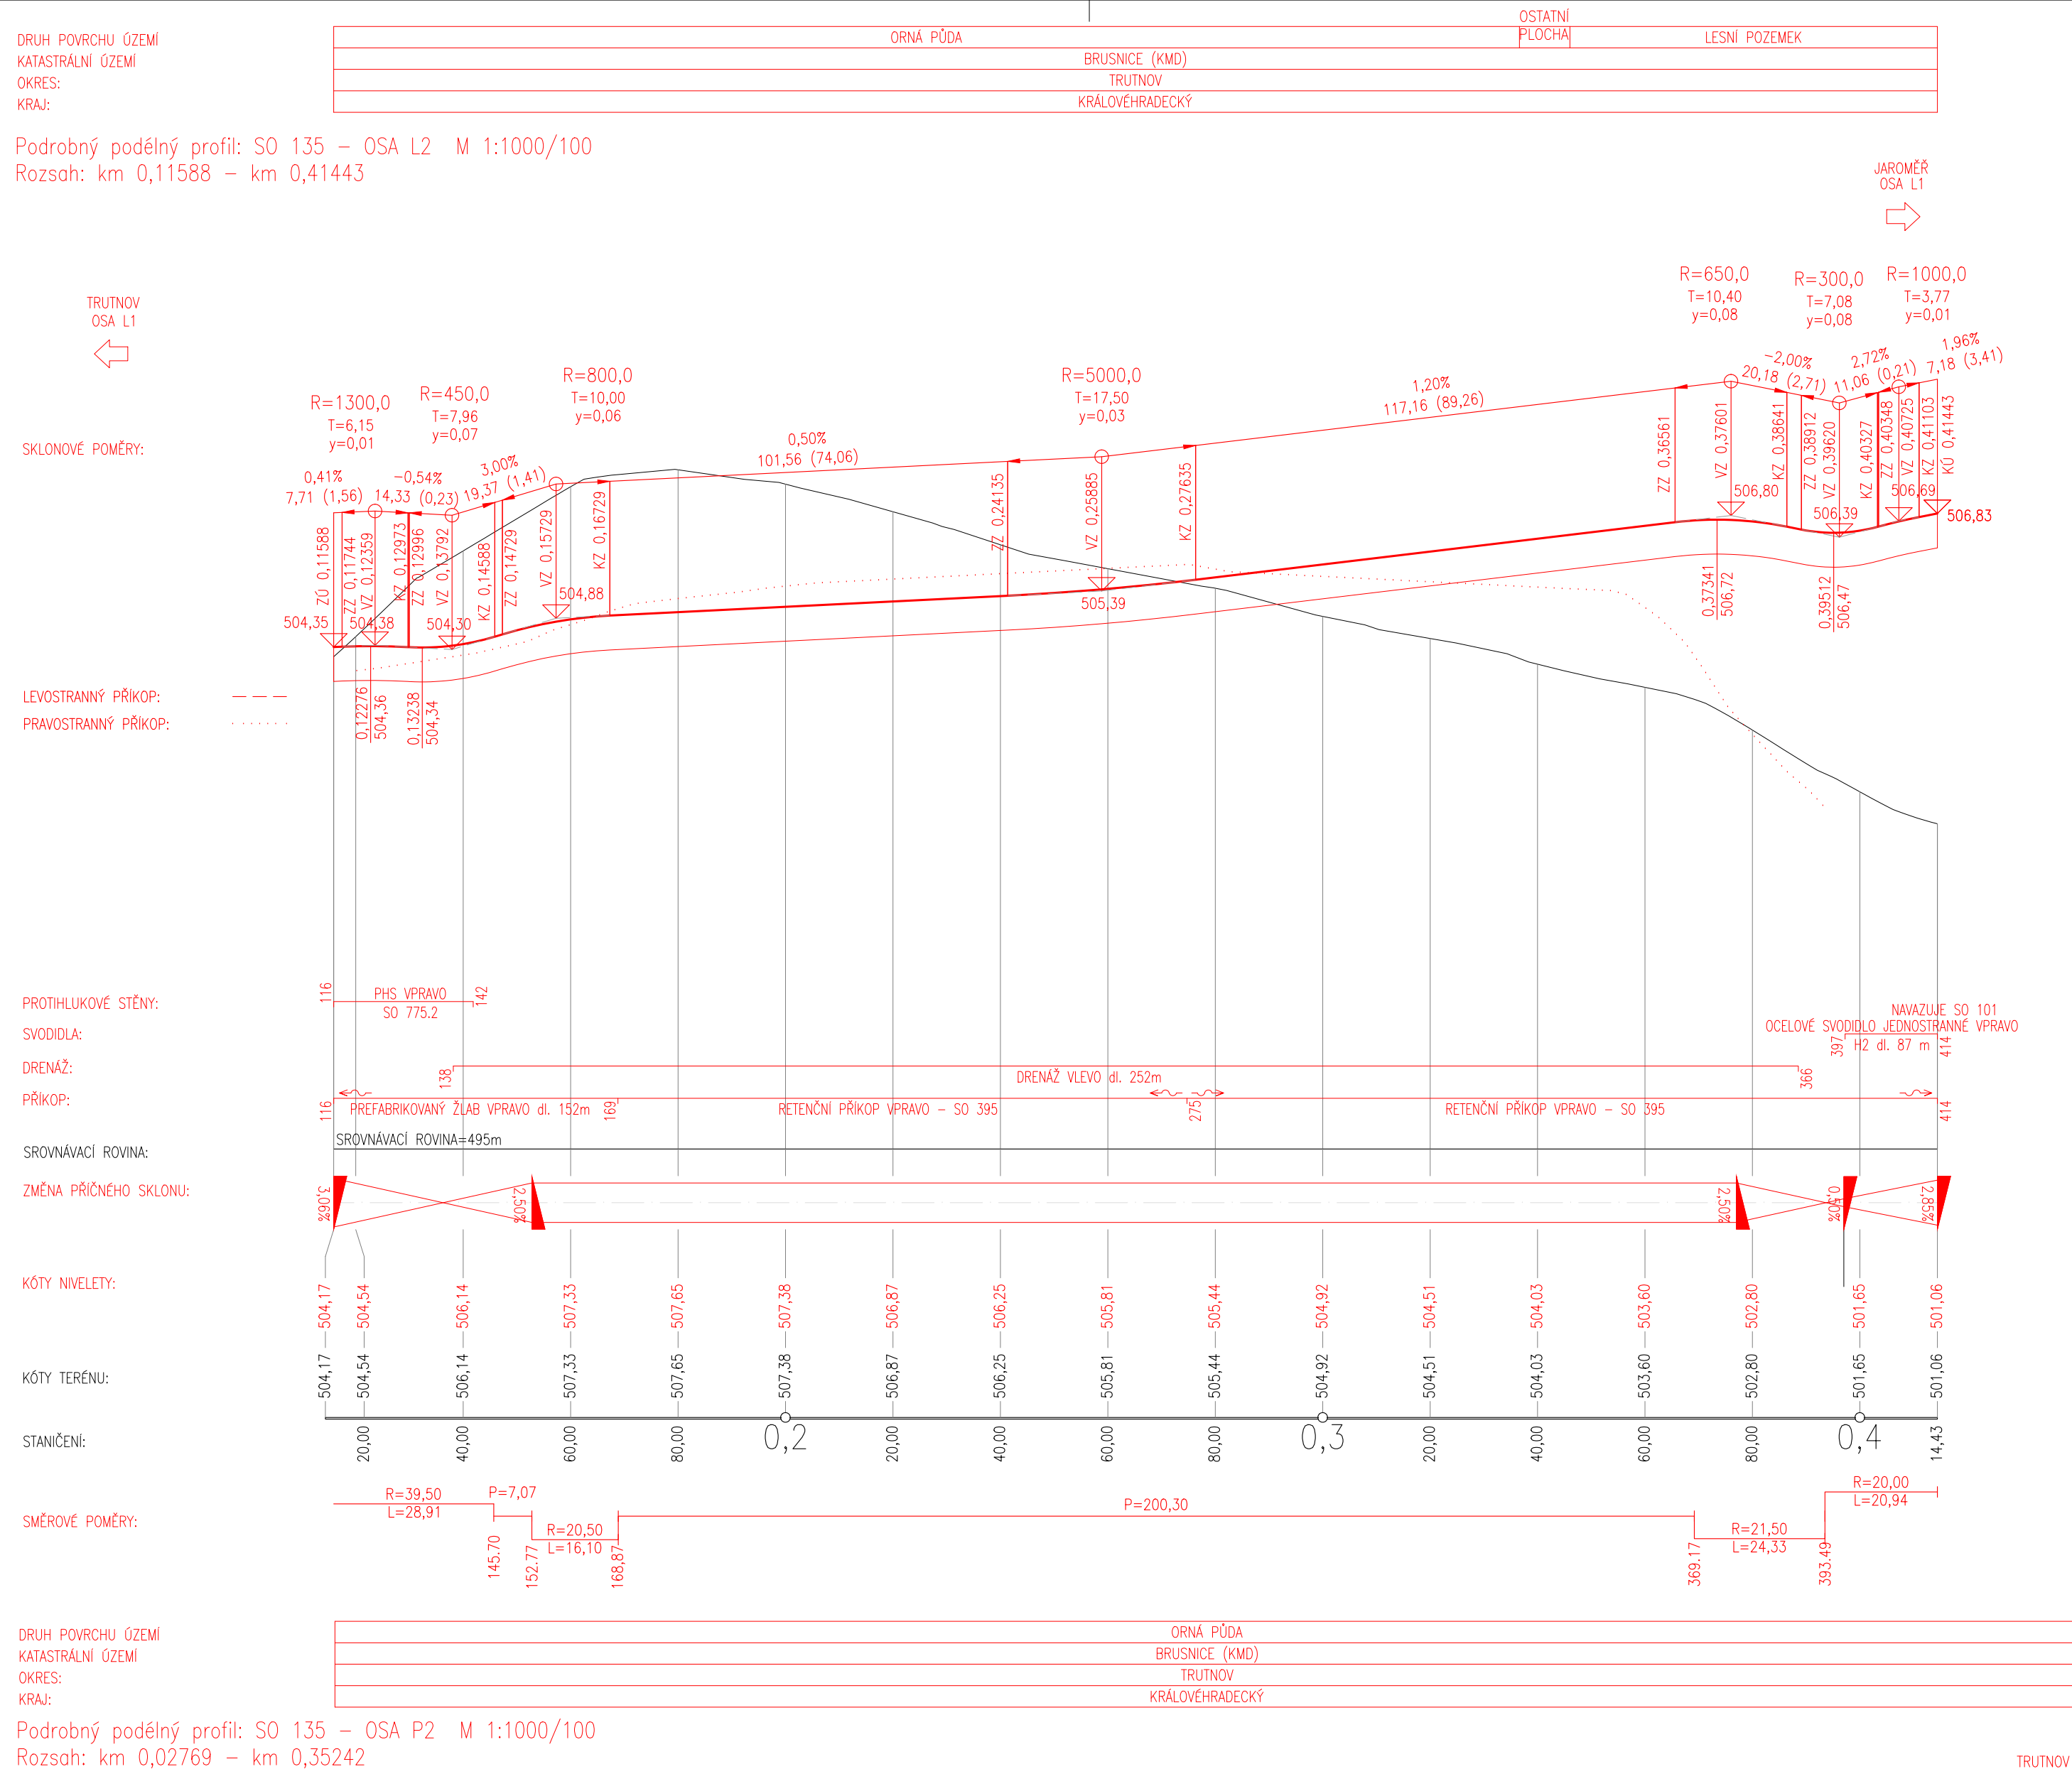
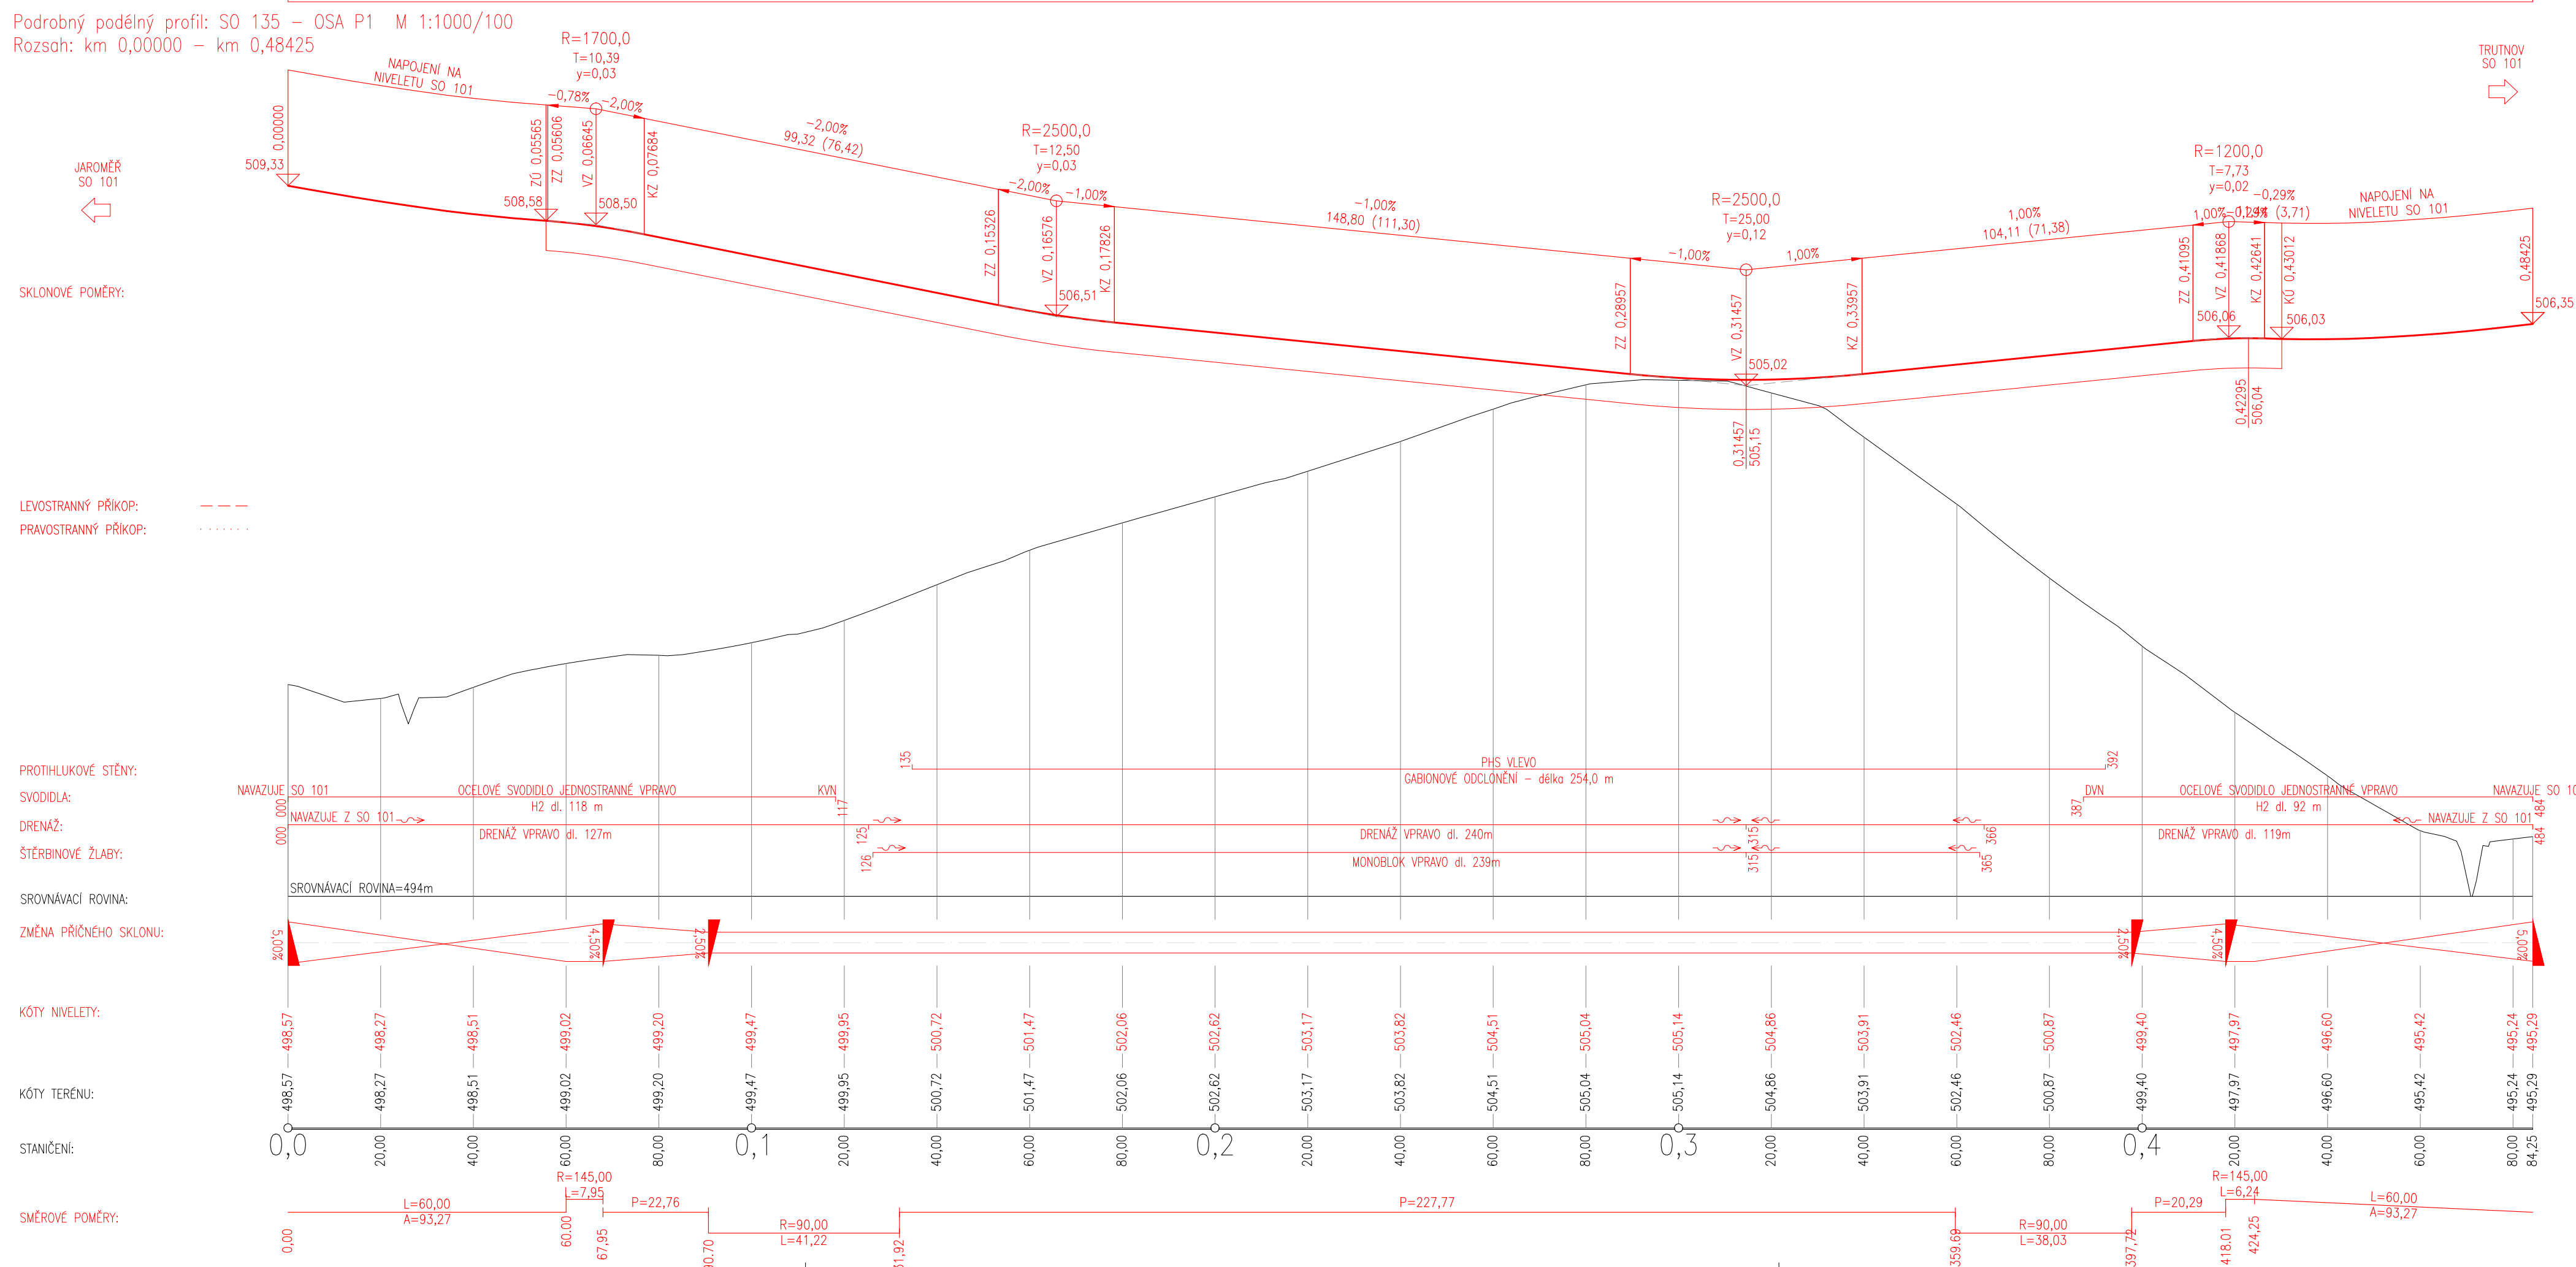


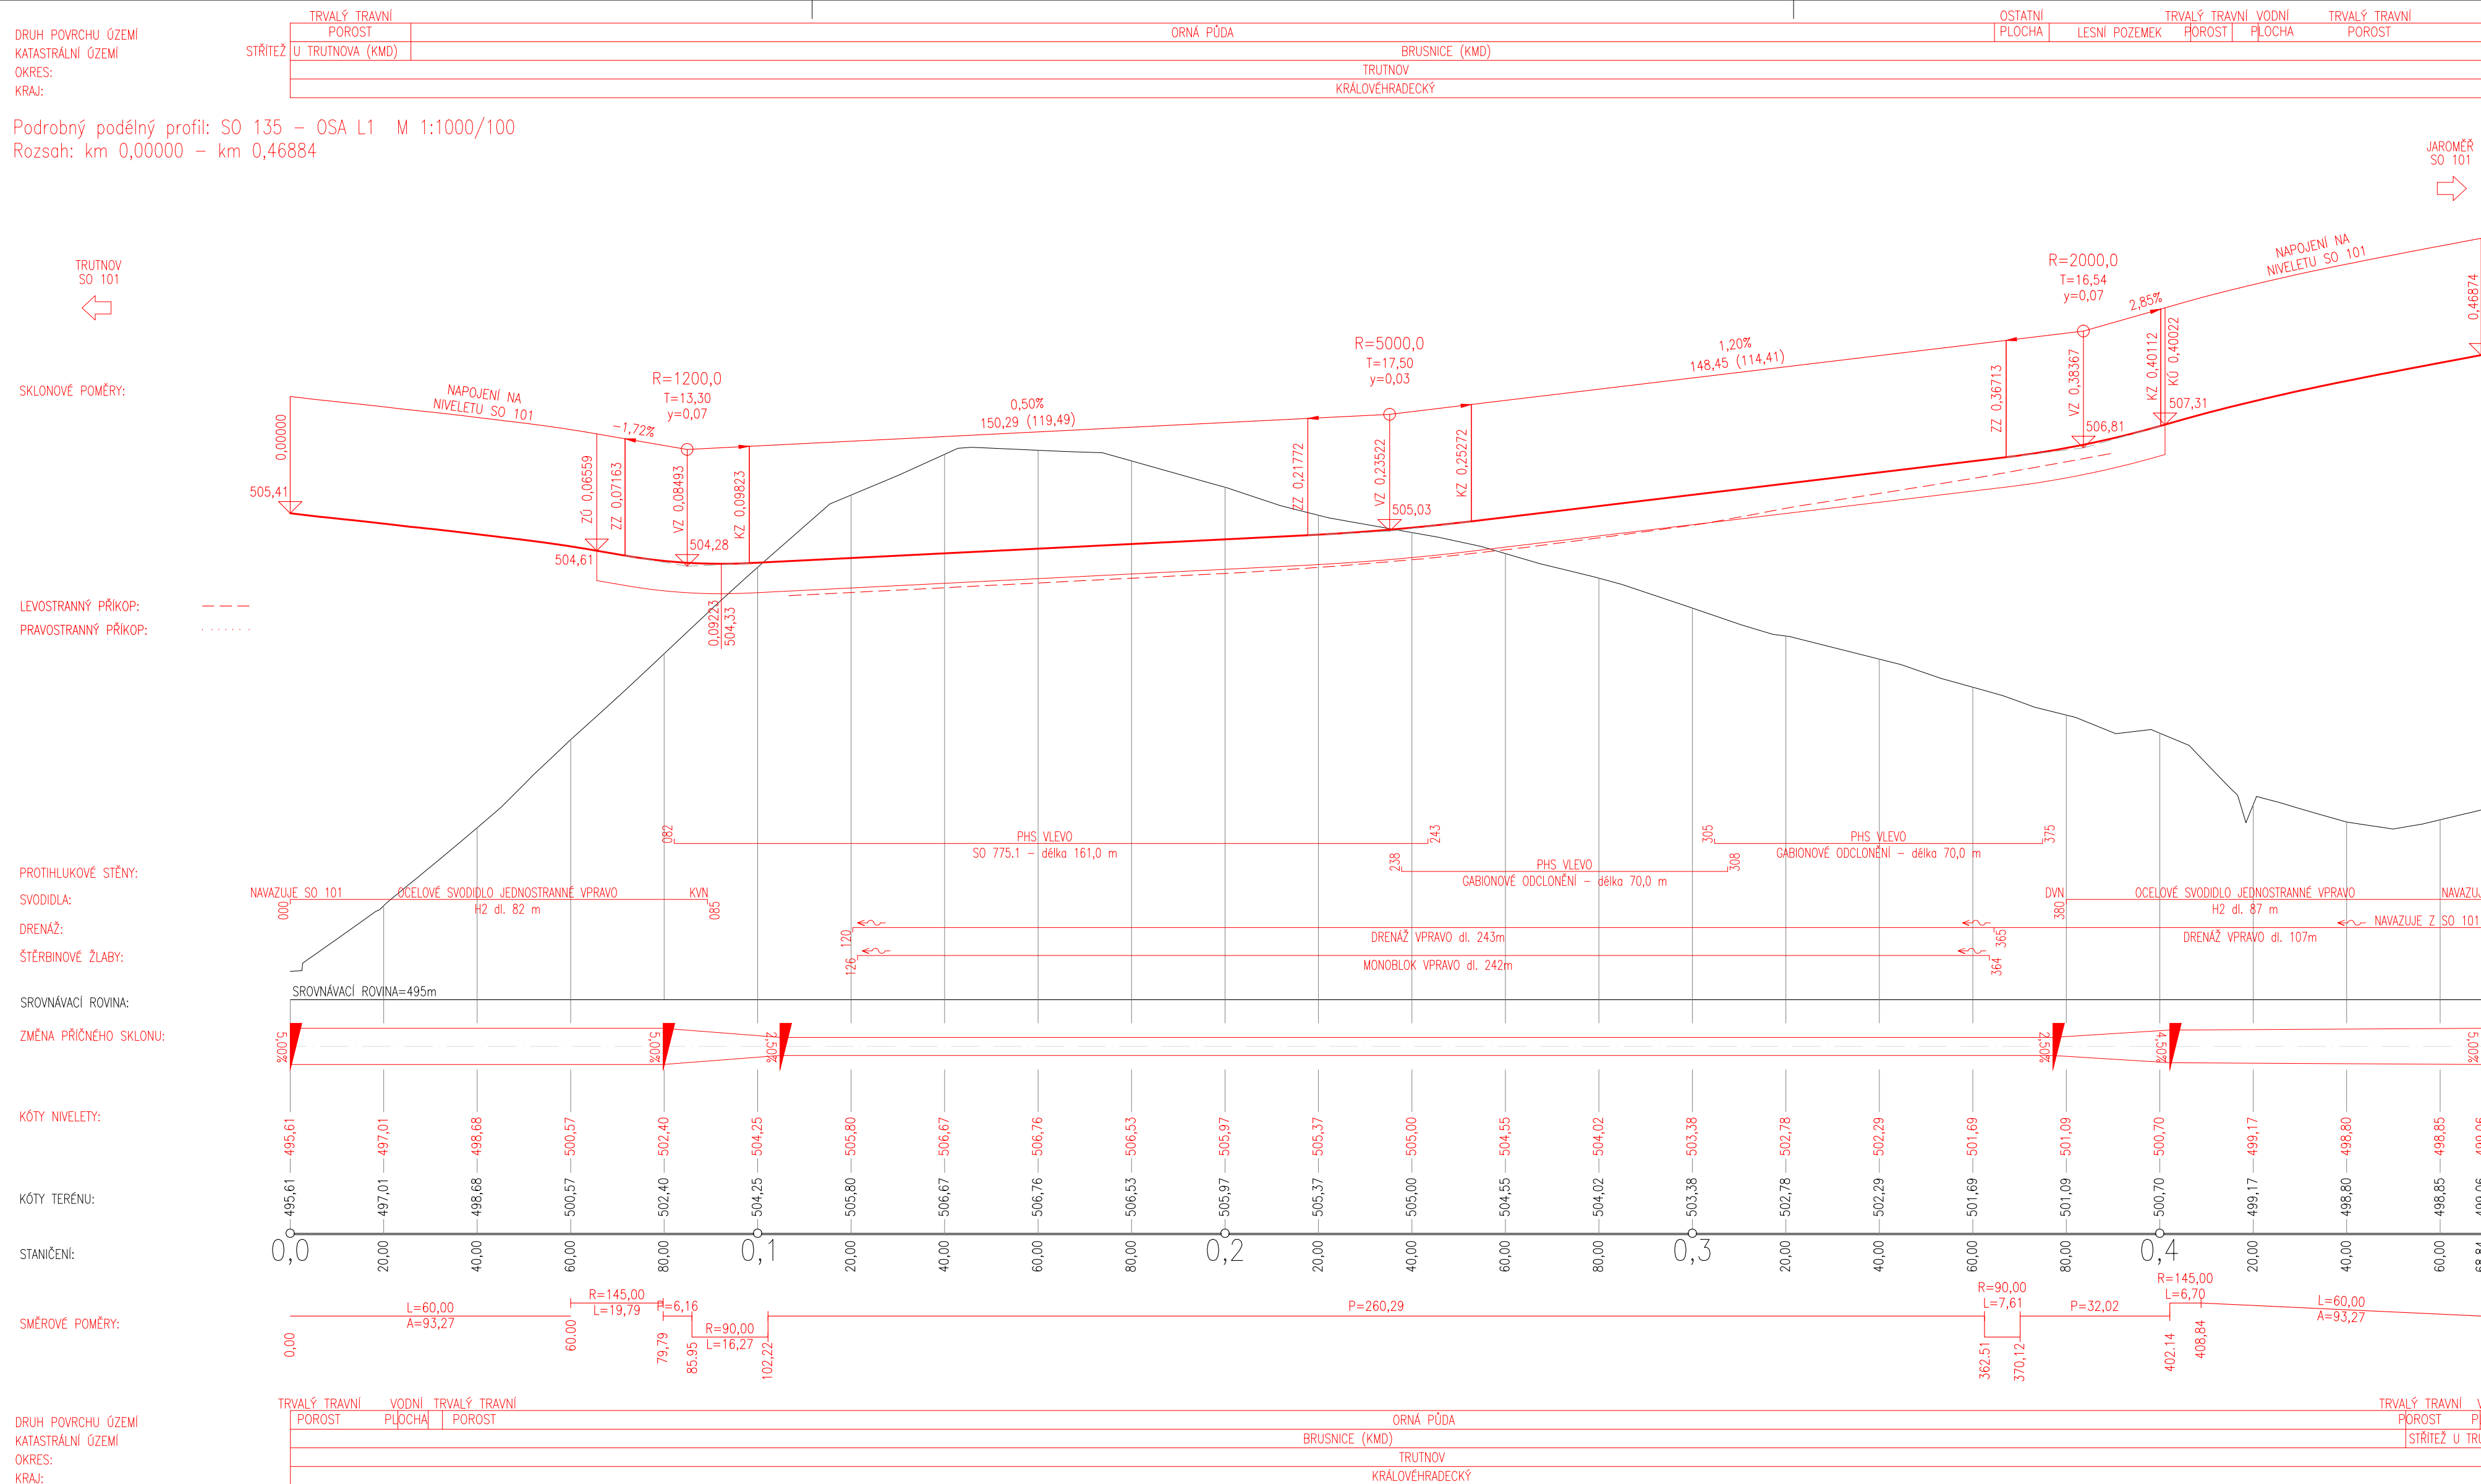

SO 135

D.1.1

VÝŠKOVÝ SYSTÉM BpV

SOUŘADNICOVÝ SYSTÉM S-JTSK

Číslo změny:	Obsah změny:	Datum změny:
01	-	-
02	-	-
03	-	-

Objednatel:

Ředitelství silnic a dálnic ČR
Na Pankraci 546/56, 140 00 Praha 4
Stavbu zajišťuje Závod Praha
Na Pankraci 546/56, 140 00 Praha 4

Zhotovitel: Společnosti ve sdružení
SG_Veiké projekty, BIM 2020
zastoupené
SUDOP PRAHA a.s.
Hlavní inženýr projektu: Ing. Roman Petřík
Ošanská 1a, 130 80 Praha 3
telefon: +420 267 094 111

Správc:

SUDOP PRAHA a.s.
Ošanská 1a, 130 80 Praha 3
tel.: +420 267 094 111
e-mail: praha@sudop.cz

Vedoucí týmu:
Ing. PAVEL MICHL
Specialista profese: -

Zpracovatel:

projektová, průzkumná a konzultační společnost
PUDIS a.s., Podbabská 1014/20, 160 00 Praha 6
tel.: +420 267 004 111, www.pudis.cz, info@pudis.cz

Vedoucí střediska:
Ing. ZDEŇKA BOLEHOVSKÁ

Odpovědný projektant SO, I/O, P/S:
Ing. MICHAL TUREK

Vypracoval:
PETR KOTLABA

Kontroloval:
Ing. MICHAL TUREK

Název akce:
D11 1108 Jaroměř - Trutnov VD-ZDS + TP + AD

Projektový stupeň:
VD-ZDS

Čas:
11/2024

**D.1.1 OBJEKTY POZEMNÍCH KOMUNIKACÍ VČETNĚ PROPUSTKŮ
SO 135 ODPOČÍVKA BRUSNICE V KM 131,0**

Měřítko:
1:1000/100

Podst. formát:
12xA4

Název přílohy:
PODÉLNÝ PROFIL

Číslo přílohy:
3

DOKUMENT LZE UŽÍVAT POUZE V SANKCÍ PŘÍSLUŠNÉ SOUDOVÝ OŘÁD. ŽÁDNÉ JINÉ ČÁSTI NEMŮŽE BYT QLE ZAKLÁNĚ L 15110008 NA KOPÍROVÁNÍ NEBO JINÝM ZPŮSOBEM ROZŠÍŘOVÁNÁ. BEZ SOUHLASU SUDOP PRAHA A