
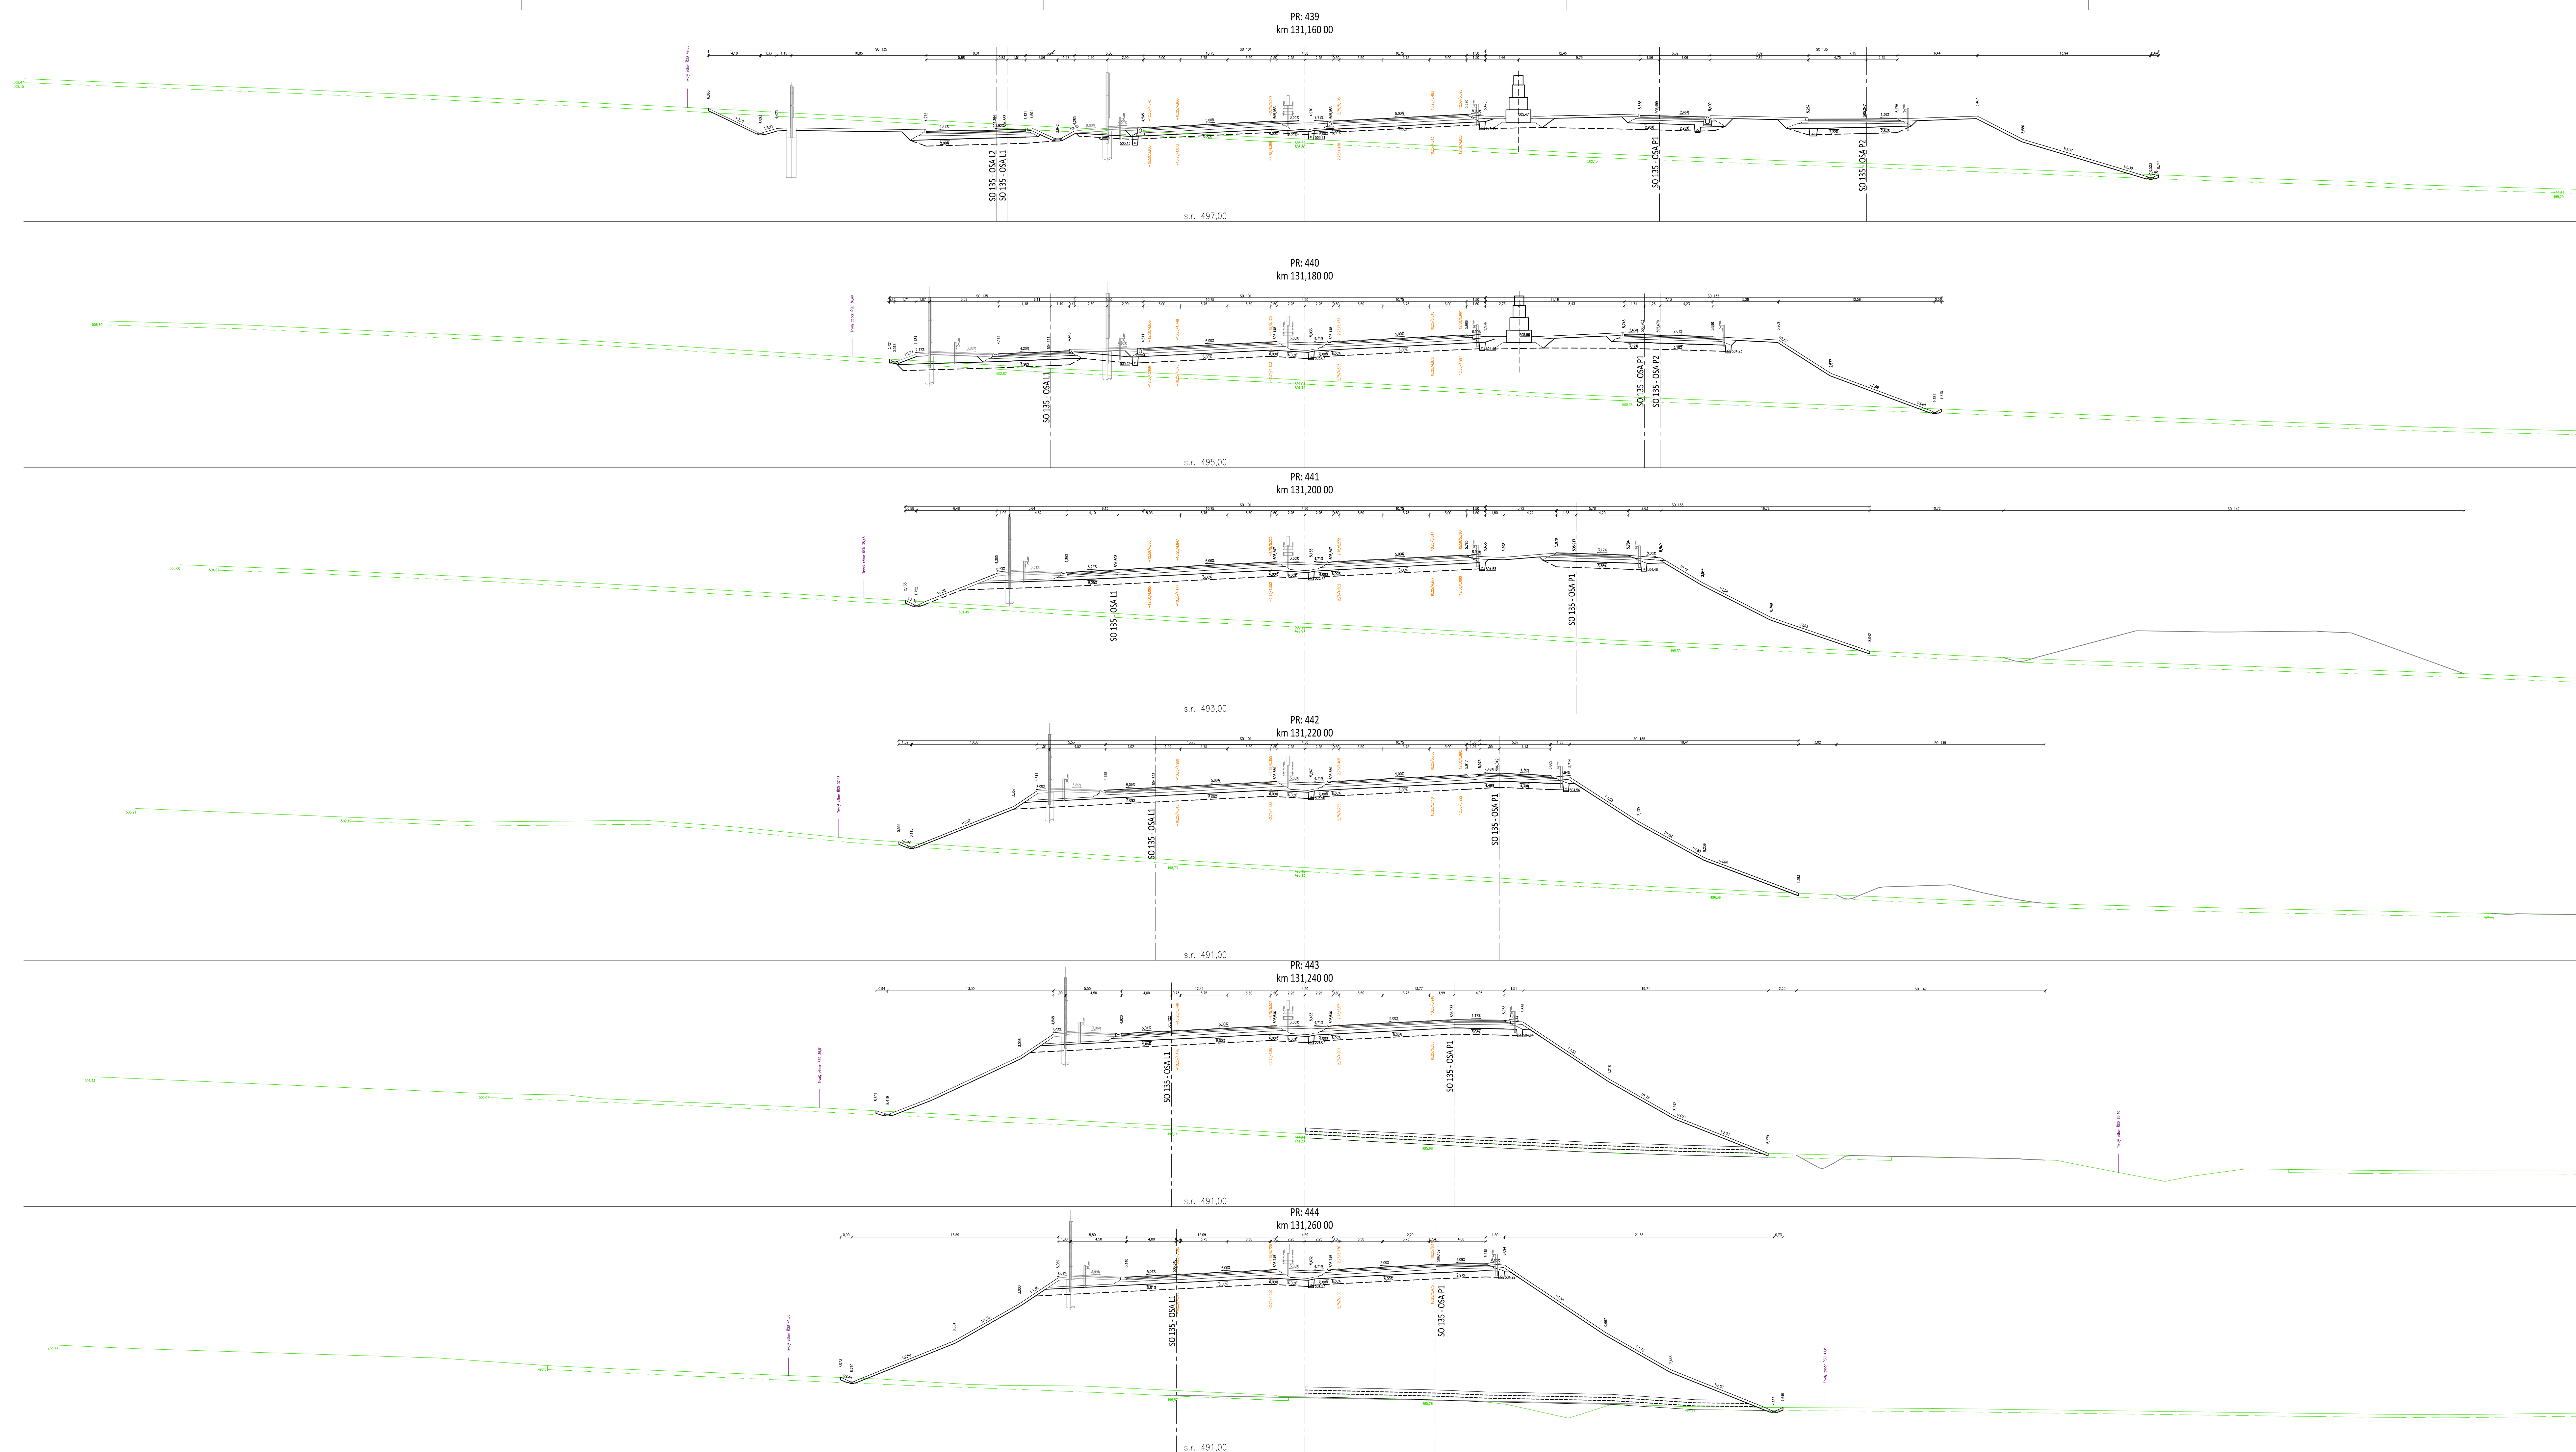


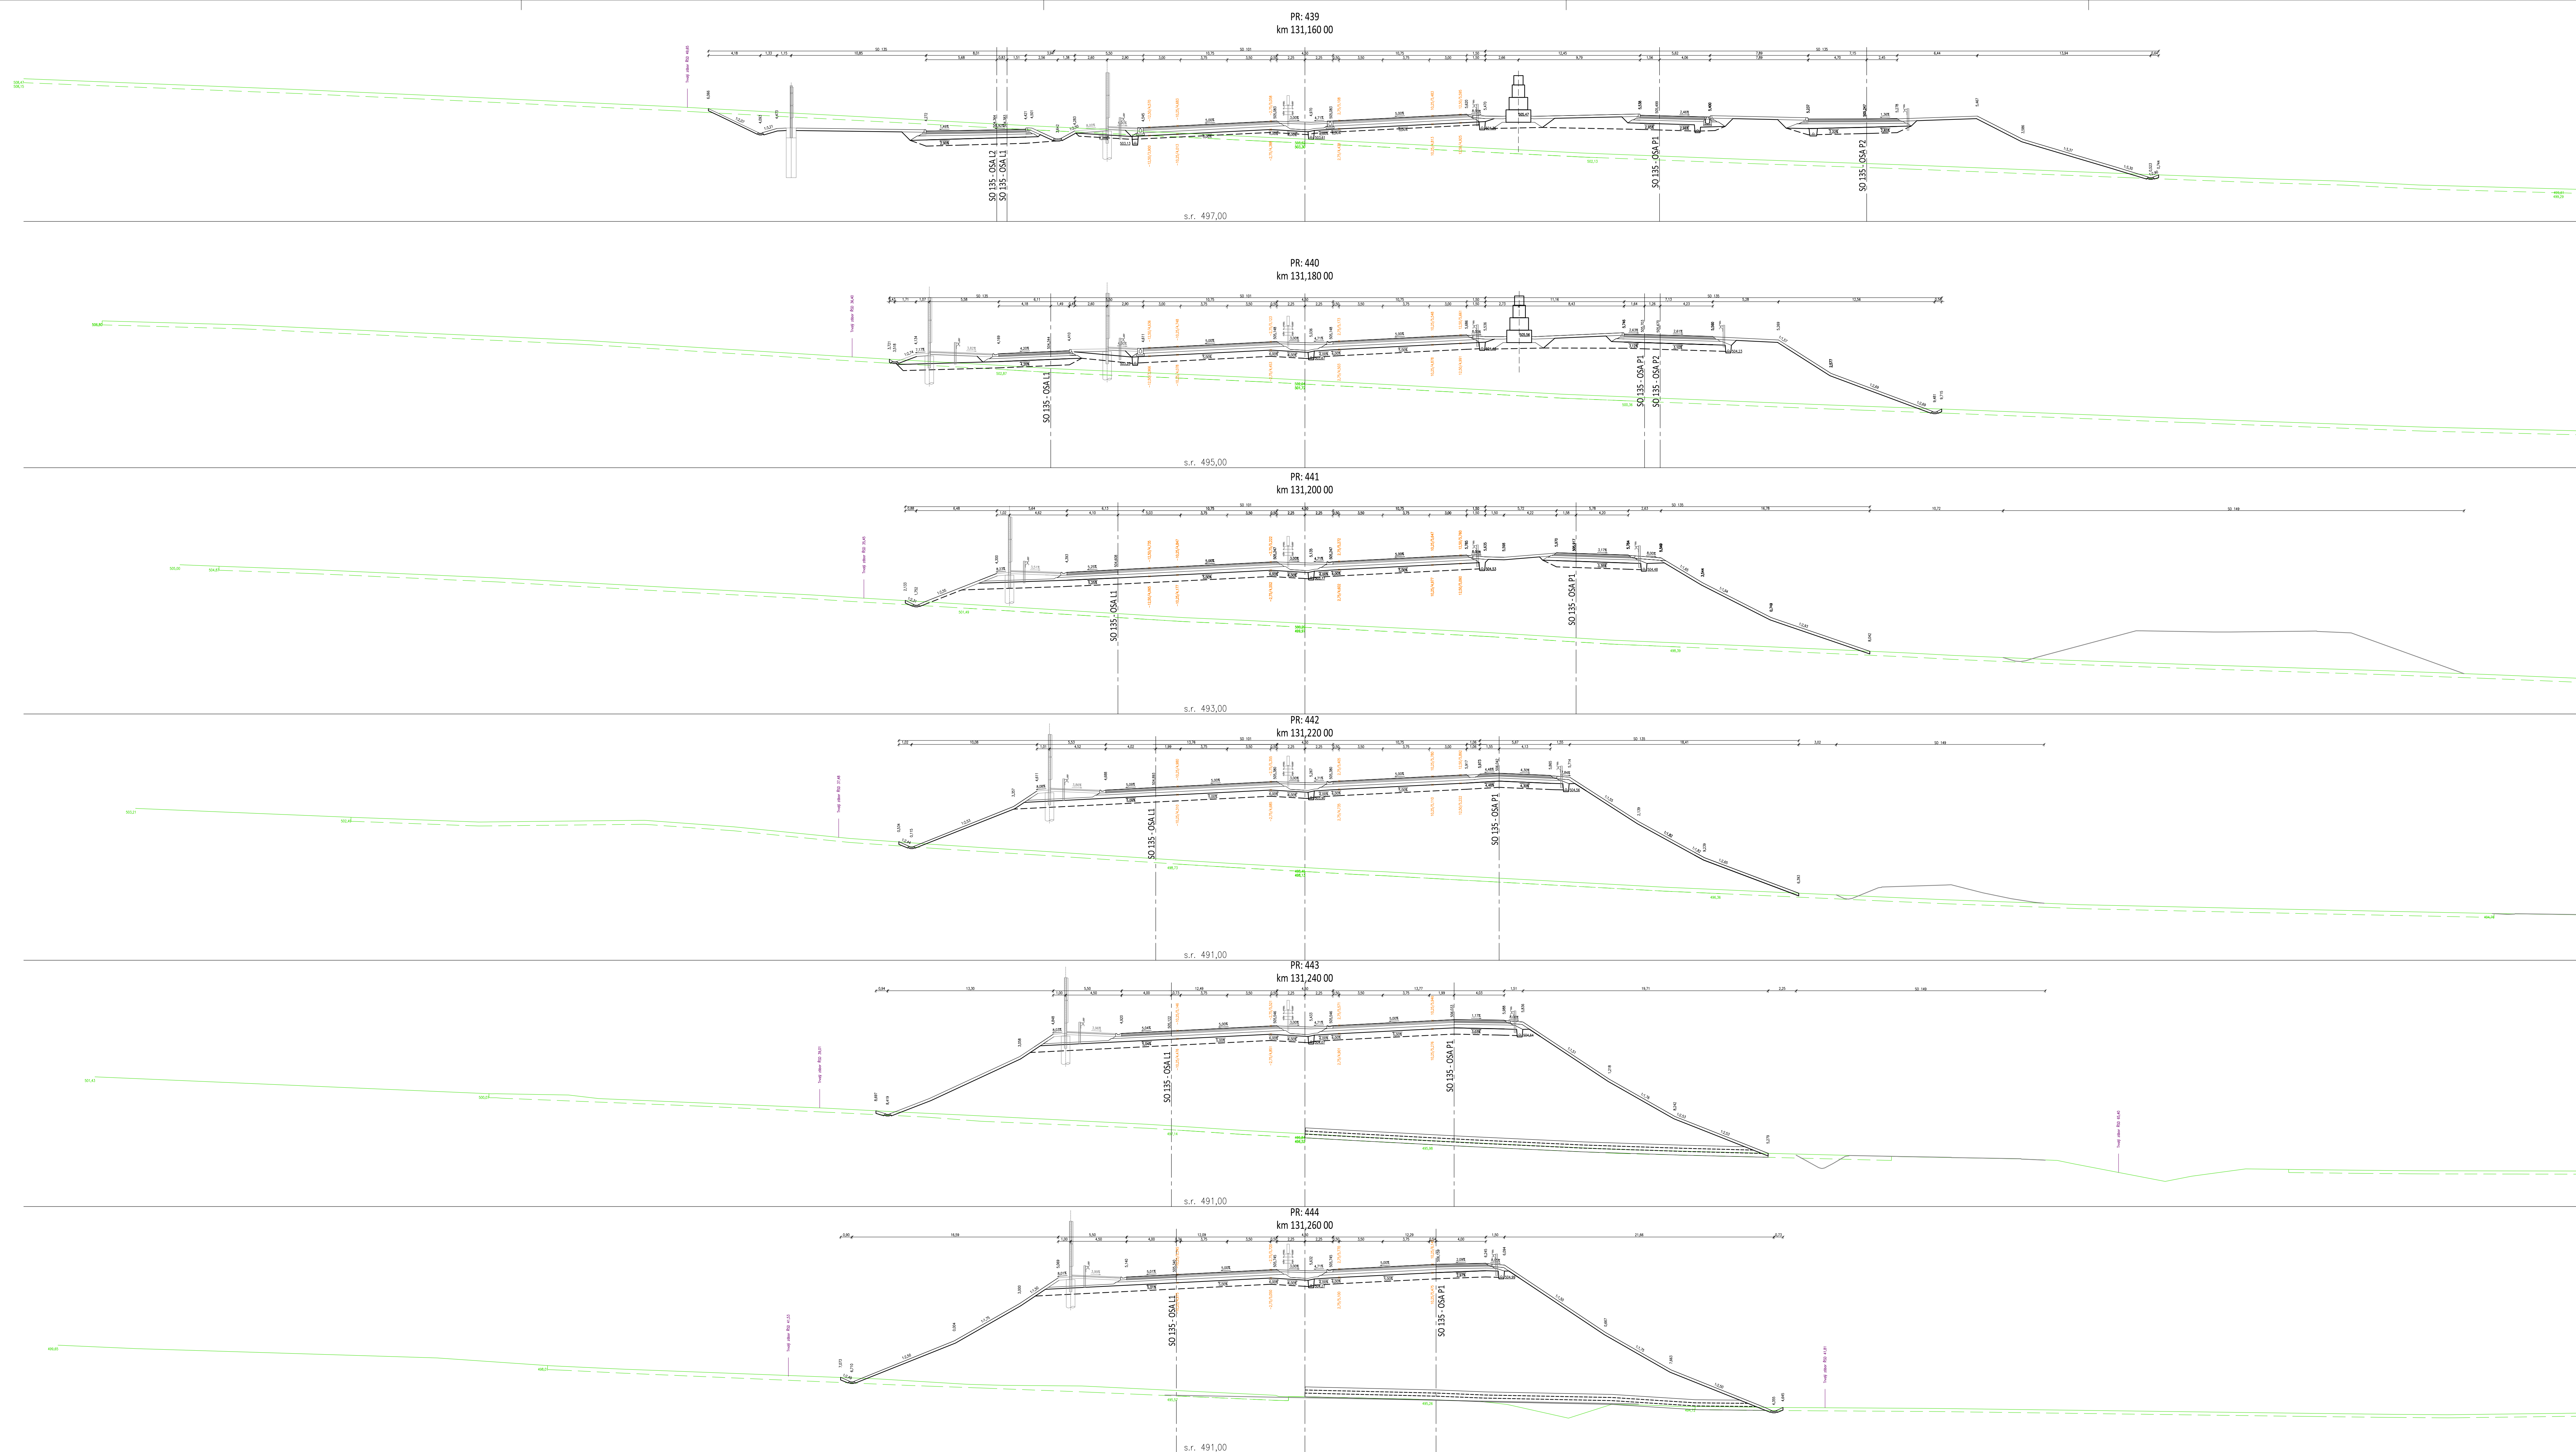

SOUŘADNICOVÝ SYSTÉM S-JTS

Reditelství sílnic a dálnic s. p.
Na Pankraci 546/58, 140 00 Praha 4
Stavbu zajišťuje Závod Praha

SUDOP PRAHA a.s. Hlavní inženýr projektu: Ing. Roman Petřík	Ošarská 1a, 130 80 Praha 3 telefon: +420 267 094 111
--	---

Společnost: SUDOP	SUDOP PRAHA a.s. Gillembertova 130, 100 00 Praha 2	Vytvořitel/ firma: ...	Asistent vedoucího týmu: ING. PAVEL MICHL
---	---	---------------------------	--

projektová, průzkumná a konzultační společnost
PUDIS a.s., Podbabská 1014/20, 160 00 Praha 6

ING. ZDENKA BOLEHOVSKÁ	ING. MICHAL TUREK	PETR KOTLABA	ING. MICHAL TUREK
Místní odvol:			Státní zastupitel:

Case:	Date:
	11/202

Měřítko:		1:200	Model formátu:	22xA
Číslo přílohy:				

5.2