
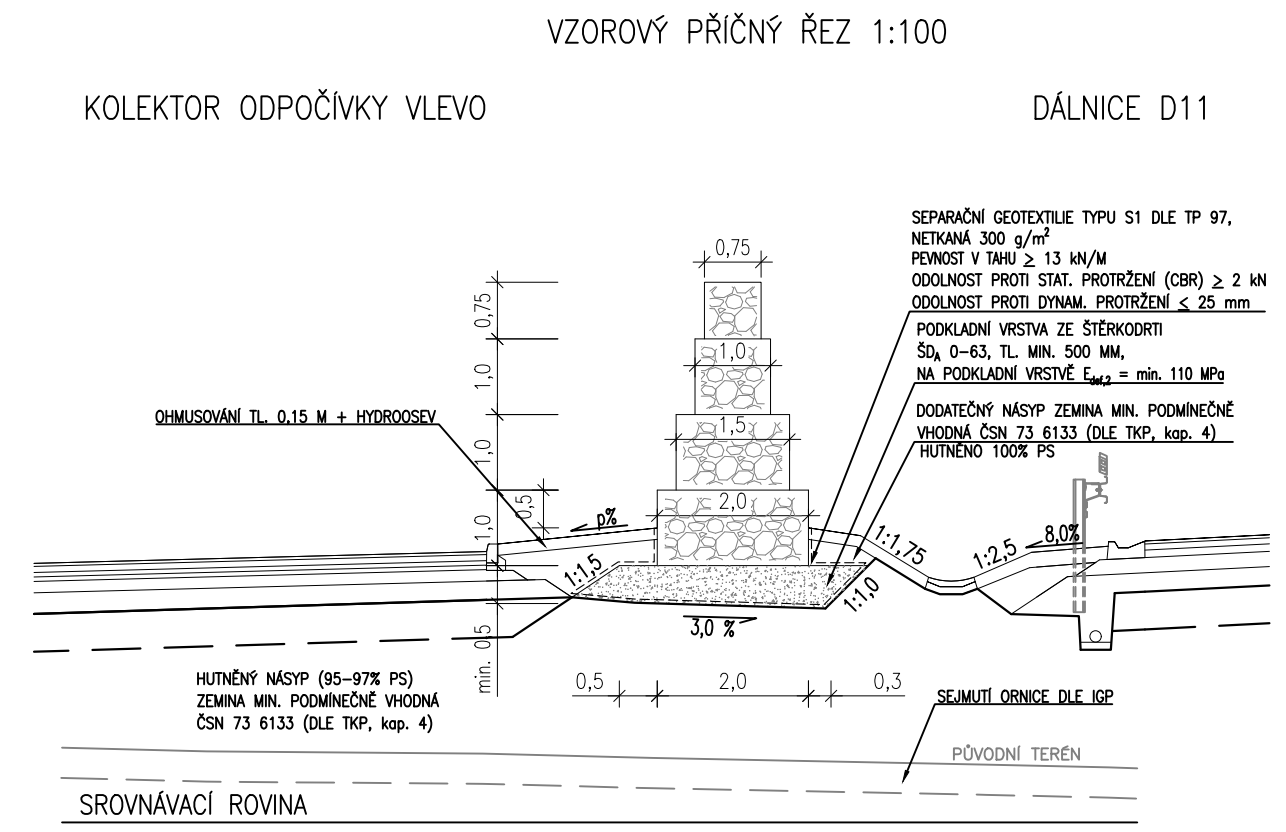
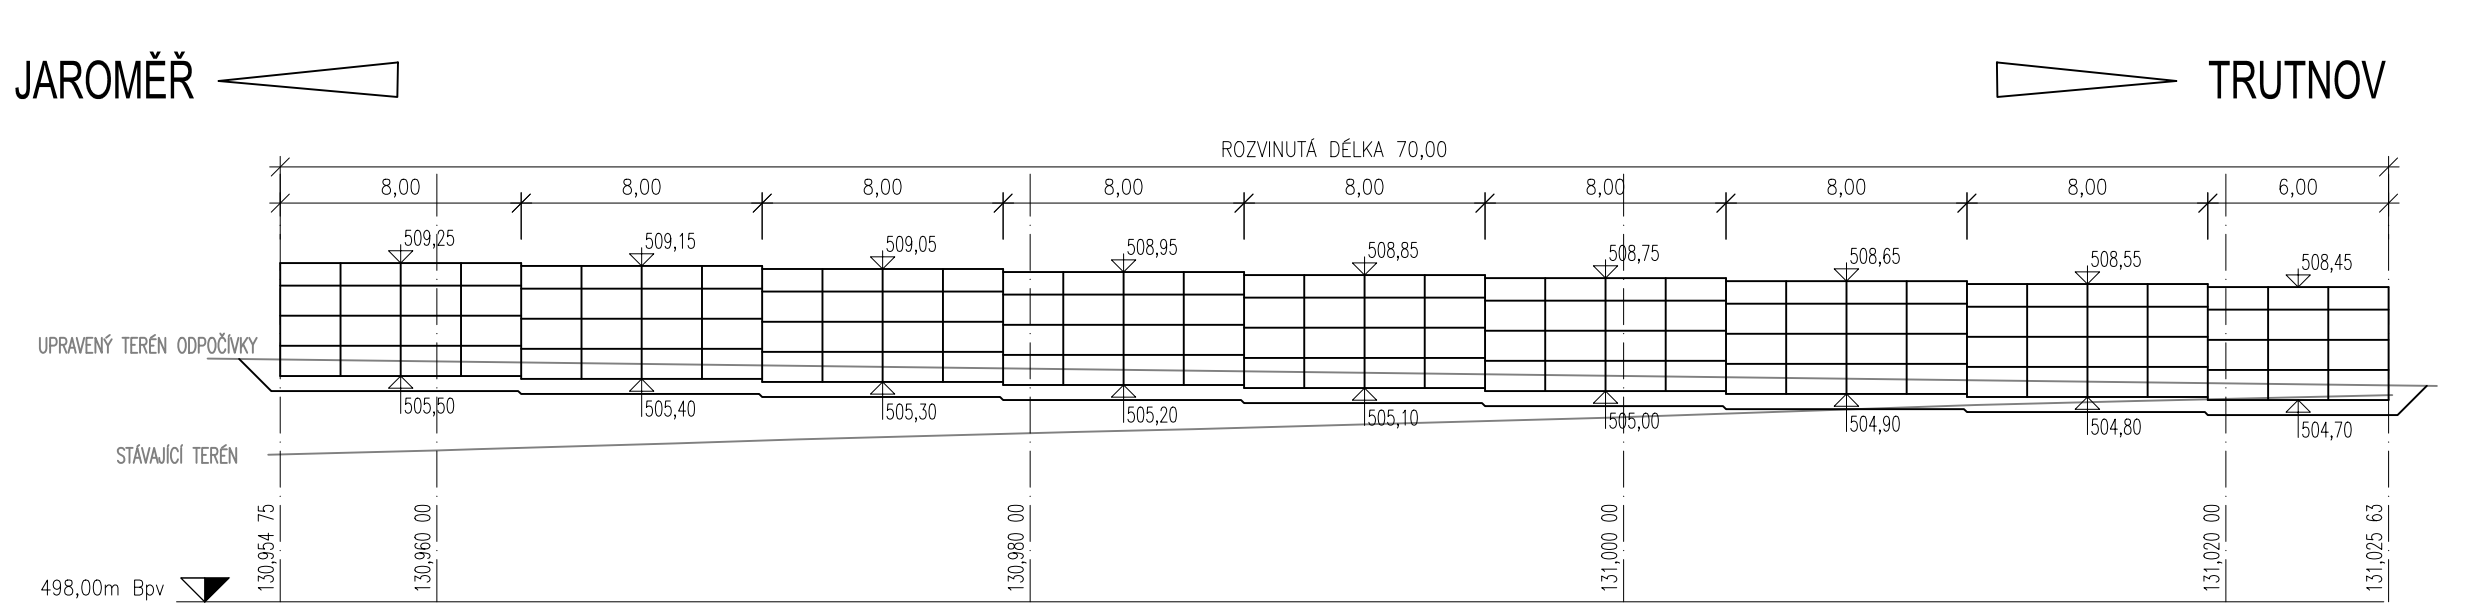
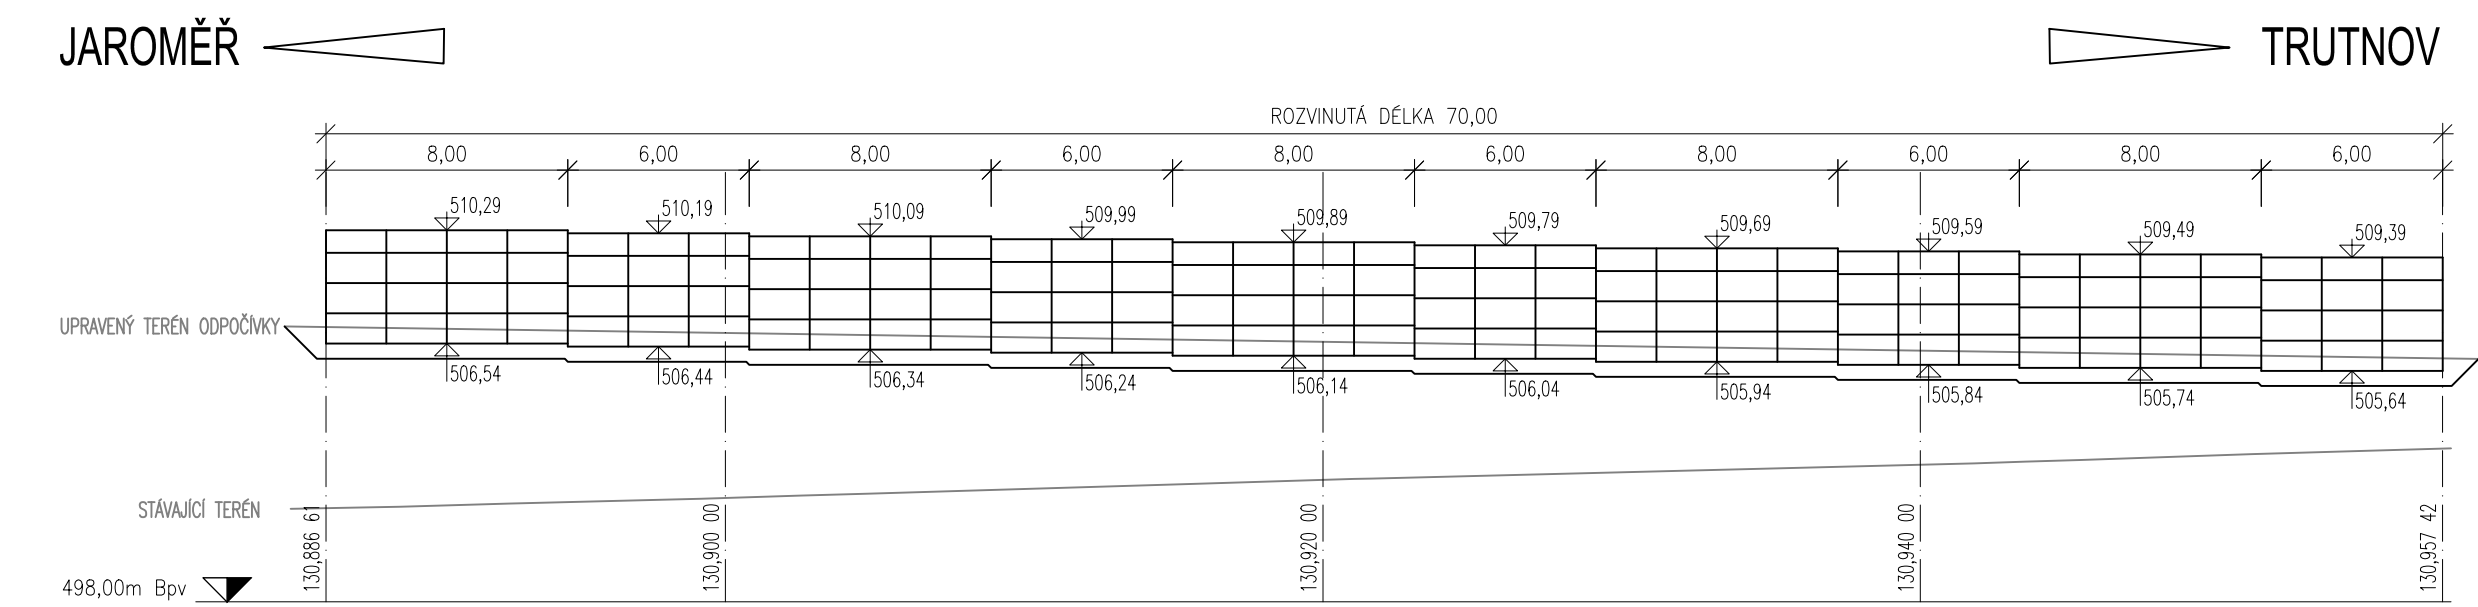
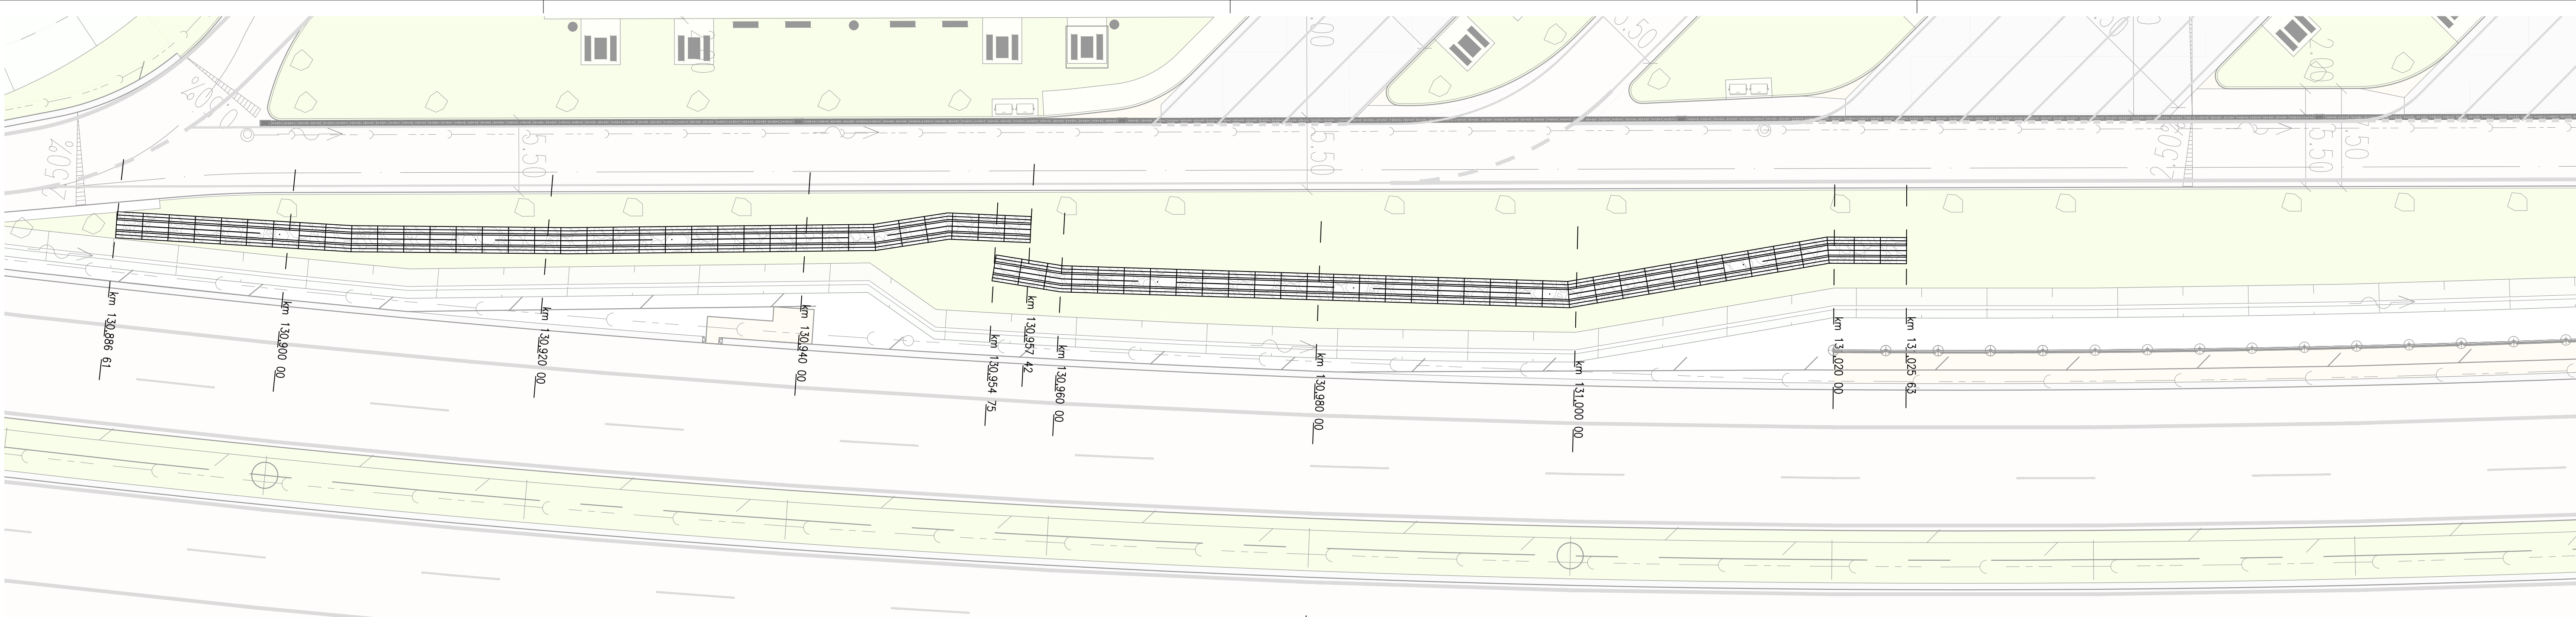


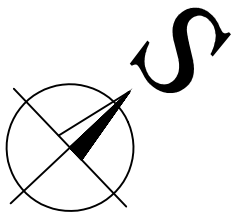

KONSTRUKČNÍ ZASADY:

OBVOD (RUB, LIC, BOČNÍ STĚNY) KAŽDÉHO KÓŠE MUSÍ BÝT VYSKLÁDÁN VÝDÝ RUČNĚ (DOPLNĚNÍ MINIMÁLNÍ MEZEROVITOSTI, VÁZBA NA SUCHO) V MIN. TL. 250 MM (MATERIÁL MŮŽE BÝT DO KÓŠE DOPRAVEN POMOCÍ MECHANIZACE), VNITŘNÍ PROSTOR GABIONOVÉHO KÓŠE SMÍ BÝT PLNĚN A HUTNĚN STROJNĚ PO VRSŤVÁCH. VÝPLŇ GABIONŮ BUDE V TL. MIN. 250 MM SKLÁDANA VE SMĚRU VIDELNÝCH PLOCH.

DNO KAŽDÉHO KÓŠE MUSÍ BÝT PŘED ZAČÁTKEM PLNĚNÍ OPATŘENO OCHRANNOU VRSTVOU KAMENIVA O MIN. VELIKOSTI 16 MM TAK, ABY KÁMEN PŘI PLNĚNÍ NEPŘÍŠEL DO STYKU SE DNEM KÓŠE. KÁMENY NESMĚJÍ BÝT POKLÁDÁNY NA STOJATO, ALE VŽDY VĚŠÍ PLOCHOU VODODROVNĚ SE ZACHOVÁNÍM POŽADAVKŮ NA ROVNATOST LÍCE ZDÍ. POSTUPUJE SE PO 30 CM VRSŤVÁCH U 1 M VÝŠKYCH DRÁTKAMENNÝCH KONSTRUKCÍ A 25 CM VRSŤVÁCH PRO 0,5 M VÝŠKÉ KÓŠE. U KONSTRUKCÍ, KDE JE INSTALOVÁNA VÍČ NEZ JEDNA ŘADA, JE POTŘEBA PŘESTAT KAŽDOU ŘADU VRSTVOU KAMENE SILNOU PŘEBLÍŽNĚ 25 AŽ 40 MM TAK, ABY BYLO OMEZENO OČEKÁVANÉ SEDNUTÍ KAMENNÉ VÝPLNĚ. VŠECHNY VYSKYTLIVÉ SE OSTRÉ KONCE NEBO HRANY MUSÍ BÝT NATOČENY SMĚREM DO KONSTRUKCE.

BĚHEM POSTUPU PLNĚNÍ GABIONŮ KAMENEM SE NAVÁZEM PROTIHLÉ STĚNY STABILIZUJÍ VÝZTUŽNÍMÍ DRÁTY (ZTUŽLIVCI TÁHLA, ZTUŽLIVCI SMÝČKY) TAK, ABY NEDODCHÁZELO K BOULENÍ LÍCE GABIONU TLAKEM ULOŽENÉHO KAMENE.

PO NÁPLNĚNÍ KAMENEM AŽ PO HORNÍ OKRAJ SE GABION/MATRACE UZAVÍRĚ DRÁTĚNÝM VÍKEM, KTERÉ SE SPOJÍ S KOLMÝMI STĚNAMI VÁZACÍM DRÁTEM, RESP. SPÍRALOU.

MATERIÁLY, KONSTRUKČNÍ ZASADY, PROVÁDĚNÍ A PRŮKAZNÍ ZKOUŠKY POUŽITÝCH MATERIÁLŮ MUSÍ BÝT V SOULADU S TECHNIKÝMI A KVALITATIVNÍMI PODMÍNKAMI TYP – KAPITOLA 30. SPECIÁLNÍ ZEZNÍ KONSTRUKCE*, POŽADOVANÁ ŽIVOTNOST KONSTRUKCE JE PŘEDPISÁNA MIN. 100 LET S OCHRANOU NA STUPEŇ KORÓZNÍ AGRESIVNÍ PROSTŘEDÍ C4.

SO 135

D.1.1

VÝŠKOVÝ SYSTÉM BpV

SOUŘADNICOVÝ SYSTÉM S-JTSK

Číslo změny:	Obsah změny:	Datum změny:
01	-	-
02	-	-
03	-	-

Objednatel: Ředitelství silnic a dálnic s. p.
Na Pankráci 546/56, 140 00 Praha 4

Stavbu zajišťuje Závod Praha
Na Pankráci 546/56, 140 00 Praha 4

Zhotovitel: Společnosti ve sdružení SG_Velké projekty_BIM 2020 zastoupené

SUDOP PRAHA a.s.
Hlavní inženýr projektu: Ing. Roman Petřík

Olšanská 1a, 130 80 Praha 3
telefon: +420 267 094 111



Správce: SUDOP PRAHA a.s.
Olšanská 1a, 130 80 Praha 3
tel.: +420 267 094 111
e-mail: praha@sudop.cz

Vedoucí týmu: ING. ROMAN PETŘÍK

Asistent vedoucího týmu: ING. PAVEL MICHL
Specialista profese: -

Zpracovatel: PUDIS projektová, průzkumná a konzultační společnost
PUDIS a.s., Podbabská 1014/20, 160 00 Praha 6
tel.: +420 267 004 111, www.pudis.cz, info@pudis.cz

Vedoucí střediska:	Odpovědný projektant SO, IO, PS:	Vypracoval:	Kontroloval:
ING. ZDENKA BOLEHOVSKÁ	ING. MICHAL TUREK	PETR KOTLABA	ING. MICHAL TUREK

Název akce:	Číslo smlouvy:
D11 1108 Jaroměř - Trutnov VD-ZDS + TP + AD	22-014.250
Část:	Projektový stupeň:
D.1.1 OBJEKTY POZEMNÍCH KOMUNIKACÍ VČETNĚ PROPUSTKŮ SO 135 ODPOČÍVKA BRUSNICE V KM 131,0	VD-ZDS
Název přílohy:	Datum:
GABIONOVÁ ZEĎ - VLEVO	11/2024
	Číslo částí:
	D.1.1
	Měřítko:
	1:100, 1:250
	Počet formátů:
	7x4
	Číslo přílohy:
	6.2