VZOROVÝ PŘÍČNÝ ŘEZ 1:100

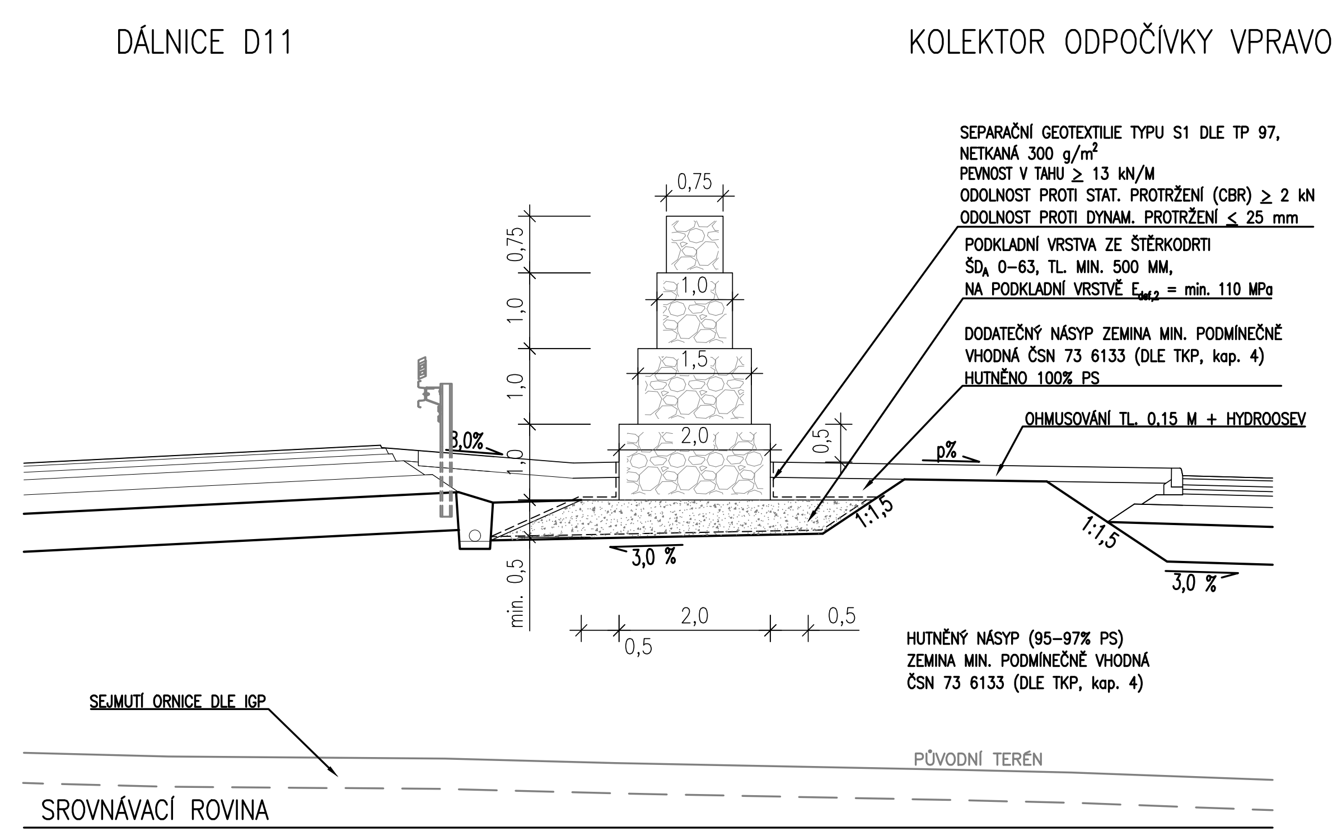
DÁLNICE D11
KOLEKTOR ODPOČÍVKY VPRAVO
SEPARAČNÍ GEOTEXTILIE TYPU S1 DLE TP 97,
NETKANÁ 300 g/m²
PEVNOST V TAHU ≥ 13 kN/M
ODOLNOST PROTI STAT. PROTRŽENÍ (CBR) ≥ 2 kN
ODOLNOST PROTI DYNAM. PROTRŽENÍ ≤ 25 mm
PODKLADNÍ VRSTVA ZE ŠTĚRKODRTI
ŠDA 0–63, TL. MIN. 500 MM,
NA PODKLADNÍ VRSTVĚ Edef,2 = min. 110 MPa
DODATEČNÝ NÁSYP ZEMINA MIN. PODMÍNEČNĚ
VHODNÁ ČSN 73 6133 (DLE TKP, kap. 4)
HUTNĚNO 100% PS
OHMUSOVÁNÍ TL. 0,15 M + HYDROOSEV
HUTNĚNÝ NÁSYP (95–97% PS)
ZEMINA MIN. PODMÍNEČNĚ VHODNÁ
ČSN 73 6133 (DLE TKP, kap. 4)
0,75
1,0
1,5
2,0
0,75
1,0
1,0
1,0
min. 0,5
0,5
0,5
2,0
0,5
3,0%
3,0 %
3,0 %
p%
1:1,5
1:1,5
SEJMUTÍ ORNICE DLE IGP
PŮVODNÍ TERÉN
SROVNÁVACÍ ROVINA

KONSTRUKČNÍ ZÁSADY:

OBVOD (RUB, LÍC, BOČNÍ STĚNY) KAŽDÉHO KOŠE MUSÍ BÝT VYSKLÁDÁN VŽDY RUČNĚ (DOCÍLENÍ MINIMÁLNÍ MEZEROVITOSTI, VAZBA NA SUCHO) V MIN. TL. 250 MM (MATERIÁL MŮŽE BÝT DO KOŠE DOPRAVEN POMOCÍ MECHANIZACE), VNITŘNÍ PROSTOR GABIONOVÉHO KOŠE SMÍ BÝT PLNĚN A HUTNĚN STROJNĚ PO VRSTVÁCH. VÝPLŇ GABIONŮ BUDE V TL. MIN. 250 MM SKLÁDÁNA VE SMĚRU VIDITELNÝCH PLOCH.

DNO KAŽDÉHO KOŠE MUSÍ BÝT PŘED ZAČÁTKEM PLNĚNÍ OPATŘENO OCHRANNOU VRSTVOU KAMENIVA O MIN. VELIKOSTI 16 MM TAK, ABY KÁMEN PŘI PLNĚNÍ NEPŘIŠEL DO STYKU SE DNEM KOŠE. KAMENY NESMĚJÍ BÝT POKLÁDÁNY NA STOJATO, ALE VŽDY VĚTŠÍ PLOCHOU VODOROVNĚ SE ZACHOVÁNÍM POŽADAVKU NA ROVINATOST LÍCE ZDI. POSTUPUJE SE PO 30 CM VRSTVÁCH U 1 M VYSOKÝCH DRÁTOKAMENNÝCH KONSTRUKCÍ A 25 CM VRSTVÁCH PRO 0,5 M VYSOKÉ KOŠE. U KONSTRUKCÍ, KDE JE INSTALOVÁNA VÍC NEŽ JEDNA ŘADA, JE POTŘEBA PŘESYPAT KAŽDOU ŘADU VRSTVOU KAMENE SILNOU PŘIBLIŽNĚ 25 AŽ 40 MM TAK, ABY BYLO OMEZENO OČEKÁVANÉ SEDNUTÍ KAMENNÉ VÝPLNĚ. VŠECHNY VYSKYTUJÍCÍ SE OSTRÉ KONCE NEBO HRANY MUSEJÍ BÝT NATOČENY SMĚREM DO KONSTRUKCE.

BĚHEM POSTUPU PLNĚNÍ GABIONŮ KAMENEM SE NAVZÁJEM PROTILEHLÉ STĚNY STABILIZUJÍ VÝZTUŽNÝMI DRÁTY (ZTUŽUJÍCÍ TÁHLA, ZTUŽUJÍCÍ SMYČKY) TAK, ABY NEDOCHÁZELO K BOULENÍ LÍCE GABIONU TLAKEM ULOŽENÉHO KAMENE.

PO NAPLNĚNÍ KAMENEM AŽ PO HORNÍ OKRAJ SE GABION/MATRACE UZAVŘE DRÁTĚNÝM VÍKEM, KTERÉ SE SPOJÍ S KOLMÝMI STĚNAMI VÁZACÍM DRÁTEM, RESP. SPIRÁLOU.

MATERIÁLY, KONSTRUKČNÍ ZÁSADY, PROVÁDĚNÍ A PRŮKAZNÍ ZKOUŠKY POUŽITÝCH MATERIÁLŮ MUSÍ BÝT V SOULADU S TECHNICKÝMI A KVALITATIVNÍMI PODMÍNKAMI TKP – „KAPITOLA 30. SPECIÁLNÍ ZEMNÍ KONSTRUKCE". POŽADOVANÁ ŽIVOTNOST KONSTRUKCE JE PŘEDEPSÁNA MIN. 100 LET S OCHRANOU NA STUPEŇ KOROZNÍ AGRESIVITY PROSTŘEDÍ C4.

SO 135
D.1.1

VÝŠKOVÝ SYSTÉM Bpv
SOUŘADNICOVÝ SYSTÉM S-JTSK

Číslo změny:	*Obsah změny:*	*Datum změny:*
01	-	-
02	-	-
03	-	-

Objednatel:
ŘEDITELSTVÍ SILNIC A DÁLNIC
Ředitelství silnic a dálnic s. p.
Na Pankráci 546/56, 140 00 Praha 4

Stavbu zajišťuje Závod Praha
Na Pankráci 546/56, 140 00 Praha 4

Zhotovitel: Společníci ve sdružení
SG_Velké projekty_BIM 2020
zastoupené
SUDOP PRAHA a.s.
Hlavní inženýr projektu: Ing. Roman Petřík
Olšanská 1a, 130 80 Praha 3
telefon: +420 267 094 111

SUDOP PRAHA | PUDIS | SUDOP EU | DOPRAVOPROJEKT BRNO | DOPRAVOPROJEKT

Správce:
SUDOP PRAHA
SUDOP PRAHA a.s.
Olšanská 1a, 130 80 Praha 3
tel.: +420 267 094 111
e-mail: praha@sudop.cz

Vedoucí týmu: ING. ROMAN PETŘÍK
Asistent vedoucího týmu: ING. PAVEL MICHL
Specialista profese: -

Zpracovatel části:
PUDIS
projektová, průzkumná a konzultační společnost
PUDIS a.s., Podbabská 1014/20, 160 00 Praha 6
tel.: +420 267 004 111, www.pudis.cz, info@pudis.cz

Vedoucí střediska:	*Odpovědný projektant SO, IO, PS:*	*Vypracoval:*	*Kontroloval:*
ING. ZDEŇKA BOLEHOVSKÁ	ING. MICHAL TUREK	PETR KOTLABA	ING. MICHAL TUREK

Název akce:
D11 1108 Jaroměř - Trutnov VD-ZDS + TP + AD

Číslo smlouvy: 22-014.250
Projektový stupeň: VD-ZDS

Část:
D.1.1 OBJEKTY POZEMNÍCH KOMUNIKACÍ VČETNĚ PROPUSTKŮ
SO 135 ODPOČÍVKA BRUSNICE V KM 131,0

Datum: 11/2024
Číslo části: D.1.1

Název přílohy:
GABIONOVÁ ZEĎ - VPRAVO

Měřítko: 1:100, 1:250
Počet formátů: 7xA4
Číslo přílohy: **6.1**

DOKUMENT LZE UŽÍVAT POUZE VE SMYSLU PŘÍSLUŠNÉ SMLOUVY O DÍLO. ŽÁDNÁ JEHO ČÁST NEMŮŽE BÝT DLE ZÁKONA č.121/2000 Sb. KOPÍROVÁNA NEBO JINÝM ZPŮSOBEM ROZŠIŘOVÁNA BEZ SOUHLASU SUDOP PRAHA a.s.