


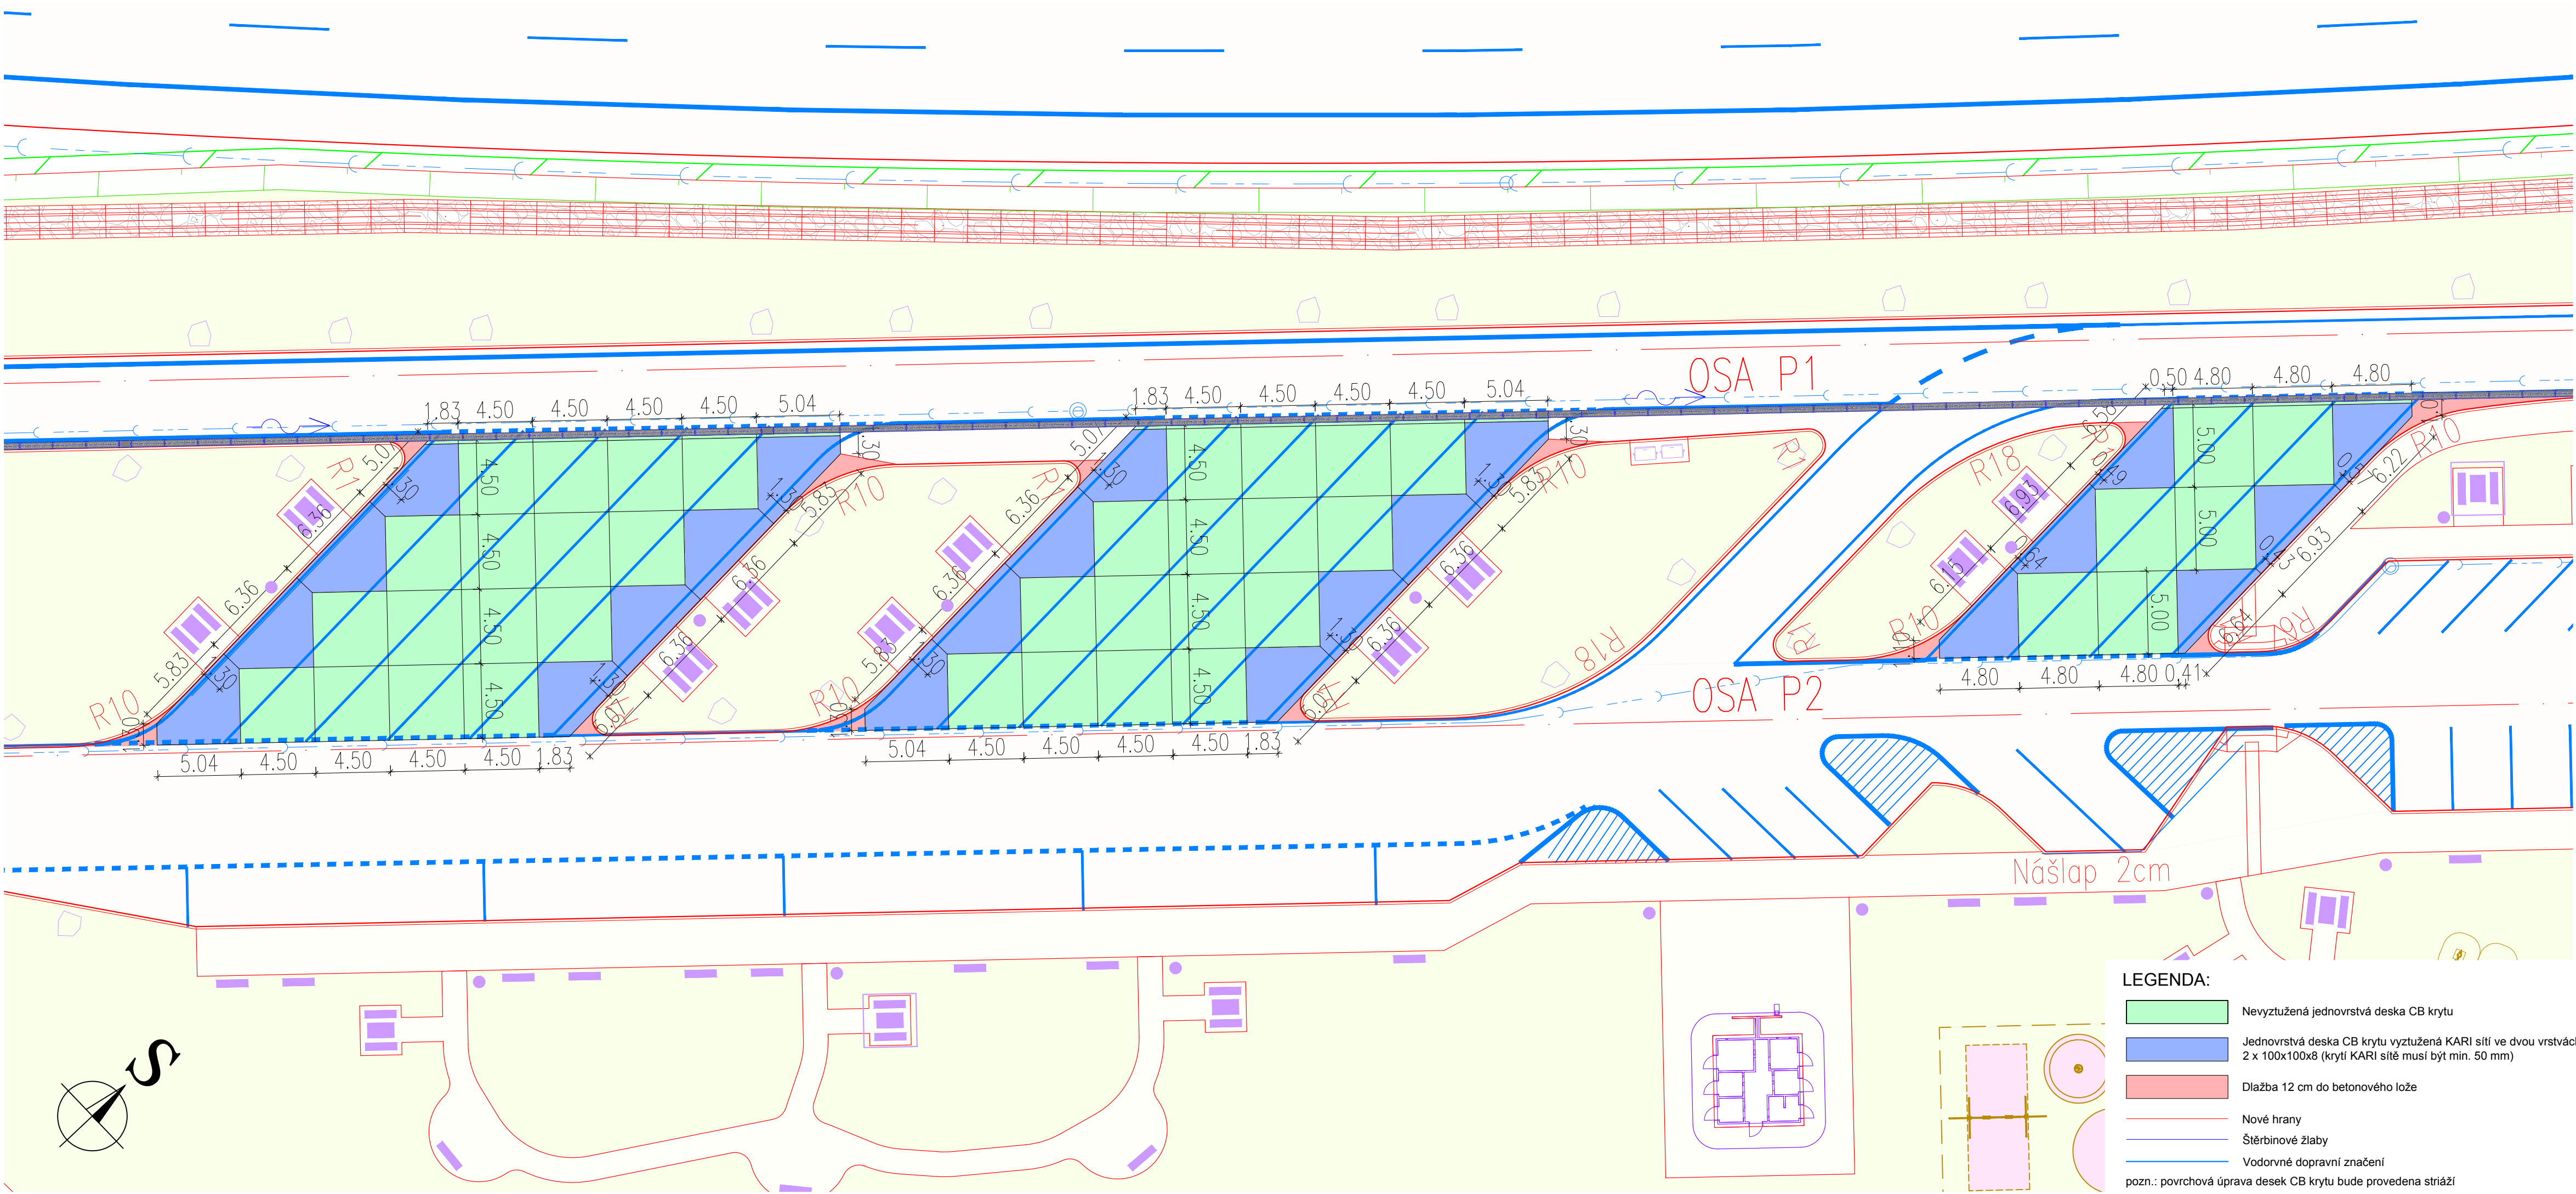

LEGENDA:

- Nevyužitá jednovrstvá deska CB krytu
- Jednovrstvá deska CB krytu vyztužená KARI sítí ve dvou vrstvách 2 x 100x100x8 (krytí KARI síť musí být min. 50 mm)
- Dlažba 12 cm do betonového lože
- Nové hrany
- Štěrbinové žlaby
- Vodorovné dopravní značení

pozn.: povrchová úprava desek CB krytu bude provedena striáží

SO 135

D.1.1

VÝŠKOVÝ SYSTÉM Bpv SOUŘADNICOVÝ SYSTÉM S-JTSK

Číslo změny:	Obsah změny:	Datum změny:
01	-	-
02	-	-
03	-	-

Objednatel:

Ředitelství silnic a dálnic s. p.
Na Pankráci 546/56, 140 00 Praha 4
Stavbu zajišťuje Závod Praha
Na Pankráci 546/56, 140 00 Praha 4

Zhotovitel: Společníci ve sdružení SG_Velké projekty_BIM 2020
zastoupené

SUDOP PRAHA a.s.
Hlavní inženýr projektu: Ing. Roman Petřík

Olišanská 1a, 130 80 Praha 3
telefon: +420 267 094 111



Správce:

SUDOP PRAHA a.s.
Olišanská 1a, 130 80 Praha 3
tel.: +420 267 094 111
e-mail: praha@sudop.cz

Vedoucí týmu:
ING. ROMAN PETŘÍK

Asistent vedoucího týmu:
ING. PAVEL MICHL
Specialista profese:
-

Zpracovatel částí:

projektová, průzkumná a konzultační společnost
PUDIS a.s., Podbabská 1014/20, 160 00 Praha 6
tel.: +420 267 004 111, www.pudis.cz, info@pudis.cz

Vedoucí střediska:	Odpovědný projektant SO, IO, PS:	Vypracoval:	Kontroloval:
ING. ZDENKA BOLEHOVSKÁ	ING. MICHAL TUREK	PETR KOTLABA	ING. MICHAL TUREK

Název akce:		Číslo smlouvy:	
D11 1108 Jaroměř - Trutnov VD-ZDS + TP + AD		22-014.250	
Část:		Projektový stupeň:	
D.1.1 OBJEKTY POZEMNÍCH KOMUNIKACÍ VČETNĚ PROPUSTKŮ SO 135 ODPOČÍVKA BRUSNICE V KM 131,0		VD-ZDS	
Název přílohy:		Datum:	
SPÁROŘEZ - VPRAVO		11/2024	
		Číslo části:	
		D.1.1	
		Měřítko:	Počet formátů:
		1:250	4xA4
		Číslo přílohy:	
		7.1	