


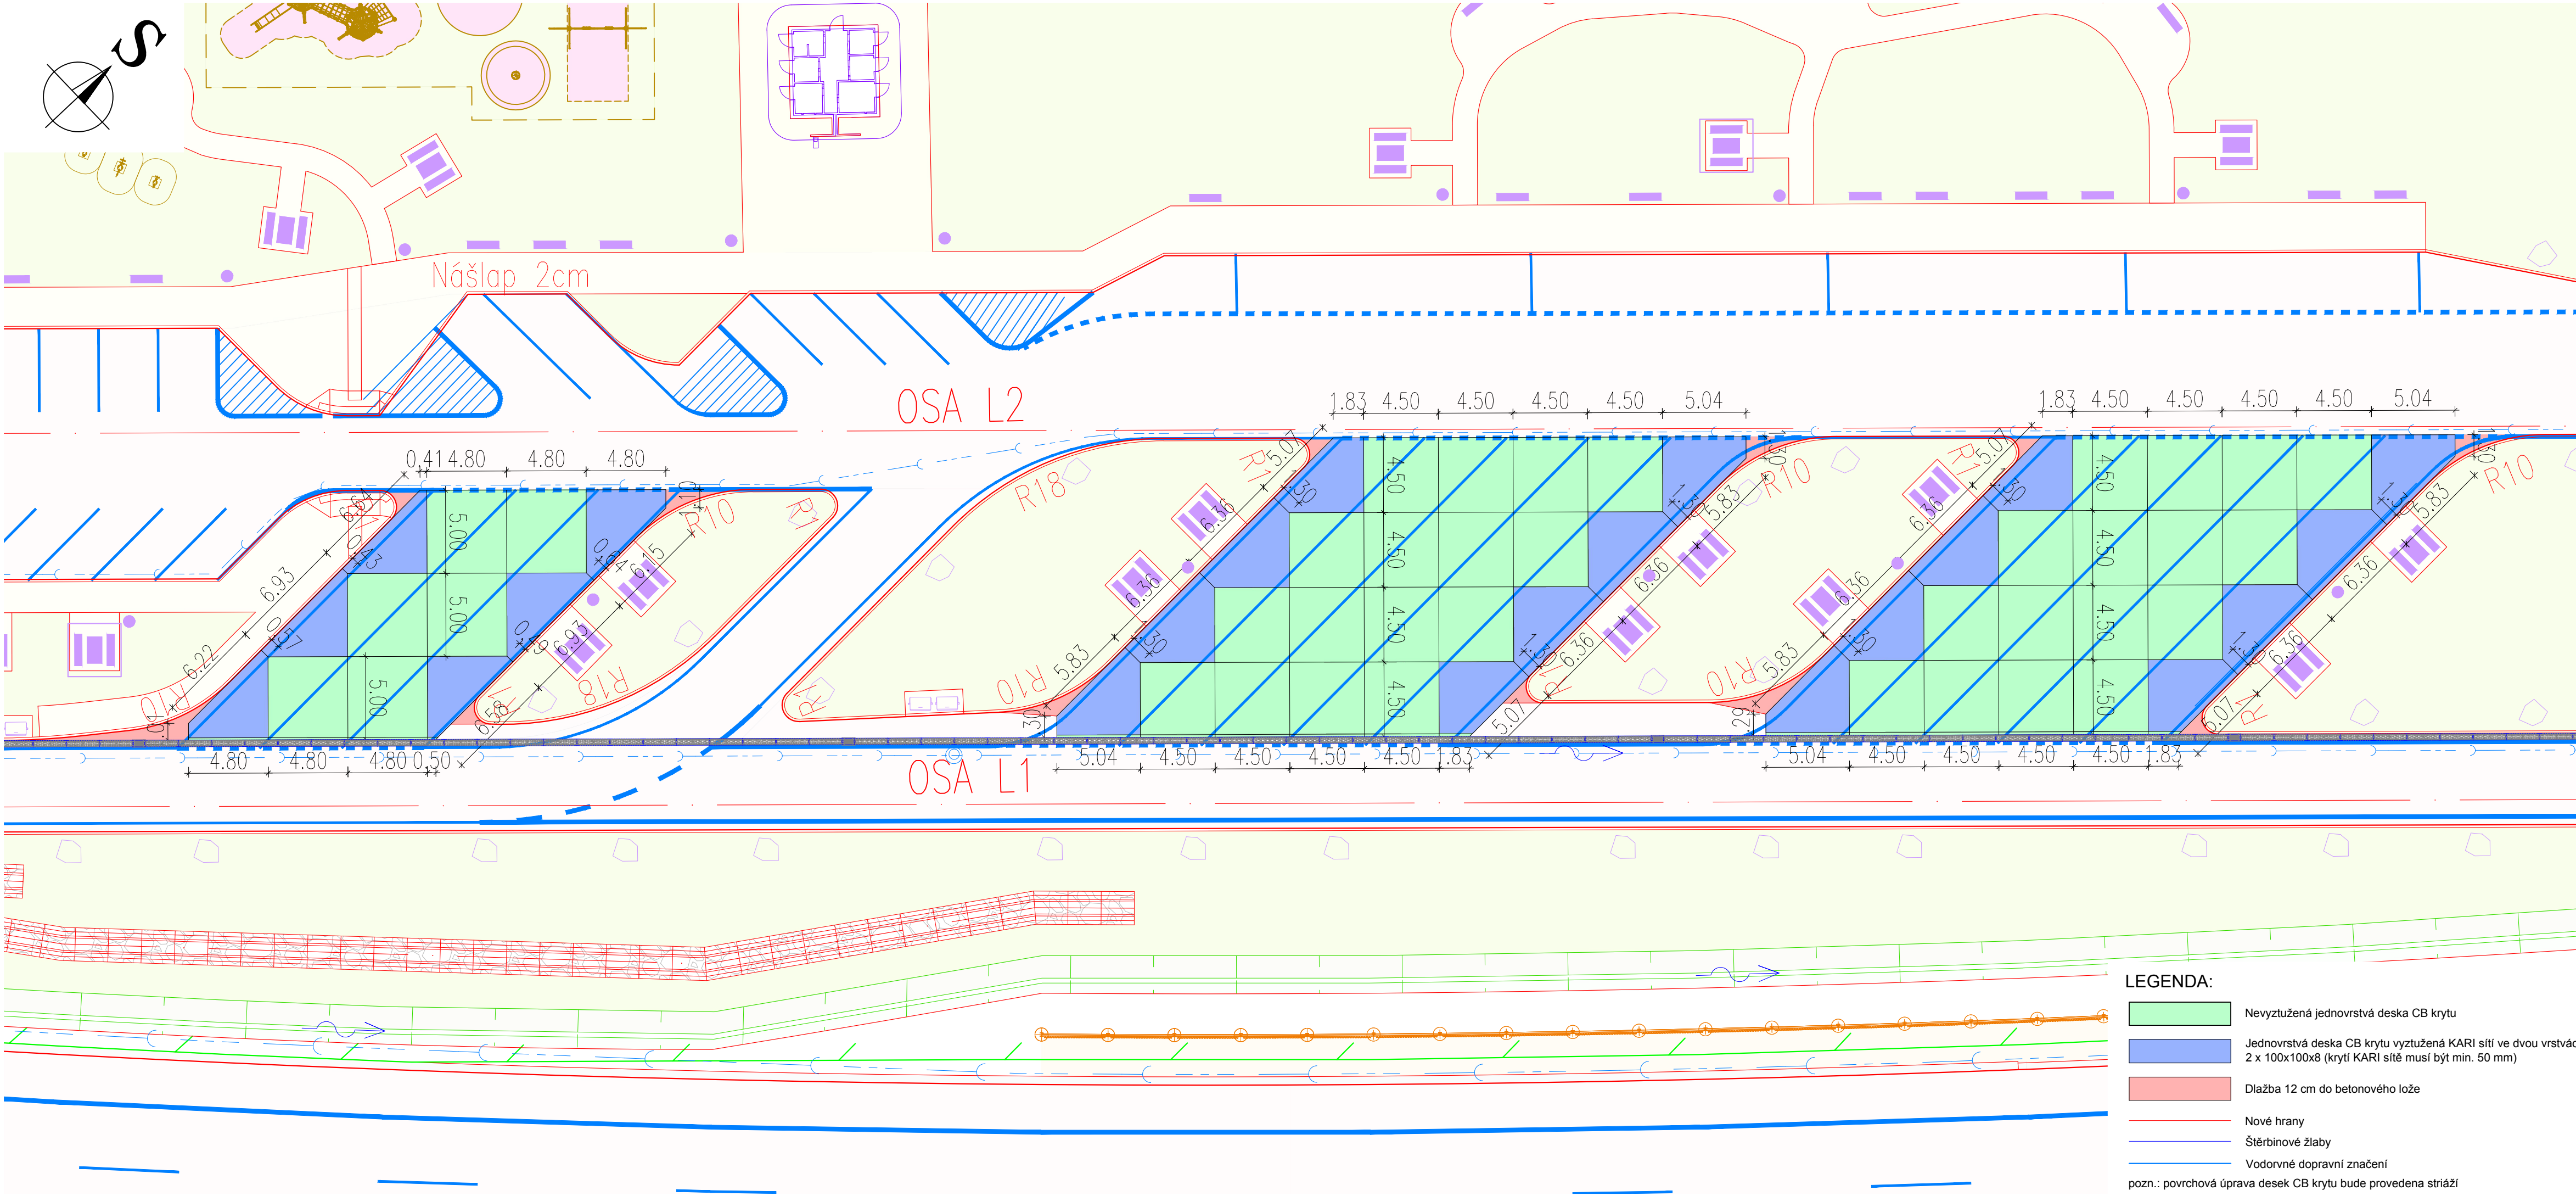

SO 135

D.1.1

VÝŠKOVÝ SYSTÉM Bpv

SOUŘADNICOVÝ SYSTÉM S-JTSK

Číslo změny:	Obsah změny:	Datum změny:
01	-	-
02	-	-
03	-	-

Objednatel:
**ŘEDITELSTVÍ SILNIC A DÁLNIC**

Ředitelství silnic a dálnic s. p.
Na Pankráci 546/56, 140 00 Praha 4

Stavbu zajišťuje Závod Praha
Na Pankráci 546/56, 140 00 Praha 4

Zhotovitel: Společníci ve sdružení

SG_Velké projekty_BIM 2020
zastoupené

SUDOP PRAHA a.s.
Hlavní inženýr projektu: Ing. Roman Petřík

Olšanská 1a, 130 80 Praha 3
telefon: +420 267 094 111

**SUDOP PRAHA**

**PUDIS**

**SUDOP BRNO**

**DOPRAVOPROJEKT BRNO**

**DOPRAVOPROJEKT**

Správce:
**SUDOP PRAHA**

SUDOP PRAHA a.s.
Olšanská 1a, 130 80 Praha 3
tel.: +420 267 094 111
e-mail: praha@sudop.cz

Vedoucí týmu:
ING. ROMAN PETŘÍK

Asistent vedoucího týmu:
ING. PAVEL MICHL
Specialista profese:
-

Zpracovatel částí:
**PUDIS**

projektová, průzkumná a konzultační společnost
PUDIS a.s., Podbabská 1014/20, 160 00 Praha 6
tel.: +420 267 004 111, www.pudis.cz, info@pudis.cz

Vedoucí střediska:	Odpovědný projektant SO, IO, PS:	Vypracoval:	Kontroloval:
ING. ZDENKA BOLEHOVSKÁ	ING. MICHAL TUREK	PETR KOTLABA	ING. MICHAL TUREK

Název akce:		Číslo smlouvy:	
D11 1108 Jaroměř - Trutnov VD-ZDS + TP + AD		22-014.250	
Část:		Projektový stupeň:	
D.1.1 OBJEKTY POZEMNÍCH KOMUNIKACÍ VČETNĚ PROPUSTKŮ SO 135 ODPOČÍVKA BRUSNICE V KM 131,0		VD-ZDS	
Název přílohy:		Datum:	
SPÁROŘEZ - VLEVO		11/2024	
		Číslo části:	
		D.1.1	
		Měřítko:	Počet formátů:
		1:250	4xA4
		Číslo přílohy:	
		7.2	

DOKUMENT LZE UŽÍVAT POUZE VE SMYSLU PŘÍSLUŠNÉ SMLOUVY O DÍLO. ŽÁDNÁ JEHO ČÁST NEMŮŽE BYT DLE ZÁKONA č. 121/2000 Sb. KOPIROVÁNA NEBO JINÝM ZPŮSOBEM ROZŠÍŘOVÁNA. BEZ SOUHLASU SUDOP PRAHA a.s.