


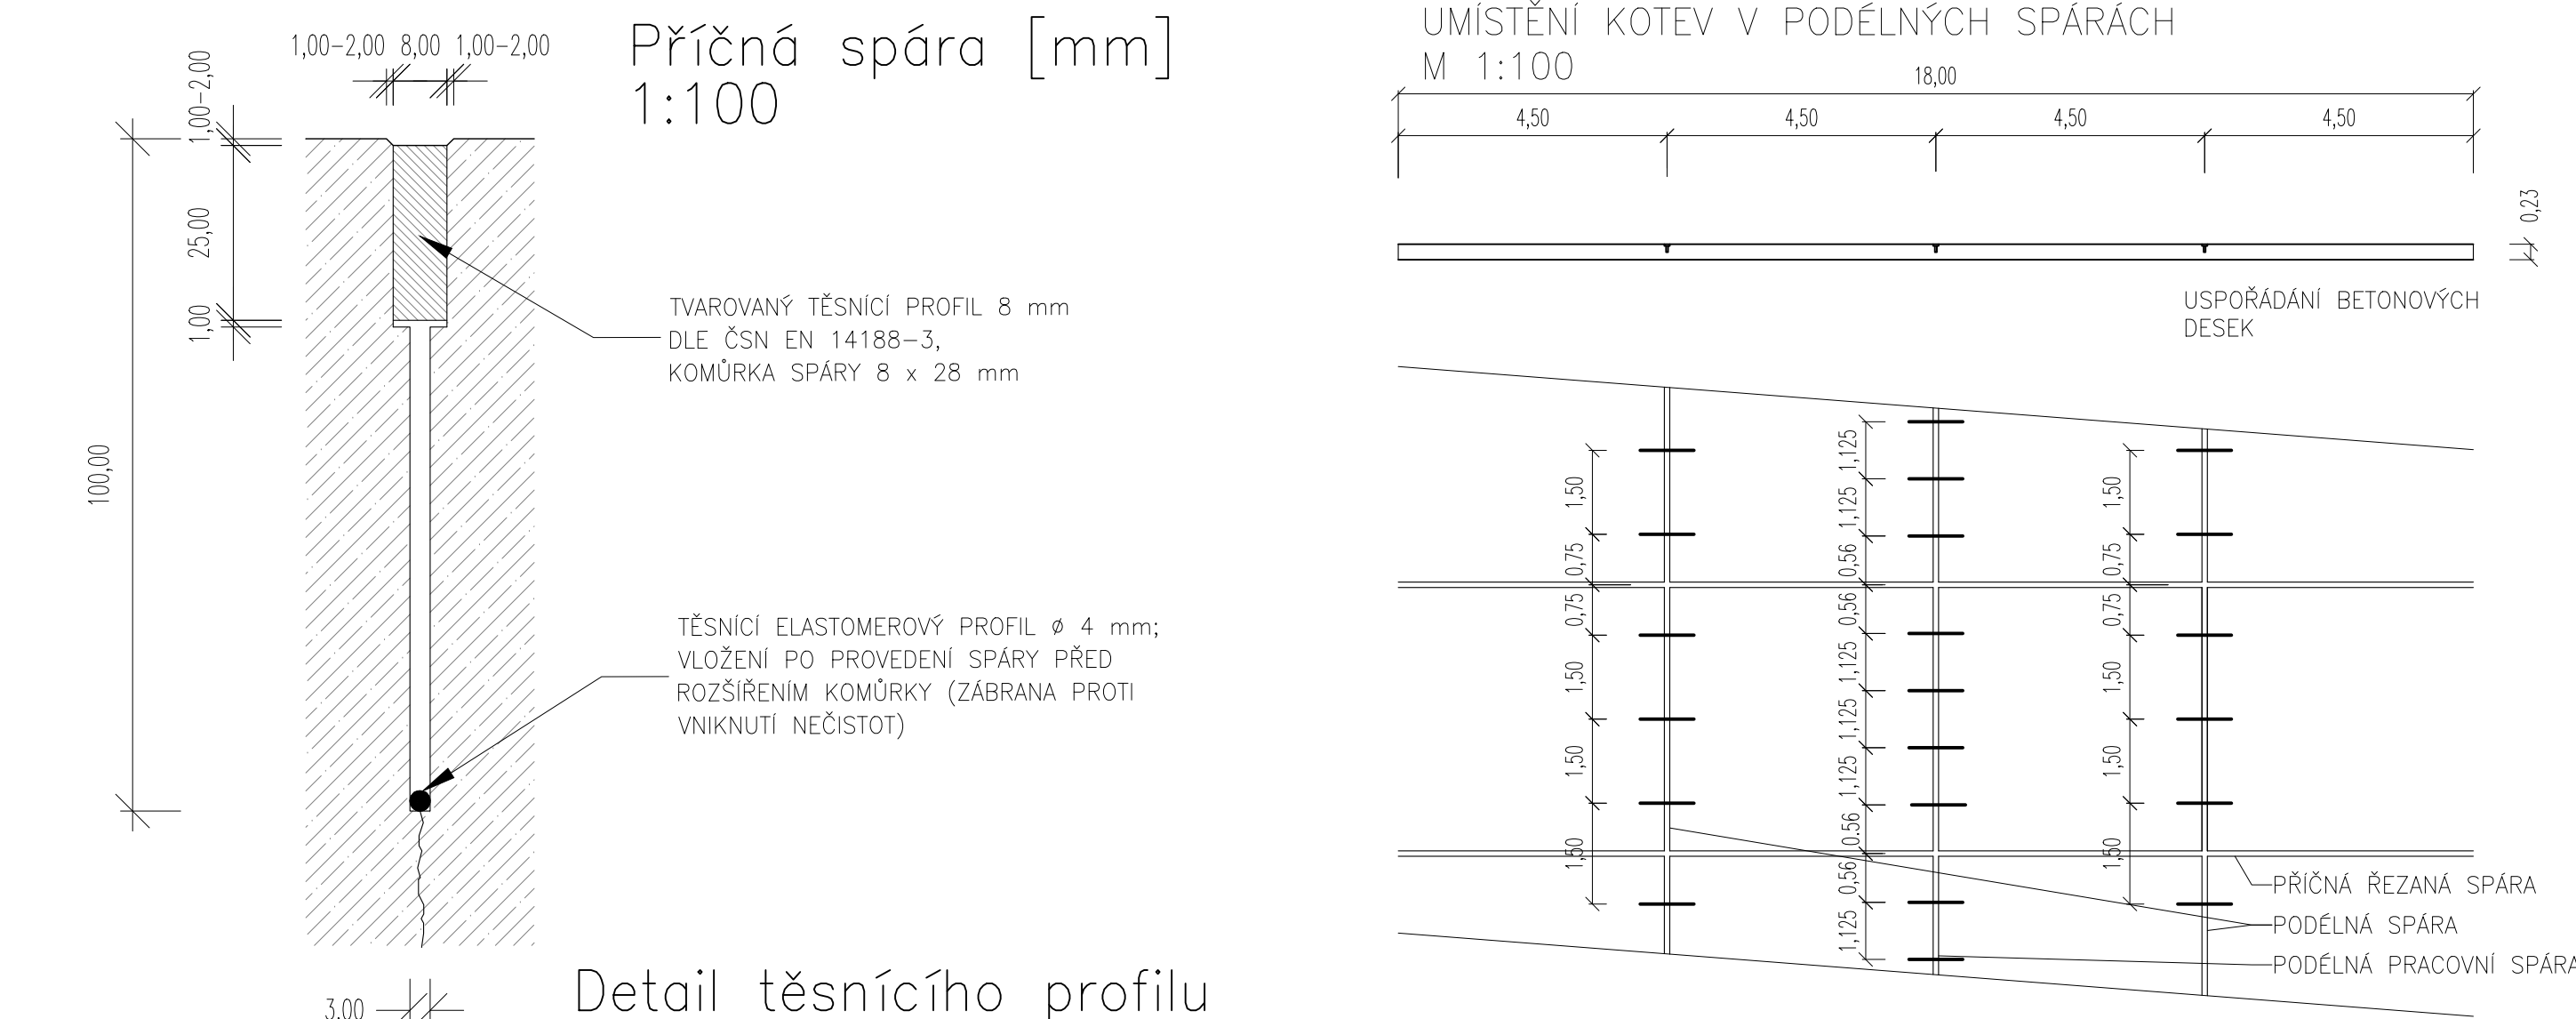


Příčná spára [mm]
1:100

Detail těsnícího profilu před uložením [mm]
1:100

POZNÁMKA:

Příčné spáry budou proříznuty do hloubky 100 mm. V rozsahu betonáže se řežou příčné spáry postupně do zatvrdělého betonu, nejpozději však 24 hodin po betonáži. Co nejdříve po proříznutí spáry musí být řezný kal beze zbytku odstraněn tlakovou vodou, aby nezatvrdly případně zbytky nezhydratovaného cementu obsažené v kalu.

Bezprostředně po vyčištění bude těsně pod povrch krytu do spár aplikována předtěsnění (těsnící profil), které bude sloužit jako provizorní těsnění během stavebního provozu. Pro definitivní spáry bude předtěsnění odstraněno, spára se rozšíří drážkou na šířku 8 mm a hloubku 28 mm. Komůrka bude utěsněna těsnícím profilem šířky 8 mm dle ČSN EN 14188-3.

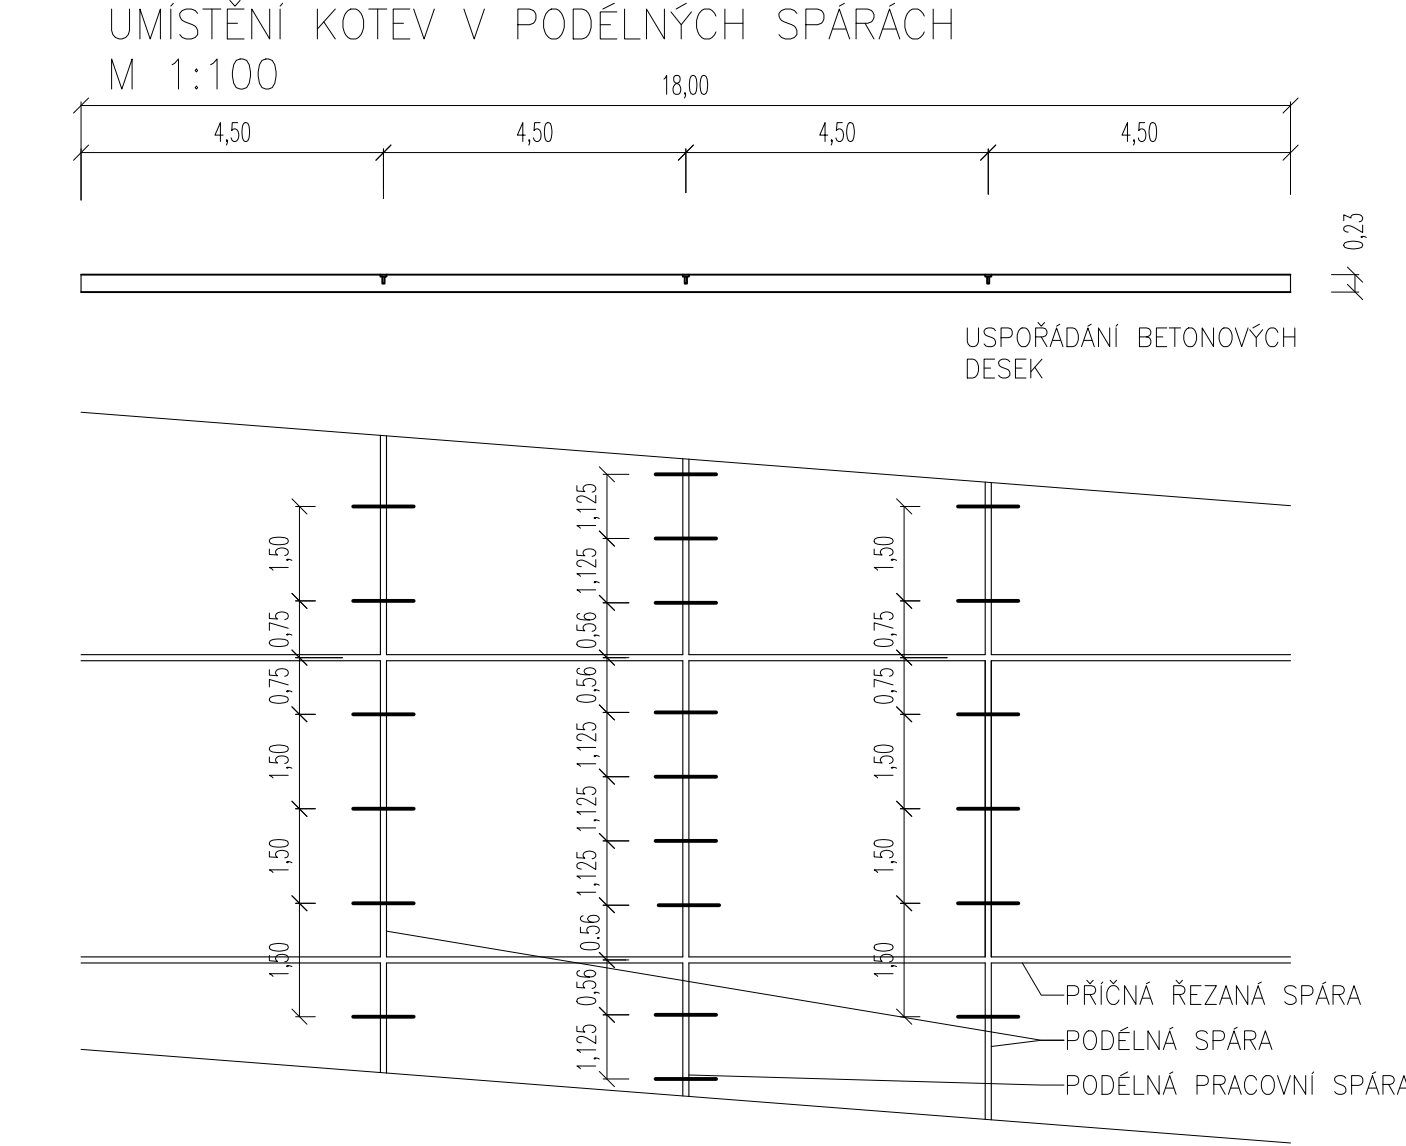


Podélná spára [mm]
1:100

Detail těsnícího profilu před uložením [mm]
1:100

POZNÁMKA:

Kotvy v podélných pracovních spárách se umístí do 1/2 tloušťky desky (tj. 115 mm) po třech kusech na desku ve stejných vzdálenostech od sebe. U podélných pracovních spár musí být vzdálenost kotev max. 1,0 m

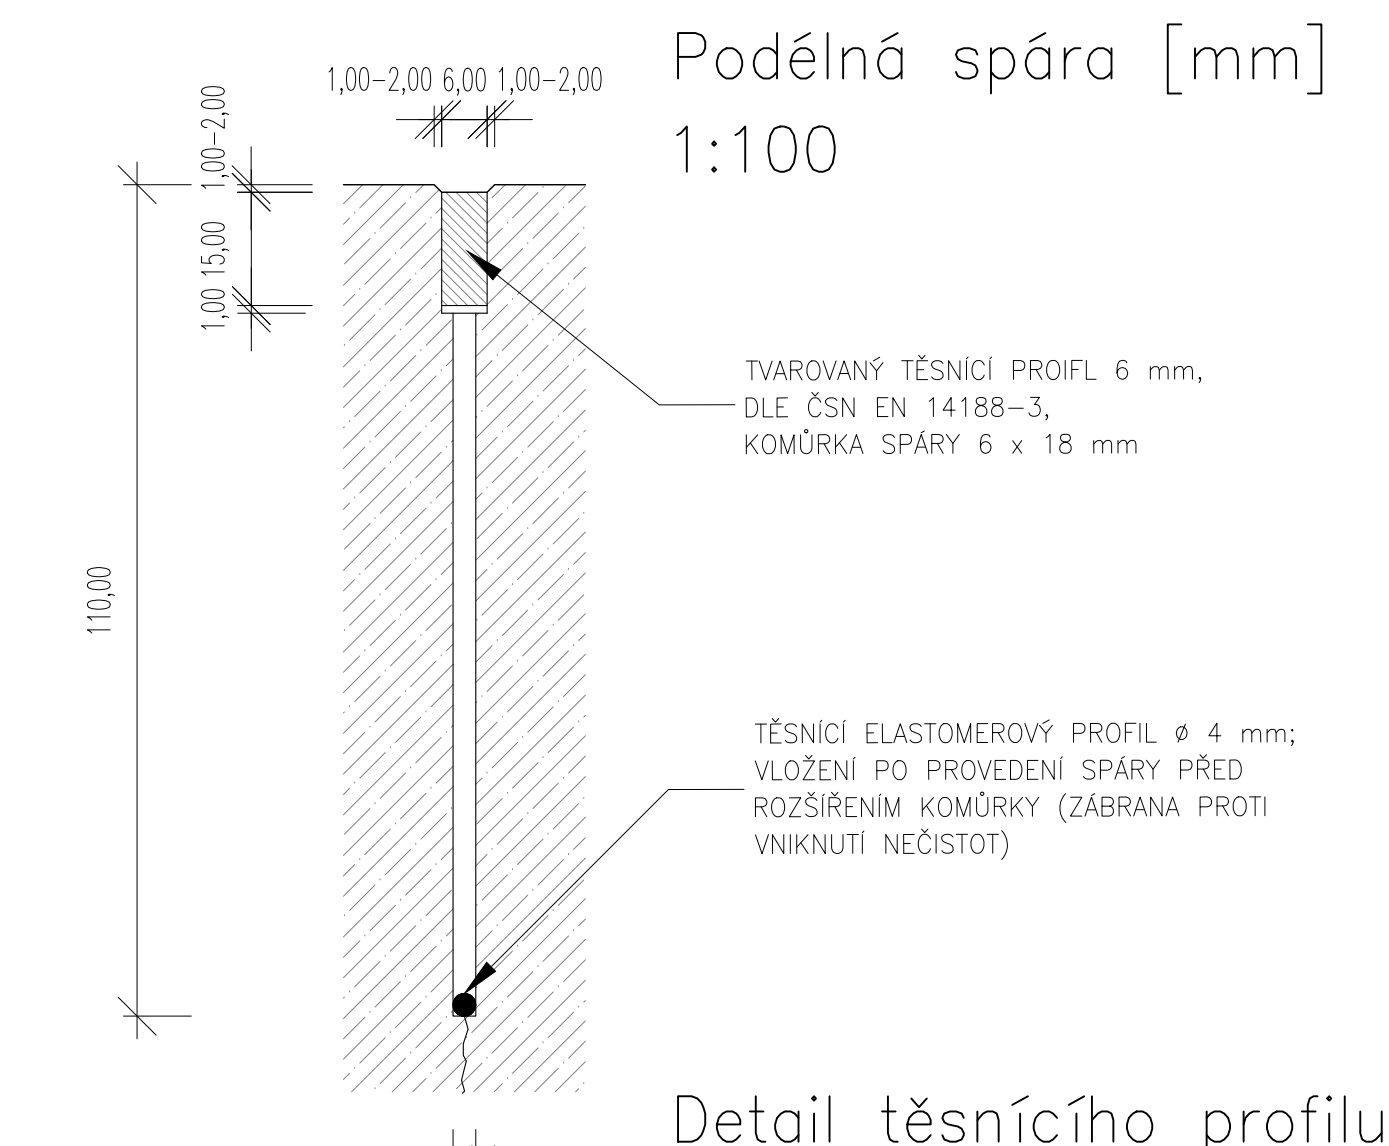


Podélná spára [mm]
1:100

Detail těsnícího profilu před uložením [mm]
1:100

POZNÁMKA:

Podélné spáry budou proříznuty do hloubky 110 mm, následně po nařezání příčných spár, nejpozději však 48 hodin po betonáži. Podélné spáry na vybetonovaném pásu musí být řezány současně.

Rozšiřovací komůrka šířky 6 mm bude provedena do hloubky 18 mm. Komůrka je souměrná vzhledem k původnímu řezu spáry a vytváří se bezprostředně před utěsněním pár. Komůrka bude utěsněna těsnícím profilem šířky 6 mm dle ČSN EN 14188-3.

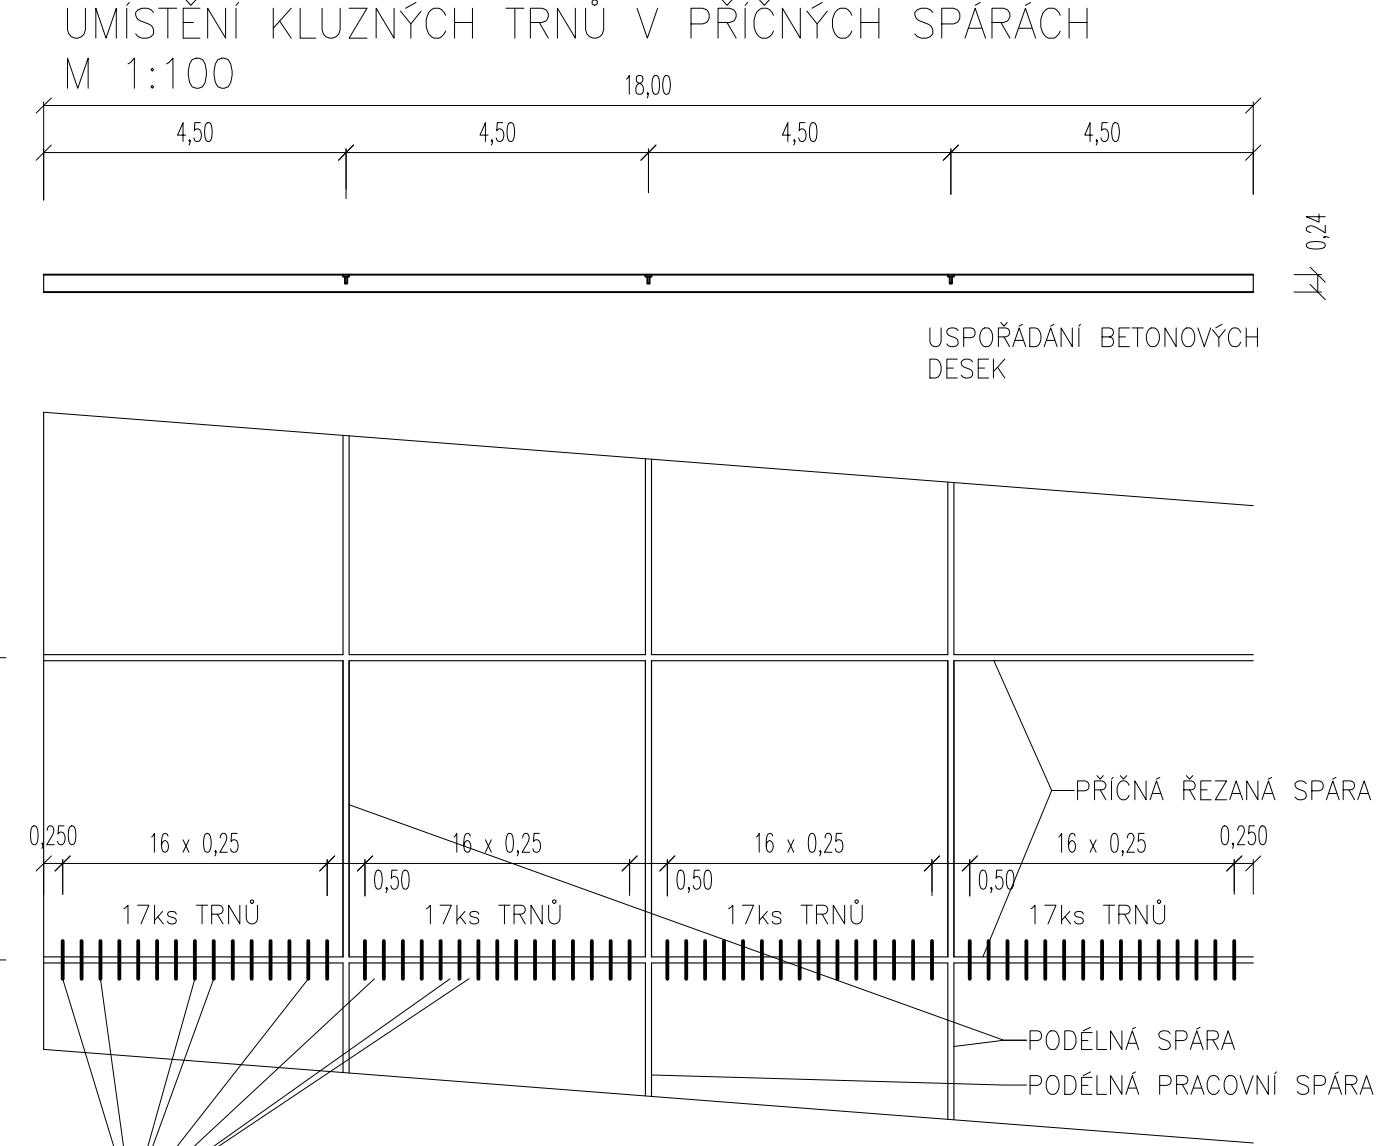

Podélná spára [mm]
1:100

Detail těsnícího profilu před uložením [mm]
1:100

POZNÁMKA:

Kotvy v podélných pracovních spárách se umístí do 1/2 tloušťky desky (tj. 115 mm) po třech kusech na desku ve stejných vzdálenostech od sebe. U podélných pracovních spár musí být vzdálenost kotev max. 1,0 m

SO 135

D.1.1

Číslo změny:	Obsah změny:	Datum změny:
01	-	-
02	-	-
03	-	-

Objednatel:	Ředitelství silnic a dálnic s. p. Na Pankráci 546/56, 140 00 Praha 4
Stavbu zajišťuje:	Závod Praha Na Pankráci 546/56, 140 00 Praha 4

Zhotovitel: Společnosti ve sdružení	SG_Velké projekty_BIM 2020 zastoupené
SUDOP PRAHA a.s. Hlavní inženýr projektu: Ing. Roman Petřík	Olšanská 1a, 130 80 Praha 3 telefon: +420 267 094 111

Spřávce:	SUDOP PRAHA a.s. Olšanská 1a, 130 80 Praha 3 tel.: +420 267 094 111 e-mail: praha@sudop.cz	Vedoucí týmu:	ING. ROMAN PETŘÍK	Asistent vedoucího týmu:	ING. PAVEL MICHL
Specialista profese:			-		

Zpracovatel:	projektová, průzkumná a konzultační společnost PUDIS a.s., Podbabská 1014/20, 160 00 Praha 6 tel.: +420 267 004 111, www.pudis.cz, info@pudis.cz
--------------	--

Vedoucí střediska:	Odpovědný projektant SO, IO, PS:	Vypracoval:	Kontroloval:
ING. ZDENKA BOLEHOVSKÁ	ING. MICHAL TUREK	PETR KOTLABA	ING. MICHAL TUREK

Název akce:	Číslo smlouvy:
D11 1108 Jaroměř - Trutnov VD-ZDS + TP + AD	22-014.250
Projekový stupeň:	VD-ZDS
Část:	Datum:
D.1.1 OBJEKTY POZEMNÍCH KOMUNIKACÍ VČETNĚ PROPUSTKŮ SO 135 ODPOČÍVKA BRUSNICE V KM 131,0	11/2024
Název přílohy:	Měřítko:
DETAILY CBK	1:100/1:10
	Číslo přílohy:
	8