


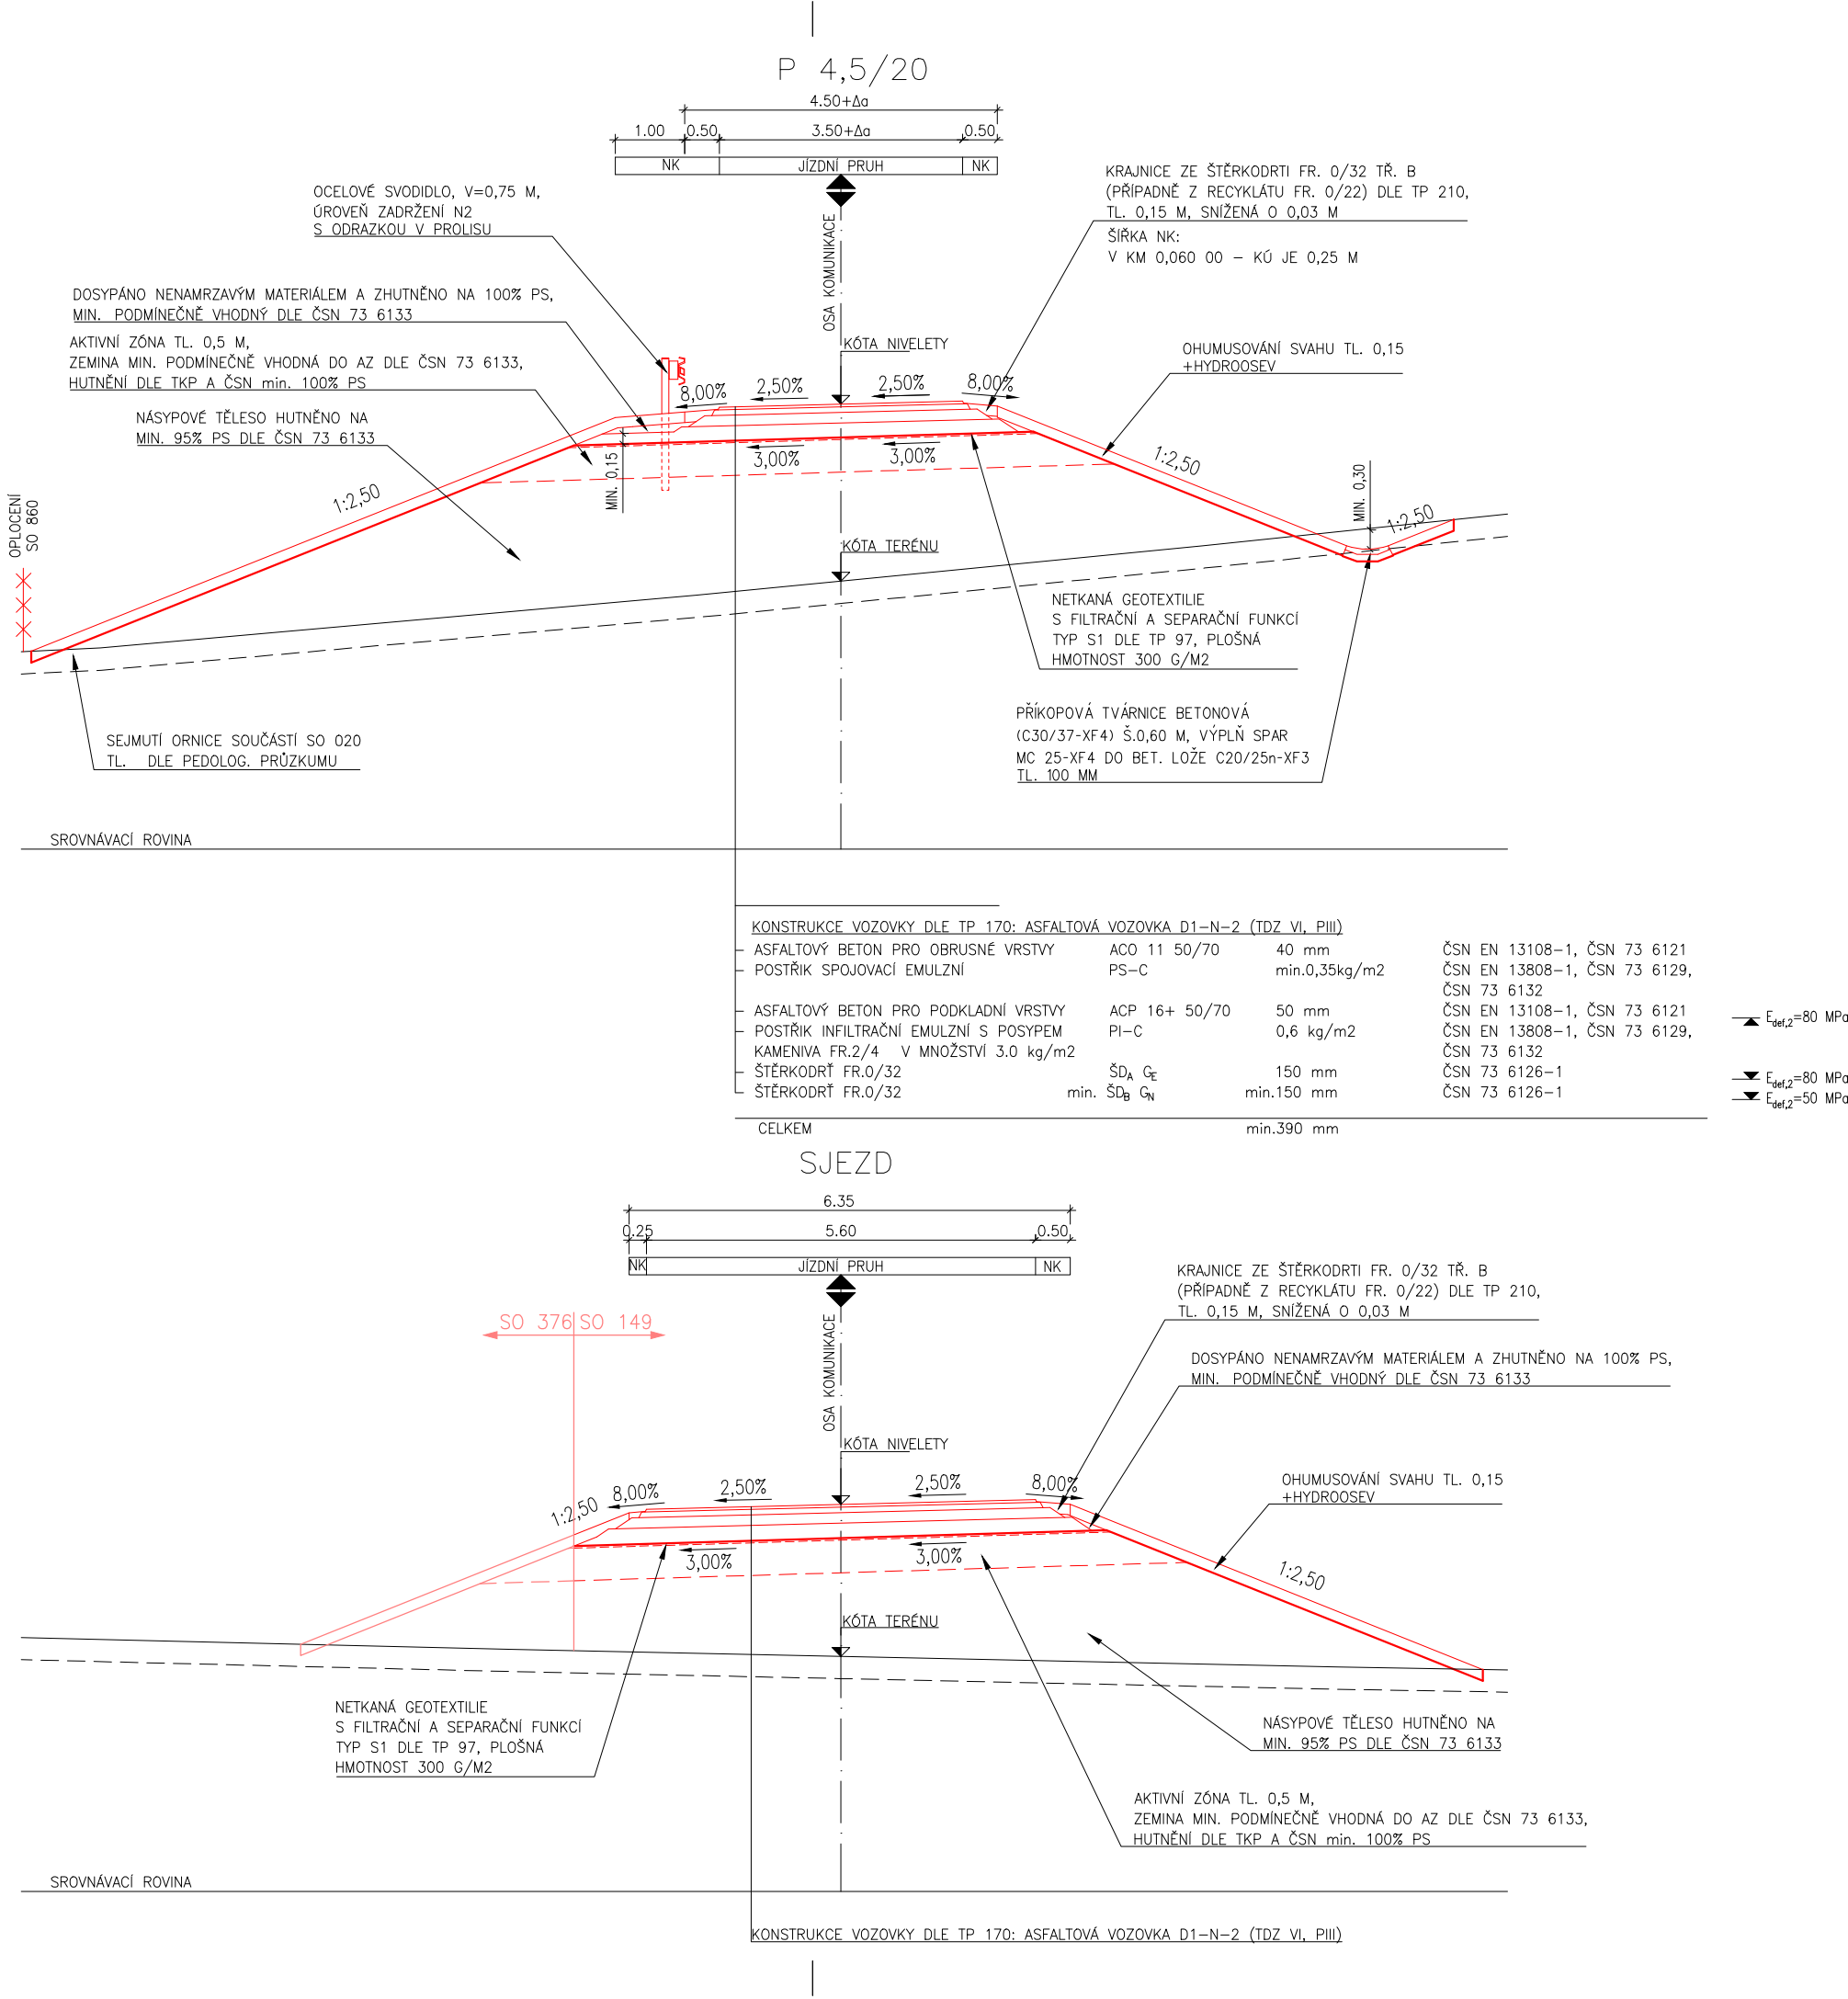

SO 149

D.1.1

VÝŠKOVÝ SYSTÉM Bpv

SOUŘADNICOVÝ SYSTÉM S-JTSK

Číslo změny:	Obsah změny:	Datum změny:
01	-	-
02	-	-
03	-	-



ŘEDITELSTVÍ
SILNIC
A DÁLNIC

Objednatel:
Ředitelství silnic a dálnic s. p.
Na Pankráci 546/56, 140 00 Praha 4

Stavbu zajišťuje Závod Praha
Na Pankráci 546/56, 140 00 Praha 4

Zhotovitel: Společníci ve sdružení

SG_Velké projekty_BIM 2020
zastoupené

SUDOP PRAHA a.s.
Hlavní inženýr projektu: Ing. Roman Petřík

Olšanská 1a, 130 80 Praha 3
telefon: +420 267 094 111













SUDOP PRAHA a.s.
Olšanská 1a, 130 80 Praha 3
tel.: +420 267 094 111
e-mail: praha@sudop.cz

Správce:

Vedoucí týmu:
ING. ROMAN PETŘÍK

Asistent vedoucího týmu:
ING. PAVEL MICHL
Specialista profese:
-

Zpracovatel částí:


projektová, průzkumná a konzultační společnost
PUDIS a.s., Podbabská 1014/20, 160 00 Praha 6
tel.: +420 267 004 111, www.pudis.cz, info@pudis.cz

Vedoucí střediska:
ING. ZDEŇKA BOLEHOVSKÁ

Odpovědný projektant SO, IO, PS:
ING. MICHAL TUREK

Vypracoval:
BC. ZARRINA UTEULINA

Kontroloval:
ING. MICHAL TUREK

Název akce:		Číslo smlouvy: 22-014.250	
D11 1108 Jaroměř - Trutnov VD-ZDS + TP + AD		Projektový stupeň: VD-ZDS	
Část:		Datum: 11/2024	
D.1.1 OBJEKTY POZEMNÍCH KOMUNIKACÍ VČETNĚ PROPUSTKŮ SO 149 PŘÍJEZD K RETENČNÍ NÁDRŽI KM 131,2		Číslo části: D.1.1	
Název přílohy:		Měřítko: 1:100	Počet formátů: 3xA4
VZOROVÝ PŘÍČNÝ ŘEZ		Číslo přílohy: 4	