


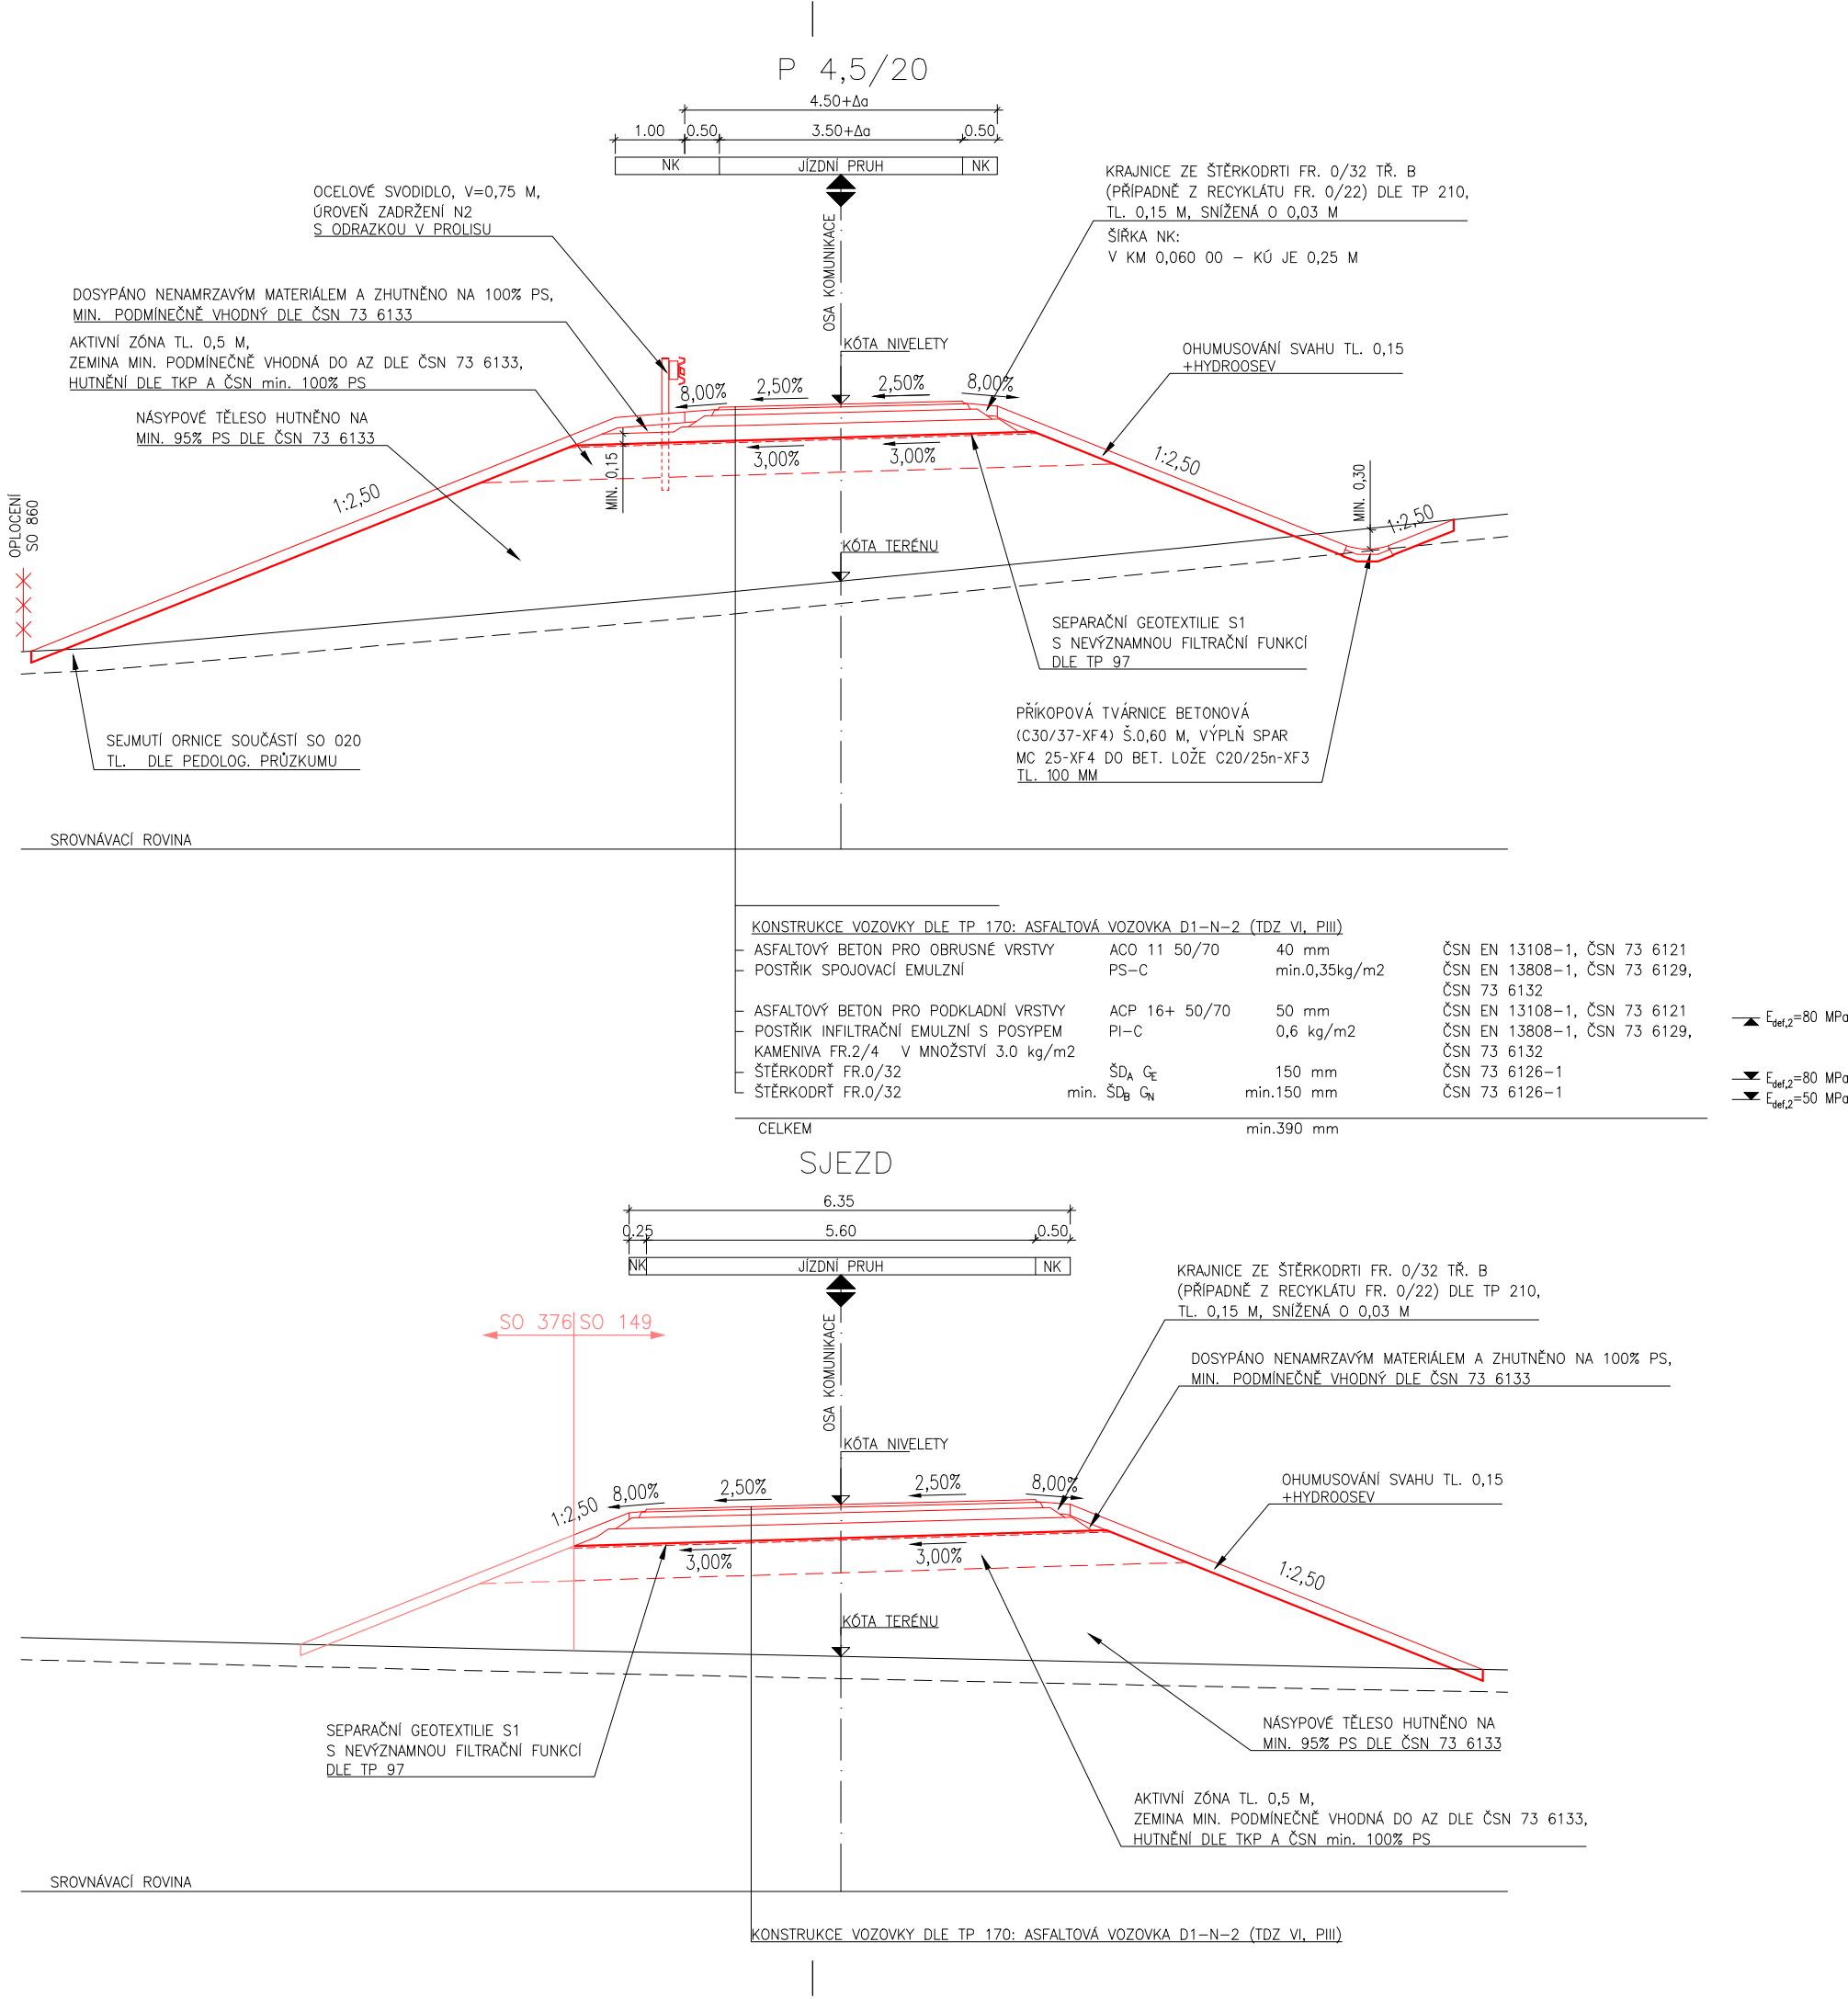

SO 149

D.1.1

VÝŠKOVÝ SYSTÉM Bpv

SOUŘADNICOVÝ SYSTÉM S-JTSK

Číslo změny:	Obsah změny:	Datum změny:
01	-	-
02	-	-
03	-	-



ŘEDITELSTVÍ SILNIC A DÁLNIC

Objednatel:

Ředitelství silnic a dálnic s. p.
Na Pankráci 546/56, 140 00 Praha 4

Stavbu zajišťuje Závod Praha
Na Pankráci 546/56, 140 00 Praha 4

Zhotovitel: Společníci ve sdružení

SG_Velké projekty_BIM 2020
zastoupené

SUDOP PRAHA a.s.
Hlavní inženýr projektu: Ing. Roman Petřík

Olšanská 1a, 130 80 Praha 3
telefon: +420 267 094 111



Správce:



SUDOP PRAHA a.s.
Olšanská 1a, 130 80 Praha 3
tel.: +420 267 094 111
e-mail: praha@sudop.cz

Vedoucí týmu:

ING. ROMAN PETŘÍK

Asistent vedoucího týmu:

ING. PAVEL MICHL

Specialista profese:

-

Zpracovatel částí:



projektová, průzkumná a konzultační společnost

PUDIS a.s., Podbabská 1014/20, 160 00 Praha 6
tel.: +420 267 004 111, www.pudis.cz, info@pudis.cz

Vedoucí střediska:	Odpovědný projektant SO, IO, PS:	Vypracoval:	Kontroloval:
ING. ZDEŇKA BOLEHOVSKÁ	ING. MICHAL TUREK	BC. ZARRINA UTEULINA	ING. MICHAL TUREK

Název akce:	Číslo smlouvy:
D11 1108 Jaroměř - Trutnov VD-ZDS + TP + AD	22-014.250
Část:	Projektový stupeň:
D.1.1 OBJEKTY POZEMNÍCH KOMUNIKACÍ VČETNĚ PROPUSTKŮ SO 149 PŘÍJEZD K RETENČNÍ NÁDRŽI KM 131,2	VD-ZDS
Název přílohy:	Datum:
VZOROVÝ PŘÍČNÝ ŘEZ	11/2024
	Číslo části:
	D.1.1
	Měřítko:
	1:100
	Počet formátů:
	3xA4
	Číslo přílohy:
	4