


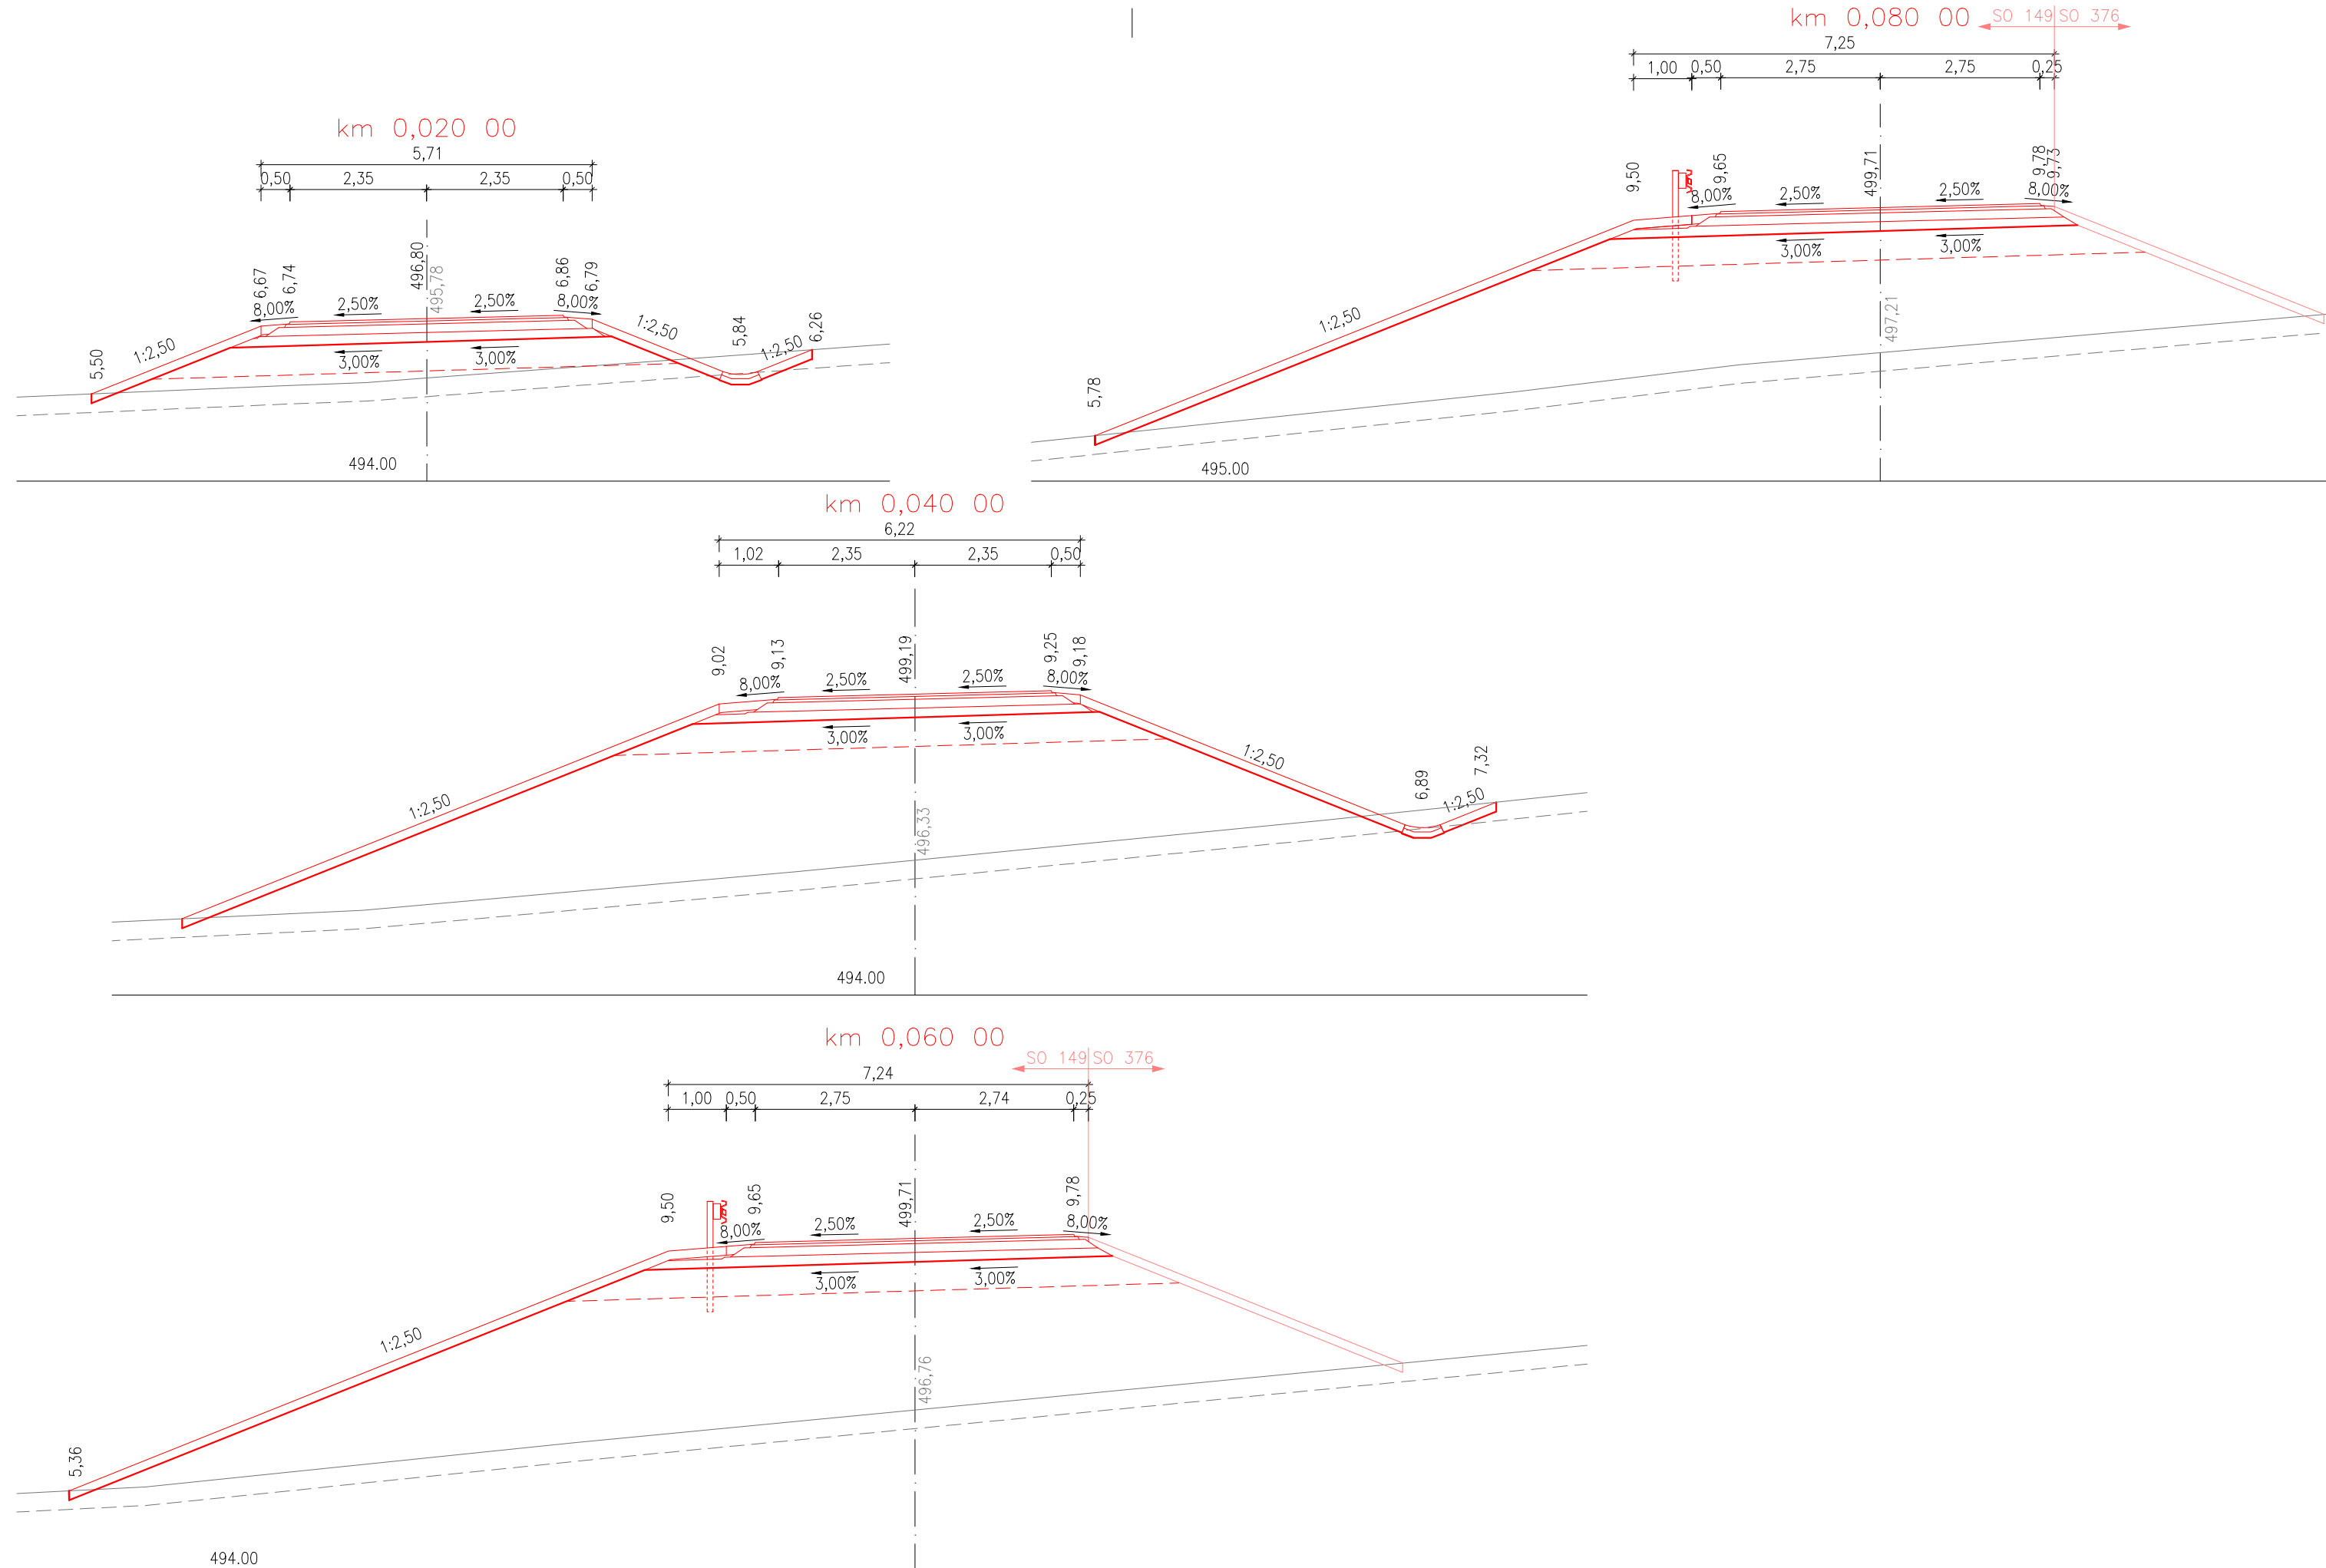

SO 149
D.1.1

VÝŠKOVÝ SYSTÉM Bpv

SOUŘADNICOVÝ SYSTÉM S-JTSK

Číslo změny:	Obsah změny:	Datum změny:
01	-	-
02	-	-
03	-	-

<i>Objednatel:</i>  ŘEDITELSTVÍ SILNIC A DÁLNIC	Ředitelství silnic a dálnic s. p. Na Pankráci 546/56, 140 00 Praha 4 Stavbu zajišťuje Závod Praha Na Pankráci 546/56, 140 00 Praha 4
--	--

<i>Zhotovitel: Společníci ve sdružení</i> SUDOP PRAHA a.s. Hlavní inženýr projektu: Ing. Roman Petřík	SG_Velké projekty_BIM 2020 zastoupené	Olšanská 1a, 130 80 Praha 3 telefon: +420 267 094 111
--	---	---







<i>Správce:</i>  SUDOP PRAHA SUDOP PRAHA a.s. Olšanská 1a, 130 80 Praha 3 tel.: +420 267 094 111 e-mail: praha@sudop.cz	<i>Vedoucí týmu:</i> ING. ROMAN PETŘÍK	<i>Asistent vedoucího týmu:</i> ING. PAVEL MICHL
		<i>Specialista profese:</i> -

Zpracovatel částí

PUDIS

projektová, průzkumná a konzultační společnost

PUDIS a.s., Podbabská 1014/20, 160 00 Praha 6
tel.: +420 267 004 111, www.pudis.cz, info@pudis.cz

<i>Vedoucí střediska:</i>	<i>Odpovědný projektant SO, IO, PS:</i>	<i>Vypracoval:</i>	<i>Kontroloval:</i>
ING. ZDEŇKA BOLEHOVSKÁ	ING. MICHAL TUREK	BC. ZARRINA UTEULINA	ING. MICHAL TUREK

<i>Název akce:</i> D11 1108 Jaroměř - Trutnov VD-ZDS + TP + AD	<i>Číslo smlouvy:</i> 22-014.250	
	<i>Projektový stupeň:</i> VD-ZDS	
<i>Část:</i> D.1.1 OBJEKTY POZEMNÍCH KOMUNIKACÍ VČETNĚ PROPUSTKŮ SO 149 PŘÍJEZD K RETENČNÍ NÁDRŽI KM 131,2	<i>Datum:</i> 11/2024	
	<i>Číslo části:</i> D.1.1	
<i>Název přílohy:</i> PŘÍČNÉ ŘEZY	<i>Měřítko:</i> 1:100	<i>Počet formátů:</i> 3xA4
	<i>Číslo přílohy:</i> 5	