


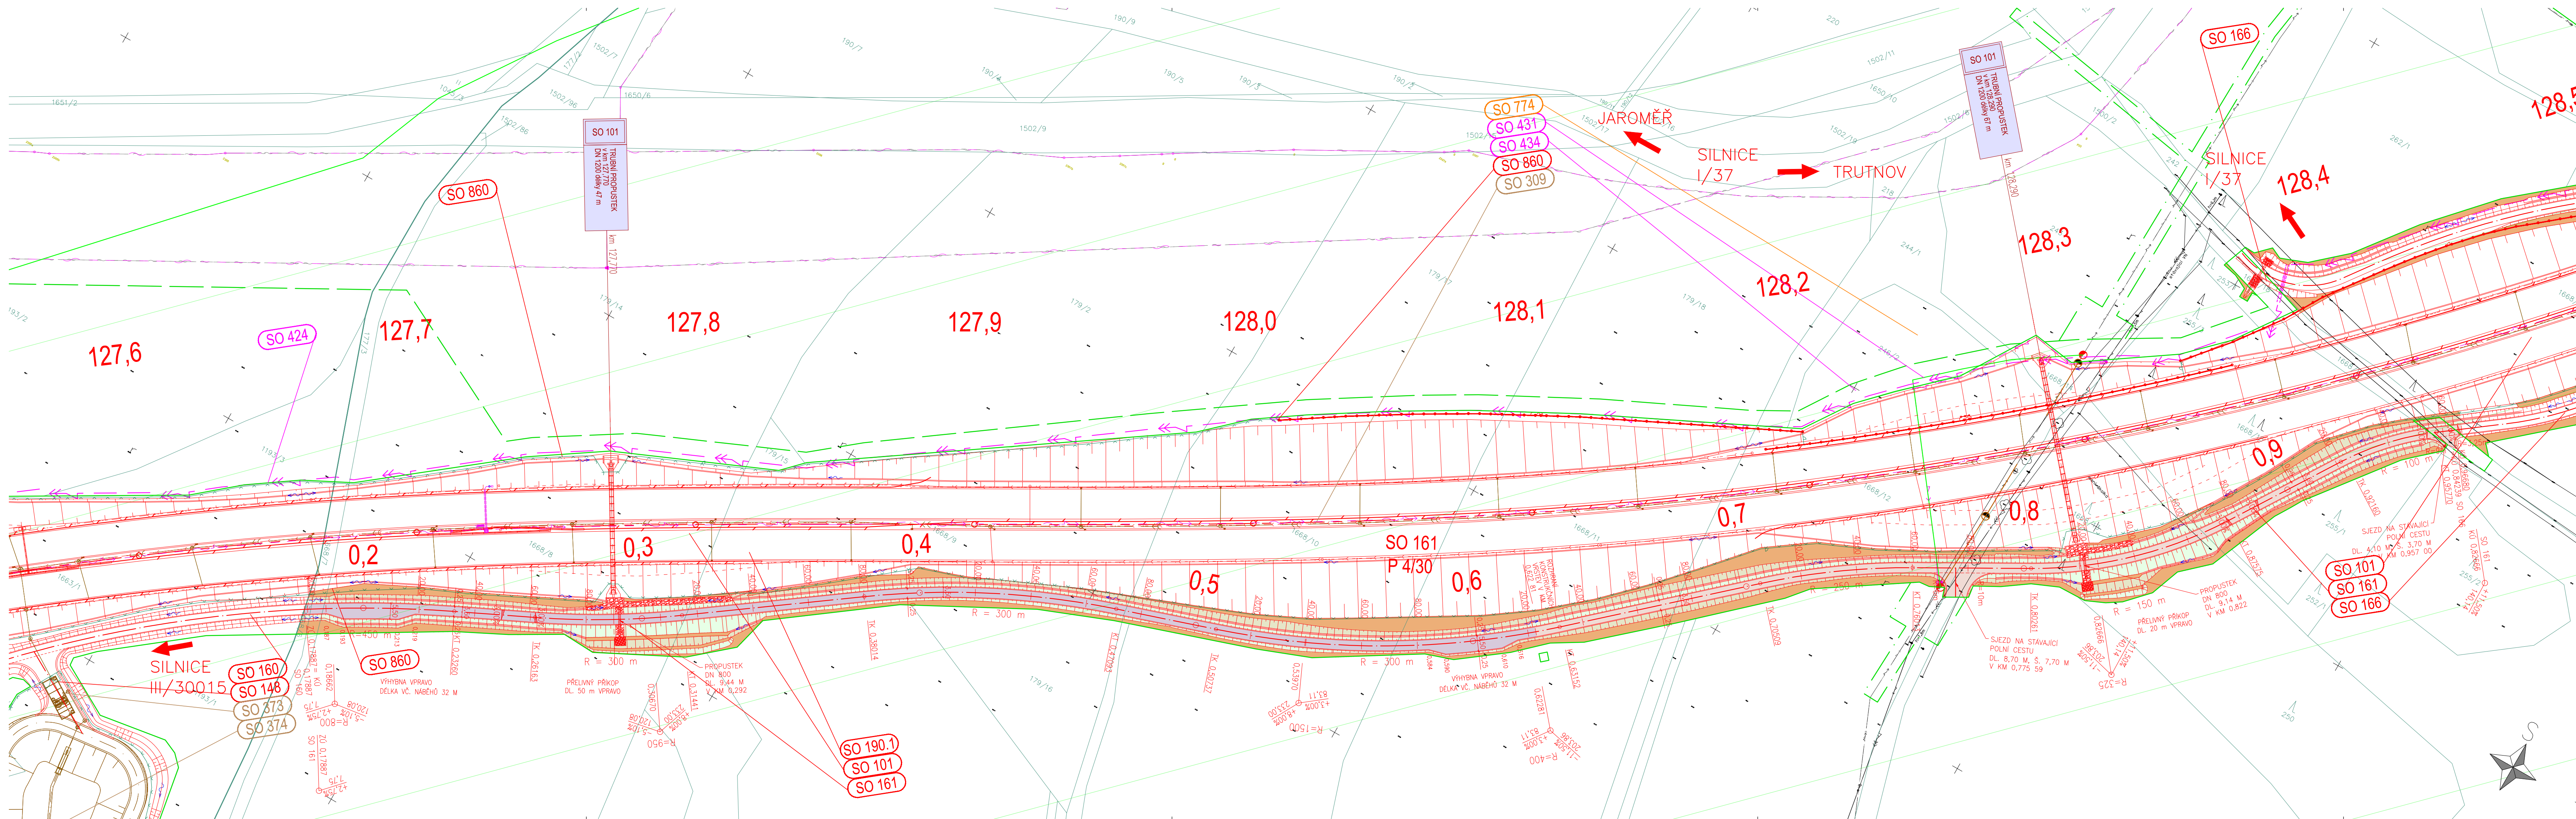

LEGENDA

HRANY:

- Nově navržené hrany trvalých SO
- Nově navržené hrany provizorních komunikací
- Související investice
- Oplocení

BAREVNÉ PLOCHY:

- Vozovka D11 – asfaltový kryt
- Vozovka silnic a MK
- Zpevněná polní cesta/účelová komunikace – asfaltový kryt
- Nezpevněná polní cesta/účelová komunikace – nestmelový kryt
- Násyp
- Zářez
- Technologické napojení na stav.vrstvy
- Úprava terénu v rovině
- Ostrůvky pojízdené
- Ostrůvky nepojízdené
- Prsteneц okružní křižovatky
- Chodník

ZÁBORY STAVBY:

- Zábor trvalý
- Zábor dočasný – do 1 roku
- Zábor dočasný – nad 1 rok

STÁVAJÍCÍ POLOHOPIS :

- Stávající polohopis
- Stávající stav – strom, neplod.půda, park, std.
- Stávající hranice parcel KN
- Stávající polohopis katastrálního území

STÁVAJÍCÍ INŽ. SÍTĚ:

- Sdělovací – nadzemní
- Sdělovací – podzemní
- Silnoproudé vedení – NN podzemní
- Silnoproudé vedení – NN nadzemní
- Silnoproudé vedení – VN nadzemní
- Silnoproudé vedení – VN podzemní
- Silnoproudé vedení – VVN nadzemní
- Plynovod – NTL
- Plynovod – STL
- Plynovod – VTL
- veřejné osvětlení
- Vodovod
- Vodovod – pitný
- Kanalizace – bez rozlišení

SO 161

D.1.1

VÝŠKOVÝ SYSTÉM Bpv SOUŘADNICOVÝ SYSTÉM S-JTSK

Číslo změny:	Obsah změny:	Datum změny:
01	-	-
02	-	-
03	-	-

Objednatel: Ředitelství silnic a dálnic s. p.
Na Pankráci 546/56, 140 00 Praha 4

Stavbu zajišťuje: Závod Praha
Na Pankráci 546/56, 140 00 Praha 4

Zhotovitel: Společnosti ve sdružení **SG_Velké projekty_BIM 2020** zastoupené

SUDOP PRAHA a.s. Olšanská 1a, 130 80 Praha 3 telefon: +420 267 094 111

Hlavní inženýr projektu: Ing. Roman Petřík

SUDOP PRAHA **PUDIS** **SUDOP** **DOPRAVOPROJEKT BUNDO** **DOPRAVOPROJEKT**

Správce: **SUDOP PRAHA** SUDOP PRAHA a.s. Olšanská 1a, 130 80 Praha 3 tel.: +420 267 094 111 e-mail: praha@sudop.cz

Vedoucí týmu: ING. ROMAN PETŘÍK

Asistent vedoucího týmu: ING. PAVEL MICHL

Specialista profese: -

Zpracovatel: **PUDIS** projektová, průzkumná a konzultační společnost

PUDIS a.s., Podbabská 1014/20, 160 00 Praha 6 tel.: +420 267 004 111, www.pudis.cz, info@pudis.cz

Vedoucí střediska: ING. ZDEŇKA BOLEHOVSKÁ **Odpovědný projektant SO, IO, PS:** ING. MICHAL TUREK **Vypracoval:** ING. TOMÁŠ VÁŇA **Kontroloval:** ING. MICHAL TUREK

Název akce: **D11 1108 Jaroměř - Trutnov VD-ZDS + TP + AD** **Číslo smlouvy:** 22-014.250

Projektový stupeň: VD-ZDS

Část: D.1.1 OBJEKTY POZEMNÍCH KOMUNIKACÍ VČETNĚ PROPUSTKŮ
SO 161 PŘÍSTUPY NA POZEMKY V K.Ú BRUSNICE

Datum: 11/2024

Číslo části: D.1.1

Název přílohy: **SITUACE** **Měřítko:** 1:1000 **Počet formátů:** 6x44

Číslo přílohy: 2