


PODROBNÝ PODÉLNÝ PROFIL: SO 161
M 1:1000/100
ROZSAH: KM 0,15609 – 0,96680
DRUH PLOCHY ÚZEMÍ: KATASTRÁLNÍ ÚZEMÍ: OKRES: KRAJ:

TRVALÝ TRÁVNÍ POROST	ORNA PŮDA	TRUTNOV	LESNÍ POZEMEK	OSTATNÍ PLOCHA
OSTATNÍ PLOCHA	BRUSNICE	KRÁLOVÉHRADECKÝ		

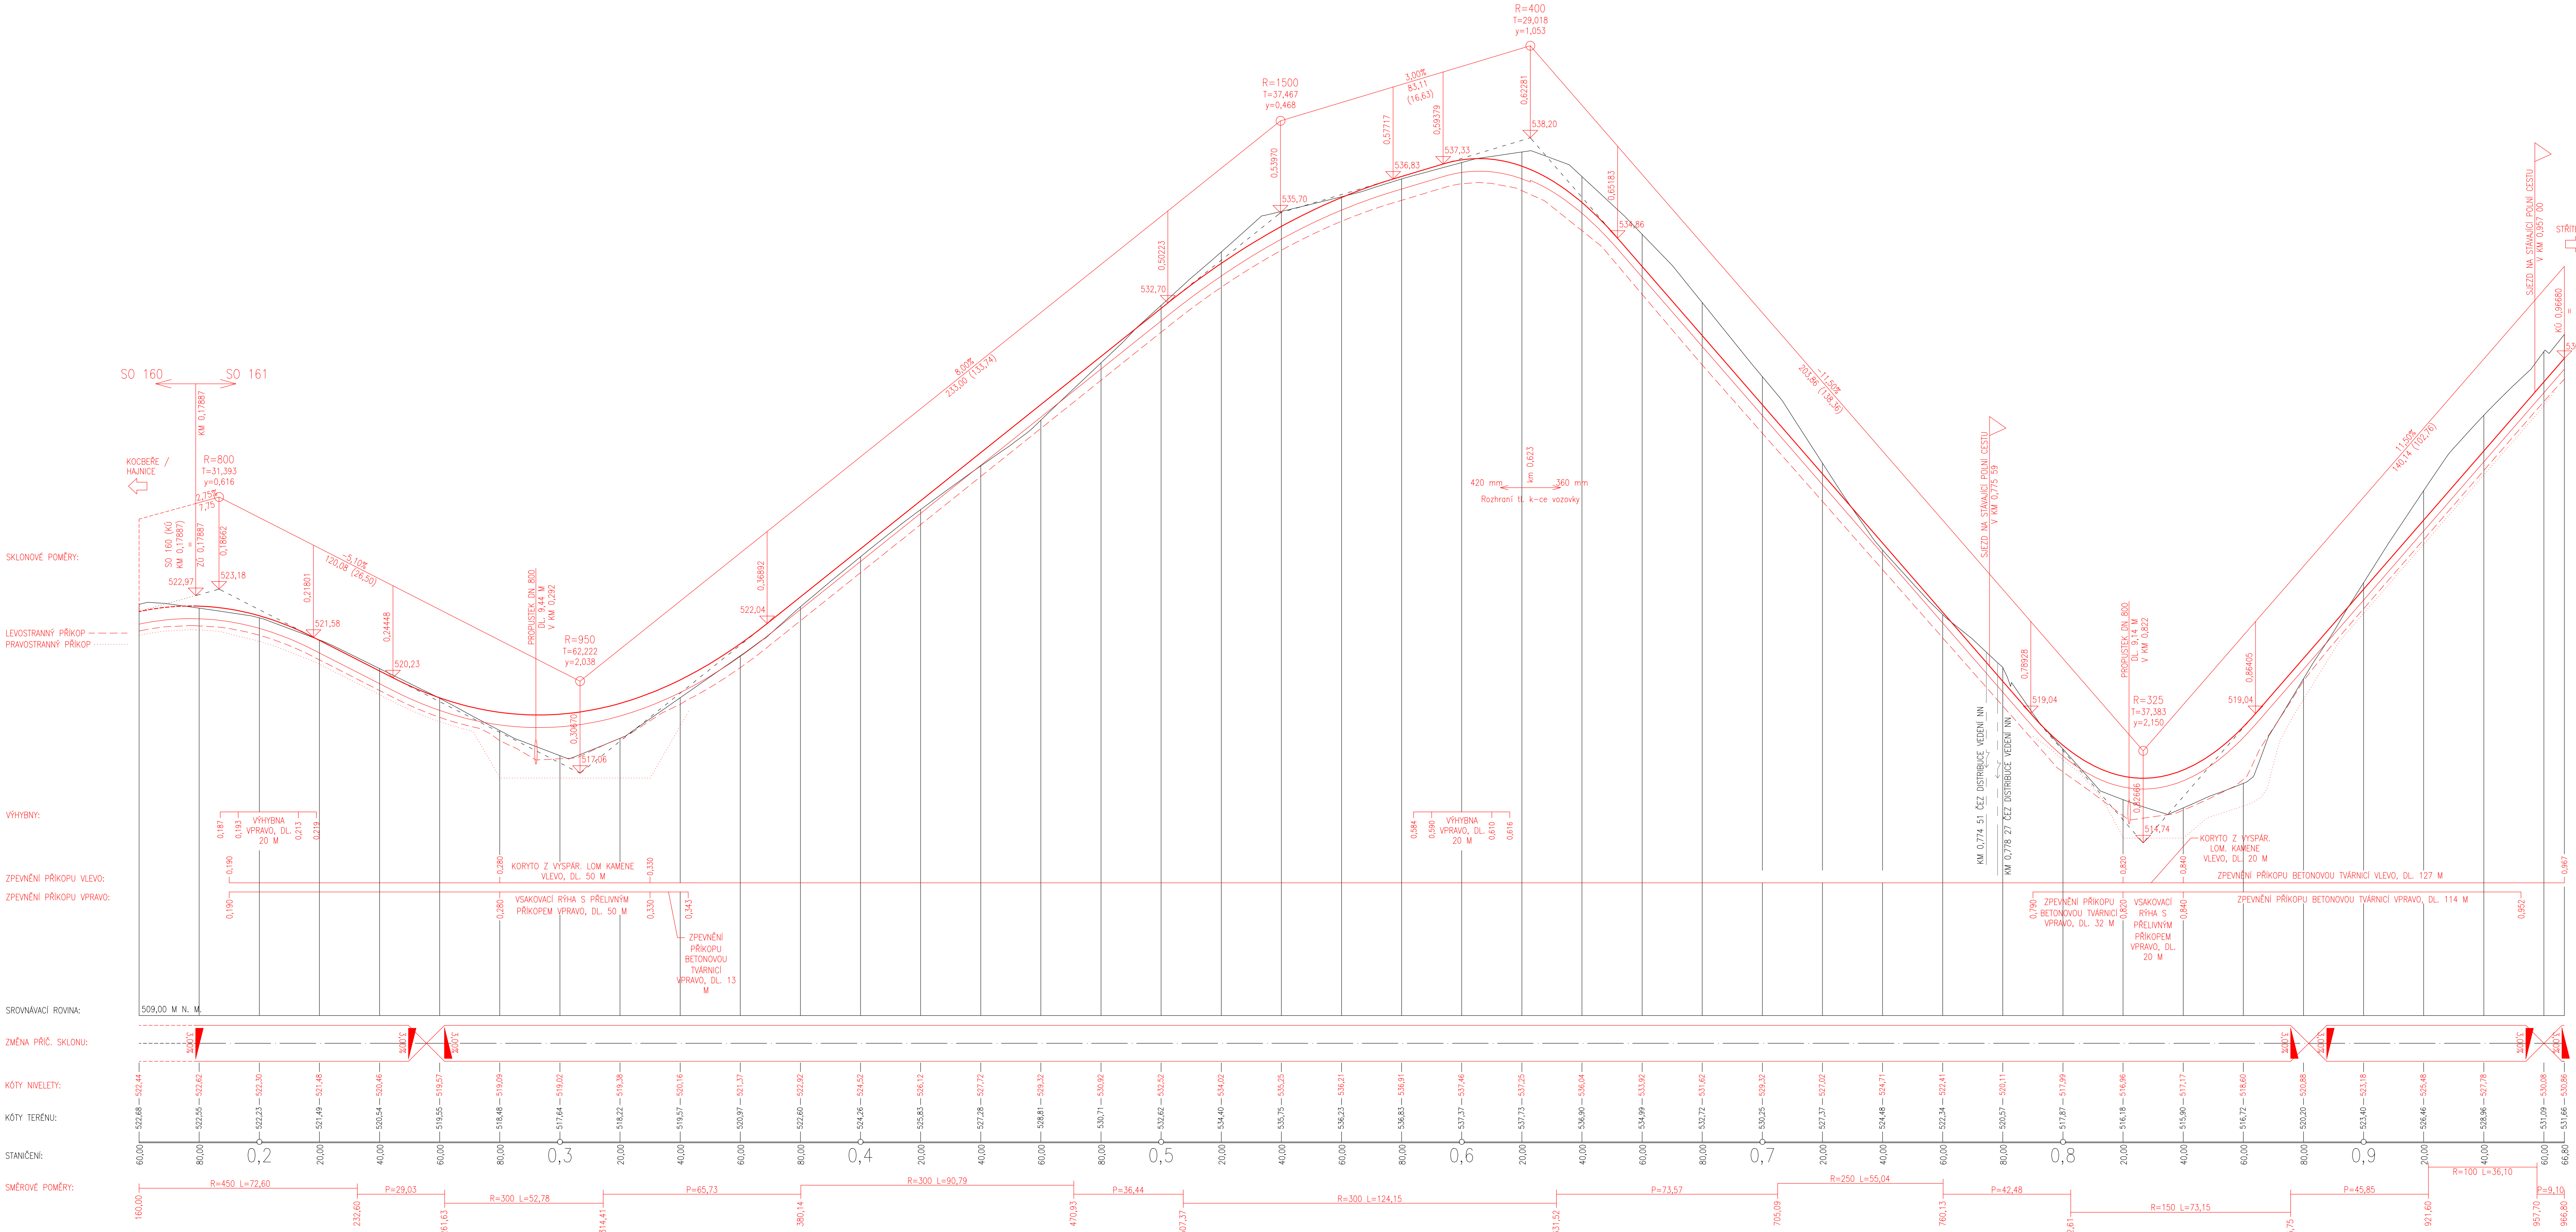

SO 161 D.1.1

VÝŠKOVÝ SYSTÉM BpV SOUŘADNICOVÝ SYSTÉM S-JTSK

Číslo změny:	Obsah změny:	Datum změny:
01	-	-
02	-	-
03	-	-

Objednatel: Ředitelství silnic a dálnic	Radikální síla a dálnic: Na Pankraci 540/56, 140 00 Praha 4 Stavbu zajišťuje Závod Praha Na Pankraci 540/56, 140 00 Praha 4
---	---

Zhotovitel: Společnost ve sdružení SG_Velké projekty BIM 2020 zastoupené

SUDOP PRAHA a.s. Hlavní inženýr projektu: Ing. Roman Petřík	Olšanská 1a, 130 80 Praha 3 telefon: +420 267 094 111
--	--

SUDOP PRAHA	PUDIS	SUDOP	PODOLSKÝ	KOPRAVOPROJEKT
--------------------	--------------	--------------	-----------------	-----------------------

Správa: SUDOP PRAHA a.s. Olšanská 1a, 130 80 Praha 3 tel.: +420 267 094 111 e-mail: praha@sudop.cz	Vedoucí týmu: ING. ROMAN PETŘÍK	Asistent vedoucího týmu: ING. PAVEL MICHLE Specialista profese: -
---	---	--

Zpracovatel: PUDIS a.s., Podbabská 1014/20, 160 00 Praha 6 tel.: +420 267 004 111, www.pudis.cz, info@pudis.cz	projektová, průzkumná a konzultační společnost
---	---

Vedoucí střediska: ING. ZDEŇKA BOLEHOVSKÁ	Odpovědný projektant SO, IO, PS: ING. MICHAL TUREK	Výpracoval: ING. TOMÁŠ VÁŇA	Kontroloval: ING. MICHAL TUREK
---	--	---------------------------------------	--

Název akce: D11 1108 Jaroměř - Trutnov VD-ZDS + TP + AD	Číslo směrnice: 22-014.250
---	--------------------------------------

Číslo: D.1.1	Projektový stupeň: VD-ZDS
------------------------	-------------------------------------

D.1.1 OBJEKTU POZEMNÍCH KOMUNIKACÍ VČETNĚ PROPUSTKŮ SO 161 PŘÍSTUPY NA POZEMKY V K.Ú. BRUSNICE	Číslo části: D.1.1
---	------------------------------

Podélný profil: PODÉLNÝ PROFIL	Měřítko: 1:1000/100	Podobí formátu: 12x44	Číslo přílohy: 3
--	-------------------------------	---------------------------------	----------------------------

DOKUMENT JE UŽITÝ POUZE VE SMYSLU PŘEDLÁŽENÉHO ÚČELU. ŽÁDNÁ JEHO ČÁST NEMŮŽE BÝT UŽITA JINÝM ZPŮSOBEM NEBO JINÝM ZPŮSOBEM ROZŠÍŘOVÁNA BEZ SOUHLASU SUDOP PRAHA a.s.